

SHEET INDEX

1	COVER SHEET
2	SITE ANALYSIS
3	SITE PLAN
4	WATER MANAGEMENT PLAN
5	GROUND FLOOR PLAN
6	ROOF PLAN
7	WINDOW & DOOR SCHEDULES
8	ELEVATIONS / SECTION
9	ELEVATIONS
10	KITCHEN DETAILS
11	BATHROOM DETAILS
12	ENSUITE DETAILS
13	WC DETAILS
14	LAUNDRY DETAILS
15	KITCHEN DETAILS (GRANNY FLAT)
16	BATHROOM 1 DETAILS (GRANNY FLAT)
17	LAUNDRY DETAILS (GRANNY FLAT)
18	FLOOR COVERINGS
19	SLAB PLAN
20	DRAINAGE PLAN

TOTAL FLOOR AREAS

GRANNY FLAT, GROUND FLOOR		
	LIVING	57.66
		57.66 m²
MAIN DWELLING, GROUND FLOOR		
	ALFRESCO	8.10
	GARAGE	33.14
	LIVING	145.53
	PATIO	4.79
		191.56 m²
		249.22 m²

AS & NCC COMPLIANCE

- ALL CONSTRUCTION TO BE IN ACCORDANCE WITH NCC 2022 AND APPLICABLE AUSTRALIAN STANDARDS AT TIME OF APPROVAL.
- SLAB IN ACCORDANCE WITH AS 2870. REFER TO ENGINEERS DETAILS FOR ALL SLAB DETAILS.
 - BRICK CONTROL JOINTS PROVIDED IN ACCORDANCE WITH NCC 2022.
 - ALL STEEL FRAMING TO BE DESIGNED TO AS 4100-2020 OR AS/NZS 4600-2018.
 - INSULATION TO BE INSTALLED IN ACCORDANCE WITH NCC 2022 AND ALL APPLICABLE AUSTRALIAN STANDARDS.
 - TERMITE PROTECTION IN ACCORDANCE WITH AS 3660 AND NCC 2022.
 - GLAZING IN ACCORDANCE WITH AS 1288 AND NCC 2022.
 - SMOKE ALARMS IN ACCORDANCE WITH AS 3786 AND NCC 2022.
 - INTERNAL WATERPROOFING IN ACCORDANCE WITH NCC 2022 HOUSING PROVISIONS PART 10.2.
 - EXTERNAL WATERPROOFING IN ACCORDANCE WITH AS 3740 AND AS 4654.
 - WET AREA FLOORS TO FALL TO FLOOR WASTES AT MIN. 1:80 AND MAX. 1:50 GRADE (IF APPLICABLE).
 - CONDENSATION MANAGEMENT IN ACCORDANCE WITH NCC 2022 HOUSING PROVISIONS PART 10.8.
 - BUILDING SEALING IN ACCORDANCE WITH NCC 2022.
 - SERVICES IN ACCORDANCE WITH NCC 2022.
 - EARTHWORKS IN ACCORDANCE WITH AS 3798-2007.
 - EXTERNAL WALL WRAP (SARKING) IN ACCORDANCE WITH NCC 2022 (IF APPLICABLE).
 - EXHAUST FANS DUCTED TO OUTSIDE AIR (IF APPLICABLE).


SITE SPECIFIC CONTROLS

CONTROL	DETAILS
ACID SULPHATE SOIL	NO
BIODIVERSITY	NO
BUILDING ENVELOPE	NO
BUSHFIRE	NO
CLASSIFIED ROAD	NO
DESIGN WIND CLASSIFICATION	N1 (NOT EXPOSED)
ESTATE/DEVELOPER GUIDELINES	NO
HERITAGE	NO
LANDSLIP HAZARD	NO
MINE SUBSIDENCE	NO
MINIMUM FLOOR LEVEL	NO
NOISE ATTENUATION	NO
SALINE SOIL	NO
SITE CLASSIFICATION	P-H1
SNOW LOAD	NO
WITHIN 1km CALM SALT WATER	NO
WITHIN 50km BREAKING SURF	23.53km
ZONING	R2 - LOW DENSITY RESIDENTIAL

BUILDING CONTROLS & COMPLIANCE

CONTROL	REQUIRED	PROPOSED
SETBACKS		
FRONT	MIN. 5,500mm	5,500mm
GARAGE TO BOUNDARY	MIN. 6,500mm	6,849mm
GARAGE TO BUILDING LINE	MIN. 1,000mm	1,000mm
SIDE	MIN. 900mm	915mm
REAR	MIN. 0mm	5,000mm
BULK & SCALE		
SITE AREA	482.9m²	
SITE COVERAGE	N/A	49.04%
FLOOR SPACE RATIO	MAX. 0.5:1	0:1
BUILDING HEIGHT	MAX. 9,000mm	6,370mm
LANDSCAPE		
LANDSCAPED AREA - FRONT	MIN. 35.96m²	57.72m²
EARTHWORKS		
CUT DEPTH	MAX. 600mm	200mm
FILL DEPTH	MAX. 600mm	479mm
ACCESS & AMENITY		
PRINCIPAL PRIVATE OPEN SPACE	MIN. 80m²	96.22m²

3D PERSPECTIVE

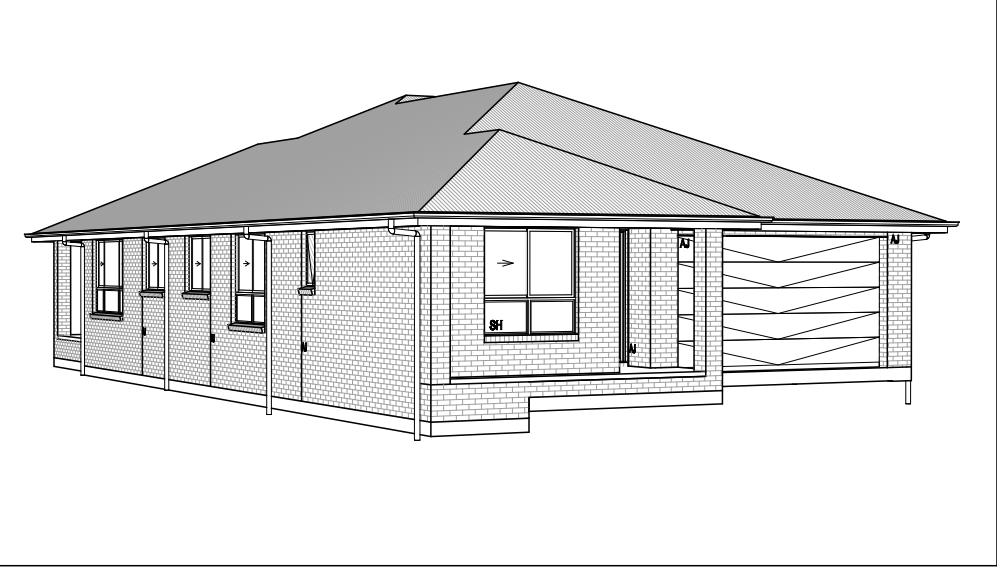

NOTE TO OWNER

THESE PLANS MAY FEATURE WORKS THAT ARE EXCLUDED FROM THE SCOPE OF WORKS WITH THE BUILDER, BUT THEY HAVE BEEN INCLUDED IN THESE DRAWINGS TO ASSIST IN THE OVERALL PLANNING AND ASSESSMENT OF THE BUILDING PROJECT. EXAMPLES OF SOME REGULARLY EXCLUDED WORKS INCLUDE DRIVEWAYS, RETAINING WALLS, SOLAR PANEL SPACING AND SITE DRAINAGE. PLEASE REFER TO YOUR SCOPE OF WORKS AND COLOUR SELECTIONS DOCUMENTATION FOR DETAILS OF INCLUDED WORKS. SOME DETAILS ARE INDICATIVE ONLY FOR EXAMPLE FLOORING, TILING, BRICKWORK AND CLADDING (EXPANSION JOINTS, ORIENTATION AND LAYOUT) AND ARE SUBJECT TO CHANGE.

LOCATION MAP



SUSTAINABILITY

PRELIMINARY SUSTAINABILITY COMPLIANCE FOR YOUR HOME REQUIRES FURTHER ASSESSMENT TO DETERMINE COMPLIANCE CRITERIA. THIS ASSESSMENT WILL BE FINALISED UPON APPROVAL OF YOUR EXTERNAL COLOUR SELECTIONS TO DETERMINE IF VARIATIONS ARE REQUIRED TO THE PROPOSED DWELLING E.G. ADDITIONAL INSULATION, CHANGES IN WINDOW GLAZING / SIZE / ORIENTATION ETC. YOU WILL BE ADVISED OF ANY REQUIREMENTS OR ALTERNATIVES ONCE THE ASSESSMENT HAS BEEN COMPLETED.

BASIX AREAS	
CONDITIONED AREA	161.89 m²
UNCONDITIONED AREA	17.79 m²
WATER RATINGS	
SHOWER HEADS	3 STAR (> 7.5 BUT <= 9 L/MIN)
TOILET SUITES	4 STAR
KITCHEN TAPS	4 STAR
BATHROOM TAPS	5 STAR
WATER HARVESTING AND USAGE	
TOTAL ROOF AREA	281.28 m²
MIN. WATER TANK CAPACITY	5034 L
MIN. ROOF AREA DIRECTED TO TANK(S)	184.00 m²
WATER TANK(S) CONNECTED TO	AT LEAST ONE OUTDOOR TAP ALL TOILETS WASHING MACHINE
GARDEN/LAWN AREA	50 m²
RECYCLED WATER	
RETICULATED RECYCLED WATER	N/A

ENERGY COMMITMENTS	
HOT WATER SYSTEM	ELECTRIC HEAT PUMP (325L) 26-30 RECS
HEATING SYSTEM	1-PHASE REVERSE CYCLE AIR CONDITIONING COP 3.0 - 3.5
COOLING SYSTEM	1-PHASE REVERSE CYCLE AIR CONDITIONING EER 3.0 - 3.5
VENTILATION (EXHAUST FANS)	
AT LEAST ONE BATHROOM: DUCTED TO OUTSIDE AIR, INTERLOCKED TO LIGHT	
KITCHEN RANGEHOOD: DUCTED TO OUTSIDE AIR, MANUAL SWITCH ON/OFF	
LAUNDRY: DUCTED TO OUTSIDE AIR, INTERLOCKED TO LIGHT	
PRIMARY FLUORESCENT/LED LIGHTING (INCL. COVER)	
N/A	
NATURAL LIGHTING	
NATURAL LIGHTING TO	1 x BATHROOM(S)/TOILET(S)
ALTERNATIVE ENERGY	
PHOTOVOLTAIC SYSTEM	MIN. 6.60KW PEAK
OTHER	
ELECTRIC COOKTOP, ELECTRIC OVEN FIXED OUTDOOR CLOTHESLINE BY OWNER NO FIXED INDOOR CLOTHESLINE	

INSULATION

ROOF	MIN. 60mm FOIL FACED BLANKET UNDER ROOFING
CEILING	R6.0 BATTS (INCL. GARAGE)
EXT. WALLS	R2.0 BATTS (EXCL. GARAGE)
INT. WALLS	R2.0 BATTS TO GARAGE INTERNAL WALLS
FLOOR	NO ADDITIONAL INSULATION

BUILDING INFORMATION

GROUND FLOOR PITCHING HEIGHT(S)	2745mm
FRAMES AND TRUSSES	STEEL
ROOF PITCH (U.N.O.)	26.0°
ELECTRICITY SUPPLY	SINGLE PHASE
GAS SUPPLY	NONE
ROOF MATERIAL	SHEET METAL
ROOF COLOUR	N/A
WALL MATERIAL	BRICK VENEER
WALL COLOUR	N/A
SLAB CLASSIFICATION	H1

GRANNY FLAT

ENERGY COMMITMENTS	
HOT WATER SYSTEM	ELECTRIC HEAT PUMP (325L) 26-30 RECS
HEATING SYSTEM	N/A
COOLING SYSTEM	N/A
VENTILATION (EXHAUST FANS)	
AT LEAST ONE BATHROOM: DUCTED TO OUTSIDE AIR, INTERLOCKED TO LIGHT	
KITCHEN RANGEHOOD: DUCTED TO OUTSIDE AIR, MANUAL SWITCH ON/OFF	
LAUNDRY: DUCTED TO OUTSIDE AIR, INTERLOCK TO LIGHT	
PRIMARY FLUORESCENT/LED LIGHTING (INCL. COVER)	
N/A	
NATURAL LIGHTING	
NATURAL LIGHTING TO	KITCHEN
ALTERNATIVE ENERGY	
N/A	
OTHER	
ELECTRIC COOKTOP, ELECTRIC OVEN NO FIXED OUTDOOR CLOTHESLINE NO FIXED INDOOR CLOTHESLINE	

SUBJECT TO NCC 2022
(1 OCT 2023 + 7 STAR BASIX)
WATERPROOFING & PLUMBING
CONDENSATION MANAGEMENT
7-STAR ENERGY EFFICIENCY

PLAN ACCEPTANCE BY OWNER

SIGNATURE:	DATE:
-----	-----
SIGNATURE:	DATE:
-----	-----
PLEASE NOTE THAT VARIATIONS WILL NOT BE ACCEPTED AFTER THIS PLAN ACCEPTANCE HAS BEEN SIGNED	


© 2024 MCDONALD JONES HOMES PTY LTD (ABN 82 003 687 232). THIS DRAWING IS AN ORIGINAL ARTISTIC WORK WITHIN THE MEANING OF THE COPYRIGHT ACT 1968 (CTH). MCDONALD JONES HOMES PTY LTD IS THE OWNER OF COPYRIGHT IN THIS DRAWING. YOU HEREBY AGREE AND UNDERTAKE THAT YOU WILL NOT IN ANY WAY REPRODUCE, COPY, MODIFY, USE OR TAKE ADVANTAGE OF THE DRAWING TO BUILD A HOUSE BASED ON THIS PLAN (WHETHER IN WHOLE OR IN PART) WITHOUT THE PRIOR WRITTEN CONSENT OF MCDONALD JONES HOMES PTY LTD.

SPECIFICATION:		REVISION	DRAWN
NOW	2	APPOINTMENT AMEDEMMENTS	LIR 01/02/2024
COPYRIGHT:	3	WORKING DRAWINGS	TNT 07/02/2024
© 2024	4	WD CHECK	ALW 13/02/2024
	5	AMENDED AS PER PCV003	ALW 01/03/2024
	6	AMENDED AS PER PCV004	ALW 07/03/2024

CLIENT:	LINH THANH THAO LE & HUU PHU LE	
ADDRESS:	40 WEEMALA ROAD, CHESTER HILL NSW 2162	
LOT / SECTION / DP:	42 / - / 15807	COUNCIL:
		CANTERBURY BANKSTOWN COUNCIL

HOUSE DESIGN:	SERRANO TWO		HOUSE CODE:	H-SRNCCLAS21420
FACADE DESIGN:	CLASSIC		FACADE CODE:	F-SRNCCLAS01
SHEET TITLE:	COVER SHEET	SHEET No.:	1 / 20	SCALES:
				1:170.32
				607126

DO NOT SCALE DRAWINGS, USE FIGURED DIMENSIONS ONLY. CHECK AND VERIFY DIMENSIONS AND LEVELS PRIOR TO THE COMMENCEMENT OF ANY WORK. ALL DISCREPANCIES TO BE REPORTED TO THE DRAFTING OFFICE.




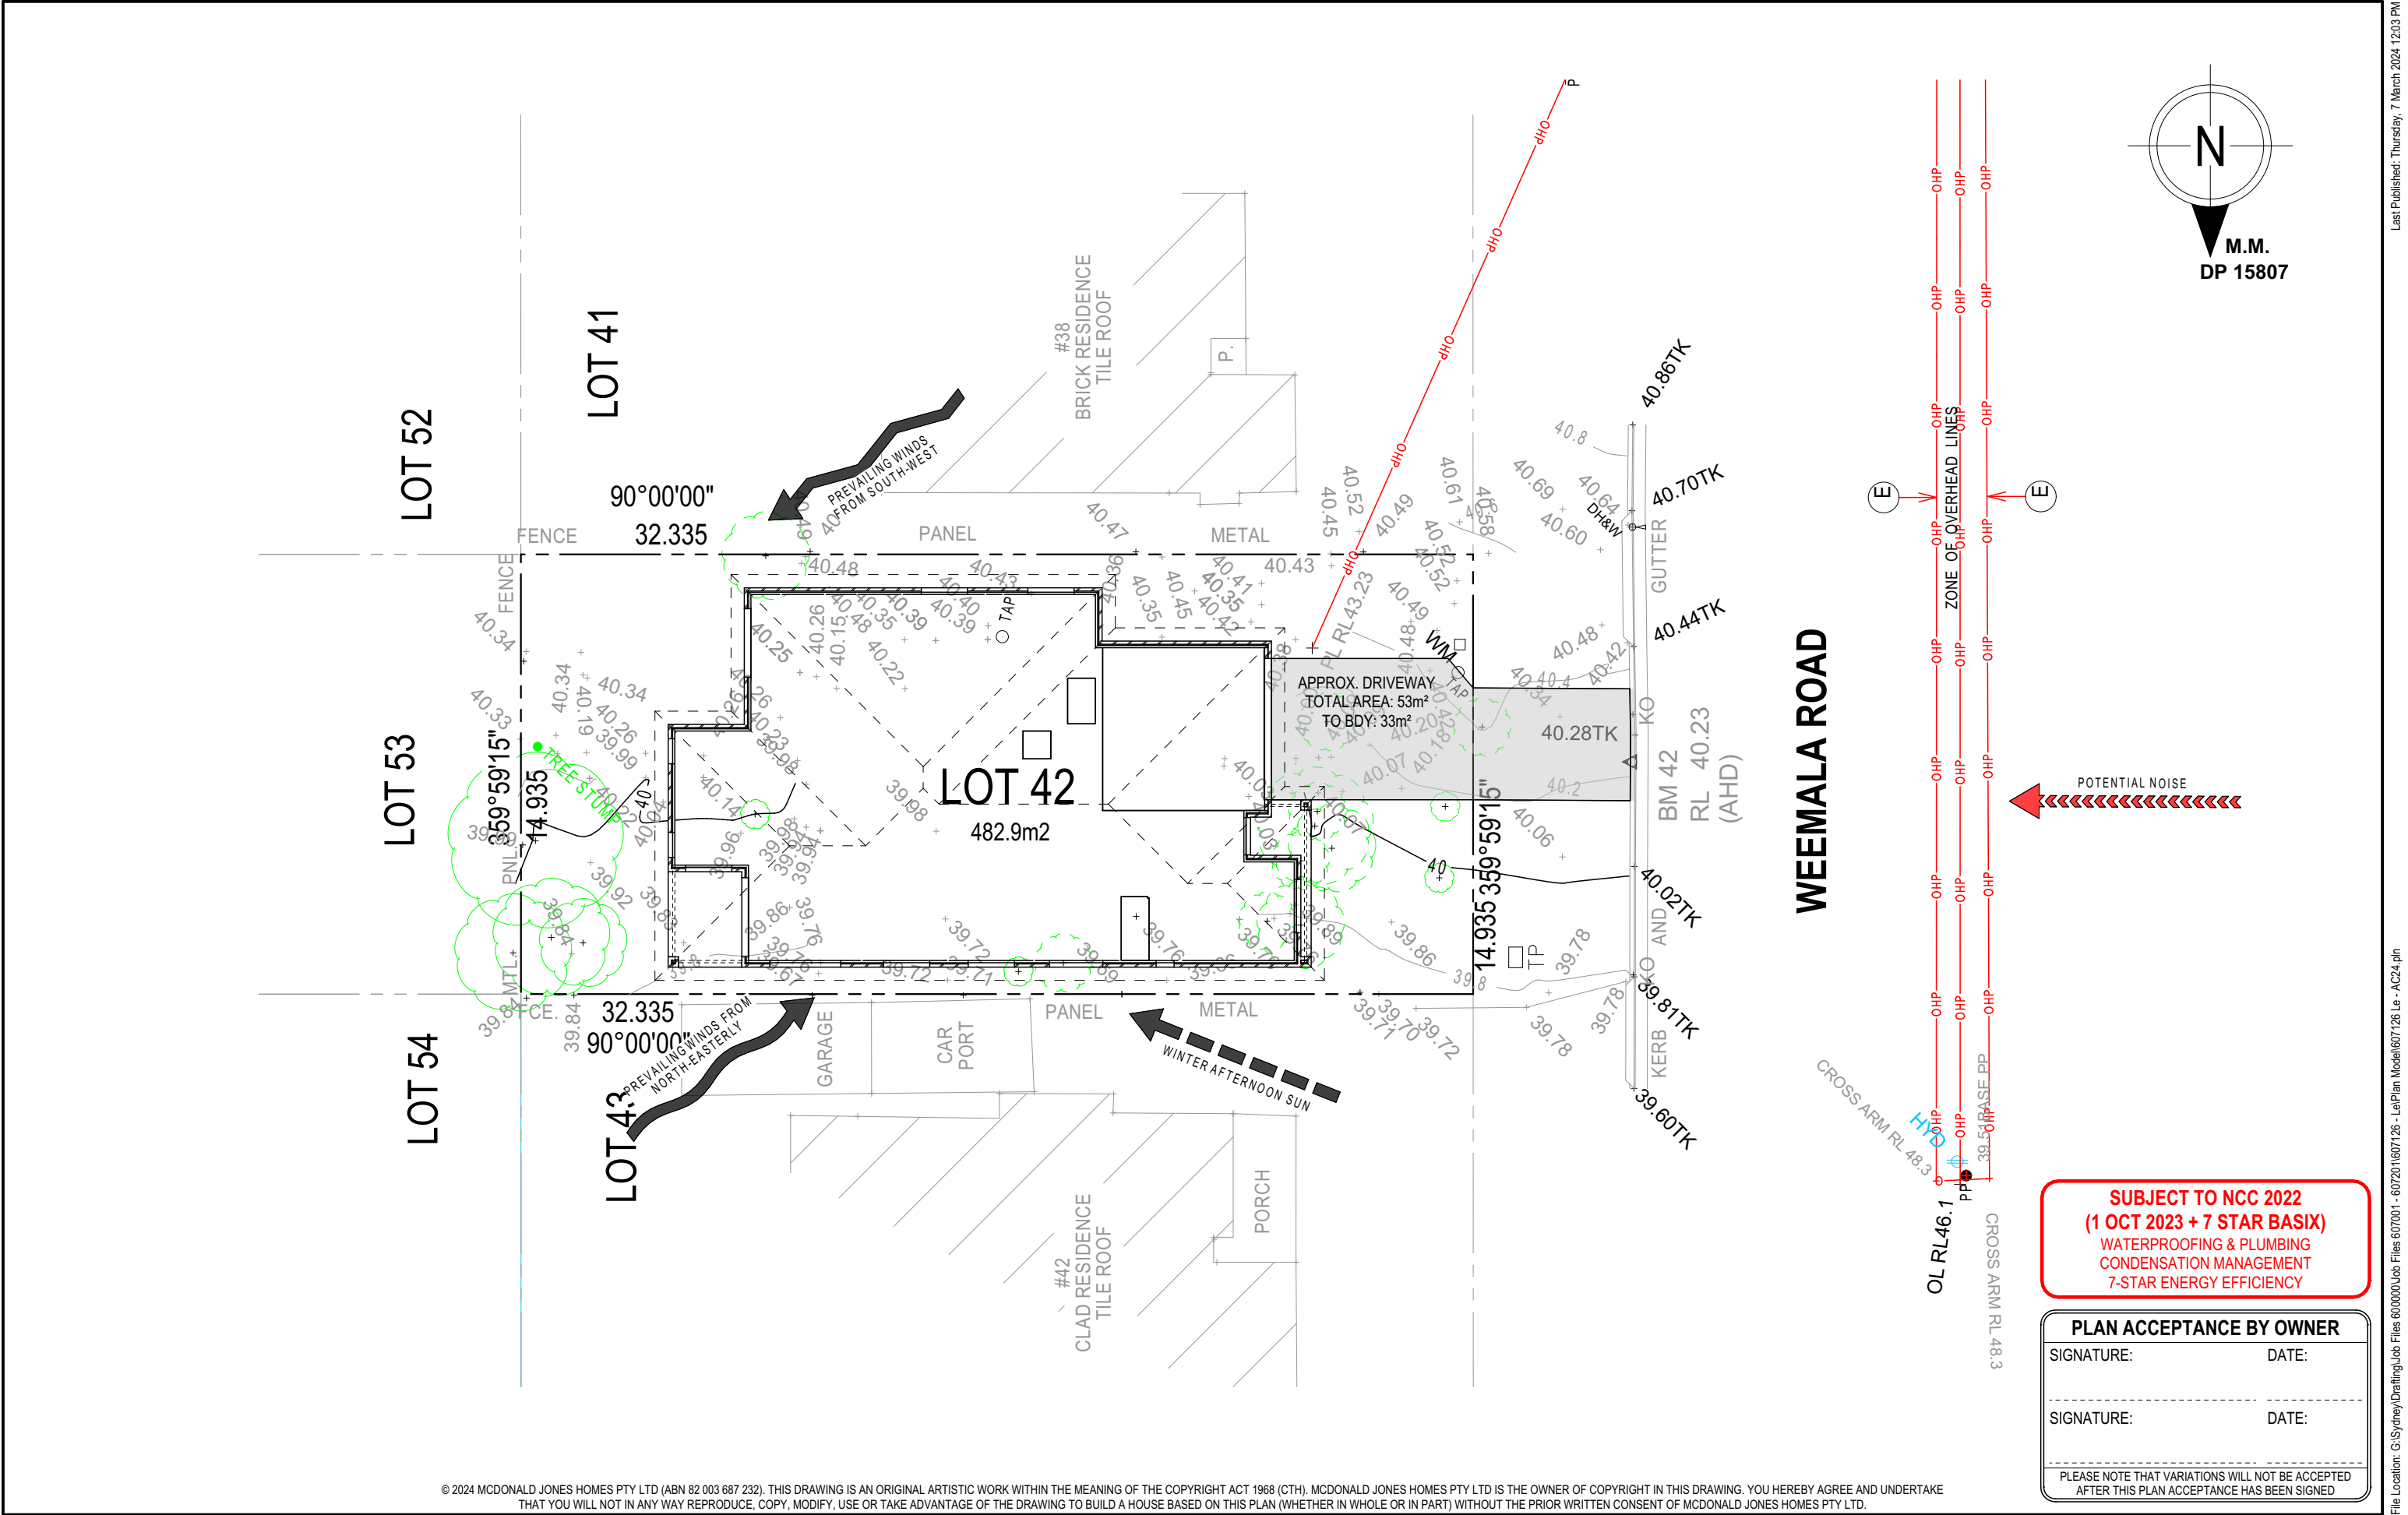


 mcdonald jones FIND YOURSELF AT HOME	SPECIFICATION:		REVISION		DRAWN		CLIENT:				HOUSE DESIGN:				HOUSE CODE:		DO NOT SCALE DRAWINGS. USE FIGURED DIMENSIONS ONLY. CHECK AND VERIFY DIMENSIONS AND LEVELS PRIOR TO THE COMMENCEMENT OF ANY WORK. ALL DISCREPANCIES TO BE REPORTED TO THE DRAFTING OFFICE.
	NOW		2	APPOINTMENT AMENDMENTS	LIR	01/02/2024	LINH THANH THAO LE & HUU PHU LE				SERRANO TWO				H-SRNCAS21420		
	COPYRIGHT:		3	WORKING DRAWINGS	TNT	07/02/2024	ADDRESS:				FACADE DESIGN:				FACADE CODE:		
	© 2024		4	WD CHECK	ALW	13/02/2024	40 WEEMALA ROAD, CHESTER HILL NSW 2162				CLASSIC				F-SRNCAS01		
			5	AMENDED AS PER PCV003	ALW	01/03/2024	LOT / SECTION / DP:		COUNCIL:		SHEET TITLE:		SHEET No.:	SCALES:			
			6	AMENDED AS PER PCV004	ALW	07/03/2024	42 / - / 15807		CANTERBURY BANKSTOWN COUNCIL		SITE ANALYSIS		2 / 20	1:200			

Template Version: 24-03


146 TONNES OF IMPORT FILL

IMPORTANT NOTE
 ANY PART OF THE FASCIA, GUTTERING OR
 DOWNPIPE THAT IS WITHIN 450mm OF ANY
 BOUNDARY IS TO BE NON-COMBUSTIBLE IN
 ACCORDANCE WITH THE REQUIREMENTS OF PART
 3.7.1.7(C) OF THE BCA

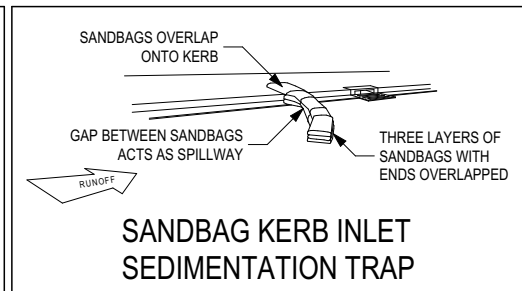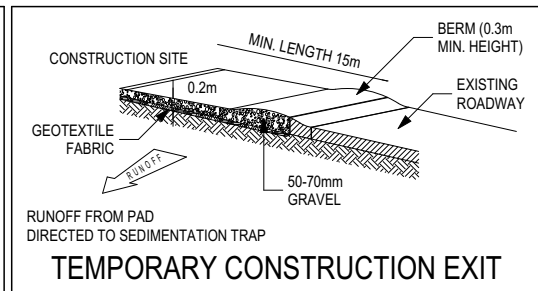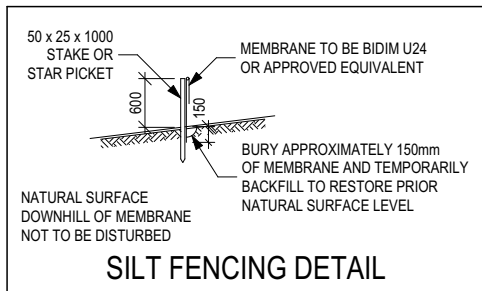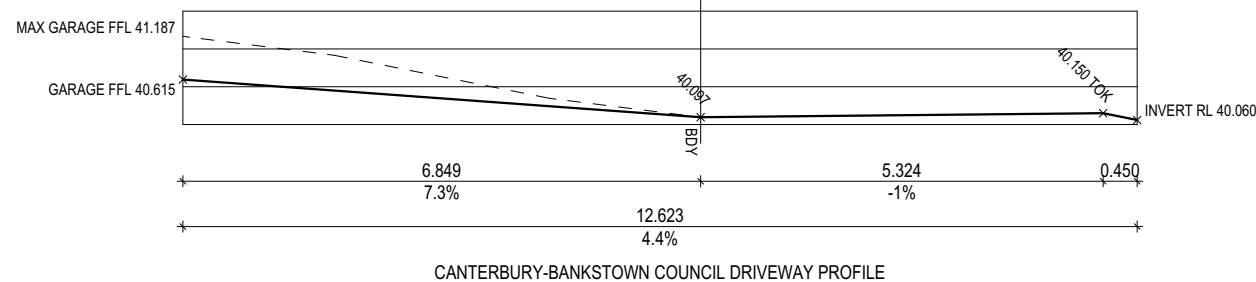

EXISTING TREE TO
BE REMOVED BY
OWNER = TOTAL (12)

EXISTING TREE
TO REMAIN

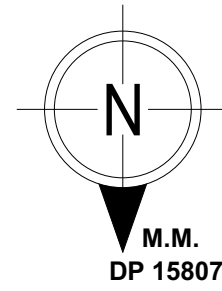

**SUBJECT TO NCC 2022
(1 OCT 2023 + 7 STAR BASIX)
WATERPROOFING & PLUMBING
CONDENSATION MANAGEMENT
7-STAR ENERGY EFFICIENCY**

PLAN ACCEPTANCE BY OWNER

SIGNATURE: _____ DATE: _____

SIGNATURE: _____ DATE: _____

PLEASE NOTE THAT VARIATIONS WILL NOT BE ACCEPTED
AFTER THIS PLAN ACCEPTANCE HAS BEEN SIGNED

REFER TO SHEET 1 (COVER SHEET) FOR ALL BUILDING INFORMATION REGARDING:

- SUSTAINABILITY REQUIREMENTS
- SITE CLASSIFICATION
- GENERAL BUILDING INFORMATION

STORMWATER LAYOUT IS DIAGRAMMATIC ONLY AND NO REPRESENTATION IS MADE AS TO THE AS-BUILT LOCATION OF STORMWATER ASSETS (INCLUDING SURFACE INLET PITS) OR THE TYPE OF SYSTEM USED (CHARGED OR GRAVITY FED). ALL STORMWATER DESIGN IS SUBJECT TO CONTRACTORS RECOMMENDATIONS AND/OR ANY CONSTRUCTION CONSTRAINTS OR CHANGES AT THE DISCRETION OF THE BUILDER. THE STORMWATER SYSTEM IS NOT SUITABLE FOR ANY OTHER USE. ALL SURFACE WATER DRAINAGE MUST BE MANAGED BY OWNER INCLUDING INSTALLATION OF ADDITIONAL DISCHARGE LINES AND INLETS AS REQUIRED. THE BUILDER PROVIDES CAPACITY FOR DISPOSAL OF ROOF COLLECTED STORMWATER ONLY AND TAKES NO RESPONSIBILITY FOR OVERFLOW OR DAMAGE TO PROPERTY IF OWNER ADDS ADDITIONAL DISCHARGE LOADS TO EXISTING STANDARD PROVISIONS.

NOTE TO PLUMBER: ROOF WATER FROM COLLECTION AREAS

TO BE DIVERTED TO WATER TANK. BALANCE STREET KERB VIA CHARGED SYSTEM WITHIN 10M OF THE TANK. COLLECTION AREA = 184.00m²

ALL STORMWATER OVERFLOW OTHER THAN THAT BEING DIRECTED TO WATER TANK(S) TO BE DIRECTED STREET KERB VIA CHARGED SYSTEM WITHIN 10M OF THE TANK.

LEGEND

WATER PUMP IN ACC. WITH LOCAL WATER AUTHORITY REQUIREMENTS

TANK CAPACITY TO BE MAINTAINED AT MINIMUM 10% CAPACITY

ALL RECY. WATER TO BE IN APPROVED COLOUR CODED PIPEWORK (PURPLE)

ALL DRAINAGE LINES ARE FOR ROOF WATER / WATER TANK DRAINAGE ONLY

SDP

CDP

WM

WC

+

STANDARD DOWNPIPE

CHARGED DOWNPIPE

RECYCLED COLD WATER LINE

TANK COLD WATER LINE

WATER LINE TO MAIN SUPPLY

NON-CHARGED STORMWATER LINE

CHARGED STORMWATER LINE

WASHING MACHINE

TOILET

YARD TAP

REFER TO STORMWATER DESIGN BY ALW DESIGN STORMWATER CONSULTANTS FOR STORMWATER REQUIREMENTS
REFERENCE: SW24092, ISSUE A
DATED: 23.02.2024

SUBJECT TO NCC 2022
(1 OCT 2023 + 7 STAR BASIX)
WATERPROOFING & PLUMBING
CONDENSATION MANAGEMENT
7-STAR ENERGY EFFICIENCY

PLAN ACCEPTANCE BY OWNER

SIGNATURE:DATE:

SIGNATURE:DATE:

PLEASE NOTE THAT VARIATIONS WILL NOT BE ACCEPTED AFTER THIS PLAN ACCEPTANCE HAS BEEN SIGNED

© 2024 MCDONALD JONES HOMES PTY LTD (ABN 82 003 687 232). THIS DRAWING IS AN ORIGINAL ARTISTIC WORK WITHIN THE MEANING OF THE COPYRIGHT ACT 1968 (CTH). MCDONALD JONES HOMES PTY LTD IS THE OWNER OF COPYRIGHT IN THIS DRAWING. YOU HEREBY AGREE AND UNDERTAKE THAT YOU WILL NOT IN ANY WAY REPRODUCE, COPY, MODIFY, USE OR TAKE ADVANTAGE OF THE DRAWING TO BUILD A HOUSE BASED ON THIS PLAN (WHETHER IN WHOLE OR IN PART) WITHOUT THE PRIOR WRITTEN CONSENT OF MCDONALD JONES HOMES PTY LTD.



 mcdonald jones FIND YOURSELF AT HOME	SPECIFICATION:		REVISION		DRAWN		CLIENT:		HOUSE DESIGN:		HOUSE CODE:	DO NOT SCALE DRAWINGS. USE FIGURED DIMENSIONS ONLY. CHECK AND VERIFY DIMENSIONS AND LEVELS PRIOR TO THE COMMENCEMENT OF ANY WORK. ALL DISCREPANCIES TO BE REPORTED TO THE DRAFTING OFFICE. 607126
	NOW	2	APPOINTMENT AMEDEMMENTS		LIR	01/02/2024	LINH THANH THAO LE & HUU PHU LE		SERRANO TWO		H-SRNCCLAS21420	
	COPYRIGHT:	3	WORKING DRAWINGS		TNT	07/02/2024	ADDRESS:		FACADE DESIGN:		FACADE CODE:	
	© 2024	4	WD CHECK		ALW	13/02/2024	40 WEEMALA ROAD, CHESTER HILL NSW 2162		CLASSIC		F-SRNCCLAS01	
		5	AMENDED AS PER PCV003		ALW	01/03/2024	LOT / SECTION / DP:	COUNCIL:	SHEET TITLE:	SHEET No.:	SCALES:	
		6	AMENDED AS PER PCV004		ALW	07/03/2024	42 / - / 15807	CANTERBURY BANKSTOWN COUNCIL	WATER MANAGEMENT PLAN	4 / 20		

UNLESS NOTED OTHERWISE
ALL ROOMS ARE REFERENCED
AS FOLLOWS:

A diagram of a diamond shape (a square rotated 45 degrees) with its four vertices labeled with letters. The top vertex is labeled 'A', the right vertex is labeled 'B', the bottom vertex is labeled 'C', and the left vertex is labeled 'D'. The diamond is drawn with solid black lines.

ALL EXTERIOR SLABS TO BE GRADED BY CONCRETER TO ACHIEVE APPROX. 1:100 FALL TO OUTSIDE EDGE WITH MAXIMUM CROSSFALL OF 30mm OVER ENTIRE SLAB.

607126

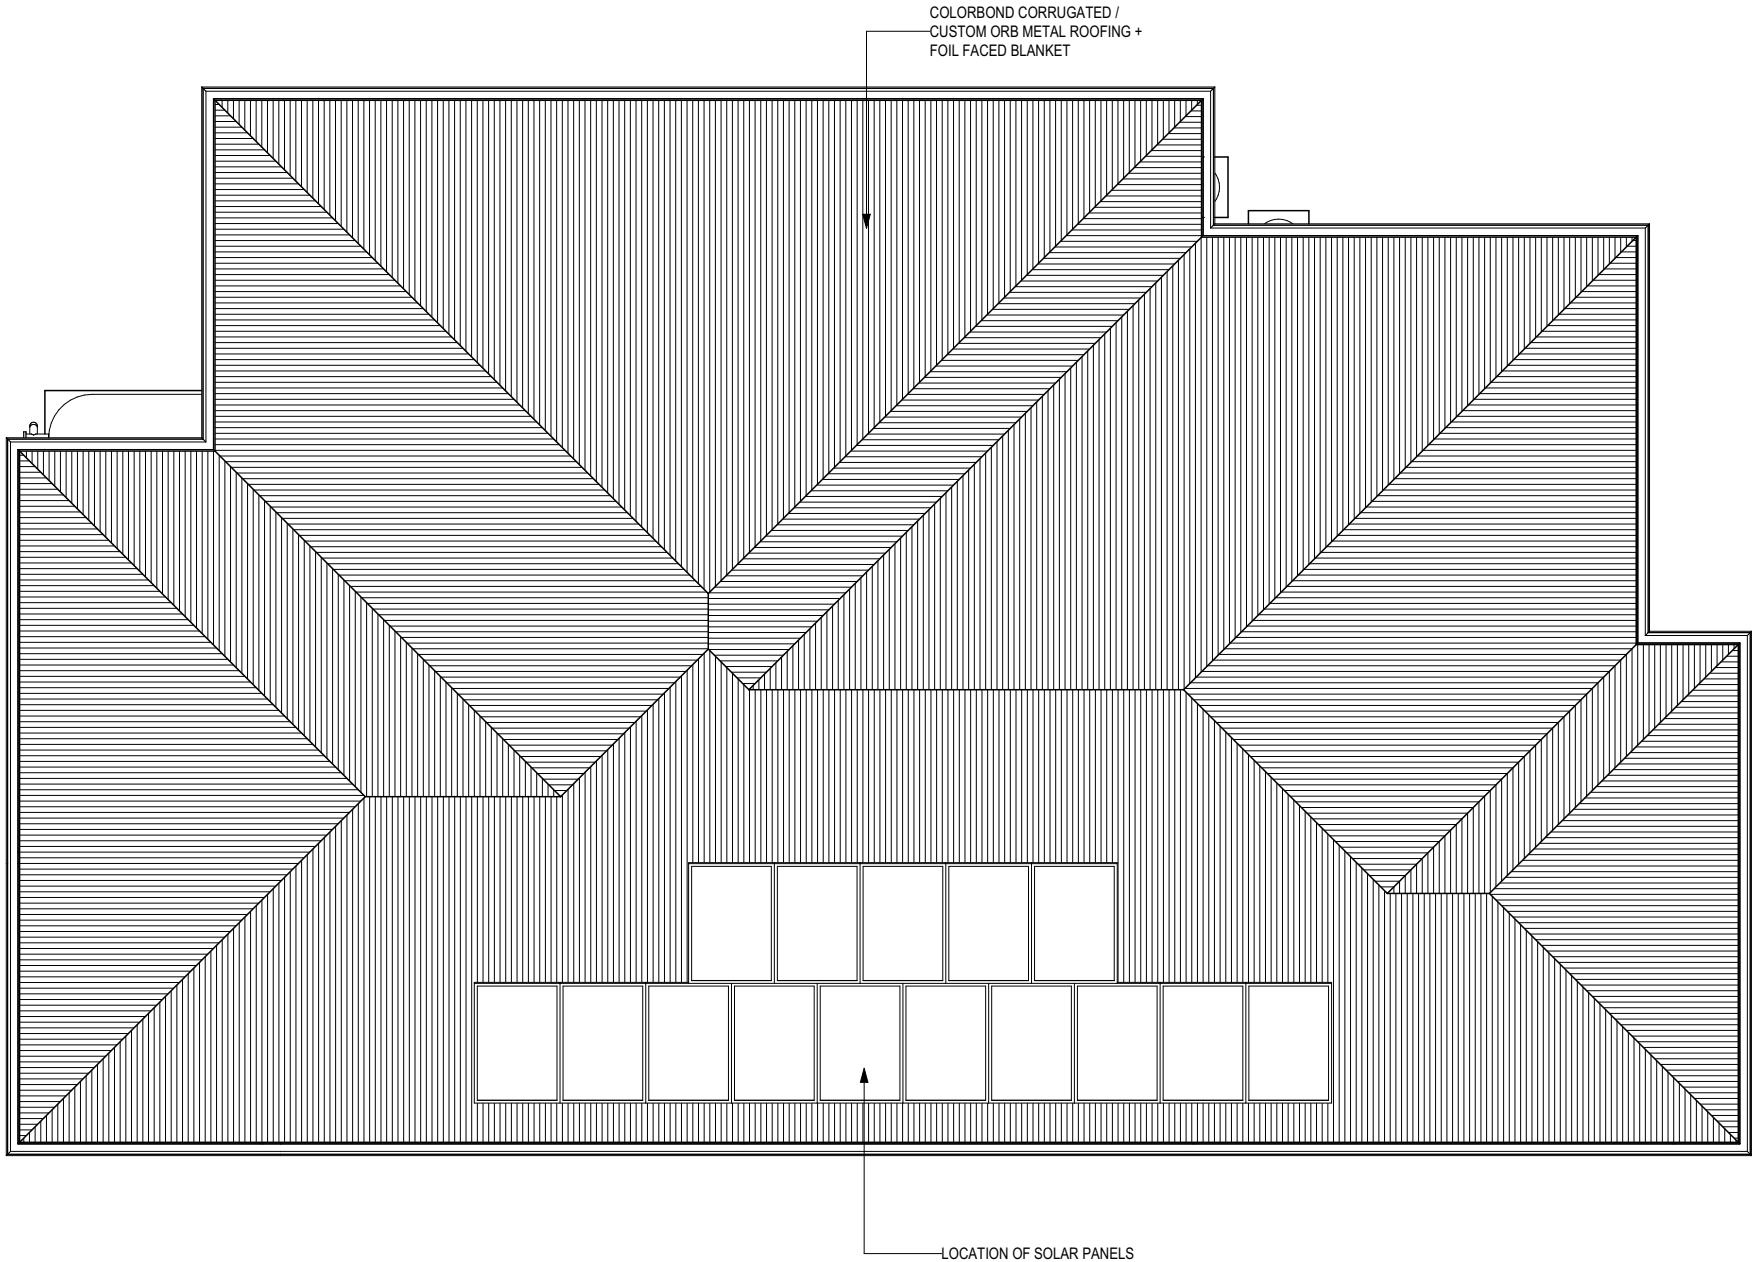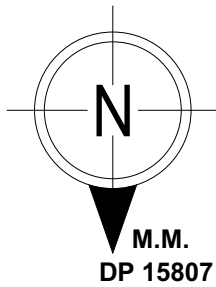

ROOF PLAN
SCALE: 1:100

**SUBJECT TO NCC 2022
(1 OCT 2023 + 7 STAR BASIX)**
WATERPROOFING & PLUMBING
CONDENSATION MANAGEMENT
7-STAR ENERGY EFFICIENCY

PLAN ACCEPTANCE BY OWNER	
SIGNATURE: _____	DATE: _____
SIGNATURE: _____	DATE: _____
PLEASE NOTE THAT VARIATIONS WILL NOT BE ACCEPTED AFTER THIS PLAN ACCEPTANCE HAS BEEN SIGNED	

© 2024 MCDONALD JONES HOMES PTY LTD (ABN 82 003 687 232). THIS DRAWING IS AN ORIGINAL ARTISTIC WORK WITHIN THE MEANING OF THE COPYRIGHT ACT 1968 (CTH). MCDONALD JONES HOMES PTY LTD IS THE OWNER OF COPYRIGHT IN THIS DRAWING. YOU HEREBY AGREE AND UNDERTAKE THAT YOU WILL NOT IN ANY WAY REPRODUCE, COPY, MODIFY, USE OR TAKE ADVANTAGE OF THE DRAWING TO BUILD A HOUSE BASED ON THIS PLAN (WHETHER IN WHOLE OR IN PART) WITHOUT THE PRIOR WRITTEN CONSENT OF MCDONALD JONES HOMES PTY LTD.

 mcdonald jones FIND YOURSELF AT HOME	SPECIFICATION: NOW		REVISION	DRAWN	CLIENT: LINH THANH THAO LE & HUU PHU LE	HOUSE DESIGN: SERRANO TWO	HOUSE CODE: H-SRNCCLAS21420	DO NOT SCALE DRAWINGS, USE FIGURED DIMENSIONS ONLY. CHECK AND VERIFY DIMENSIONS AND LEVELS PRIOR TO THE COMMENCEMENT OF ANY WORK. ALL DISCREPANCIES TO BE REPORTED TO THE DRAFTING OFFICE. 607126
	COPYRIGHT: © 2024	2	APPOINTMENT AMENDMENTS	LIR 01/02/2024	ADDRESS: 40 WEEMALA ROAD, CHESTER HILL NSW 2162	FACADE DESIGN: CLASSIC	FACADE CODE: F-SRNCCLAS01	
		3	WORKING DRAWINGS	TNT 07/02/2024	LOT / SECTION / DP: 42 / - / 15807	SHEET TITLE: ROOF PLAN	SHEET No.: 1 / 1	
		4	WD CHECK	ALW 13/02/2024	COUNCIL: CANTERBURY BANKSTOWN COUNCIL		SCALES: 1:100	
		5	AMENDED AS PER PCV003	ALW 01/03/2024				
		6	AMENDED AS PER PCV004	ALW 07/03/2024				

EXTERIOR WINDOW & DOOR SCHEDULE 1,2 ASSUME LOOKING FROM OUTSIDE

STOREY	ID	CODE¹	TYPE	ROOM	HEIGHT	WIDTH	PERIMETER	AREA (m²)	FRAME TYPE	BAL RATING	SILL TYPE	ORIENT.	GLAZING AREA (m²)	GLAZING TYPE	ADDITIONAL INFORMATION²
WINDOW															
GROUND FLOOR	W01	SF/FF1818	SLIDING	MASTER SUITE	1,800	1,810	7,220	3.26	ALUMINIUM	N/A	SNAP HEADER	W	2.79	CLEAR	BP 600, MP 905/0
GROUND FLOOR	W02	SF1216	SLIDING	BED 1	1,200	1,570	5,540	1.88	ALUMINIUM	N/A	ANGLED	S	1.64	CLEAR	
GROUND FLOOR	W03	SF1216	SLIDING	BED 2	1,200	1,570	5,540	1.88	ALUMINIUM	N/A	ANGLED	S	1.64	CLEAR	
GROUND FLOOR	W04	SF/F1809	SLIDING	LIVING	1,800	850	5,300	1.53	ALUMINIUM	N/A	ANGLED	E	1.24	CLEAR	BP 600
GROUND FLOOR	W05	SF/F1809	SLIDING	LIVING	1,800	850	5,300	1.53	ALUMINIUM	N/A	ANGLED	E	1.24	CLEAR	BP 600
GROUND FLOOR	W06	FS1216	SLIDING	LIVING	1,200	1,570	5,540	1.88	ALUMINIUM	N/A	SNAP HEADER	N	1.64	CLEAR	
GROUND FLOOR	W07	SFS/FFF1824	SLIDING	DINING	1,800	2,410	8,420	4.34	ALUMINIUM	N/A	ANGLED	N	3.70	CLEAR	BP 600, MP 603-1205/0
GROUND FLOOR	W08	SF1216	SLIDING	BED 4	1,200	1,570	5,540	1.88	ALUMINIUM	N/A	ANGLED	N	1.64	CLEAR	
GROUND FLOOR	W09	SF1216	SLIDING	BED 3	1,200	1,570	5,540	1.88	ALUMINIUM	N/A	ANGLED	N	1.64	CLEAR	
GROUND FLOOR	W10	SF/FF1818	SLIDING	ENTERTAINMENT	1,800	1,810	7,220	3.26	ALUMINIUM	N/A	ANGLED	N	2.79	CLEAR	BP 600, MP 905/0
GROUND FLOOR	W11	A1006	AWNING	ENS	1,030	610	3,280	0.63	ALUMINIUM	N/A	ANGLED	N	0.44	SATINLITE, TOUGHENED	
								23.95					20.40		
DOOR															
GROUND FLOOR	D01	1200	SWINGING	ENTRY	2,406	1,267	7,346	3.05	TIMBER	N/A	SNAP HEADER	W	---	DOOR(S): N/A - SIDELIGHT(S): N/A	LEAF SIZE: 2340 x 1200mm
GROUND FLOOR	D02	FSS2423	STACKER	LIVING / DINING	2,400	2,328	9,456	5.59	ALUMINIUM	N/A	SNAP HEADER	E	4.88	CLEAR, TOUGHENED	
GROUND FLOOR	D03	SSF2427	STACKER	DINING	2,400	2,688	10,176	6.45	ALUMINIUM	N/A	SNAP HEADER	E	5.70	CLEAR, TOUGHENED	
								15.09					10.58		
								39.04					30.98		

INTERIOR WINDOW & DOOR SCHEDULE

STOREY	QTY	CODE	TYPE	HEIGHT	WIDTH	GLAZING TYPE	ADDITIONAL INFORMATION
DOOR							
GROUND FLOOR	1	1150 SS	SQUARE SET OPENING	2,455	1,150	N/A	
GROUND FLOOR	1	1270 SS	SQUARE SET OPENING	2,455	1,270	N/A	
GROUND FLOOR	1	2 x 520 UC	SWINGING	2,340	1,040	N/A	20mm UNDERCUT
GROUND FLOOR	1	2 x 620	SWINGING	2,340	1,240	N/A	
GROUND FLOOR	3	2 x 720	SWINGING	2,340	1,440	N/A	
GROUND FLOOR	1	2340x820 CSD	CAVITY SLIDING	2,340	820	N/A	
GROUND FLOOR	1	520	SWINGING	2,340	520	N/A	
GROUND FLOOR	1	620	SWINGING	2,340	620	N/A	
GROUND FLOOR	2	720	SWINGING	2,340	720	N/A	
GROUND FLOOR	1	720	SWINGING	2,340	720	N/A	LIFT-OFF HINGES
GROUND FLOOR	1	800 SS	SQUARE SET OPENING	2,455	800	N/A	
GROUND FLOOR	6	820	SWINGING	2,340	820	N/A	
GROUND FLOOR	1	820 UC	SWINGING	2,340	820	N/A	20mm UNDERCUT
GROUND FLOOR	1	900 SS	SQUARE SET OPENING	2,455	900	N/A	
GROUND FLOOR	1	920	SWINGING	2,340	920	N/A	
GROUND FLOOR	1	970 SS	SQUARE SET OPENING	2,455	970	N/A	
GROUND FLOOR	1	990 SS	SQUARE SET OPENING	2,455	990	N/A	

REFER TO SHEET 1 (COVER SHEET) FOR ALL BUILDING INFORMATION REGARDING:
- SUSTAINABILITY REQUIREMENTS
- SITE CLASSIFICATION
- GENERAL BUILDING INFORMATION

© 2024 MCDONALD JONES HOMES PTY LTD (ABN 82 003 687 232). THIS DRAWING IS AN ORIGINAL ARTISTIC WORK WITHIN THE MEANING OF THE COPYRIGHT ACT 1968 (CTH). MCDONALD JONES HOMES PTY LTD IS THE OWNER OF COPYRIGHT IN THIS DRAWING. YOU HEREBY AGREE AND UNDERTAKE THAT YOU WILL NOT IN ANY WAY REPRODUCE, COPY, MODIFY, USE OR TAKE ADVANTAGE OF THE DRAWING TO BUILD A HOUSE BASED ON THIS PLAN (WHETHER IN WHOLE OR IN PART) WITHOUT THE PRIOR WRITTEN CONSENT OF MCDONALD JONES HOMES PTY LTD.

PICTURE, TV RECESS AND SS WINDOW OPENINGS				
QTY	TYPE	HEIGHT	WIDTH	AREA (m²)

SUBJECT TO NCC 2022
(1 OCT 2023 + 7 STAR BASIX)
WATERPROOFING & PLUMBING
CONDENSATION MANAGEMENT
7-STAR ENERGY EFFICIENCY

PLAN ACCEPTANCE BY OWNER


SIGNATURE: DATE:

SIGNATURE: DATE:


PLEASE NOTE THAT VARIATIONS WILL NOT BE ACCEPTED AFTER THIS PLAN ACCEPTANCE HAS BEEN SIGNED



SPECIFICATION: NOW		REVISION	DRAWN	CLIENT:	HOUSE DESIGN:	HOUSE CODE:	DO NOT SCALE DRAWINGS. USE FIGURED DIMENSIONS ONLY. CHECK AND VERIFY DIMENSIONS AND LEVELS PRIOR TO THE COMMENCEMENT OF ANY WORK. ALL DISCREPANCIES TO BE REPORTED TO THE DRAFTING OFFICE. 607126
	2	APPOINTMENT AMEDEMEMENTS	LIR 01/02/2024	LINH THANH THAO LE & HUU PHU LE	SERRANO TWO	H-SRNCCLAS21420	
COPYRIGHT: © 2024	3	WORKING DRAWINGS	TNT 07/02/2024	ADDRESS:	FACADE DESIGN:	FACADE CODE:	
	4	WD CHECK	ALW 13/02/2024	40 WEEMALA ROAD, CHESTER HILL NSW 2162	CLASSIC	F-SRNCCLAS01	
	5	AMENDED AS PER PCV003	ALW 01/03/2024	LOT / SECTION / DP:	SHEET TITLE:	SHEET No.:	
	6	AMENDED AS PER PCV004	ALW 07/03/2024	42 / - / 15807	COUNCIL: CANTERBURY BANKSTOWN COUNCIL	WINDOW & DOOR SCHEDULES 7 / 20	
						SCALES:	

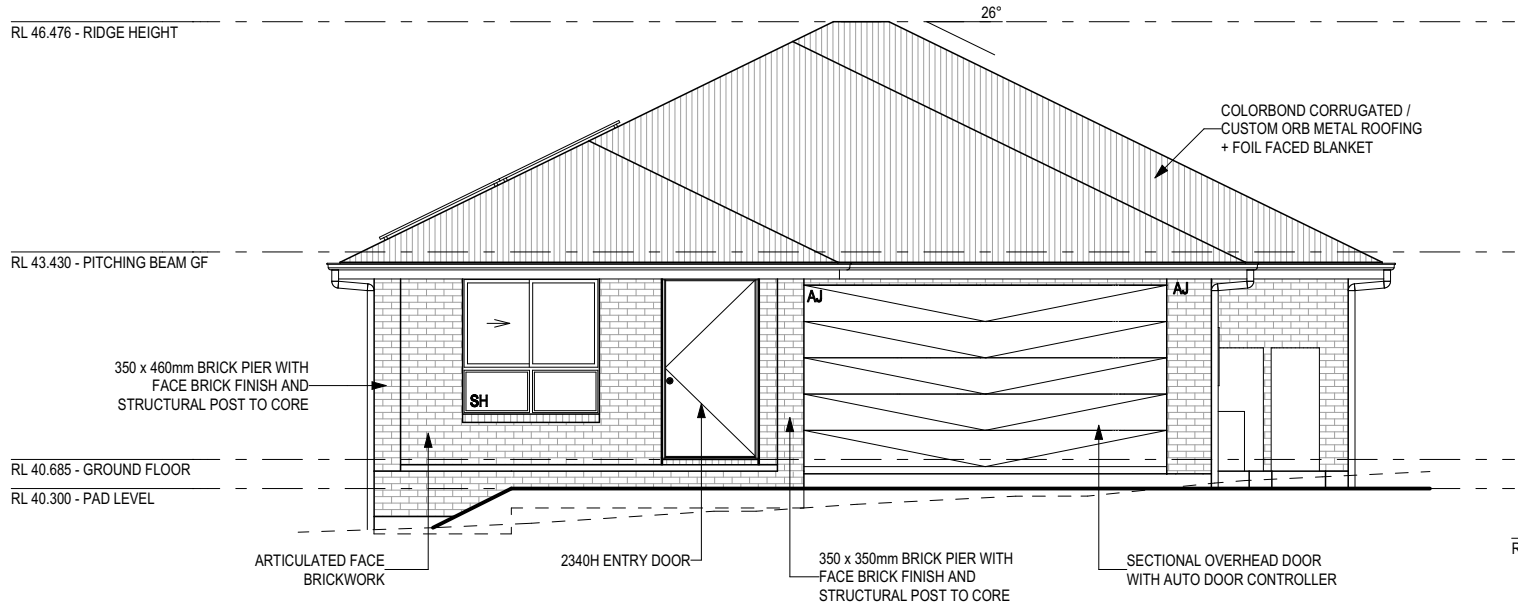

WEST ELEVATION
SCALE: 1:100

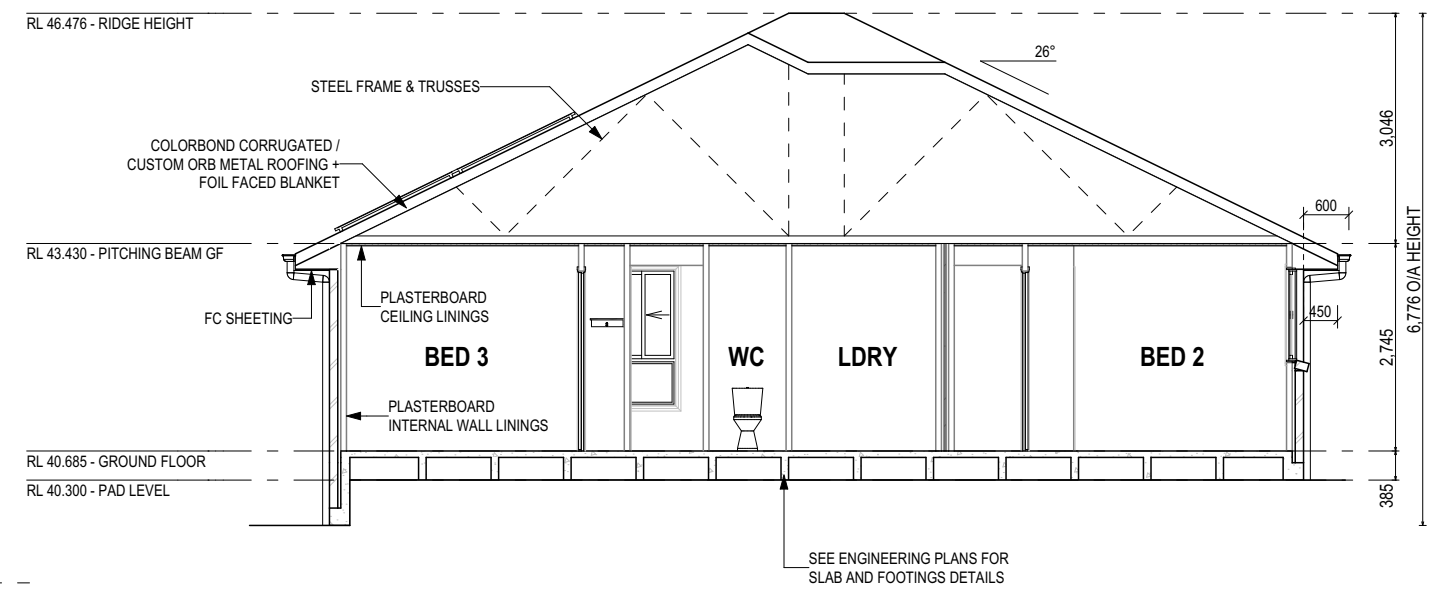

SECTION A-A
SCALE: 1:100





EAST ELEVATION
SCALE: 1:100

REFER TO SHEET 1 (COVER SHEET) FOR ALL BUILDING INFORMATION REGARDING:
- SUSTAINABILITY REQUIREMENTS
- SITE CLASSIFICATION
- GENERAL BUILDING INFORMATION

SOME DETAILS ON THIS SHEET ARE INDICATIVE ONLY FOR EXAMPLE BRICKWORK AND CLADDING (EXPANSION JOINTS, ORIENTATION AND LAYOUT) AND ARE SUBJECT TO CHANGE.

SH = SNAP HEADER SILL

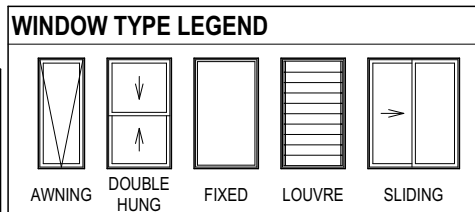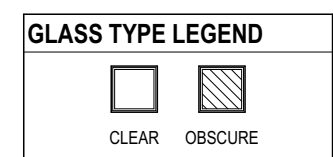

PLAN ACCEPTANCE BY OWNER

SIGNATURE:	DATE:
SIGNATURE:	DATE:

PLEASE NOTE THAT VARIATIONS WILL NOT BE ACCEPTED AFTER THIS PLAN ACCEPTANCE HAS BEEN SIGNED

© 2024 MCDONALD JONES HOMES PTY LTD (ABN 82 003 687 232). THIS DRAWING IS AN ORIGINAL ARTISTIC WORK WITHIN THE MEANING OF THE COPYRIGHT ACT 1968 (CTH). MCDONALD JONES HOMES PTY LTD IS THE OWNER OF COPYRIGHT IN THIS DRAWING. YOU HEREBY AGREE AND UNDERTAKE THAT YOU WILL NOT IN ANY WAY REPRODUCE, COPY, MODIFY, USE OR TAKE ADVANTAGE OF THE DRAWING TO BUILD A HOUSE BASED ON THIS PLAN (WHETHER IN WHOLE OR IN PART) WITHOUT THE PRIOR WRITTEN CONSENT OF MCDONALD JONES HOMES PTY LTD.



SPECIFICATION: NOW COPYRIGHT: © 2024	REVISION		DRAWN		CLIENT: LINH THANH THAO LE & HUU PHU LE ADDRESS: 40 WEEMALA ROAD, CHESTER HILL NSW 2162	HOUSE DESIGN: SERRANO TWO FACADE DESIGN: CLASSIC	HOUSE CODE: H-SRNCAS21420 FACADE CODE: F-SRNCAS01	DO NOT SCALE DRAWINGS. USE FIGURED DIMENSIONS ONLY. CHECK AND VERIFY DIMENSIONS AND LEVELS PRIOR TO THE COMMENCEMENT OF ANY WORK. ALL DISCREPANCIES TO BE REPORTED TO THE DRAFTING OFFICE. 607126
	2	APPOINTMENT AMEDEMMENTS	LIR	01/02/2024				
	3	WORKING DRAWINGS	TNT	07/02/2024				
	4	WD CHECK	ALW	13/02/2024	LOT / SECTION / DP: 42 / - / 15807 COUNCIL: CANTERBURY BANKSTOWN COUNCIL	SHEET TITLE: ELEVATIONS / SECTION	SHEET No.: 8 / 20	SCALES: 1:100
	5	AMENDED AS PER PCV003	ALW	01/03/2024				
	6	AMENDED AS PER PCV004	ALW	07/03/2024				

RL 46.476 - RIDGE HEIGHT

RL 43.430 - PITCHING BEAM GF

RL 40.685 - GROUND FLOOR

RL 40.300 - PAD LEVEL

350 x 350mm BRICK PIER WITH FACE BRICK FINISH AND STRUCTURAL POST TO CORE

350 x 460mm BRICK PIER WITH FACE BRICK FINISH AND STRUCTURAL POST TO CORE

LOCATION OF SOLAR PANELS

COLORBOND CORRUGATED / CUSTOM ORB METAL ROOFING + FOIL FACED BLANKET

ARTICULATED FACE BRICKWORK

26°

SH

AJ

AJ

AJ

NORTH ELEVATION

SCALE: 1:100

RL 46.476 - RIDGE HEIGHT

RL 43.430 - PITCHING BEAM GF

RL 40.685 - GROUND FLOOR

RL 40.300 - PAD LEVEL

350 x 350mm BRICK PIER WITH FACE BRICK FINISH AND STRUCTURAL POST TO CORE

SINGLE PHASE METER BOX

SOLAR INVERTER

AIR CONDITIONING UNIT

HOT WATER SERVICE

HOT WATER SERVICE

ARTICULATED FACE BRICKWORK

KSCM0050JB (5034L) ABOVE GROUND WATER TANK 2600 x 1150 x 1860H ON 2700 x 1250 PAD

26°

AJ

AJ

AJ

SOUTH ELEVATION

SCALE: 1:100

GLASS TYPE LEGEND

CLEAR

OBSCURE

WINDOW TYPE LEGEND

AWNING

DOUBLE HUNG

FIXED

LOUVRE

SLIDING

PLAN ACCEPTANCE BY OWNER

SIGNATURE: DATE:

SIGNATURE: DATE:

PLEASE NOTE THAT VARIATIONS WILL NOT BE ACCEPTED AFTER THIS PLAN ACCEPTANCE HAS BEEN SIGNED

REFER TO SHEET 1 (COVER SHEET) FOR ALL BUILDING INFORMATION REGARDING:

- SUSTAINABILITY REQUIREMENTS
- SITE CLASSIFICATION
- GENERAL BUILDING INFORMATION

SOME DETAILS ON THIS SHEET ARE INDICATIVE ONLY FOR EXAMPLE BRICKWORK AND CLADDING (EXPANSION JOINTS, ORIENTATION AND LAYOUT) AND ARE SUBJECT TO CHANGE.

SH = SNAP HEADER SILL


© 2024 MCDONALD JONES HOMES PTY LTD (ABN 82 003 687 232). THIS DRAWING IS AN ORIGINAL ARTISTIC WORK WITHIN THE MEANING OF THE COPYRIGHT ACT 1968 (CTH). MCDONALD JONES HOMES PTY LTD IS THE OWNER OF COPYRIGHT IN THIS DRAWING. YOU HEREBY AGREE AND UNDERTAKE THAT YOU WILL NOT IN ANY WAY REPRODUCE, COPY, MODIFY, USE OR TAKE ADVANTAGE OF THE DRAWING TO BUILD A HOUSE BASED ON THIS PLAN (WHETHER IN WHOLE OR IN PART) WITHOUT THE PRIOR WRITTEN CONSENT OF MCDONALD JONES HOMES PTY LTD.

mcdonald jones FIND YOURSELF AT HOME	SPECIFICATION: NOW		REVISION	DRAWN	CLIENT: LINH THANH THAO LE & HUU PHU LE	HOUSE DESIGN: SERRANO TWO	HOUSE CODE: H-SRNCCLAS21420	DO NOT SCALE DRAWINGS. USE FIGURED DIMENSIONS ONLY. CHECK AND VERIFY DIMENSIONS AND LEVELS PRIOR TO THE COMMENCEMENT OF ANY WORK. ALL DISCREPANCIES TO BE REPORTED TO THE DRAFTING OFFICE. 607126
	COPYRIGHT: © 2024	2	APPOINTMENT AMEDEMMENTS	LIR 01/02/2024	ADDRESS: 40 WEEMALA ROAD, CHESTER HILL NSW 2162	FACADE DESIGN: CLASSIC	FACADE CODE: F-SRNCCLAS01	
		3	WORKING DRAWINGS	TNT 07/02/2024	LOT / SECTION / DP: 42 / - / 15807	SHEET TITLE: ELEVATIONS	SHEET No.: 9 / 20	
		4	WD CHECK	ALW 13/02/2024	COUNCIL: CANTERBURY BANKSTOWN COUNCIL		SCALES: 1:100	
		5	AMENDED AS PER PCV003	ALW 01/03/2024				
		6	AMENDED AS PER PCV004	ALW 07/03/2024				


Last Published: Thursday, 7 March 2024 12:03 PM

File Location: G:\Sydney\Drafting\Job Files 60000\Job Files 60700\1 - 60720\1607126 - LePlan Model\607126 Le - AC24.pln


Template Version: 24.033

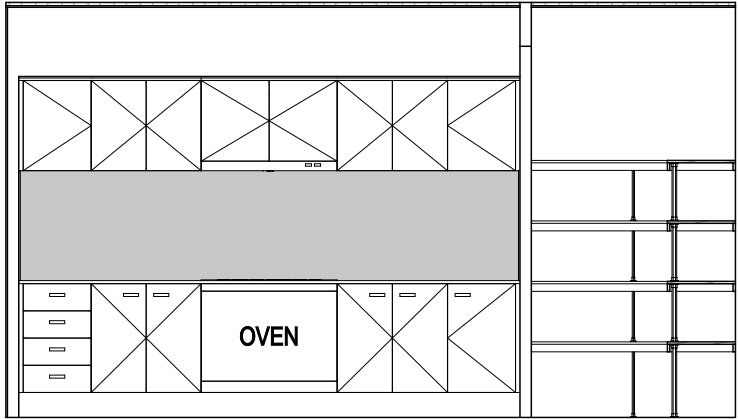


ELEVATION A
SCALE: 1:50

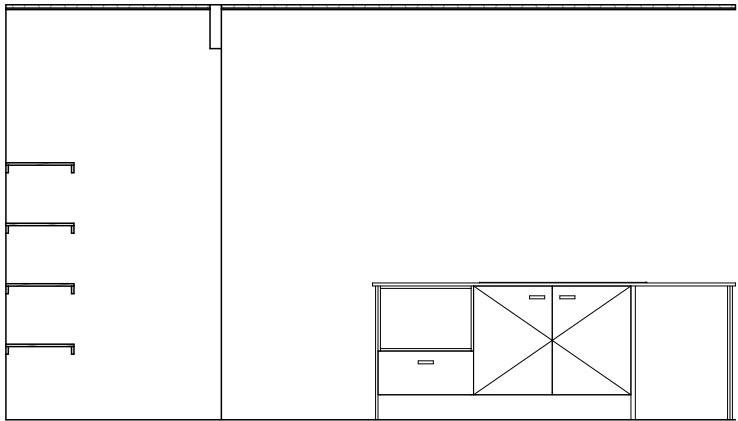

ELEVATION C
SCALE: 1:50

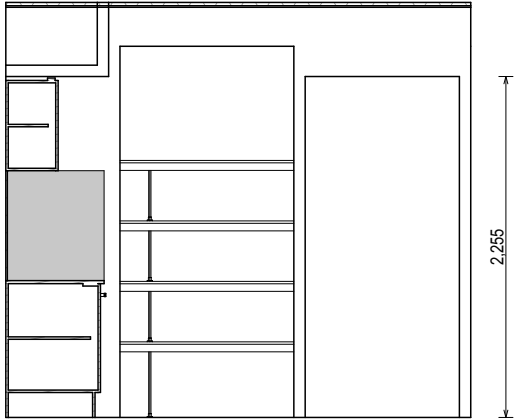


ELEVATION B
SCALE: 1:50


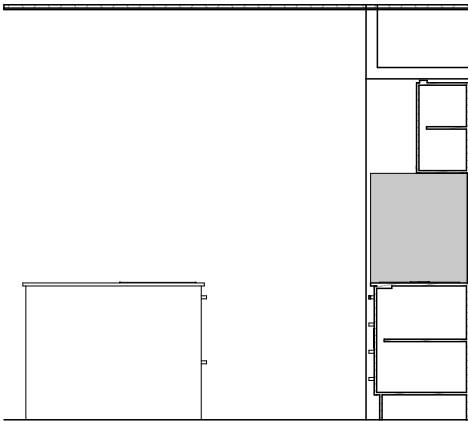


ELEVATION D
SCALE: 1:50

2255 FRAMED BULKHEAD TO
KITCHEN CUPBOARDS 2255
OFF FFL AND 680 FROM WALL

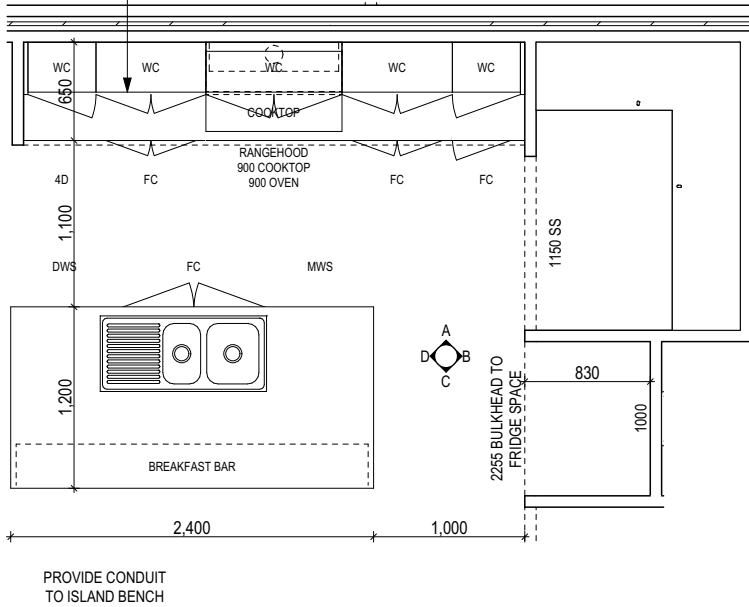

KITCHEN PLAN
SCALE: 1:50

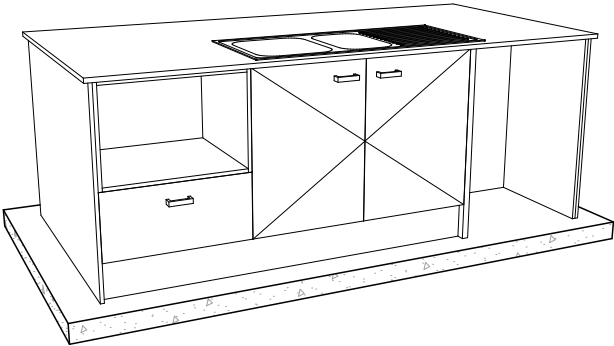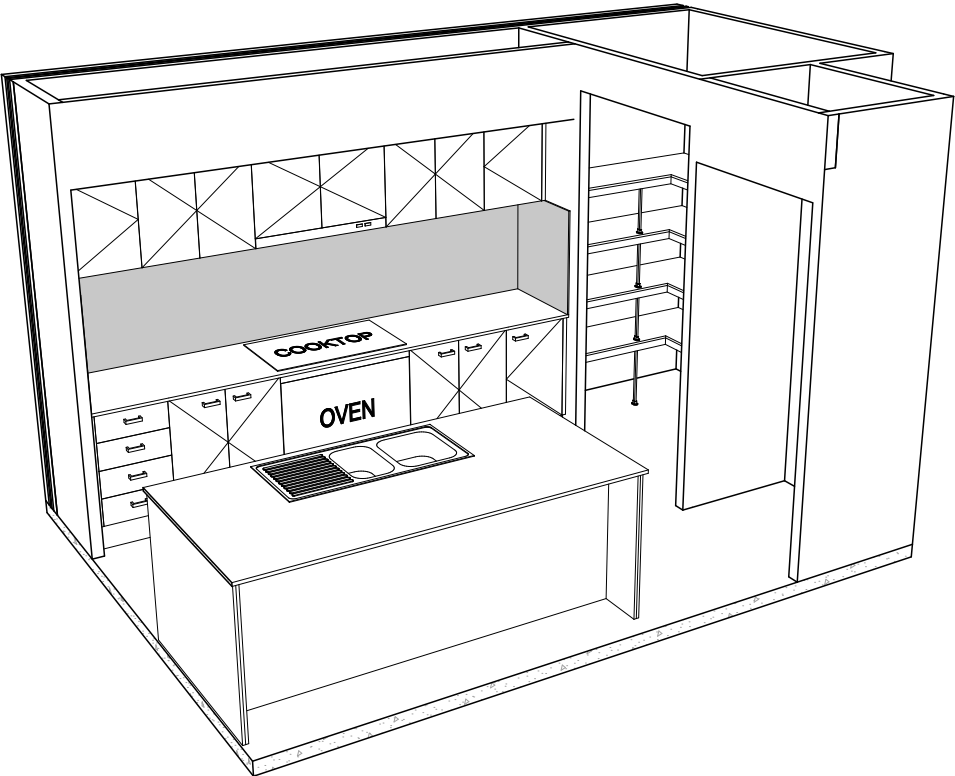

REFER TO SHEET 1 (COVER SHEET) FOR
ALL BUILDING INFORMATION REGARDING:
- SUSTAINABILITY REQUIREMENTS
- SITE CLASSIFICATION
- GENERAL BUILDING INFORMATION

DETAILS DEPICTED ON THIS SHEET ARE A
REPRESENTATION ONLY. JOINER MAY
ADJUST CABINETS AS REQUIRED.

**SUBJECT TO NCC 2022
(1 OCT 2023 + 7 STAR BASIX)**
WATERPROOFING & PLUMBING
CONDENSATION MANAGEMENT
7-STAR ENERGY EFFICIENCY

PLAN ACCEPTANCE BY OWNER

SIGNATURE:	DATE:
SIGNATURE:	DATE:

PLEASE NOTE THAT VARIATIONS WILL NOT BE ACCEPTED
AFTER THIS PLAN ACCEPTANCE HAS BEEN SIGNED

ALL DIMENSIONS ARE FRAME DIMENSIONS

© 2024 MCDONALD JONES HOMES PTY LTD (ABN 82 003 687 232). THIS DRAWING IS AN ORIGINAL ARTISTIC WORK WITHIN THE MEANING OF THE COPYRIGHT ACT 1968 (CTH). MCDONALD JONES HOMES PTY LTD IS THE OWNER OF COPYRIGHT IN THIS DRAWING. YOU HEREBY AGREE AND UNDERTAKE THAT YOU WILL NOT IN ANY WAY REPRODUCE, COPY, MODIFY, USE OR TAKE ADVANTAGE OF THE DRAWING TO BUILD A HOUSE BASED ON THIS PLAN (WHETHER IN WHOLE OR IN PART) WITHOUT THE PRIOR WRITTEN CONSENT OF MCDONALD JONES HOMES PTY LTD.







SPECIFICATION: NOW		REVISION		DRAWN		CLIENT:		HOUSE DESIGN:		HOUSE CODE:		DO NOT SCALE DRAWINGS, USE FIGURED DIMENSIONS ONLY. CHECK AND VERIFY DIMENSIONS AND LEVELS PRIOR TO THE COMMENCEMENT OF ANY WORK. ALL DISCREPANCIES TO BE REPORTED TO THE DRAFTING OFFICE.
	2	APPOINTMENT AMENDMENTS		LIR	01/02/2024	LINH THANH THAO LE & HUU PHU LE		SERRANO TWO		H-SRNCCLAS21420		
COPYRIGHT: © 2024	3	WORKING DRAWINGS		TNT	07/02/2024	ADDRESS:		FACADE DESIGN:		FACADE CODE:		
	4	WD CHECK		ALW	13/02/2024	40 WEEMALA ROAD, CHESTER HILL NSW 2162		CLASSIC		F-SRNCCLAS01		
	5	AMENDED AS PER PCV003		ALW	01/03/2024	LOT / SECTION / DP:		SHEET TITLE:		SHEET No.:	SCALES:	
	6	AMENDED AS PER PCV004		ALW	07/03/2024	42 / - / 15807		COUNCIL: CANTERBURY BANKSTOWN COUNCIL		10 / 20	1:50	
												607126

Last Published: Thursday, 7 March 2024 12:04 PM


File Location: G:\Sydney\Drafting\Job Files 600000\Job Files 607201 - 607201\607126 - Le\Plan Model\607126 Le - AC24.pln

RSHR	RAIL SHOWER
ROSE	SHOWER ROSE
ELBW	SHOWER ELBOW CONNECTION
MIX	MIXER TAP
HT	HOT TAP
CT	COLD TAP
HS	HOB SPOUT
WS	WALL SPOUT
SC	STOP COCK
TRH	TOILET ROLL HOLDER
TR-S	TOWEL RAIL - SINGLE
TR-D	TOWEL RAIL - DOUBLE
TL	TOWEL LADDER
TH	TOWEL HOLDER
TR	TOWEL RACK
TMB	TUMBLER HOLDER
RNG	TOWEL RING
RH	ROBE HOOK
SHLF	SHELF
SR	SHAMPOO RECESS
SOAP	SOAP HOLDER

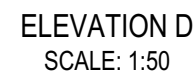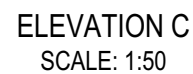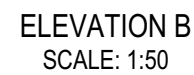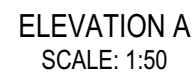


PLEASE NOTE THAT VARIATIONS WILL NOT BE ACCEPTED
AFTER THIS PLAN ACCEPTANCE HAS BEEN SIGNED


© 2024 MCDONALD JONES HOMES PTY LTD (ABN 82 003 687 232). THIS DRAWING IS AN ORIGINAL ARTISTIC WORK WITHIN THE MEANING OF THE COPYRIGHT ACT 1968 (CTH). MCDONALD JONES HOMES PTY LTD IS THE OWNER OF COPYRIGHT IN THIS DRAWING. YOU HEREBY AGREE AND UNDERTAKE THAT YOU WILL NOT IN ANY WAY REPRODUCE, COPY, MODIFY, USE OR TAKE ADVANTAGE OF THE DRAWING TO BUILD A HOUSE BASED ON THIS PLAN (WHETHER IN WHOLE OR IN PART) WITHOUT THE PRIOR WRITTEN CONSENT OF MCDONALD JONES HOMES PTY LTD.

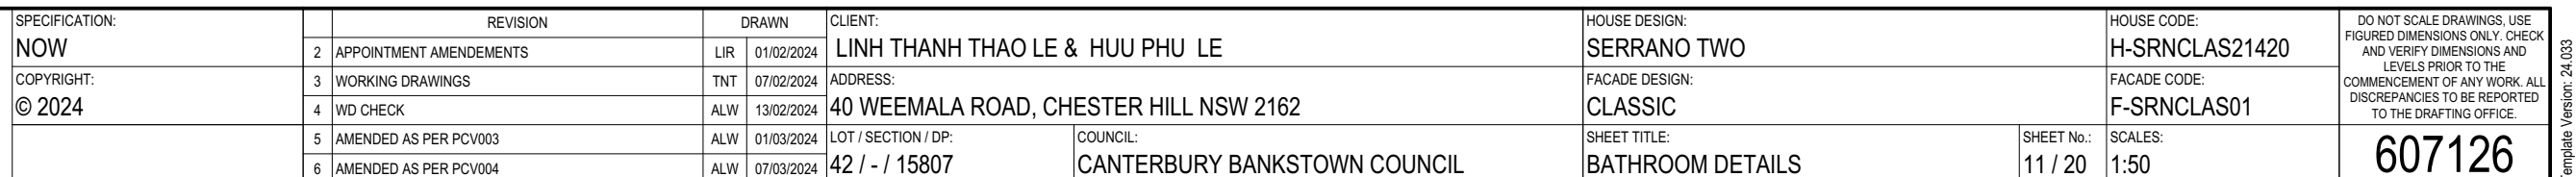


Template Version: 24.033

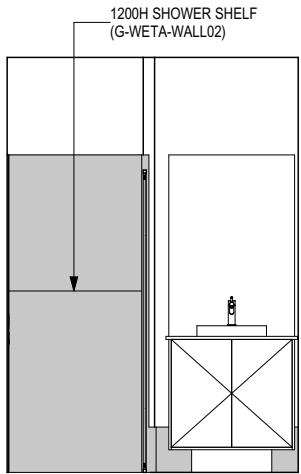


ELEVATION A
SCALE: 1:50

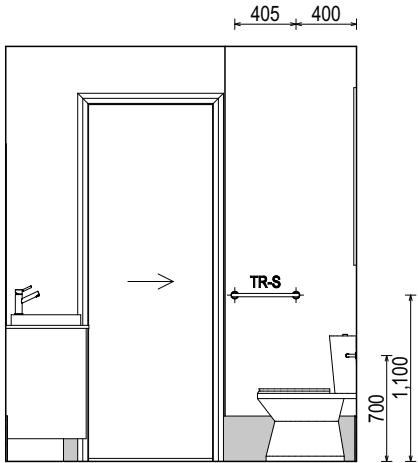


ELEVATION B
SCALE: 1:50

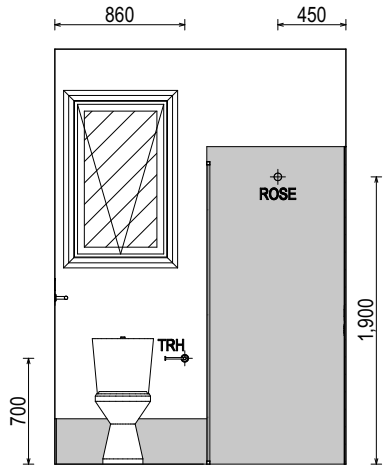

ELEVATION C
SCALE: 1:50

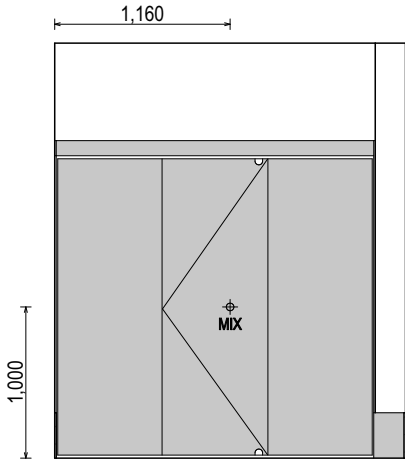

ELEVATION D
SCALE: 1:50

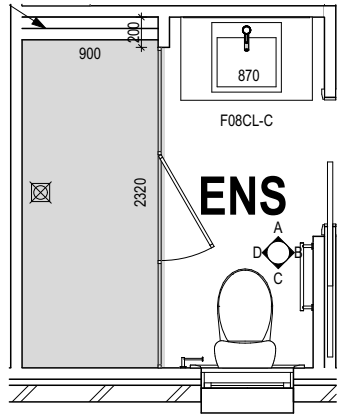

ENSUITE PLAN
SCALE: 1:50

REFER TO SHEET 1 (COVER SHEET) FOR ALL BUILDING INFORMATION REGARDING:

- SUSTAINABILITY REQUIREMENTS
- SITE CLASSIFICATION
- GENERAL BUILDING INFORMATION

DETAILS DEPICTED ON THIS SHEET ARE A REPRESENTATION ONLY

LEGEND

RSHR	RAIL SHOWER
ROSE	SHOWER ROSE
ELBW	SHOWER ELBOW CONNECTION
MIX	MIXER TAP
HT	HOT TAP
CT	COLD TAP
HS	HOB SPOUT
WS	WALL SPOUT
SC	STOP COCK
TRH	TOILET ROLL HOLDER
TR-S	TOWEL RAIL - SINGLE
TR-D	TOWEL RAIL - DOUBLE
TL	TOWEL LADDER
TH	TOWEL HOLDER
TR	TOWEL RACK
TMB	TUMBLER HOLDER
RNG	TOWEL RING
RH	ROBE HOOK
SHLF	SHELF
SR	SHAMPOO RECESS
SOAP	SOAP HOLDER

**SUBJECT TO NCC 2022
(1 OCT 2023 + 7 STAR BASIX)**
WATERPROOFING & PLUMBING
CONDENSATION MANAGEMENT
7-STAR ENERGY EFFICIENCY

PLAN ACCEPTANCE BY OWNER

SIGNATURE: DATE:

SIGNATURE: DATE:


PLEASE NOTE THAT VARIATIONS WILL NOT BE ACCEPTED AFTER THIS PLAN ACCEPTANCE HAS BEEN SIGNED

ALL DIMENSIONS ARE FRAME DIMENSIONS


© 2024 MCDONALD JONES HOMES PTY LTD (ABN 82 003 687 232). THIS DRAWING IS AN ORIGINAL ARTISTIC WORK WITHIN THE MEANING OF THE COPYRIGHT ACT 1968 (CTH). MCDONALD JONES HOMES PTY LTD IS THE OWNER OF COPYRIGHT IN THIS DRAWING. YOU HEREBY AGREE AND UNDERTAKE THAT YOU WILL NOT IN ANY WAY REPRODUCE, COPY, MODIFY, USE OR TAKE ADVANTAGE OF THE DRAWING TO BUILD A HOUSE BASED ON THIS PLAN (WHETHER IN WHOLE OR IN PART) WITHOUT THE PRIOR WRITTEN CONSENT OF MCDONALD JONES HOMES PTY LTD.




SPECIFICATION: NOW	REVISION	DRAWN	CLIENT:	HOUSE DESIGN:	HOUSE CODE:	DO NOT SCALE DRAWINGS. USE FIGURED DIMENSIONS ONLY. CHECK AND VERIFY DIMENSIONS AND LEVELS PRIOR TO THE COMMENCEMENT OF ANY WORK. ALL DISCREPANCIES TO BE REPORTED TO THE DRAFTING OFFICE. 607126
COPYRIGHT: © 2024	2 APPOINTMENT AMENDMENTS	LIR 01/02/2024	LINH THANH THAO LE & HUU PHU LE	SERRANO TWO	H-SRNCLAS21420	
	3 WORKING DRAWINGS	TNT 07/02/2024	ADDRESS: 40 WEEMALA ROAD, CHESTER HILL NSW 2162	FACADE DESIGN: CLASSIC	FACADE CODE: F-SRNCLAS01	
	4 WD CHECK	ALW 13/02/2024	LOT / SECTION / DP:	SHEET TITLE:	SCALES:	
	5 AMENDED AS PER PCV003	ALW 01/03/2024	COUNCIL: CANTERBURY BANKSTOWN COUNCIL	12 / 20	1:50	
	6 AMENDED AS PER PCV004	ALW 07/03/2024	42 / - / 15807	ENSUITE DETAILS		

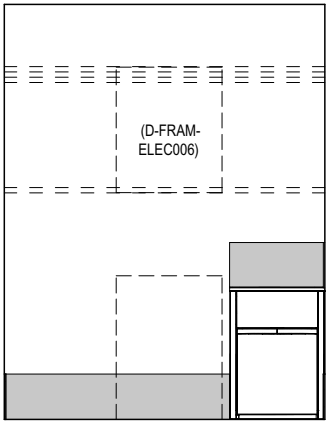


ELEVATION A
SCALE: 1:50

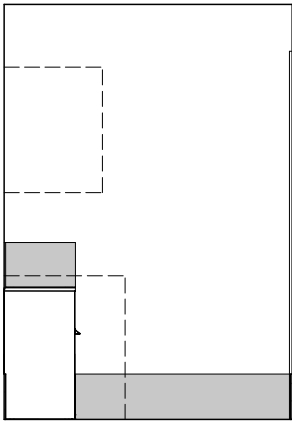


ELEVATION B
SCALE: 1:50

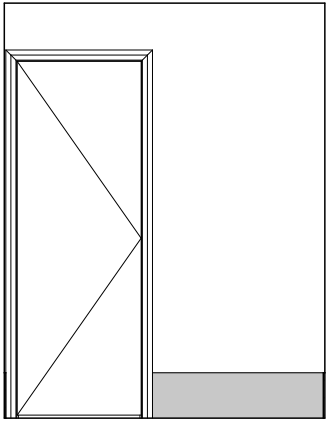

ELEVATION C
SCALE: 1:50

 

ELEVATION D
SCALE: 1:50

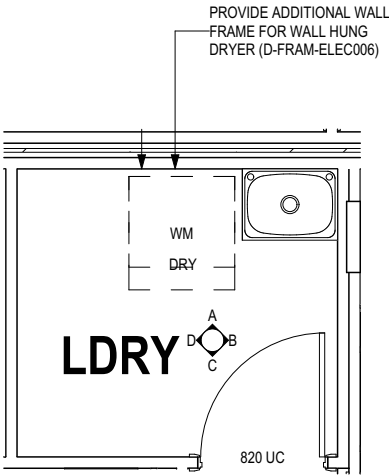

LAUNDRY PLAN
SCALE: 1:50

REFER TO SHEET 1 (COVER SHEET) FOR ALL BUILDING INFORMATION REGARDING:
- SUSTAINABILITY REQUIREMENTS
- SITE CLASSIFICATION
- GENERAL BUILDING INFORMATION

DETAILS DEPICTED ON THIS SHEET ARE A REPRESENTATION ONLY

PROVIDE ADDITIONAL NOGGING TO LAUNDRY FOR FIXING OF WALL MOUNTED CLOTHES DRYER AS PER D-FRAM-ELEC006

LEGEND

RSHR	RAIL SHOWER
ROSE	SHOWER ROSE
ELBW	SHOWER ELBOW CONNECTION
MIX	MIXER TAP
HT	HOT TAP
CT	COLD TAP
HS	HOB SPOUT
WS	WALL SPOUT
SC	STOP COCK
TRH	TOILET ROLL HOLDER
TR-S	TOWEL RAIL - SINGLE
TR-D	TOWEL RAIL - DOUBLE
TL	TOWEL LADDER
TH	TOWEL HOLDER
TR	TOWEL RACK
TMB	TUMBLER HOLDER
RNG	TOWEL RING
RH	ROBE HOOK
SHLF	SHELF
SR	SHAMPOO RECESS
SOAP	SOAP HOLDER

**SUBJECT TO NCC 2022
(1 OCT 2023 + 7 STAR BASIX)**
WATERPROOFING & PLUMBING
CONDENSATION MANAGEMENT
7-STAR ENERGY EFFICIENCY

PLAN ACCEPTANCE BY OWNER

SIGNATURE: DATE:

SIGNATURE: DATE:

PLEASE NOTE THAT VARIATIONS WILL NOT BE ACCEPTED AFTER THIS PLAN ACCEPTANCE HAS BEEN SIGNED

ALL DIMENSIONS ARE FRAME DIMENSIONS

© 2024 MCDONALD JONES HOMES PTY LTD (ABN 82 003 687 232). THIS DRAWING IS AN ORIGINAL ARTISTIC WORK WITHIN THE MEANING OF THE COPYRIGHT ACT 1968 (CTH). MCDONALD JONES HOMES PTY LTD IS THE OWNER OF COPYRIGHT IN THIS DRAWING. YOU HEREBY AGREE AND UNDERTAKE THAT YOU WILL NOT IN ANY WAY REPRODUCE, COPY, MODIFY, USE OR TAKE ADVANTAGE OF THE DRAWING TO BUILD A HOUSE BASED ON THIS PLAN (WHETHER IN WHOLE OR IN PART) WITHOUT THE PRIOR WRITTEN CONSENT OF MCDONALD JONES HOMES PTY LTD.




SPECIFICATION: NOW	REVISION 2 APPOINTMENT AMEDEMMENTS	DRAWN LIR 01/02/2024	CLIENT: LINH THANH THAO LE & HUU PHU LE	HOUSE DESIGN: SERRANO TWO	HOUSE CODE: H-SRNCCLAS21420	DO NOT SCALE DRAWINGS. USE FIGURED DIMENSIONS ONLY. CHECK AND VERIFY DIMENSIONS AND LEVELS PRIOR TO THE COMMENCEMENT OF ANY WORK. ALL DISCREPANCIES TO BE REPORTED TO THE DRAFTING OFFICE. 607126
COPYRIGHT: © 2024	3 WORKING DRAWINGS	TNT 07/02/2024	ADDRESS: 40 WEEMALA ROAD, CHESTER HILL NSW 2162	FACADE DESIGN: CLASSIC	FACADE CODE: F-SRNCCLAS01	
	4 WD CHECK	ALW 13/02/2024	LOT / SECTION / DP: 42 / - / 15807	SHEET TITLE: LAUNDRY DETAILS	SHEET No.: 14 / 20	
	5 AMENDED AS PER PCV003	ALW 01/03/2024	COUNCIL: CANTERBURY BANKSTOWN COUNCIL		SCALES: 1:50	
	6 AMENDED AS PER PCV004	ALW 07/03/2024				


REFER TO SHEET 1 (COVER SHEET) FOR ALL BUILDING INFORMATION REGARDING:

- SUSTAINABILITY REQUIREMENTS
- SITE CLASSIFICATION
- GENERAL BUILDING INFORMATION


DETAILS DEPICTED ON THIS SHEET ARE A REPRESENTATION ONLY. JOINER MAY ADJUST CABINETRY AS REQUIRED.

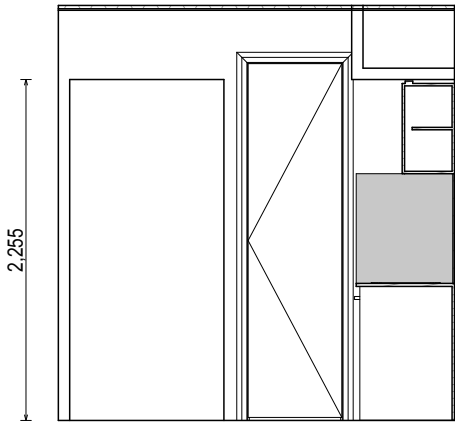


ELEVATION A
SCALE: 1:50

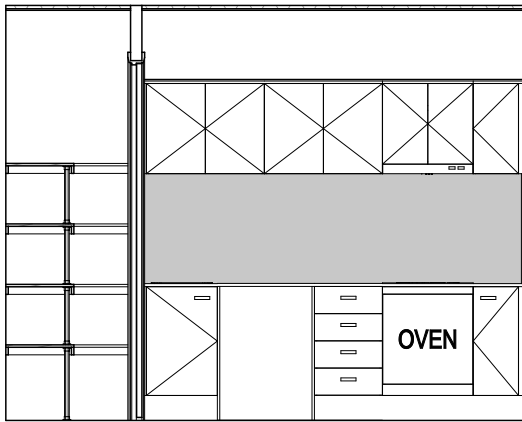


ELEVATION B
SCALE: 1:50

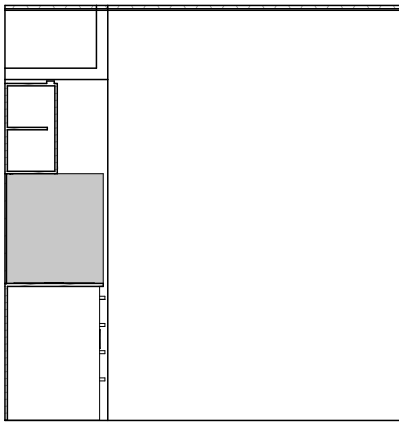


ELEVATION C
SCALE: 1:50

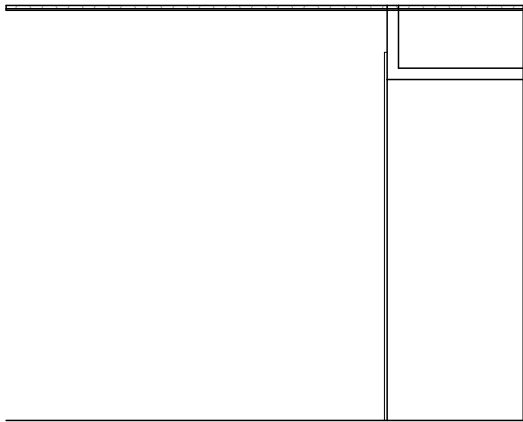

ELEVATION D
SCALE: 1:50

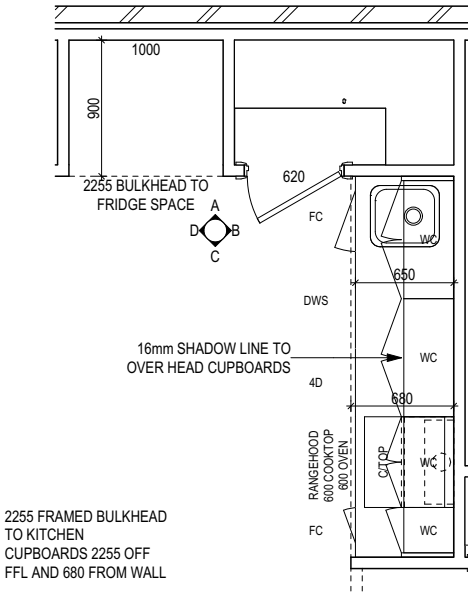

KITCHEN PLAN (GRANNY FLAT)
SCALE: 1:50

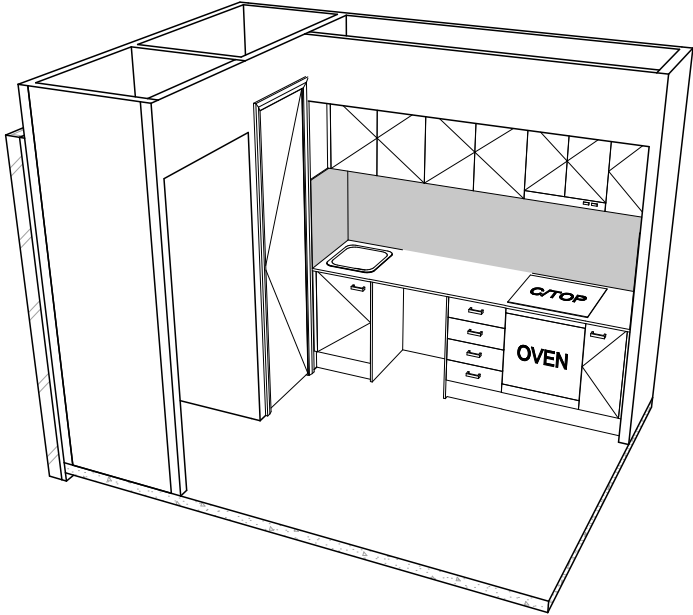

**SUBJECT TO NCC 2022
(1 OCT 2023 + 7 STAR BASIX)**
WATERPROOFING & PLUMBING
CONDENSATION MANAGEMENT
7-STAR ENERGY EFFICIENCY

PLAN ACCEPTANCE BY OWNER

SIGNATURE: _____ DATE: _____

SIGNATURE: _____ DATE: _____

PLEASE NOTE THAT VARIATIONS WILL NOT BE ACCEPTED AFTER THIS PLAN ACCEPTANCE HAS BEEN SIGNED

ALL DIMENSIONS ARE FRAME DIMENSIONS

© 2024 MCDONALD JONES HOMES PTY LTD (ABN 82 003 687 232). THIS DRAWING IS AN ORIGINAL ARTISTIC WORK WITHIN THE MEANING OF THE COPYRIGHT ACT 1968 (CTH). MCDONALD JONES HOMES PTY LTD IS THE OWNER OF COPYRIGHT IN THIS DRAWING. YOU HEREBY AGREE AND UNDERTAKE THAT YOU WILL NOT IN ANY WAY REPRODUCE, COPY, MODIFY, USE OR TAKE ADVANTAGE OF THE DRAWING TO BUILD A HOUSE BASED ON THIS PLAN (WHETHER IN WHOLE OR IN PART) WITHOUT THE PRIOR WRITTEN CONSENT OF MCDONALD JONES HOMES PTY LTD.



SPECIFICATION:		REVISION		DRAWN		CLIENT:		HOUSE DESIGN:		HOUSE CODE:		DO NOT SCALE DRAWINGS, USE FIGURED DIMENSIONS ONLY. CHECK AND VERIFY DIMENSIONS AND LEVELS PRIOR TO THE COMMENCEMENT OF ANY WORK. ALL DISCREPANCIES TO BE REPORTED TO THE DRAFTING OFFICE.	
NOW		2	APPOINTMENT AMEDEMMENTS	LIR	01/02/2024	LINH THANH THAO LE & HUU PHU LE		SERRANO TWO		H-SRNCCLAS21420			
COPYRIGHT:		3	WORKING DRAWINGS	TNT	07/02/2024	ADDRESS:		FACADE DESIGN:		FACADE CODE:			
© 2024		4	WD CHECK	ALW	13/02/2024	40 WEEMALA ROAD, CHESTER HILL NSW 2162		CLASSIC		F-SRNCCLAS01			
		5	AMENDED AS PER PCV003	ALW	01/03/2024	LOT / SECTION / DP:		SHEET TITLE:		SHEET No.:	SCALES:		
		6	AMENDED AS PER PCV004	ALW	07/03/2024	42 / - / 15807		CANTERBURY BANKSTOWN COUNCIL		15 / 20	1:50		
													607126


REFER TO SHEET 1 (COVER SHEET) FOR
ALL BUILDING INFORMATION REGARDING:

- SUSTAINABILITY REQUIREMENTS
- SITE CLASSIFICATION
- GENERAL BUILDING INFORMATION


DETAILS DEPICTED ON THIS SHEET ARE A REPRESENTATION ONLY

LEGEND


RSHR	RAIL SHOWER
ROSE	SHOWER ROSE
ELBW	SHOWER ELBOW CONNECTION
MIX	MIXER TAP
HT	HOT TAP
CT	COLD TAP
HS	HOB SPOUT
WS	WALL SPOUT
SC	STOP COCK
TRH	TOILET ROLL HOLDER
TR-S	TOWEL RAIL - SINGLE
TR-D	TOWEL RAIL - DOUBLE
TL	TOWEL LADDER
TH	TOWEL HOLDER
TR	TOWEL RACK
TMB	TUMBLER HOLDER
RNG	TOWEL RING
RH	ROBE HOOK
SHLF	SHELF
SR	SHAMPOO RECESS
SOAP	SOAP HOLDER

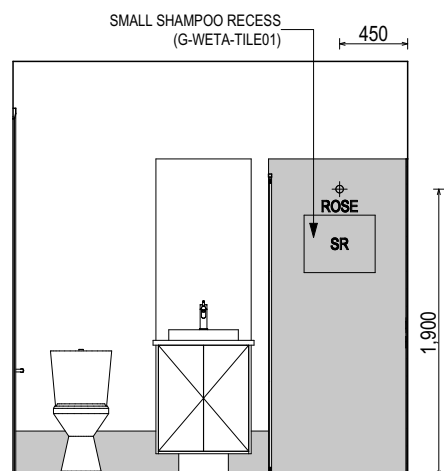


ELEVATION A
SCALE: 1:50

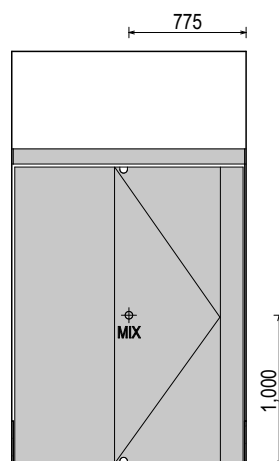


ELEVATION B
SCALE: 1:50

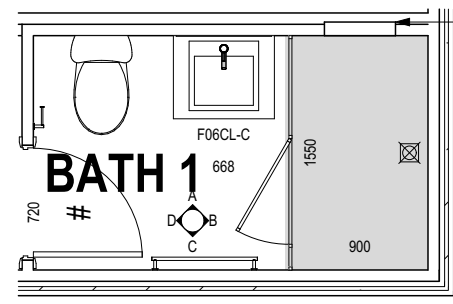

BATHROOM 1 PLAN (GRANNY FLAT)
SCALE: 1:50

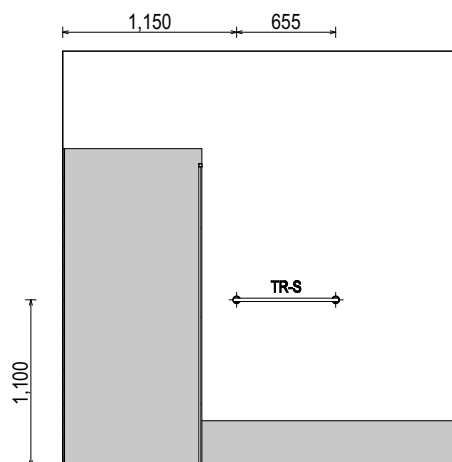

ELEVATION C
SCALE: 1:50

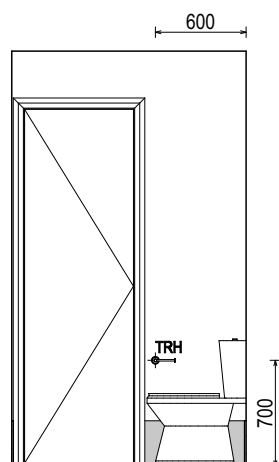

ELEVATION D
SCALE: 1:50

**SUBJECT TO NCC 2022
(1 OCT 2023 + 7 STAR BASIX)
WATERPROOFING & PLUMBING
CONDENSATION MANAGEMENT
7-STAR ENERGY EFFICIENCY**

PLAN ACCEPTANCE BY OWNER

SIGNATURE:	DATE:
------------	-------

SIGNATURE: _____ DATE: _____

PLEASE NOTE THAT VARIATIONS WILL NOT BE ACCEPTED
AFTER THIS PLAN ACCEPTANCE HAS BEEN SIGNED

ALL DIMENSIONS ARE FRAME DIMENSIONS

© 2024 MCDONALD JONES HOMES PTY LTD (ABN 82 003 687 232). THIS DRAWING IS AN ORIGINAL ARTISTIC WORK WITHIN THE MEANING OF THE COPYRIGHT ACT 1968 (CTH). MCDONALD JONES HOMES PTY LTD IS THE OWNER OF COPYRIGHT IN THIS DRAWING. YOU HEREBY AGREE AND UNDERTAKE THAT YOU WILL NOT IN ANY WAY REPRODUCE, COPY, MODIFY, USE OR TAKE ADVANTAGE OF THE DRAWING TO BUILD A HOUSE BASED ON THIS PLAN (WHETHER IN WHOLE OR IN PART) WITHOUT THE PRIOR WRITTEN CONSENT OF MCDONALD JONES HOMES PTY LTD.

 mcDonald jones FIND YOURSELF AT HOME	SPECIFICATION:		REVISION		DRAWN		CLIENT:				HOUSE DESIGN:				HOUSE CODE:		DO NOT SCALE DRAWINGS. USE FIGURED DIMENSIONS ONLY. CHECK AND VERIFY DIMENSIONS AND LEVELS PRIOR TO THE COMMENCEMENT OF ANY WORK. ALL DISCREPANCIES TO BE REPORTED TO THE DRAFTING OFFICE.	
	NOW		2	APPOINTMENT AMEDEMMENTS		LIR	01/02/2024	LINH THANH THAO LE & HUU PHU LE				SERRANO TWO				H-SRNCCLAS21420		
	COPYRIGHT:		3	WORKING DRAWINGS		TNT	07/02/2024	ADDRESS:				FACADE DESIGN:				FACADE CODE:		
	© 2024		4	WD CHECK		ALW	13/02/2024	40 WEEMALA ROAD, CHESTER HILL NSW 2162				CLASSIC				F-SRNCCLAS01		
			5	AMENDED AS PER PCV003		ALW	01/03/2024	LOT / SECTION / DP:		COUNCIL:		SHEET TITLE:		SHEET No.:	SCALES:			
			6	AMENDED AS PER PCV004		ALW	07/03/2024	42 / - / 15807		CANTERBURY BANKSTOWN COUNCIL		BATHROOM 1 DETAILS (GRANNY FLAT)		16 / 20	1:50			

607126

REFER TO SHEET 1 (COVER SHEET) FOR ALL BUILDING INFORMATION REGARDING:


- SUSTAINABILITY REQUIREMENTS
- SITE CLASSIFICATION
- GENERAL BUILDING INFORMATION

DETAILS DEPICTED ON THIS SHEET ARE A REPRESENTATION ONLY


PROVIDE ADDITIONAL NOGGING TO LAUNDRY FOR FIXING OF WALL MOUNTED CLOTHES DRYER AS PER D-FRAM-ELEC006

LEGEND


- | | |
|------|-------------------------|
| RSHR | RAIL SHOWER |
| ROSE | SHOWER ROSE |
| ELBW | SHOWER ELBOW CONNECTION |
| MIX | MIXER TAP |
| HT | HOT TAP |
| CT | COLD TAP |
| HS | HOB SPOUT |
| WS | WALL SPOUT |
| SC | STOP COCK |
| TRH | TOILET ROLL HOLDER |
| TR-S | TOWEL RAIL - SINGLE |
| TR-D | TOWEL RAIL - DOUBLE |
| TL | TOWEL LADDER |
| TH | TOWEL HOLDER |
| TR | TOWEL RACK |
| TMB | TUMBLER HOLDER |
| RNG | TOWEL RING |
| RH | ROBE HOOK |
| SHLF | SHELF |
| SR | SHAMPOO RECESS |
| SOAP | SOAP HOLDER |

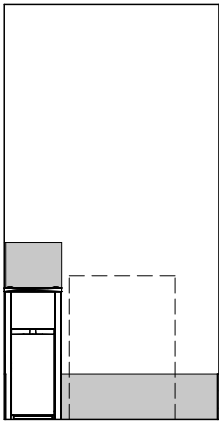


ELEVATION A
SCALE: 1:50

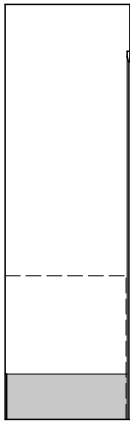


ELEVATION B
SCALE: 1:50

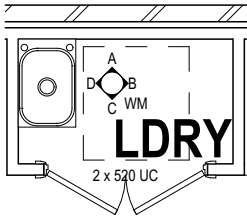

LAUNDRY 1 PLAN (GRANNY FLAT)
SCALE: 1:50

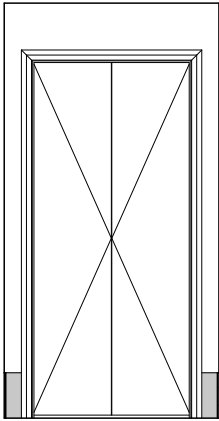

ELEVATION C
SCALE: 1:50

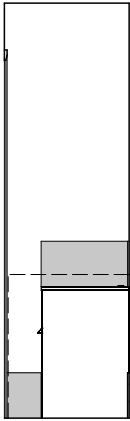

ELEVATION D
SCALE: 1:50

**SUBJECT TO NCC 2022
(1 OCT 2023 + 7 STAR BASIX)**
WATERPROOFING & PLUMBING
CONDENSATION MANAGEMENT
7-STAR ENERGY EFFICIENCY

PLAN ACCEPTANCE BY OWNER

SIGNATURE: DATE:

SIGNATURE: DATE:

PLEASE NOTE THAT VARIATIONS WILL NOT BE ACCEPTED AFTER THIS PLAN ACCEPTANCE HAS BEEN SIGNED

ALL DIMENSIONS ARE FRAME DIMENSIONS

© 2024 MCDONALD JONES HOMES PTY LTD (ABN 82 003 687 232). THIS DRAWING IS AN ORIGINAL ARTISTIC WORK WITHIN THE MEANING OF THE COPYRIGHT ACT 1968 (CTH). MCDONALD JONES HOMES PTY LTD IS THE OWNER OF COPYRIGHT IN THIS DRAWING. YOU HEREBY AGREE AND UNDERTAKE THAT YOU WILL NOT IN ANY WAY REPRODUCE, COPY, MODIFY, USE OR TAKE ADVANTAGE OF THE DRAWING TO BUILD A HOUSE BASED ON THIS PLAN (WHETHER IN WHOLE OR IN PART) WITHOUT THE PRIOR WRITTEN CONSENT OF MCDONALD JONES HOMES PTY LTD.



SPECIFICATION:		REVISION	DRAWN	CLIENT:	HOUSE DESIGN:	HOUSE CODE:	DO NOT SCALE DRAWINGS, USE FIGURED DIMENSIONS ONLY. CHECK AND VERIFY DIMENSIONS AND LEVELS PRIOR TO THE COMMENCEMENT OF ANY WORK. ALL DISCREPANCIES TO BE REPORTED TO THE DRAFTING OFFICE.	
NOW	2	APPOINTMENT AMEDEMMENTS	LIR 01/02/2024	LINH THANH THAO LE & HUU PHU LE	SERRANO TWO	H-SRNCCLAS21420		
COPYRIGHT:	3	WORKING DRAWINGS	TNT 07/02/2024	ADDRESS:	FACADE DESIGN:	FACADE CODE:		
© 2024	4	WD CHECK	ALW 13/02/2024	40 WEEMALA ROAD, CHESTER HILL NSW 2162	CLASSIC	F-SRNCCLAS01		
	5	AMENDED AS PER PCV003	ALW 01/03/2024	LOT / SECTION / DP:	SHEET TITLE:	SHEET No.:		
	6	AMENDED AS PER PCV004	ALW 07/03/2024	42 / - / 15807	COUNCIL:	SCALES:		
				CANTERBURY BANKSTOWN COUNCIL	LAUNDRY DETAILS (GRANNY FLAT)	17 / 20	1:50	607126

607126

FLOOR TILES SHOWN ON PLAN DO NOT INDICATE THE SIZE OR JOINT LOCATIONS OF THE ACTUAL FLOOR TILES. TIMBER FLOORING SHOWN ON PLAN DOES NOT INDICATE THE BOARD SIZE OR DIRECTION OF THE ACTUAL FLOORING.

	NO COVERING
	COVER GRADE CONCRETE
	CARPET
	TIMBER/LAMINATE (BY OWNER)
	TILE (STANDARD WET AREAS)
	TILE (UPGRADED AREAS)
	VINYL



FLOOR COVERINGS
SCALE: 1:100

**SUBJECT TO NCC 2022
(1 OCT 2023 + 7 STAR BASIX)
WATERPROOFING & PLUMBING
CONDENSATION MANAGEMENT
7-STAR ENERGY EFFICIENCY**


SIGNATURE: _____	DATE: _____
SIGNATURE: _____	DATE: _____
PLEASE NOTE THAT VARIATIONS WILL NOT BE ACCEPTED AFTER THIS PLAN ACCEPTANCE HAS BEEN SIGNED	

© 2024 MCDONALD JONES HOMES PTY LTD (ABN 82 003 687 232). THIS DRAWING IS AN ORIGINAL ARTISTIC WORK WITHIN THE MEANING OF THE COPYRIGHT ACT 1968 (CTH). MCDONALD JONES HOMES PTY LTD IS THE OWNER OF COPYRIGHT IN THIS DRAWING. YOU HEREBY AGREE AND UNDERTAKE THAT YOU WILL NOT IN ANY WAY REPRODUCE, COPY, MODIFY, USE OR TAKE ADVANTAGE OF THE DRAWING TO BUILD A HOUSE BASED ON THIS PLAN (WHETHER IN WHOLE OR IN PART) WITHOUT THE PRIOR WRITTEN CONSENT OF MCDONALD JONES HOMES PTY LTD.



SPECIFICATION:		REVISION	DRAWN	CLIENT:	HOUSE DESIGN:	HOUSE CODE:	DO NOT SCALE DRAWINGS, USE FIGURED DIMENSIONS ONLY. CHECK AND VERIFY DIMENSIONS AND LEVELS PRIOR TO THE COMMENCEMENT OF ANY WORK. DISCREPANCIES TO BE REPORT TO THE DRAFTING OFFICE.
NOW	2	APPOINTMENT AMEDEMEMENTS	LIR 01/02/2024	LINH THANH THAO LE & HUU PHU LE	SERRANO TWO	H-SRNCCLAS21420	
COPYRIGHT:	3	WORKING DRAWINGS	TNT 07/02/2024	ADDRESS:	FACADE DESIGN:	FACADE CODE:	
© 2024	4	WD CHECK	ALW 13/02/2024	40 WEEMALA ROAD, CHESTER HILL NSW 2162	CLASSIC	F-SRNCCLAS01	
	5	AMENDED AS PER PCV003	ALW 01/03/2024	LOT / SECTION / DP:	SHEET TITLE:	SHEET No.:	
	6	AMENDED AS PER PCV004	ALW 07/03/2024	42 / - / 15807	COUNCIL: CANTERBURY BANKSTOWN COUNCIL	FLOOR COVERINGS	18 / 20
						SCALES:	607126
						1:100	

ALL EXTERIOR SLABS TO BE GRADED BY CONCRETER TO ACHIEVE APPROX. 1:100 FALL TO OUTSIDE EDGE WITH MAXIMUM CROSSFALL OF 30mm OVER ENTIRE SLAB.

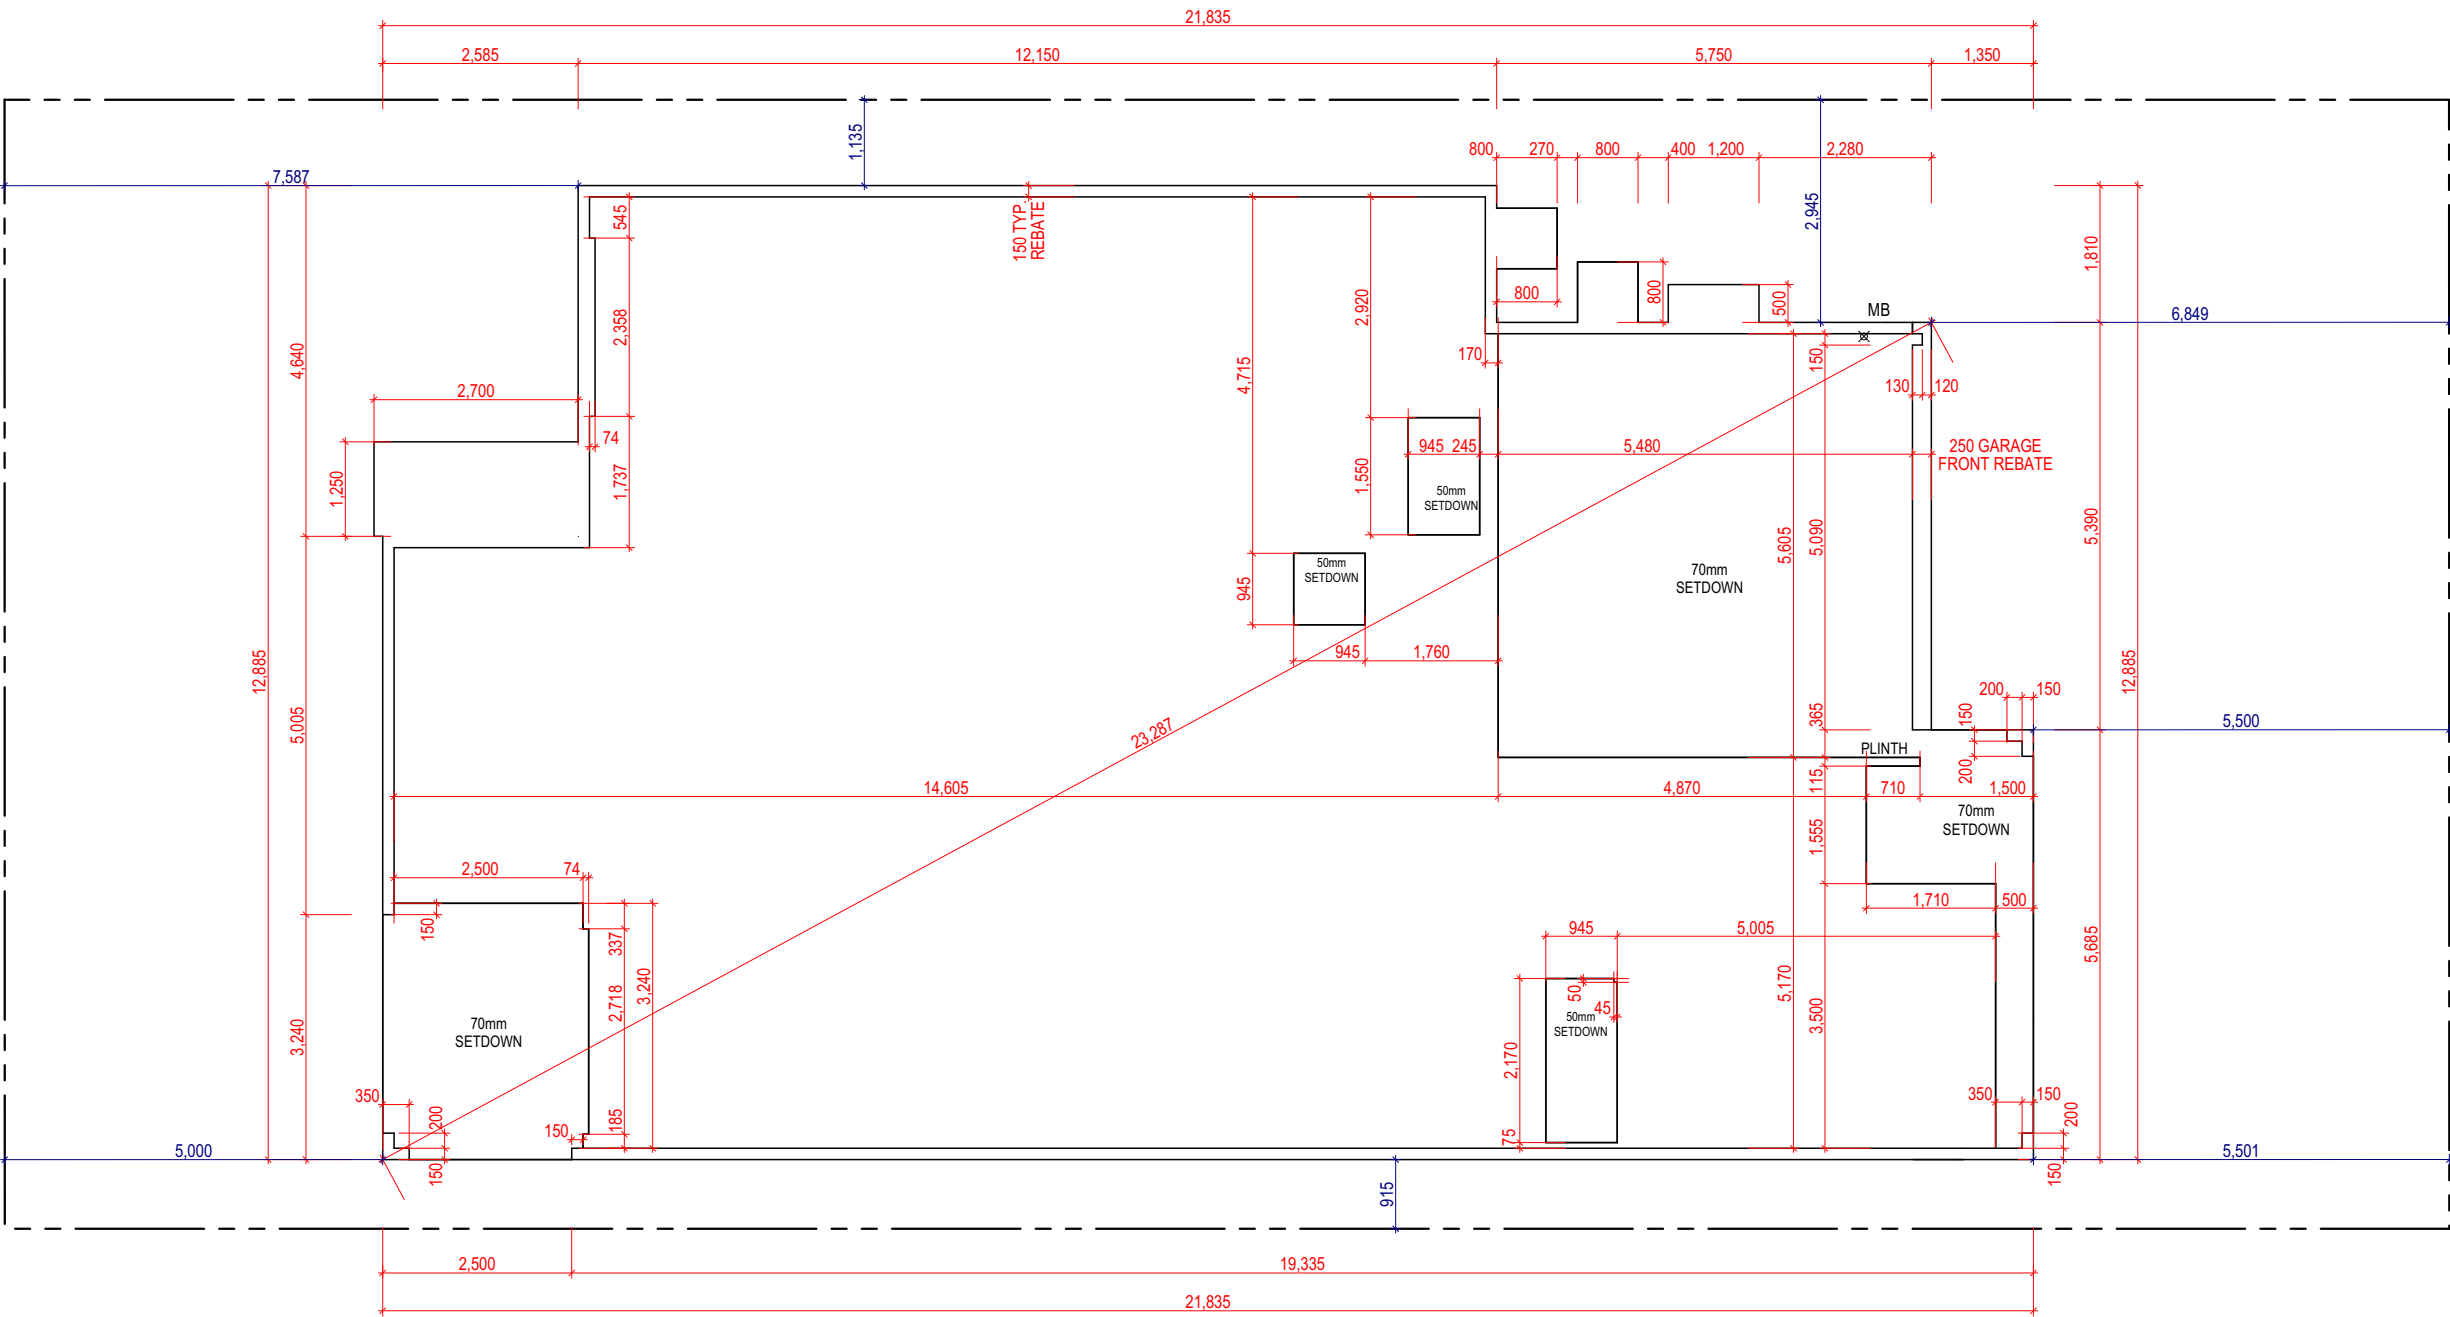

SLAB PLAN
SCALE: 1:100


**SUBJECT TO NCC 2022
(1 OCT 2023 + 7 STAR BASIX)
WATERPROOFING & PLUMBING
CONDENSATION MANAGEMENT
7-STAR ENERGY EFFICIENCY**

© 2024 MCDONALD JONES HOMES PTY LTD (ABN 82 003 687 232). THIS DRAWING IS AN ORIGINAL ARTISTIC WORK WITHIN THE MEANING OF THE COPYRIGHT ACT 1968 (CTH). MCDONALD JONES HOMES PTY LTD IS THE OWNER OF COPYRIGHT IN THIS DRAWING. YOU HEREBY AGREE AND UNDERTAKE THAT YOU WILL NOT IN ANY WAY REPRODUCE, COPY, MODIFY, USE OR TAKE ADVANTAGE OF THE DRAWING TO BUILD A HOUSE BASED ON THIS PLAN (WHETHER IN WHOLE OR IN PART) WITHOUT THE PRIOR WRITTEN CONSENT OF MCDONALD JONES HOMES PTY LTD.



SPECIFICATION: NOW		REVISION		DRAWN		CLIENT: LINH THANH THAO LE & HUU PHU LE		HOUSE DESIGN: SERRANO TWO		HOUSE CODE: H-SRNCCLAS21420		DO NOT SCALE DRAWINGS, USE FIGURED DIMENSIONS ONLY. CHECK AND VERIFY DIMENSIONS AND LEVELS PRIOR TO THE COMMENCEMENT OF ANY WORK. ALL DISCREPANCIES TO BE REPORTED TO THE DRAFTING OFFICE.		
	2	APPOINTMENT AMENDMENTS		LIR	01/02/2024									
COPYRIGHT: © 2024	3	WORKING DRAWINGS		TNT	07/02/2024	ADDRESS: 40 WEEMALA ROAD, CHESTER HILL NSW 2162		FACADE DESIGN: CLASSIC		FACADE CODE: F-SRNCCLAS01				
	4	WD CHECK		ALW	13/02/2024									
	5	AMENDED AS PER PCV003		ALW	01/03/2024	LOT / SECTION / DP: 42 / - / 15807		COUNCIL: CANTERBURY BANKSTOWN COUNCIL		SHEET TITLE: SLAB PLAN			SHEET No.: 19 / 20	SCALES: 1:100
	6	AMENDED AS PER PCV004		ALW	07/03/2024									

ALL EXTERIOR SLABS TO BE GRADED BY CONCRETER TO ACHIEVE APPROX. 1:100 FALL TO OUTSIDE EDGE WITH MAXIMUM CROSSFALL OF 30mm OVER ENTIRE SLAB.

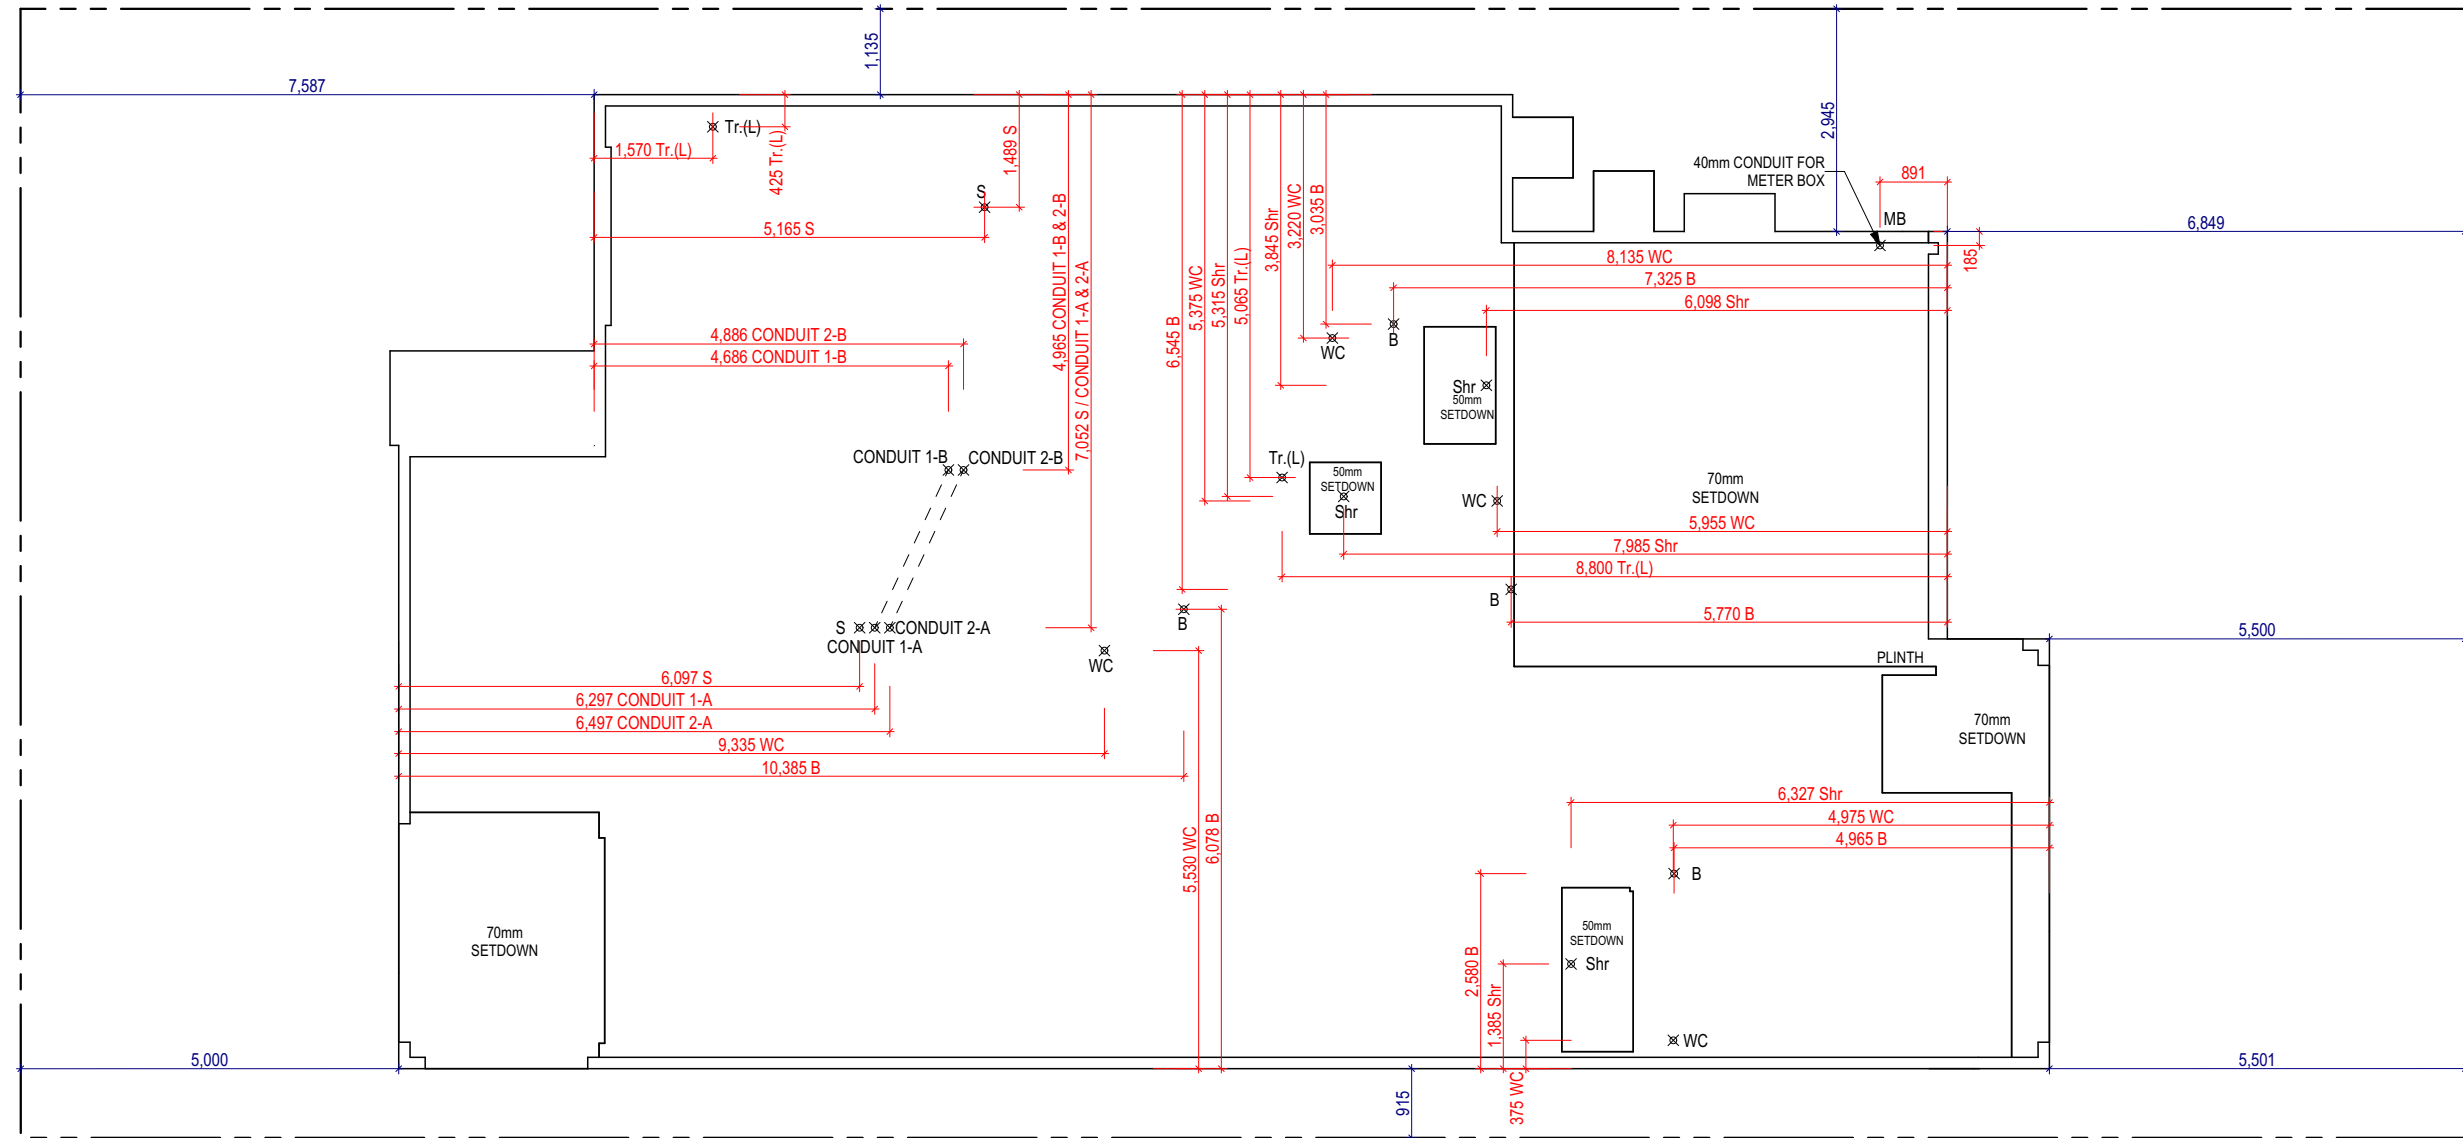

DRAINAGE PLAN

SCALE: 1:100

LEGEND

B	BASIN
Bth	BATH WASTE
FW	FLOOR WASTE GULLY
Shr	SHOWER
S	SINK (KITCHEN)
Tr.(L)	TROUGH (LAUNDRY)
WC	WATER CLOSET

**SUBJECT TO NCC 2022
(1 OCT 2023 + 7 STAR BASIX)
WATERPROOFING & PLUMBING
CONDENSATION MANAGEMENT
7-STAR ENERGY EFFICIENCY**

© 2024 MCDONALD JONES HOMES PTY LTD (ABN 82 003 687 232). THIS DRAWING IS AN ORIGINAL ARTISTIC WORK WITHIN THE MEANING OF THE COPYRIGHT ACT 1968 (CTH). MCDONALD JONES HOMES PTY LTD IS THE OWNER OF COPYRIGHT IN THIS DRAWING. YOU HEREBY AGREE AND UNDERTAKE THAT YOU WILL NOT IN ANY WAY REPRODUCE, COPY, MODIFY, USE OR TAKE ADVANTAGE OF THE DRAWING TO BUILD A HOUSE BASED ON THIS PLAN (WHETHER IN WHOLE OR IN PART) WITHOUT THE PRIOR WRITTEN CONSENT OF MCDONALD JONES HOMES PTY LTD.



mcdonald jones
FIND YOURSELF AT HOME

SPECIFICATION:		REVISION	DRAWN	CLIENT:	HOUSE DESIGN:	HOUSE CODE:	DO NOT SCALE DRAWINGS, USE FIGURED DIMENSIONS ONLY. CHECK AND VERIFY DIMENSIONS AND LEVELS PRIOR TO THE COMMENCEMENT OF ANY WORK. ALL DISCREPANCIES TO BE REPORTED TO THE DRAFTING OFFICE.
NOW	2	APPOINTMENT AMEDEMMENTS	LIR 01/02/2024	LINH THANH THAO LE & HUU PHU LE	SERRANO TWO	H-SRNCCLAS21420	
COPYRIGHT:	3	WORKING DRAWINGS	TNT 07/02/2024	ADDRESS:	FACADE DESIGN:	FACADE CODE:	
© 2024	4	WD CHECK	ALW 13/02/2024	40 WEEMALA ROAD, CHESTER HILL NSW 2162	CLASSIC	F-SRNCCLAS01	
	5	AMENDED AS PER PCV003	ALW 01/03/2024	LOT / SECTION / DP:	SHEET TITLE:	SCALES:	
	6	AMENDED AS PER PCV004	ALW 07/03/2024	42 / - / 15807	COUNCIL: CANTERBURY BANKSTOWN COUNCIL	SHEET No.: 20 / 20	607126

File Location: G:\Sydney\Drafting\Job Files 607001 - 60720\607126 - Le\Plan Model\607126 Le - AC24.pln

Template Version: 24.033