

Table of Contents	
Sheet Number	Sheet Name

DD-1451-1	Cover Sheet
DD-1451-2	NCC & AS Compliance
DD-1451-3	BASIX Commitments
DD-1451-4	Site Plan
DD-1451-5	Site Analysis Plan
DD-1451-6	Erosion & Sediment Control Plan
DD-1451-7	Concrete Plan
DD-1451-8	Ground Floor Plan
DD-1451-9	First Floor Plan
DD-1451-10	Elevations
DD-1451-11	Elevations
DD-1451-12	Cabana Plans
DD-1451-13	Schedules
DD-1451-14	Sections
DD-1451-15	GF Wet Area Details
DD-1451-16	FF Wet Area Details
DD-1451-17	Landscape Plan
DD-1451-18	GF Area Calculation Plan
DD-1451-19	FF Area Calculation Plan
DD-1451-20	GF Electrical Plan
DD-1451-21	FF Electrical Plan
DD-1451-22	Shadow Diagram - June 21 8am
DD-1451-23	Shadow Diagram - June 21 12pm
DD-1451-24	Shadow Diagram - June 21 4pm
DD-1451-25	Pool Site Plan
DD-1451-26	Revision Schedule
DD-1451-27	Facade Image

Development Application
Proposed Two-Storey Dwelling, Tree Removal, Retaining Walls,
Detached Cabana Outbuilding & Swimming Pool

General Notes:

- > All work & materials to comply with the National Construction Code (NCC) & relevant Standards Australia Codes
- > Stormwater drainage as per stormwater plan & the BASIX certificate
- > Sewer drainage & waste water to Sydney Water sewer main, where available
- > Sediment control barrier to Council specification during construction
- > An all weather access crossing of recycled concrete will be provided during construction
- > Survey levels & contours to Australian Height Datum (AHD) or as indicated on survey plan +/-100mm
- > Termite control chemical or physical barrier to be installed in accordance with AS3660
- > Verify all dimensions, levels & existing conditions on site prior to commencement of work
- > Figured dimensions take preference to scale - do not scale, ASK
- > All dimensions in millimetres (mm) unless noted otherwise
- > Driveway gradient to comply with Council regulations
- > Drop edge beams to be constructed to engineers details if required
- > All structural beam sizes, connections & details to engineers specification & details
- > Any retaining wall required will be constructed from treated pine sleepers, masonry or stone not exceeding 600mm high unless noted otherwise
- > Permanent driveway will be reinforced concrete or similarly approved hardstand surface
- > Any concrete paths to be reinforced concrete
- > Surface drains will be included in the landscaping to remove surface water from grassed & hardstand areas
- > Agricultural drains will be installed behind all retaining walls & connected into the stormwater drainage system
- > Survey drawing & information obtained from Sydney Registered Surveyors - plan reference 6647



Climate Zone: 5

Disclaimer: Some items displayed or noted on these plans may be for indicative nominal placement or certification purposes only. The written words in any accompanying building tender will on all occasions take precedence to the plan. All internal room dimensions shown on any floor plan are to timber frame for construction purpose.									
	ABN 67 250 466 867 Suite 7, Shop 11, 38 Exchange Parade Narellan NSW 2567 P: 0421 993 467 E: info@definitivedrafting.com.au W: www.definitivedrafting.com.au	This drawing and information thereon is the property of Vogue Homes and must not be loaned, partly copied, fully copied or used without the expressed permission in license or writing		License No. 115618C Unit 2/16 Weld Street Prestons NSW 2170 P: (02) 96079554 E: admin@vogue-homes.com.au W: www.vogue-homes.com.au	Hau Thi Bui & Toan Hoang Pham Lot 5 DP 959294 118 William St Condell Park 2200	Design Custom	Vogue Job No. 9013-22	Project Number DD-1451	DD-1451-1
						Facade Custom	LGA Canterbury Bankstown	Current Revision 3 26/09/23	Cover Sheet
						Inclusions Vogue	Approval Path DA	Date 18/03/22	Scale @ A3

NCC 2022 Compliance Notes <u>Section A Governing Requirements</u>		
Part A6 Building Classification A6G2 class 1 buildings: One or more buildings which in association constitute-- (1) class 1a is one or more buildings, which together form a single dwelling including the following: (a) a detached house (b) one of a group of two or more attached dwellings, each being a building, separated by a fire-resisting wall, including a row house, terrace house, town house or villa unit.		
Section H Class 1 and 10 Buildings Part H1 Structure See engineering plans		
Part H2 Damp and Weatherproofing - Part H2D8 External Waterproofing (1) performance requirement H2P2 is satisfied for the design and construction of external waterproofing for roofing systems on flat roofs, roof terraces, balconies and terraces and other similar horizontal surfaces located above internal spaces of a building provided- (a) membranes used in the external waterproofing system comply with AS 4654.1; and (b) the design and installation of the external waterproofing system is in accordance with AS 4654.2. (2) the requirements of (1) apply to- (a) roofing systems other than those complying with H1D7(2) and (3); and (b) terraces, balconies and the like other than- (i) a concrete slab that has a minimum step-down of 50 mm below the internal floor level; or (ii) a suspended concrete slab- (a) where the subfloor space is not used for habitable or non-habitable purposes; and (b) that has a minimum step-down of 50 mm below the internal floor level; or (iii) spaced decking in conjunction with framing members that are suitable for external use.		
Part H3 Fire Safety - Part H3D2.1 Fire Hazard Properties and Non-Combustible Building Elements the following materials, though combustible or containing combustible fibres, may be used wherever a non-combustible material is required: (a) plasterboard (b) perforated gypsum lath with a normal paper finish (c) fibrous-plaster sheet (d) fibre-reinforced cement sheeting (e) pre-finished metal sheeting having a combustible surface finish not exceeding 1mm thickness and where the spread-of-flame index of the product is not greater than 0 (f) sarking-type materials that do not exceed 1 mm in thickness and have a flammability index not greater than 5 (g) bonded laminated materials where- (i) each lamina, including any core, is non-combustible; and (ii) each adhesive layer does not exceed 1mm in thickness and the total thickness of the adhesive layers does not exceed 2mm; and (iii) the spread-of-flame index and the smoke-developed index of the bonded laminated material as a whole do not exceed 0 and 3 respectively.		
- Part H3D2.2 Fire Hazard Properties The fire hazard properties of materials used in a class 1 building must comply with the following: (a) sarking-type materials used in the roof must have a flammability index not greater than 5 (b) flexible ductwork used for the transfer of products initiating from a heat source that contains a flame must comply with the fire hazard properties set out in AS 4254.1.		
- Part H3D3 Fire Separation of External Walls Compliance with Part 9.2 of the ABCB Housing Provisions satisfies performance requirement H3P1 for fire separation of external walls.		
- Part H3D4 Fire Protection of Separating Walls and Floors Compliance with part 9.3 of the ABCB Housing Provisions satisfies performance requirement H3P1 for fire protection of separating walls and floors.		
- Part NSW H3D4 Fire Separation of Garage Top Dwellings Compliance with NSW Part 9.4 of the ABCB Housing Provisions satisfies performance requirement H3P1 for fire separation of garage top dwellings.		
- Part H3D6 Smoke Alarms and Evacuation Lighting (1) compliance with part 9.5 of the ABCB Housing Provisions satisfies performance requirement H3P2 for smoke alarms and evacuation lighting. (2) for the purposes of (1), a class 1 building includes a class 10a private garage located above or below the class 1 building.		

- Part H3V2 Avoidance of Spread of Fire from Allotment Boundary Compliance with H3P1(1)(b) to avoid the spread of fire from an allotment boundary is verified when- (a) the external walls and any openings in the external walls of a building, less than 0.9 m from an allotment boundary, are capable of withstanding 92.6 kw/m² of heat flux for 60 minutes; and (b) the external walls extend to the underside of a non-combustible roof covering or non-combustible eaves lining in accordance with clause 9.2.3 of the ABCB Housing Provisions.
Part H4 Health and Amenity - Part H4D2 Wet Areas Compliance with AS 3740 or part 10.2 of the ABCB Housing Provisions satisfies performance requirement H4P1 for wet areas provided the wet areas are protected in accordance with the appropriate requirements of 10.2.1 to 10.2.6 and 10.2.12 of the ABCB Housing Provisions. - Part H4D3 Materials and Installation of Wet Area Components and Systems Performance requirement H4P1 is satisfied for materials and the installation of wet area components and systems if- (a) building elements in wet areas are water resistant or waterproof in accordance with clauses 10.2.1 to 10.2.6 of the ABCB Housing provisions; and (b) they comply with either- (i) AS 3740 and clause 10.2.12 of the abcb housing provisions; or (ii) 10.2.7 to 10.2.32 of the ABCB Housing Provisions - Part H4D7 Ventilation (1) except for an exhaust fan from a sanitary compartment, laundry, kitchen or bathroom, performance requirement H4P5 is satisfied for a mechanical ventilation system if it is installed in accordance with AS 1668.2. (2) compliance with part 10.6 of the ABCB Housing provisions satisfies performance requirement H4P5 for ventilation. - Part H4D8 Sound Insulation Compliance with part 10.7 of the ABCB Housing Provisions satisfies performance requirement H4P6 for sound insulation. - Part H4D9 Condensation Management Compliance with part 10.8 of the ABCB Housing Provisions satisfies performance requirement H4P7 for condensation management.
Part H5 Safe Movement and Access - Part H5D2 Stairway and Ramp Construction Compliance with part 11.2 of the ABCB Housing Provisions satisfies performance requirement H5P1 for stairway and ramp construction.

Standards Australia Compliance The development shall be in accordance with but not limited to the following Standards	
AS 3700:2018 AS 1670.1:2018	Masonry Structures Fire Detection, Warning, Control & Intercom Systems - System Design
AS/NZS 1668:2016 AS 1428:2021 AS 2293.1:2018 AS 3500.3:2021 AS/NZS 1664.1:1997 AS/NZS 1905.1:2015 & AS/NZS 1905.2:2005 AS 2050:2018 AS 2047:2014 AS/NZS 2327:2017 AS 2870:2011 AS 1684.2:2021 AS/NZS 3013:2005 AS 1668.1:2015 & AS 1668.4:2012 AS 2444:2001 AS 3786:2014 AS 1288:2021 AS 2107:2016	The Use of Ventilation & Air Conditioning in Buildings Set General Requirements for Access - New Building Work Emergency Escape Lighting & Exit Signs for Buildings Plumbing & Drainage - Stormwater Aluminium Structures
AS 3660.3:2014 AS 3740:2021 AS 1926.1:2012 & AS 1926.2:2007	Components for the Protection of Openings in Fire Resistant Walls Installation of Roof Tiles Windows - Selection & Installation Composite Structures Residential Slabs & Footings Residential Timber Framed Construction Electrical Installations
	The Use of Mechanical Ventilation & Air Conditioning in Buildings Portable Fire Extinguishers & Fire Blankets - Selection & Location Smoke Alarms Glass - Selection & Installation Acoustics - Recommended Design Sound Levels & Reverberation Times for Building Interiors Termite Management - New Building Work Waterproofing of Domestic Wet Areas
	Safety Barriers for Swimming Pools

CONSTRUCTION NOTES			
NCC 2022 Typical Construction Notes ABCB Housing Provisions Standards clauses & Standards Australia codes referenced > Smoke alarms to be installed in accordance with clauses 9.5.1, 9.5.2 & 9.5.4 > Wet areas to be constructed in accordance with clauses 10.2.1 to 10.2.32 > Wet areas with non-compliant natural ventilation must include additional ventilation of 14,000mm² to an adjacent room in accordance with clause 10.8.2(5)(a) - to be achieved by a fixed distance between the bottom of the door and finished floor, or by a compliant door grill. Refer to specific floor plan notes where required > Where a floor waste is installed to a wet area, the minimum continuous fall of a floor plane to the waste must be 1:80 and the maximum must be 1:50, in accordance with clause 10.2.12 > Baths must discharge untrapped to a floor waste gully where a trap is not accessible, such as a bath on ground floor slab construction, in accordance with AS/NZS 3500.2 and Volume 3 of the NCC. Minimum falls to the floor waste gully must be achieved in accordance with clause 10.2.12 and noted above > Bathroom doors which are within 1.2m of the closet plan to be provided with lift-off hinges or open outwards, or slide, in accordance with clause 10.4.2 > Exhaust fans to a kitchen or wet area rooms without natural ventilation must meet the flow rates detailed in clause 10.8.2(1) and ducting to outdoor air in accordance with clause 10.8.2(2) > Wet areas without natural ventilation, must include a run-on timer on the exhaust fan. The fan must be interlocked to the light switch and run-on for 10 minutes after the light is turned off, in accordance with clause 10.8.2(4) > All stairs, landings, stair finishes and ramps are to be constructed in accordance with part 11.2 , including tread & riser dimensions as below. - tread depth = 240mm minimum & 355mm maximum - riser height = 115mm minimum & 190mm maximum > Internal staircases shall achieve a minimum P3 slip resistance rating > Balustrades to be a minimum of 1000mm high from associated floor, stair or landing level in accordance with clause 11.3.3 & 11.3.4 > Child proof screens must be fitted to ground floor bedroom windows where the ground is 2m or more below the window sill, or window openings to be restricted to 125mm, in accordance with clause 11.3.7.1 > Child proof screens must be fitted to first floor bedroom windows where the sill is less than 1.7m above floor level, or window openings to be restricted to 125mm, in accordance with clause 11.3.7.2 > Climate Zone 6 requires dwellings to include mandatory roof and eave ventilation in accordance with clause 10.8.3 > Where roofs have pitches <12.5°, valley gutters must be designed as box gutters in accordance with AS 3500.3 or as a performance solution by a professional engineer, in accordance with clause 7.4.4(4) > Vertical articulation joints in brickwork are to be installed in accordance with AS 3700 and AS 4773			
Design Custom	Vogue Job No. 9013-22	Project Number DD-1451	DD-1451-2
Facade Custom	LGA Canterbury Bankstown	Current Revision 3 26/09/23	NCC & AS Compliance
Inclusions Vogue	Approval Path DA	Date 18/03/22	Scale @ A3

Disclaimer: Some items displayed or noted on these plans may be for indicative nominal placement or certification purposes only. The written words in any accompanying building tender will on all occasions take precedence to the plan. All internal room dimensions shown on any floor plan are to timber frame for construction purpose.									
	ABN 67 250 466 867 Suite 7, Shop 11, 38 Exchange Parade Narellan NSW 2567 P: 0421 993 467 E: info@definitivedrafting.com.au W: www.definitivedrafting.com.au	This drawing and information theron is the property of Vogue Homes and must not be loaned, partly copied, fully copied or used without the expressed permission in license or writing		License No. 115618C Unit 2/16 Weld Street Prestons NSW 2170 P: (02) 96079554 E: admin@vogue-homes.com.au W: www.vogue-homes.com.au	Hau Thi Bui & Toan Hoang Pham Lot 5 DP 959294 118 William St Condell Park 2200	Design Custom	Vogue Job No. 9013-22	Project Number DD-1451	DD-1451-2
						Facade Custom	LGA Canterbury Bankstown	Current Revision 3 26/09/23	NCC & AS Compliance
						Inclusions Vogue	Approval Path DA	Date 18/03/22	Scale @ A3

BANKSTOWN COUNCIL DCP 2015 COMPLIANCE TABLE

CRITERIA	ALLOWABLE	ACHIEVED
GF FRONT SETBACK	5.5m MINIMUM	5.83m
FF FRONT SETBACK	6.5m MINIMUM	6.5m
SIDE SETBACK	0.9m MINIMUM (WALL <7m HIGH)	1.5m
SIDE SETBACK	1.5m MINIMUM (WALL >7m HIGH)	N/A
FLOOR SPACE RATIO	0.50:1 MAXIMUM	0.499:1
BUILDING HEIGHT	9.0m MAXIMUM	8.555m
WALL HEIGHT (LEP)	7.0m MAXIMUM	6.999m
FRONT LANDSCAPE AREA	(SITE AREA x 45%) MIN.	55.63%
PRIVATE OPEN SPACE	80m² MINIMUM (5m MIN.)	92.26m²
PARKING SPACES	2 SPACES MINIMUM	2 SPACES
PARKING BAY DIMENSIONS	(5.5m L x 5.4m W) MIN.	6.5m L x 6.03m W
ROOF PITCH	35° MAXIMUM	18° PITCH

NOTE: EXISTING OVERHEAD POWER FEED TO BE RELOCATED TO AN UNDERGROUND (UGOH) CONNECTION, SUPPLIED BY PRIVATE POLE TO DWELLING


SITE AREA CALCULATION

SITE AREA	1005.30m²
SITE COVERAGE	31.28% (314.45m²)
FLOOR SPACE RATIO	0.499:1 (502.64m²)
DWELLING ROOF AREA	363.04m²
CABANA ROOF AREA	39.50m²

Area Schedule		
Number	Name	Area
1	Garage	43.49 m²
2	Ground Floor	242.44 m²
3	First Floor	283.31 m²
4	Porch	8.33 m²
5	Alfresco	34.58 m²
6	Balcony	6.09 m²
7	Cabana	28.52 m²
Total Floor Area		646.75 m²




Disclaimer: Some items displayed or noted on these plans may be for indicative nominal placement or certification purposes only. The written words in any accompanying building tender will on all occasions take precedence to the plan. All internal room dimensions shown on any floor plan are to timber frame for construction purpose.

	ABN 67 250 466 867 Suite 7, Shop 11, 38 Exchange Parade Narellan NSW 2567 P: 0421 993 467 E: info@definitivedrafting.com.au W: www.definitivedrafting.com.au	This drawing and information thereon is the property of Vogue Homes and must not be loaned, partly copied, fully copied or used without the expressed permission in license or writing		License No. 115618C Unit 2/16 Weld Street Prestons NSW 2170 P: (02) 96079554 E: admin@vogue-homes.com.au W: www.vogue-homes.com.au	Hau Thi Bui & Toan Hoang Pham Lot 5 DP 959294 118 William St Condell Park 2200	Design Custom	Vogue Job No. 9013-22	Project Number DD-1451	DD-1451-4
						Facade Custom	LGA Canterbury Bankstown	Current Revision 3 26/09/23	Site Plan
						Inclusions Vogue	Approval Path DA	Date 18/03/22	Scale 1 : 200 @ A3

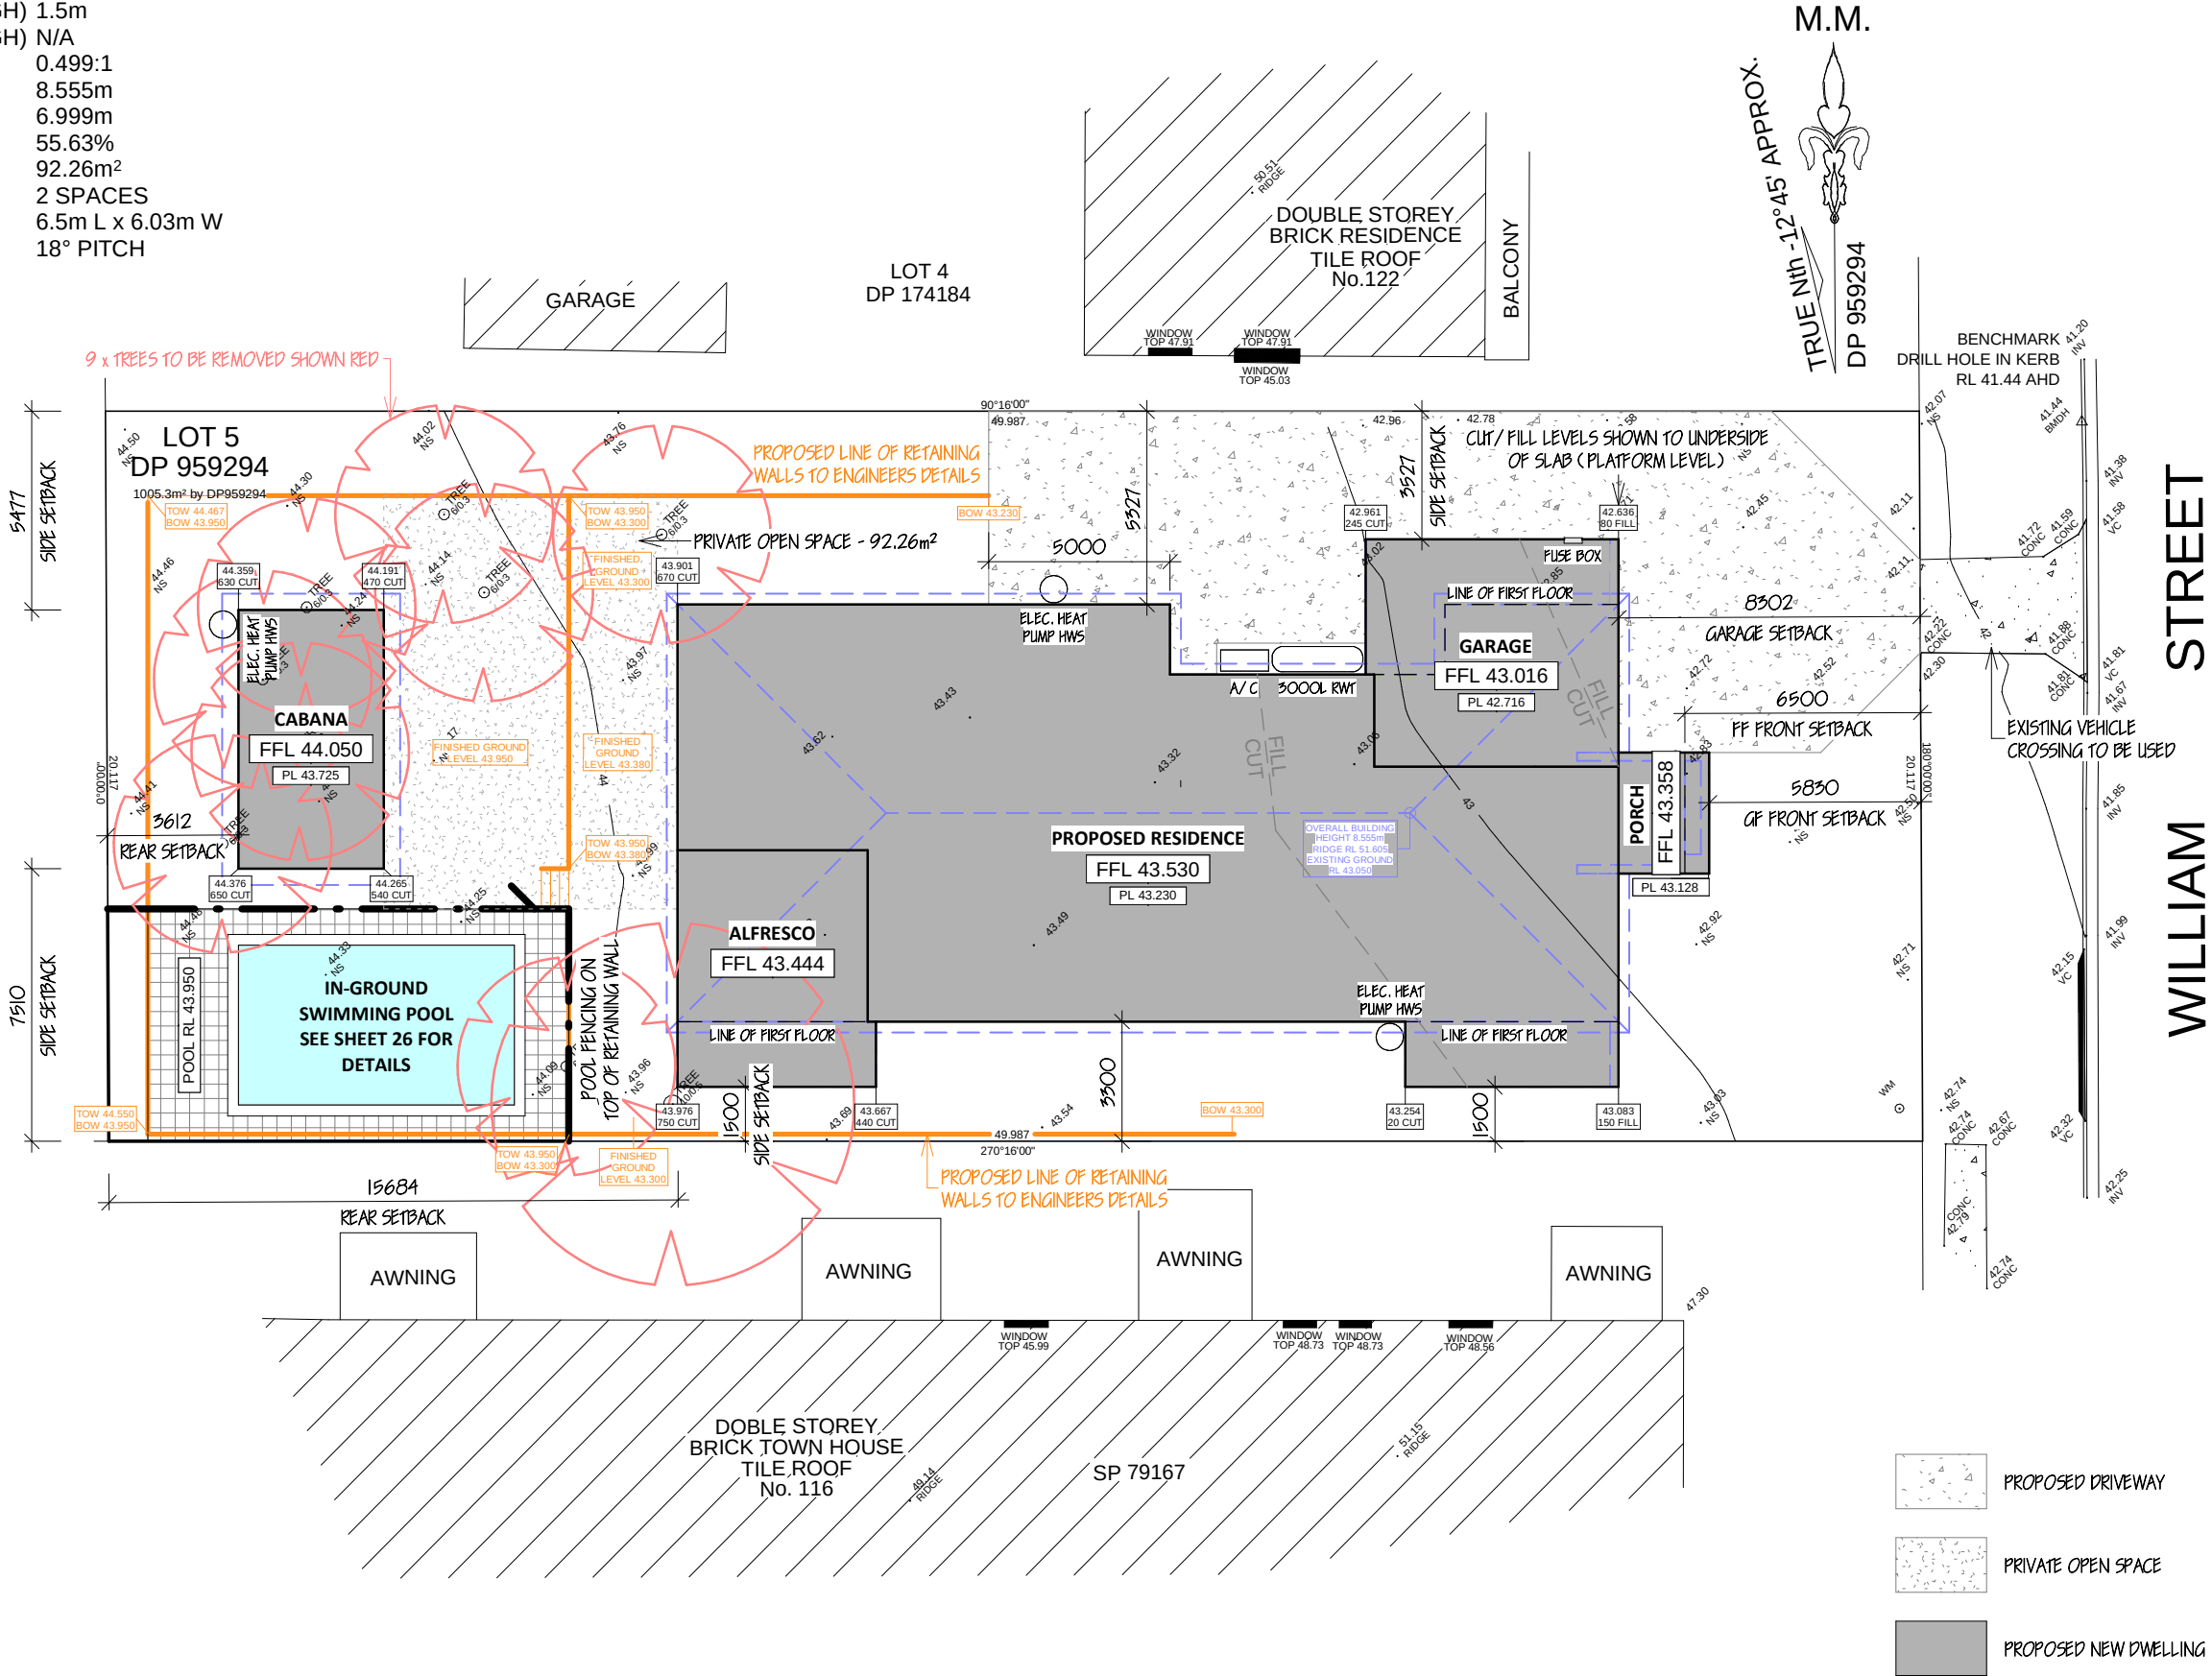




1. ALL EROSION & SEDIMENT CONTROL MEASURES, INCLUDING REVEGETATION & STORAGE OF SOIL & TOPSOIL, SHALL BE IMPLEMENTED TO THE STANDARDS OF THE SOIL CONSERVATION OF NSW.
2. ALL DRAINAGE WORKS SHALL BE CONSTRUCTED & STABILIZED AS EARLY AS POSSIBLE DURING DEVELOPMENT.
3. SEDIMENT TRAPS SHALL BE CONSTRUCTED AROUND ALL INLET PITS, CONSISTING OF 300mm WIDE x 300mm DEEP TRENCH.
4. ALL SEDIMENT BASINS & TRAPS SHALL BE CLEANED WHEN THE STRUCTURES ARE A MAXIMUM OF 60% FULL OF SOIL MATERIALS, INCLUDING THE MAINTENANCE PERIOD.
5. ALL DISTURBED AREAS SHALL BE REVEGETATED AS SOON AS THE RELEVANT WORKS ARE COMPLETED.
6. SOIL & TOPSOIL STOCKPILES SHALL BE LOCATED AWAY FROM DRAINAGE LINES & AREA WHERE WATER MAY CONCENTRATE.
7. FILTER SHALL BE CONSTRUCTED BY STRETCHING A FILTER FABRIC (PROPEX OR APPROVED EQUIVALENT) BETWEEN POSTS AT 2.0M CENTRES. FABRIC SHALL BE BURIED 150mm ALONG ITS LOWER EDGE.
8. REFER TO PROPOSED SEDIMENT FENCE DETAIL.

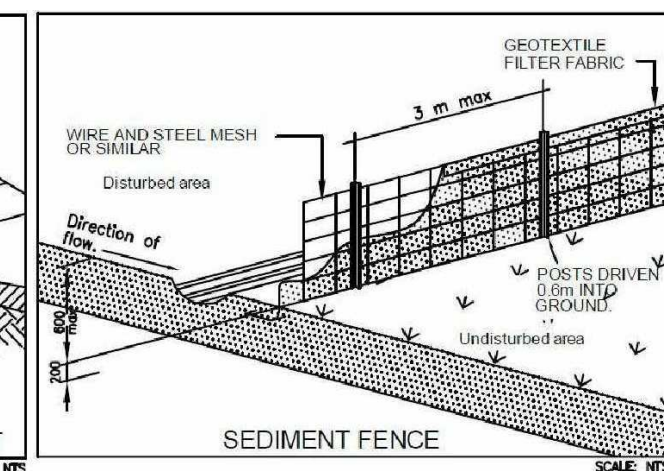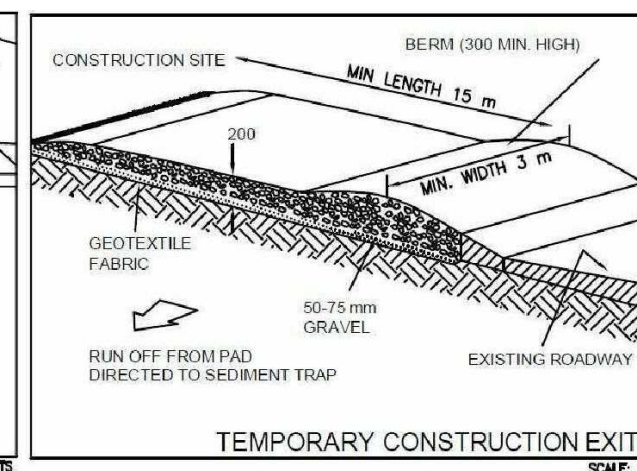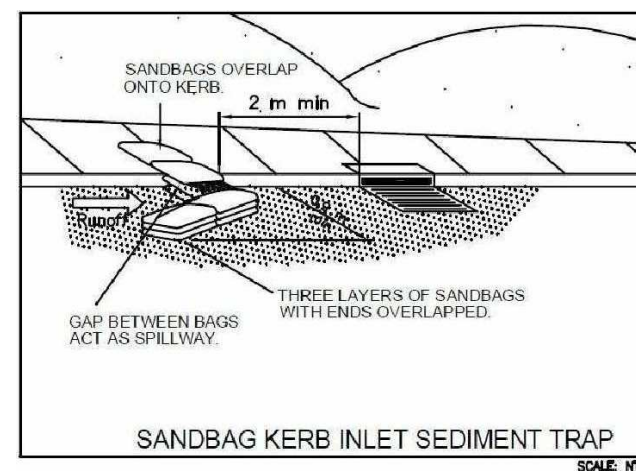

Disclaimer: Some items displayed or noted on these plans may be for indicative nominal placement or certification purposes only. The written words in any accompanying building tender will on all occasions take precedence to the plan. All internal room dimensions shown on any floor plan are to timber frame for construction purpose.



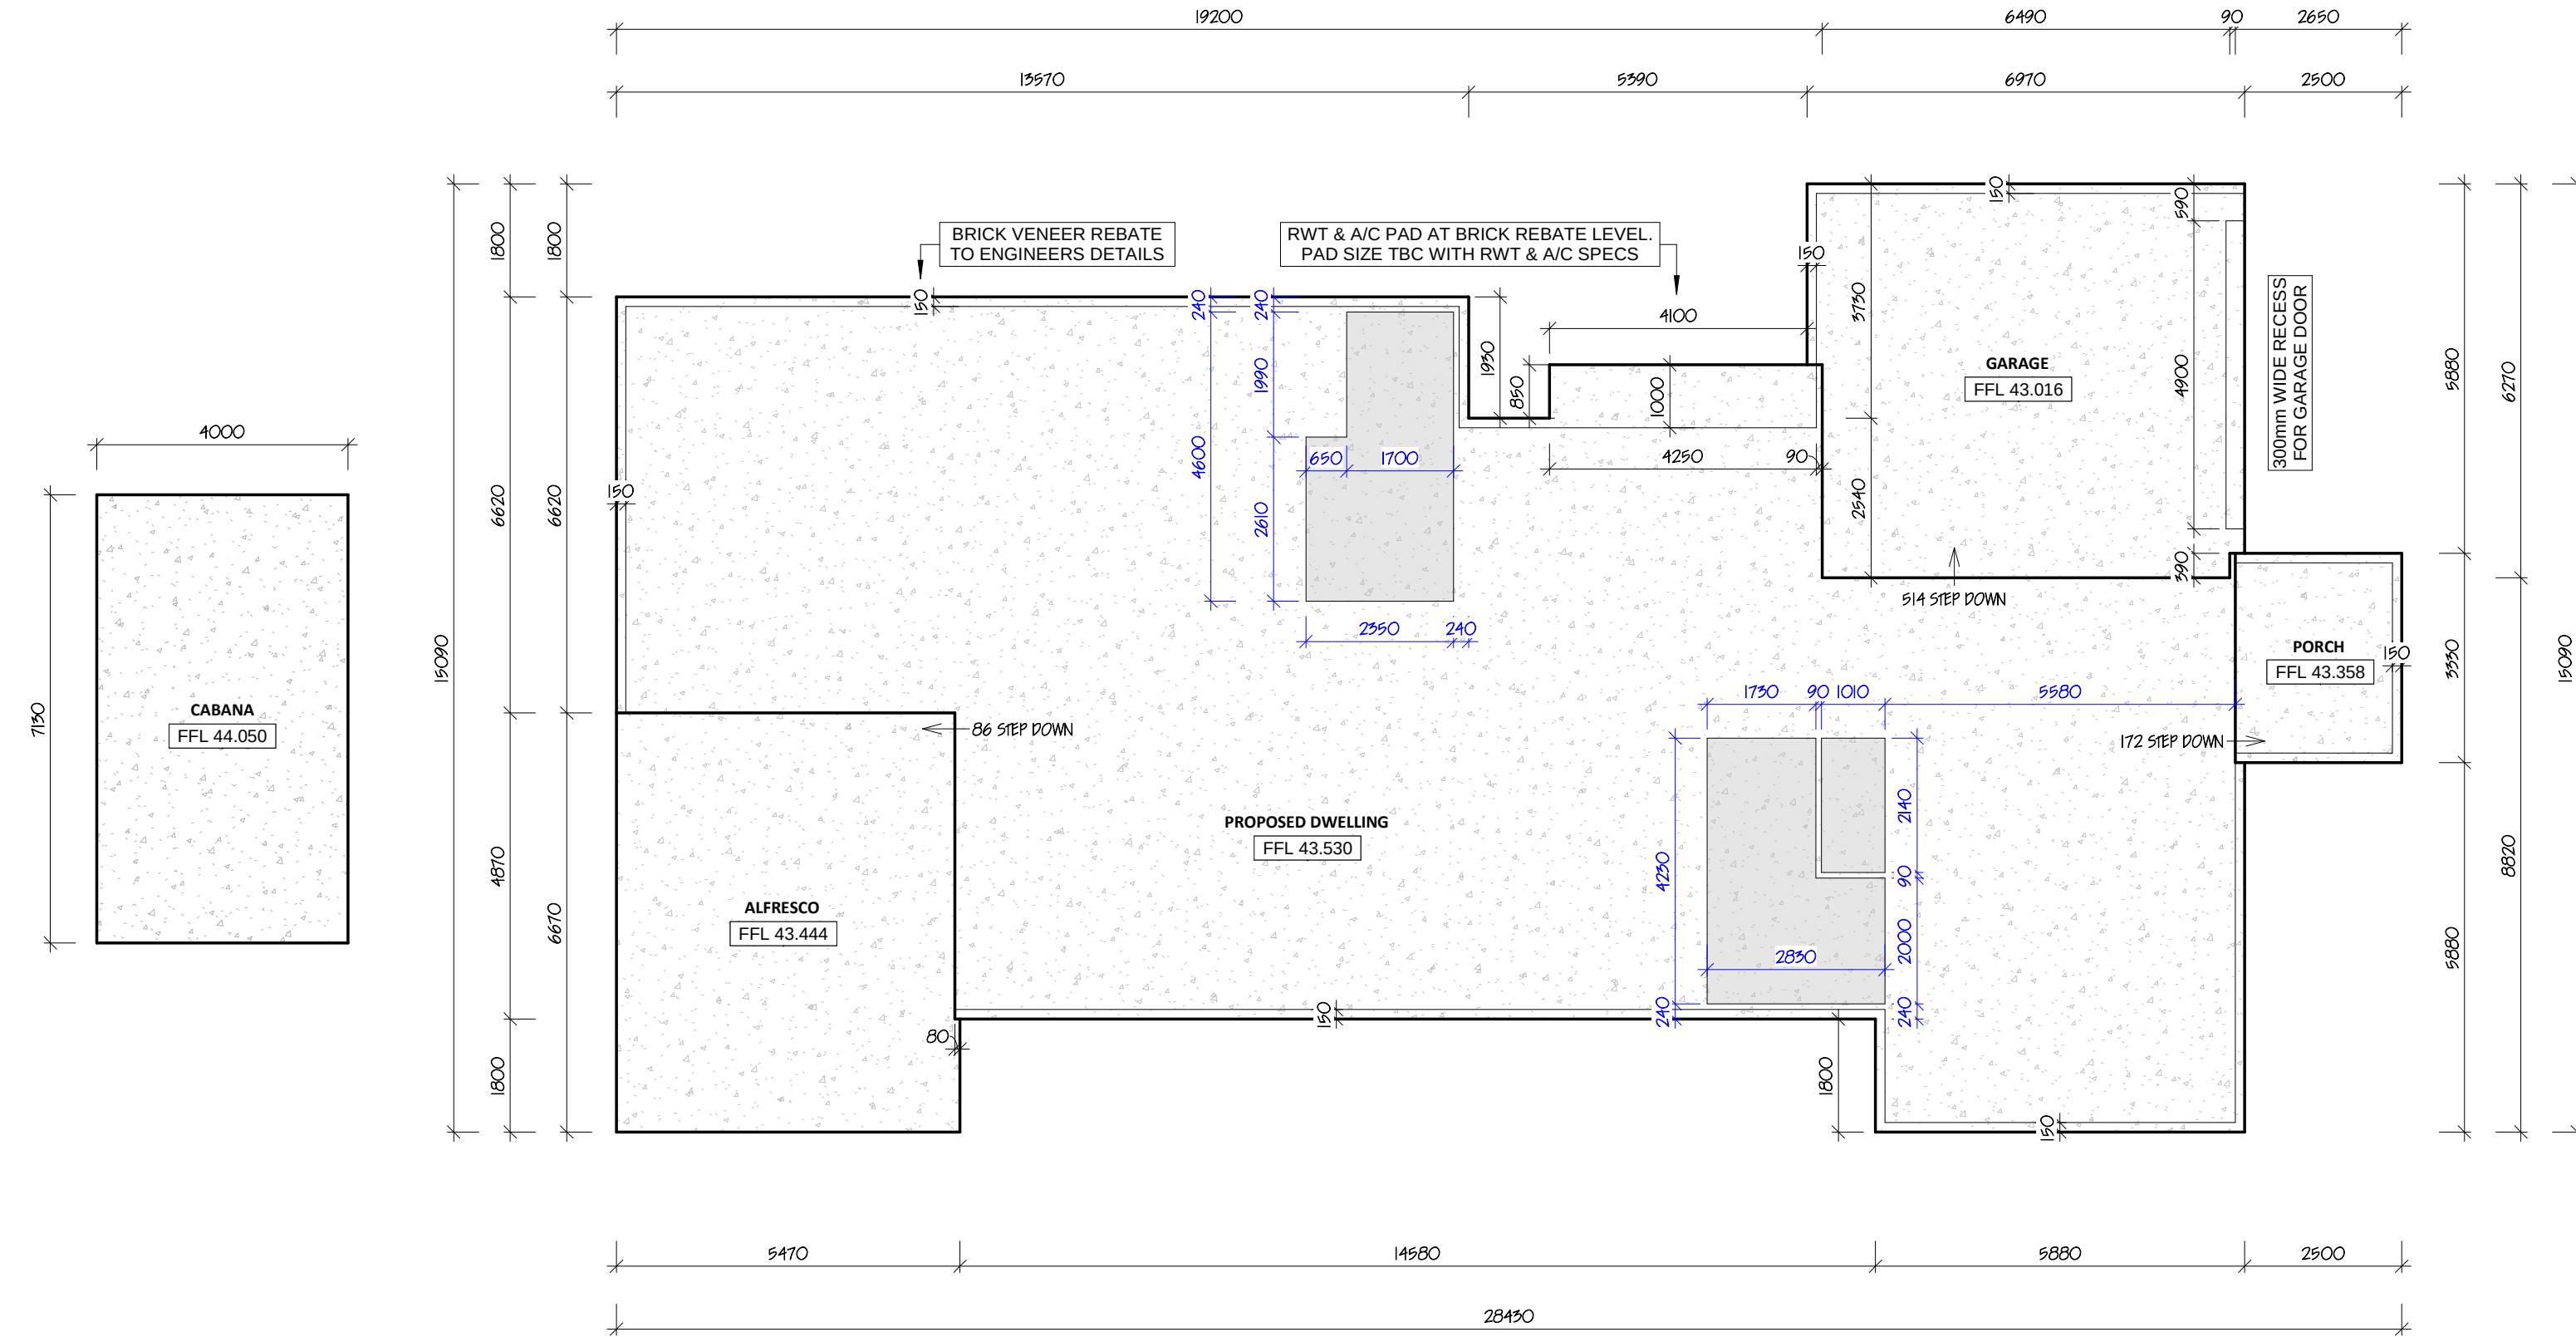

REFER TO ARCHITECTURAL PLANS FOR CROSS REFERENCING - ARCHITECTURAL PLANS TAKE PRECEDENCE OVER CONCRETE PLAN

WET AREAS SET DOWN 40mm - SHADED GREY

Disclaimer: Some items displayed or noted on these plans may be for indicative nominal placement or certification purposes only. The written words in any accompanying building tender will on all occasions take precedence to the plan. All internal room dimensions shown on any floor plan are to timber frame for construction purpose.									
	ABN 67 250 466 867 Suite 7, Shop 11, 38 Exchange Parade Narellan NSW 2567 P: 0421 993 467 E: info@definitivedrafting.com.au W: www.definitivedrafting.com.au	This drawing and information thereon is the property of Vogue Homes and must not be loaned, partly copied, fully copied or used without the expressed permission in license or writing		License No. 115618C Unit 2/16 Weld Street Prestons NSW 2170 P: (02) 96079554 E: admin@vogue-homes.com.au W: www.vogue-homes.com.au	Hau Thi Bui & Toan Hoang Pham Lot 5 DP 959294 118 William St Condell Park 2200	Design Custom	Vogue Job No. 9013-22	Project Number DD-1451	DD-1451-7
						Facade Custom	LGA Canterbury Bankstown	Current Revision 3 26/09/23	Concrete Plan
						Inclusions Vogue	Approval Path DA	Date 18/03/22	Scale 1 : 100 @ A3

D10 TO BE INSTALLED WITH
MINIMUM 17mm CLEARANCE TO FFL


NOTE: WET AREAS SET DOWN 40mm
IN SLAB FOR LEVEL ENTRY FINISH

NOTE: ALL INTERNAL/EXTERNAL
DOORS ON GROUND FLOOR TO BE
2340/2400 HIGH U.N.O.





GROUND FLOOR SQUARE SETS @
2700H U.N.O

MV MECHANICAL VENTILATION

Ⓢ APPROX. LOCATION OF SMOKE ALARMS

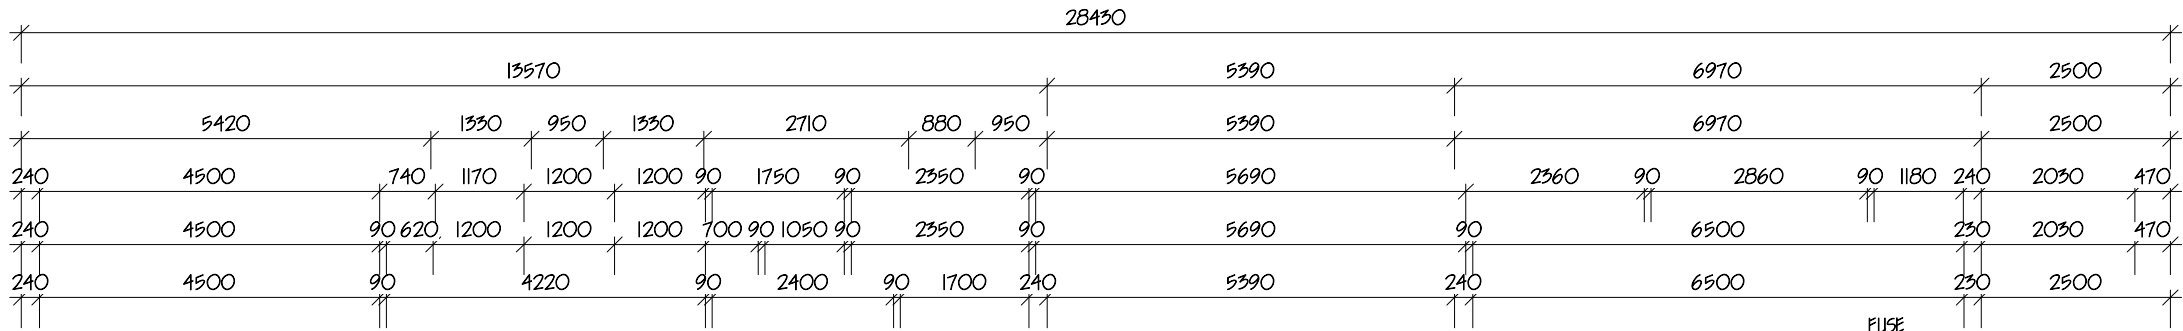

Spacing of Articulation Joints - Unreinforced Masonry Walls				
Site class	Wall construction & surface finish	Joint Spacing (m)		
		Up to 4m high for 10mm joints	4m-8.5m high for 10mm joints	4m-8.5m high for 15mm joints
AS2870	External face finish masonry	6.0	4.2	6.0
	External rendered and/or painted masonry	5.5	3.9	5.5
	Internal face finish or sheeted masonry	6.0	4.2	6.0
	Internal rendered and/or painted masonry	5.5	3.9	5.5
H, H1-D	External face finish masonry	5.5	3.9	5.5
	External rendered and/or painted masonry	5.0	3.5	5.0
	Internal face finish or sheeted masonry	5.5	3.9	5.5
	Internal rendered and/or painted masonry	5.0	3.5	5.0
H2, H2-D	External face finish masonry	5.0	3.5	5.0
	External rendered and/or painted masonry	4.5	3.2	4.5
	Internal face finish or sheeted masonry	5.0	3.5	5.0
	Internal rendered and/or painted masonry	4.5	3.2	4.5

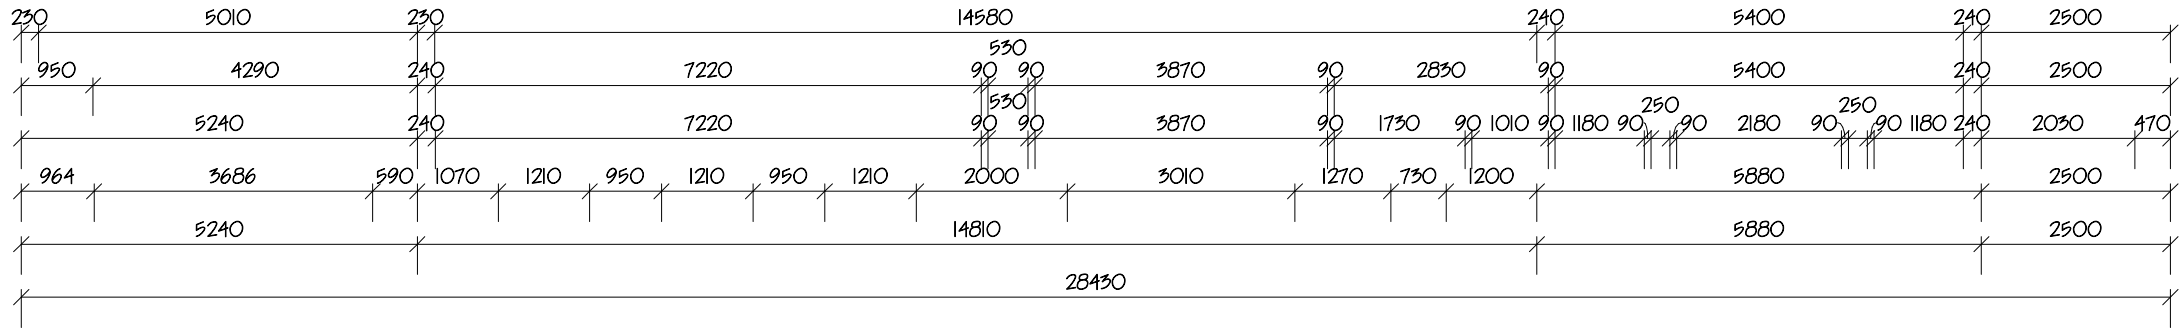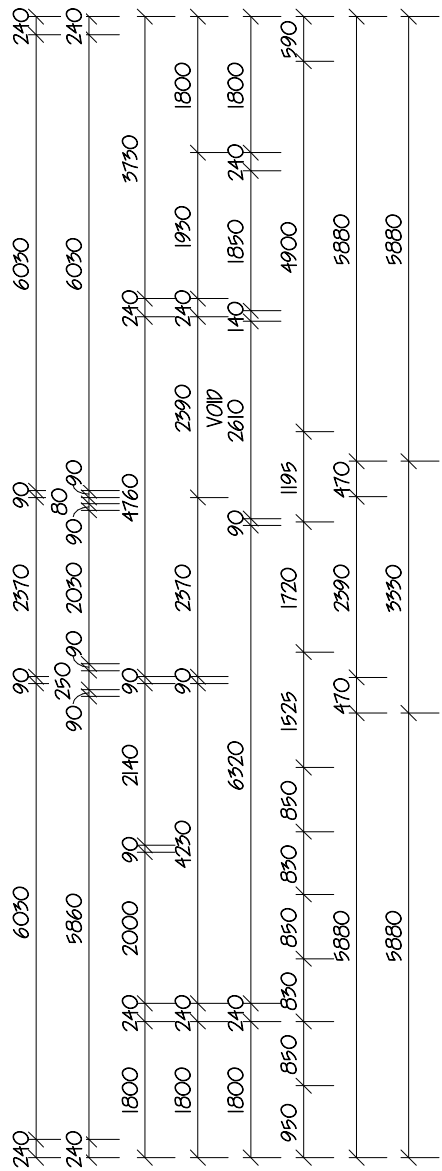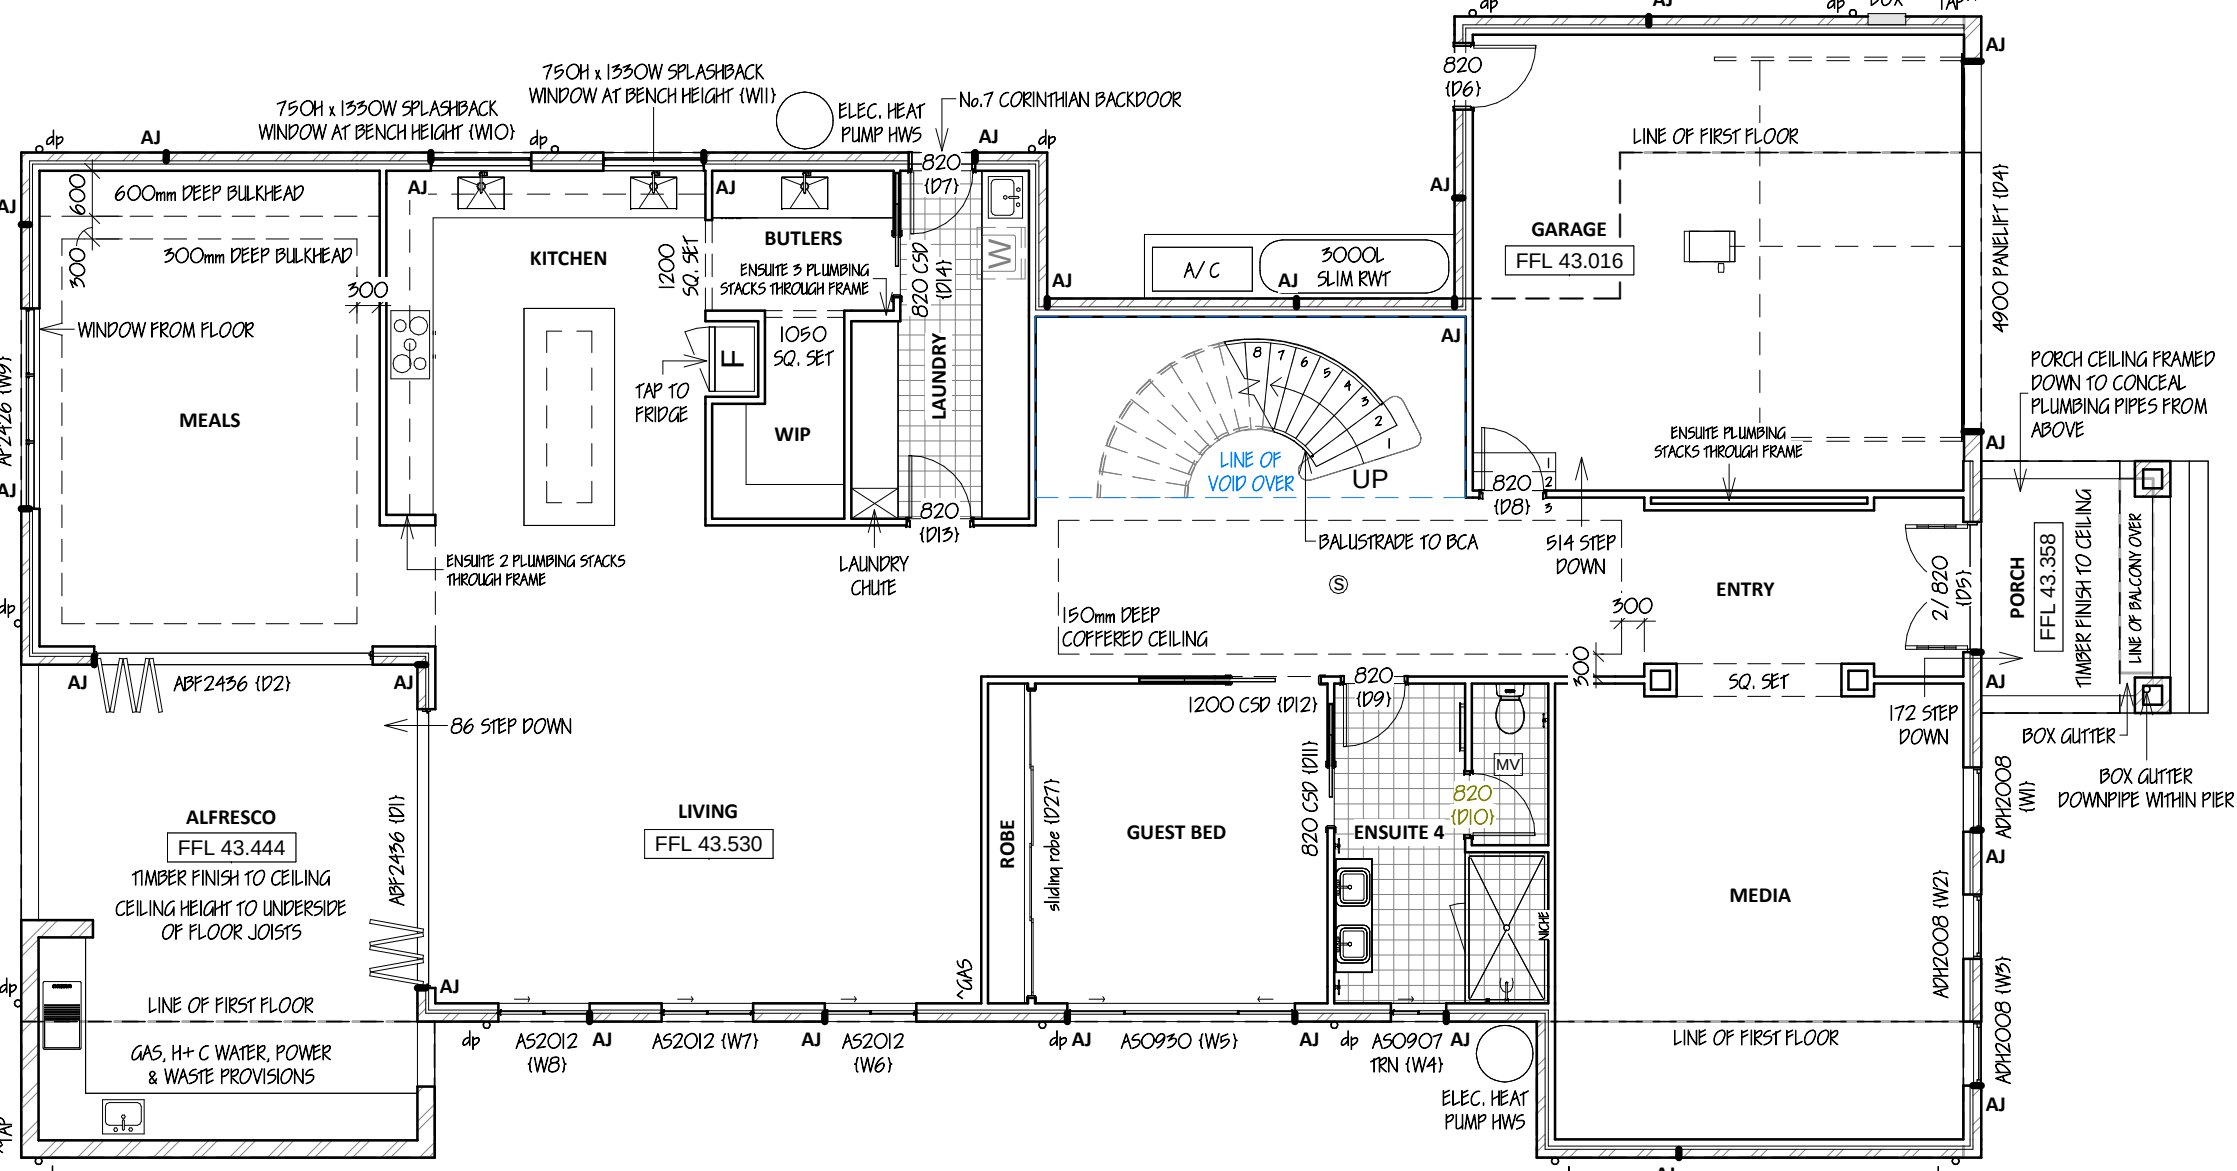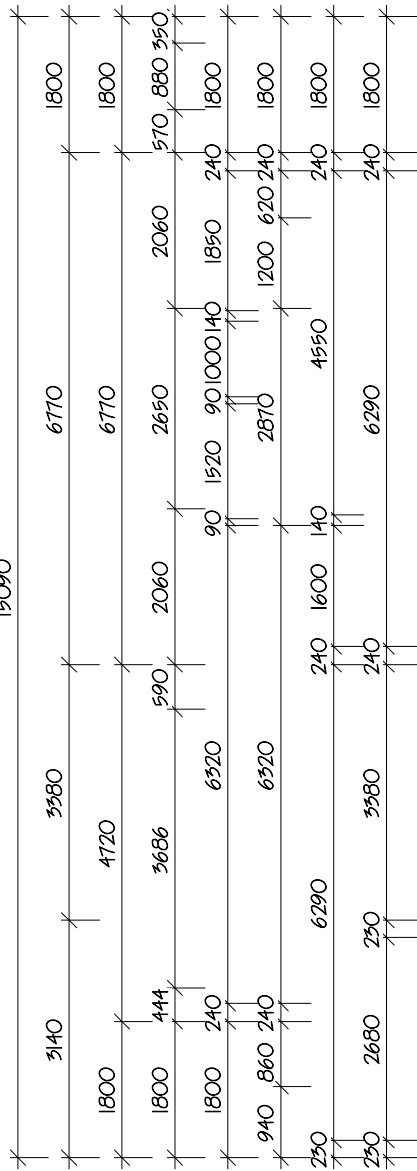

Disclaimer: Some items displayed or noted on these plans may be for indicative nominal placement or certification purposes only. The written words in any accompanying building tender will on all occasions take precedence to the plan. All internal room dimensions shown on any floor plan are to timber frame for construction purpose.



ABN 67 250 466 867
Suite 7, Shop 11, 38 Exchange Parade Narellan NSW 2567
P: 0421 993 467
E: info@definitivedrafting.com.au
W: www.definitivedrafting.com.au

This drawing and information theron is the property of Vogue Homes and must not be loaned, partly copied, fully copied or used without the expressed permission in license or writing



License No. 115618C
Unit 2/16 Weld Street
Prestons NSW 2170
P: (02) 96079554
E: admin@vogue-homes.com.au
W: www.vogue-homes.com.au






Hau Thi Bui & Toan Hoang Pham

Lot 5 DP 959294
118 William St Condell Park 2200

Design Custom	Vogue Job No. 9013-22	Project Number DD-1451	DD-1451-8
Facade Custom	LGA Canterbury Bankstown	Current Revision 3 26/09/23	Ground Floor Plan
Inclusions Vogue	Approval Path DA	Date 18/03/22	Scale 1 : 100 @ A3

⑤ APPROX. LOCATION OF SMOKE ALARMS

Spacing of Articulation Joints - Unreinforced Masonry Walls				
Site class	Wall construction & surface finish	Joint Spacing (m)		
		Up to 4m high for 10mm joints	4m-5m high for 10mm joints	4m-5m high for 15mm joints
M, M-D	External face finish masonry	6.0	4.2	6.0
	Internal rendered and/or painted masonry	5.5	3.9	5.5
	Internal face finish or sheeted masonry	6.0	4.2	6.0
	Internal rendered and/or painted masonry	5.5	3.9	5.5
H, HL-D	External face finish masonry	5.5	3.9	5.5
	External rendered and/or painted masonry	5.0	3.5	5.0
	Internal face finish or sheeted masonry	5.5	3.9	5.5
	Internal rendered and/or painted masonry	5.0	3.5	5.0
H2, H2-D	External face finish masonry	5.0	3.5	5.0
	Internal rendered and/or painted masonry	4.5	3.2	4.5
	Internal face finish or sheeted masonry	5.0	3.5	5.0
	Internal rendered and/or painted masonry	4.5	3.2	4.5

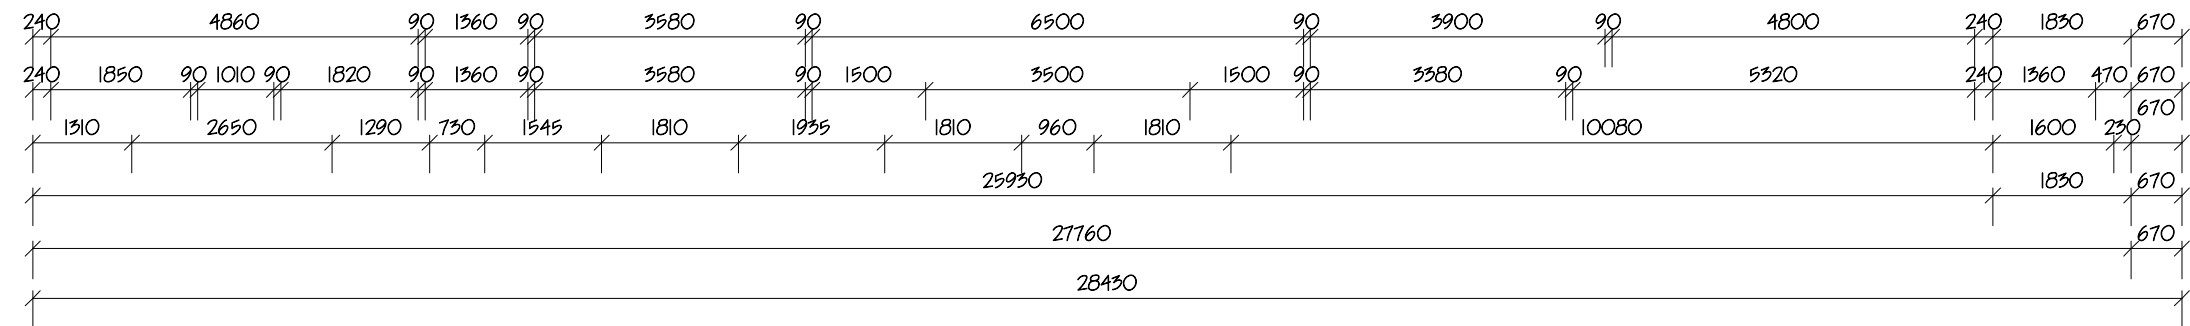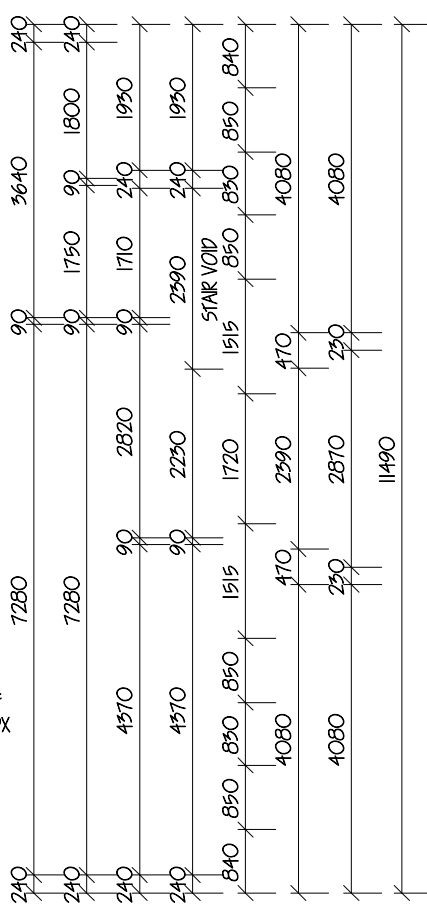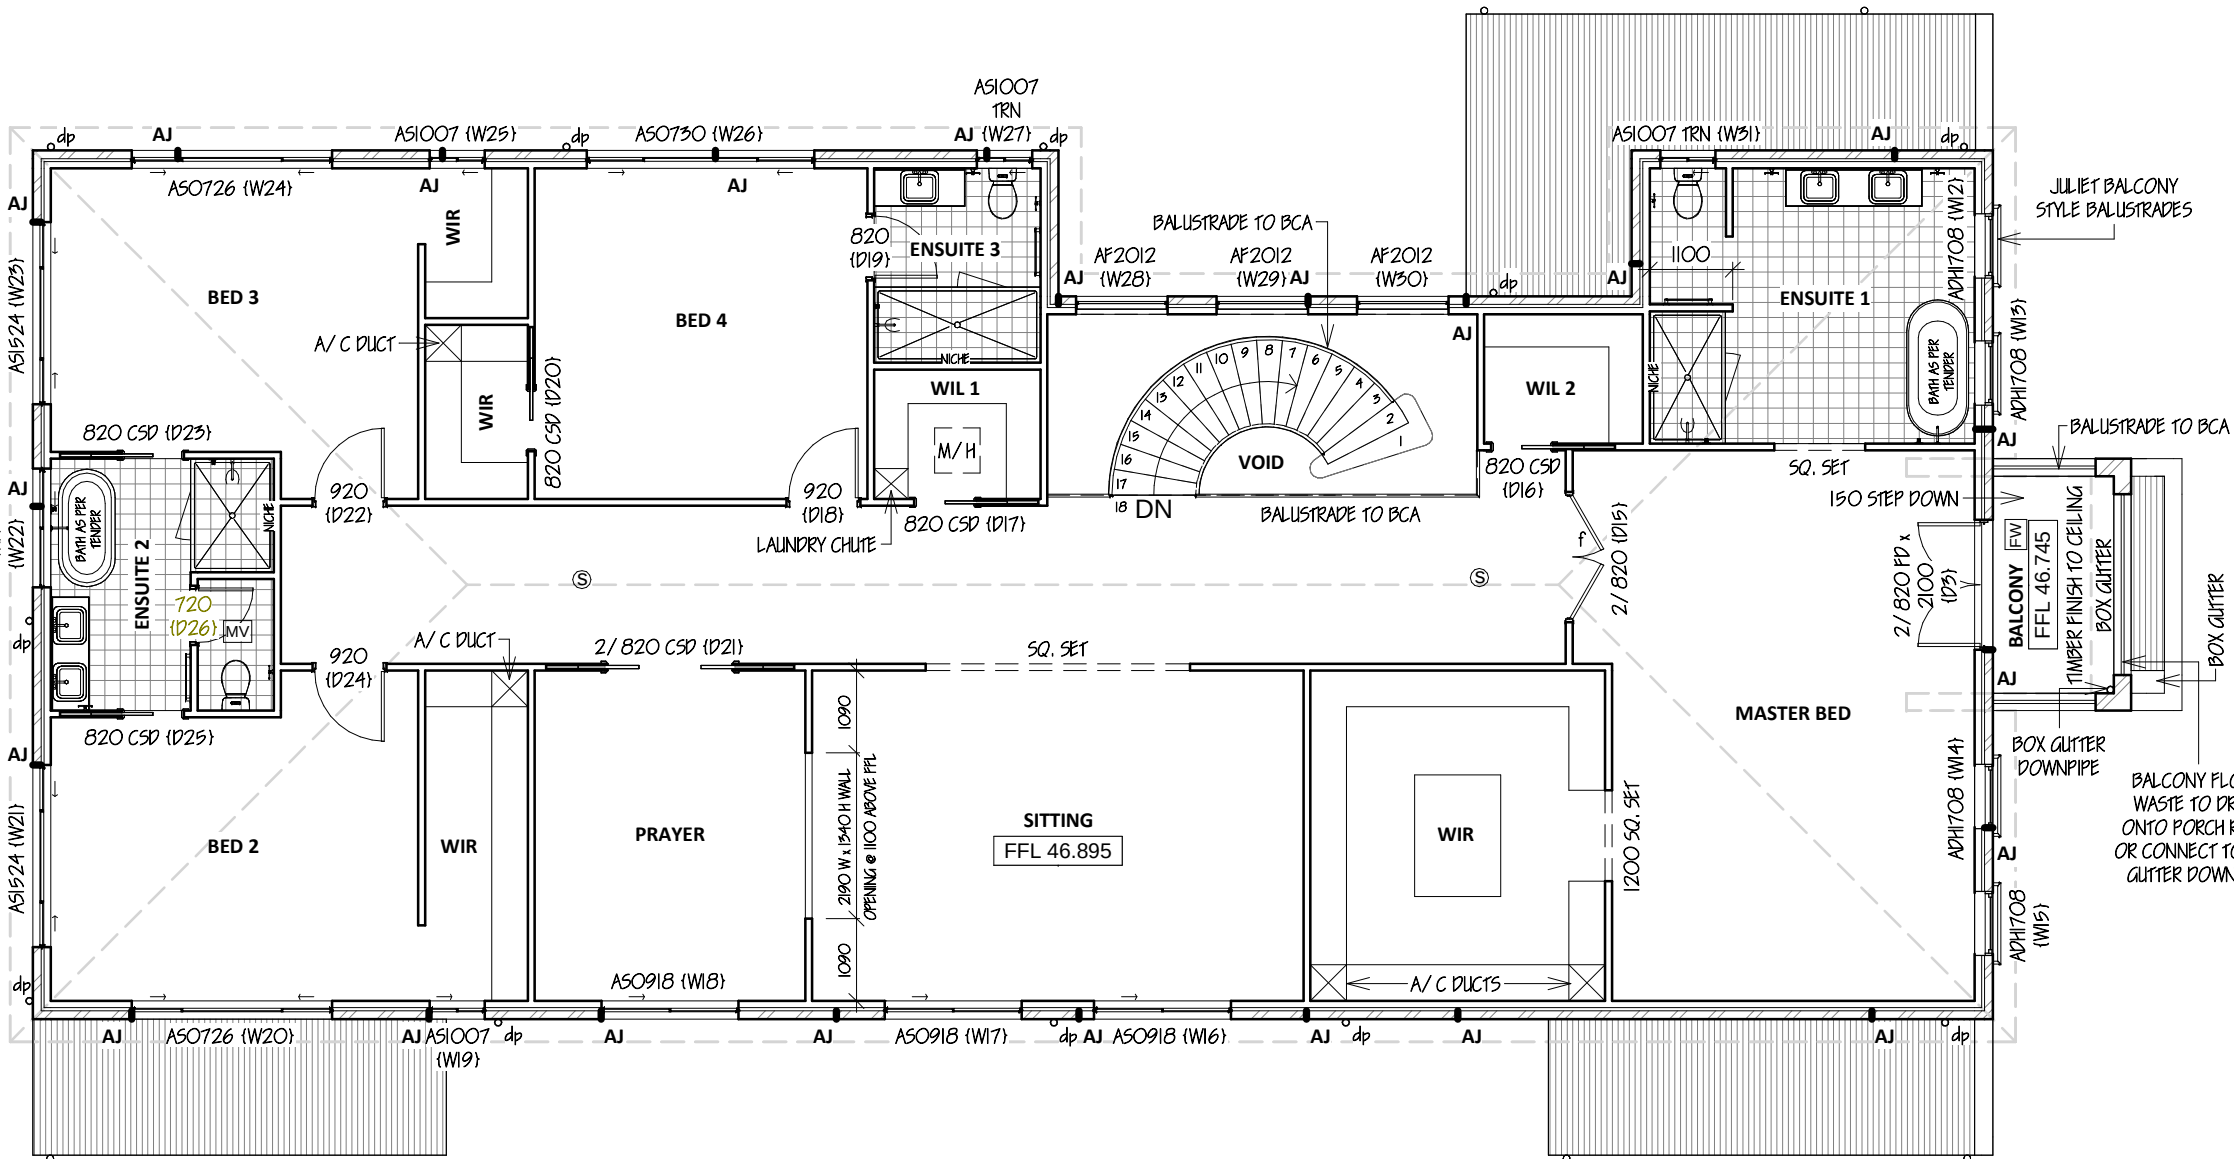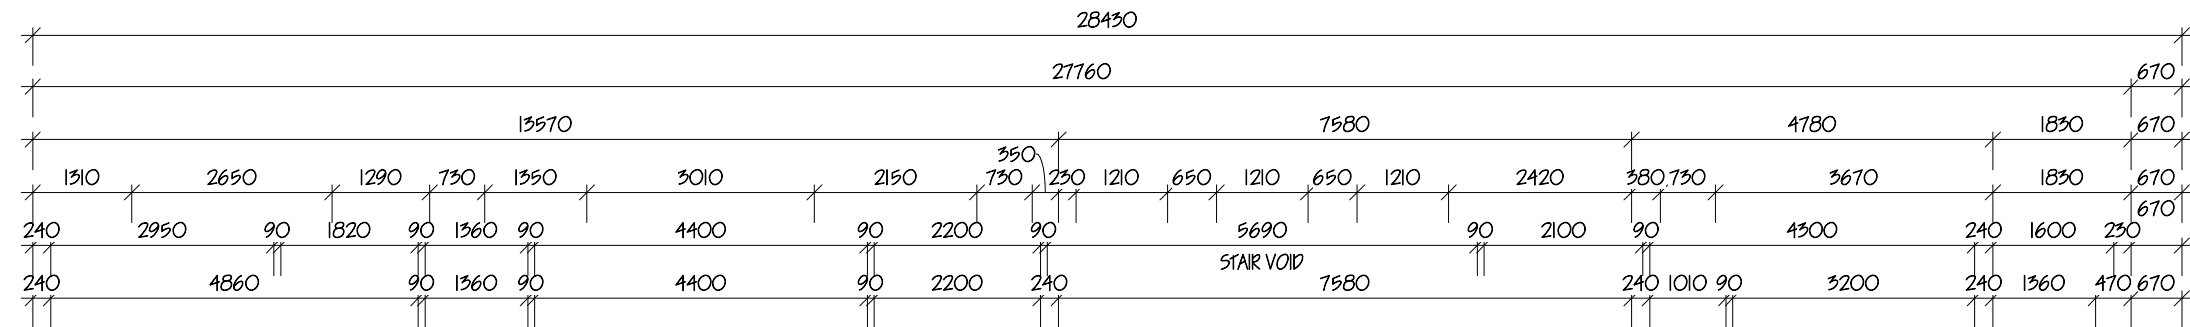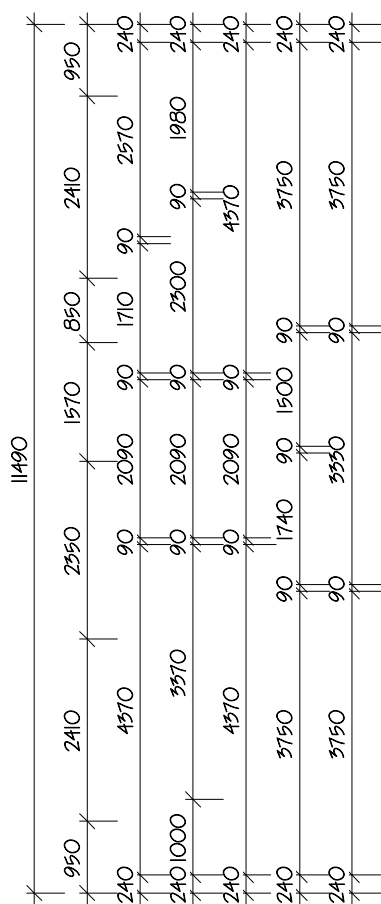

Disclaimer: Some items displayed or noted on these plans may be for indicative nominal placement or certification purposes only. The written words in any accompanying building tender will on all occasions take precedence to the plan. All internal room dimensions shown on any floor plan are to timber frame for construction purpose.



P: 0421 993 467
E: info@definitivedrafting.com.au
W: www.definitivedrafting.com.au

This drawing and information
theron is the property of Vogue
Homes and must not be loaned,
partly copied, fully copied or used
without the expressed permission
in license or writing



P: (02) 96079554
E: admin@vogue-homes.com.au
W: www.vogue-homes.com.au

Lot 5 DP 959294
118 William St Condell Park 2200

Inclusions
Vogue

Approval Path
DA

Date
18/03/22

Scale
1 : 100 @ A3

Materials Legend

Note: All materials on plan are to be confirmed with the associated building tender/selections document. Where a discrepancy occurs, the building tender/selections document takes precedence.

Walls


-  Face brick
-  Face brick
-  Render & painted finish
Wall material noted on plans
-  Render & painted finish
Wall material noted on plans
-  Texture coat & painted finish
on brickwork
-  Stacked stone or cultured stone
-  Fibre cement clad to AS 2908.2
-  Fibre cement clad to AS 2908.2
-  Fibre cement clad to AS 2908.2
-  Fibre cement clad to AS 2908.2
-  Fibre cement clad to AS 2908.2
-  Fibre cement board & timber
batten finish to AS 2908.2

Roofing

-  Concrete roof tiles
-  Colorbond
-  Klip-lok / Trimdek

Other (unless noted otherwise)


-  Aluminium windows
-  Aluminium sliding/stacker/bi-fold doors
-  Colorbond fascia & gutter
-  Translucent/obscure glazing
(see window schedule)

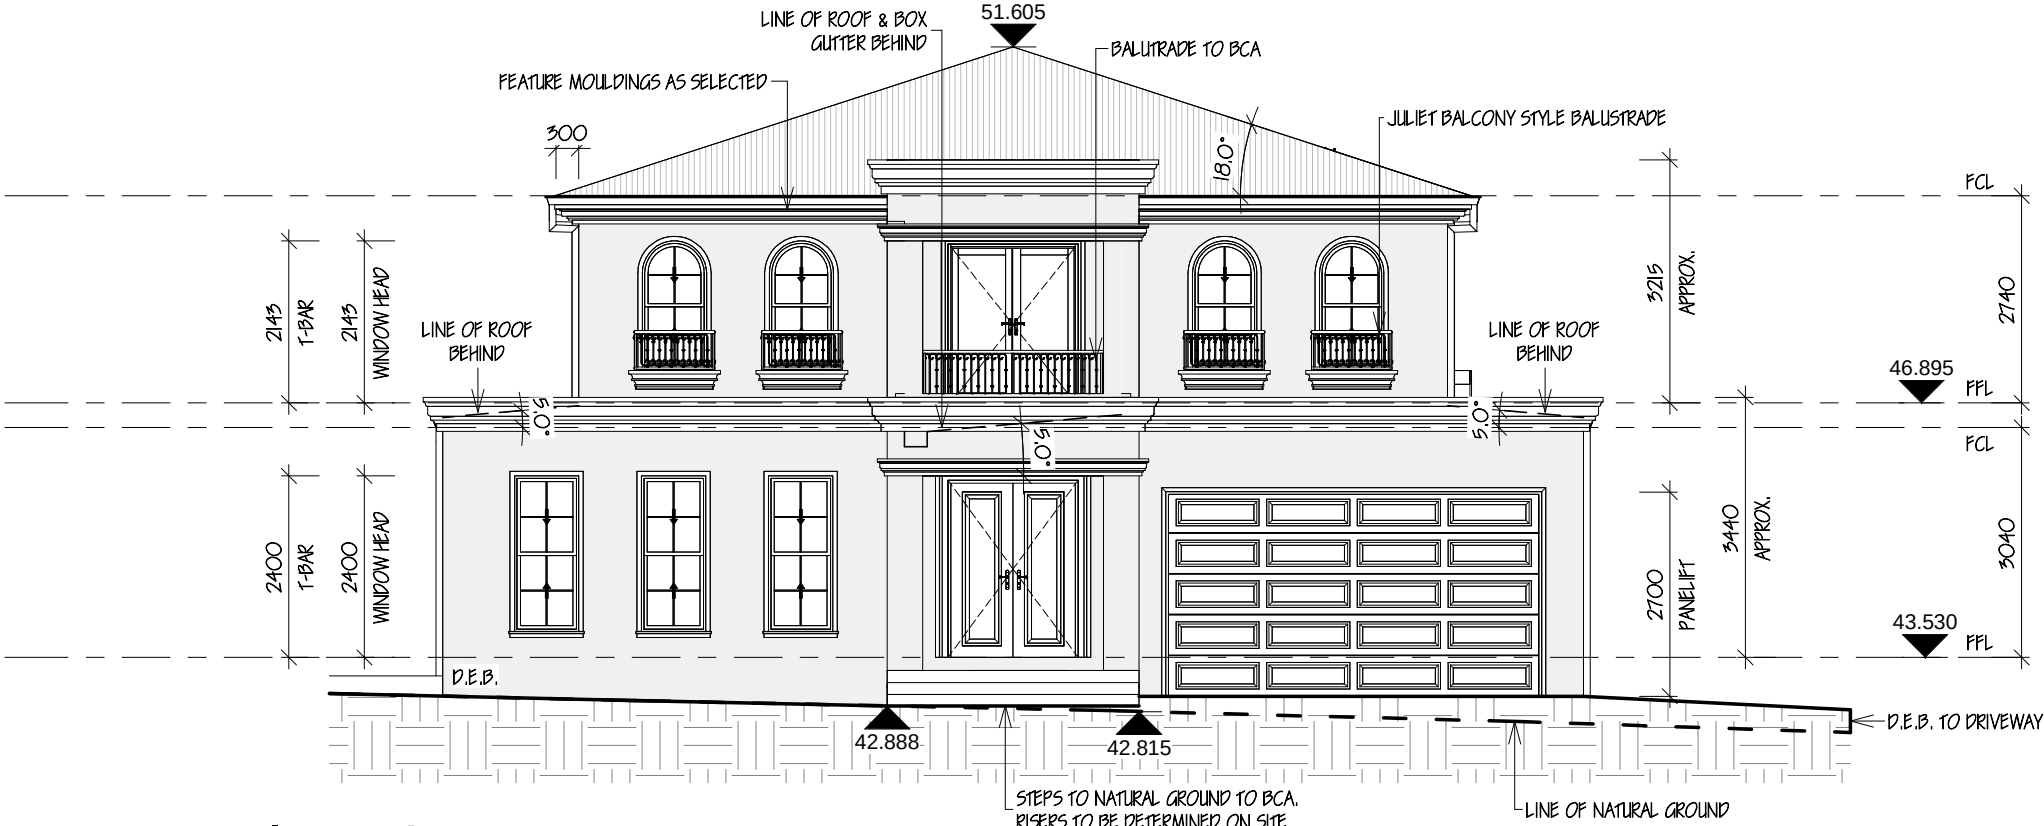

East Elevation

1 : 100

1

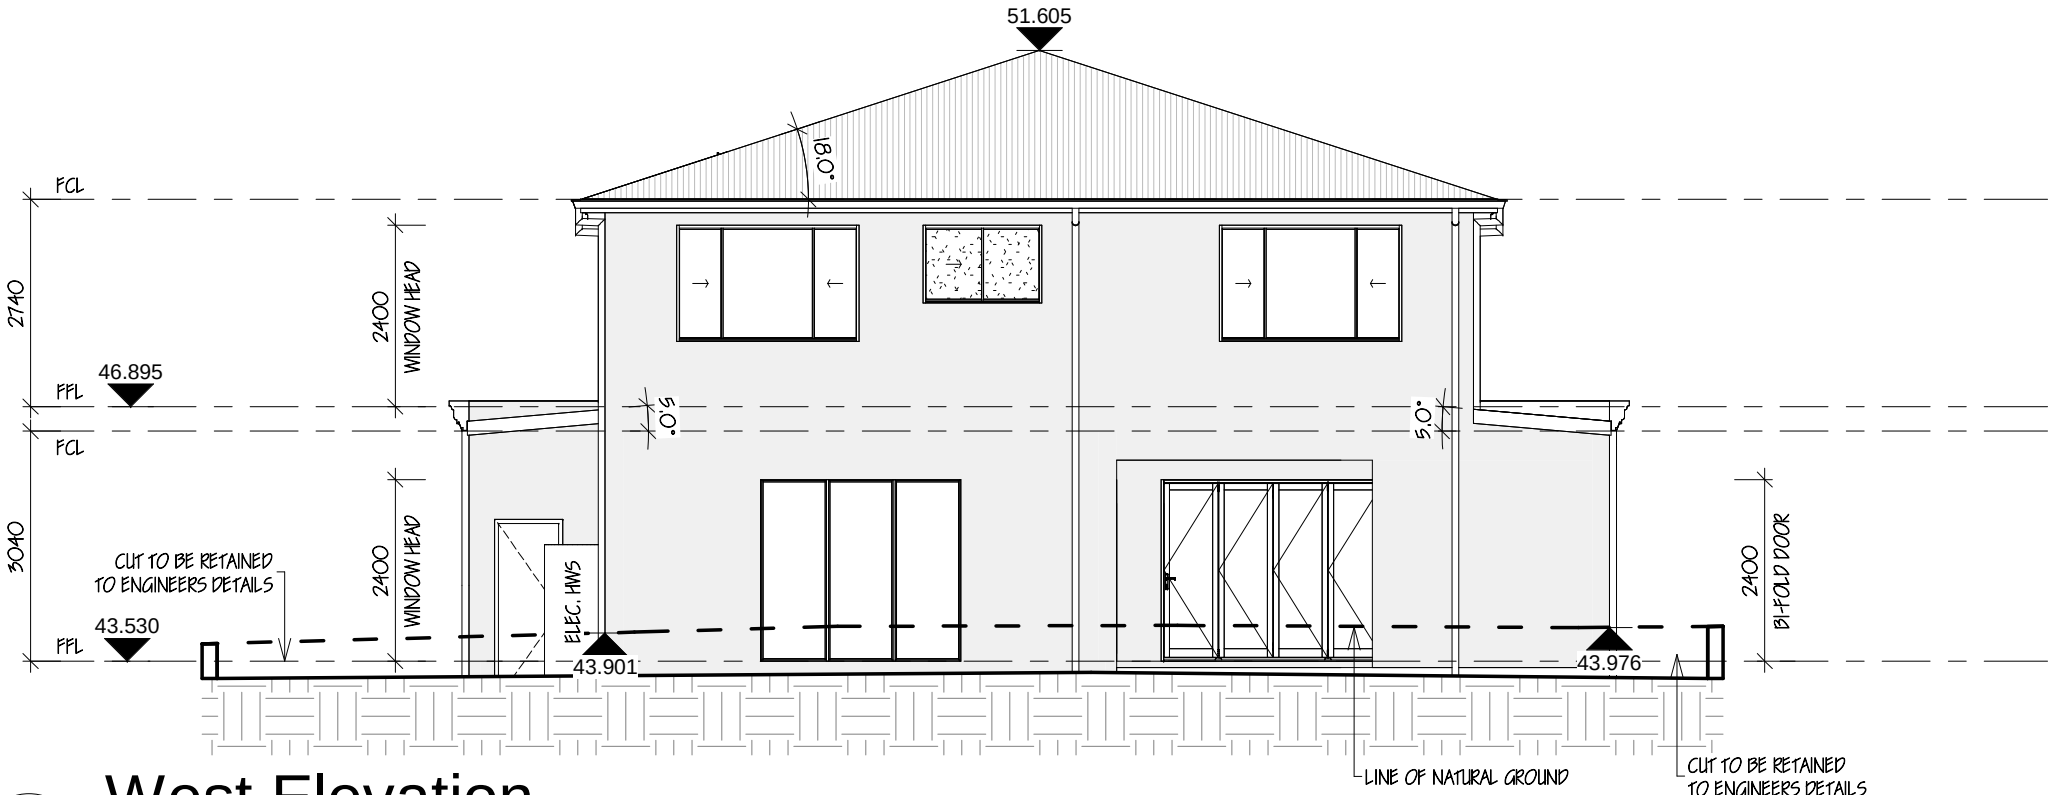



West Elevation

1 : 100

2

Disclaimer: Some items displayed or noted on these plans may be for indicative nominal placement or certification purposes only. The written words in any accompanying building tender will on all occasions take precedence to the plan. All internal room dimensions shown on any floor plan are to timber frame for construction purpose.

	ABN 67 250 466 867 Suite 7, Shop 11, 38 Exchange Parade Narellan NSW 2567 P: 0421 993 467 E: info@definitivedrafting.com.au W: www.definitivedrafting.com.au	This drawing and information thereon is the property of Vogue Homes and must not be loaned, partly copied, fully copied or used without the expressed permission in license or writing		License No. 115618C Unit 2/16 Weld Street Prestons NSW 2170 P: (02) 96079554 E: admin@vogue-homes.com.au W: www.vogue-homes.com.au	Hau Thi Bui & Toan Hoang Pham Lot 5 DP 959294 118 William St Condell Park 2200	Design Custom	Vogue Job No. 9013-22	Project Number DD-1451	DD-1451-10
						Facade Custom	LGA Canterbury Bankstown	Current Revision 3 26/09/23	Elevations
						Inclusions Vogue	Approval Path DA	Date 18/03/22	Scale 1 : 100 @ A3

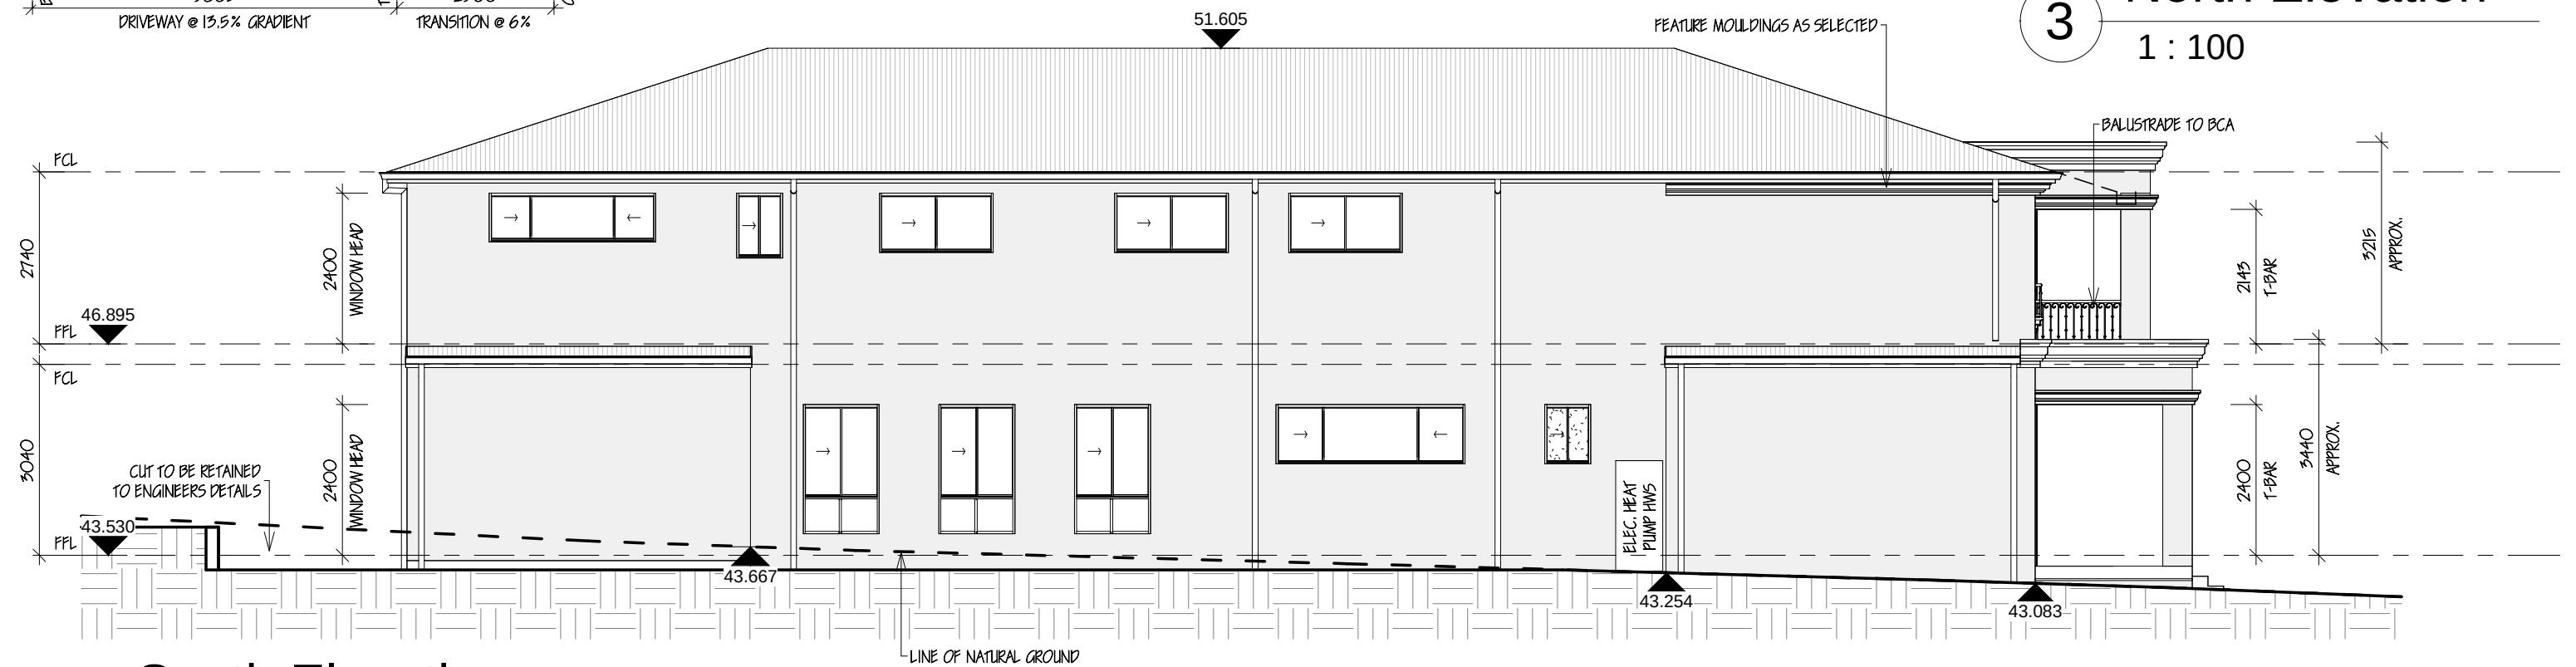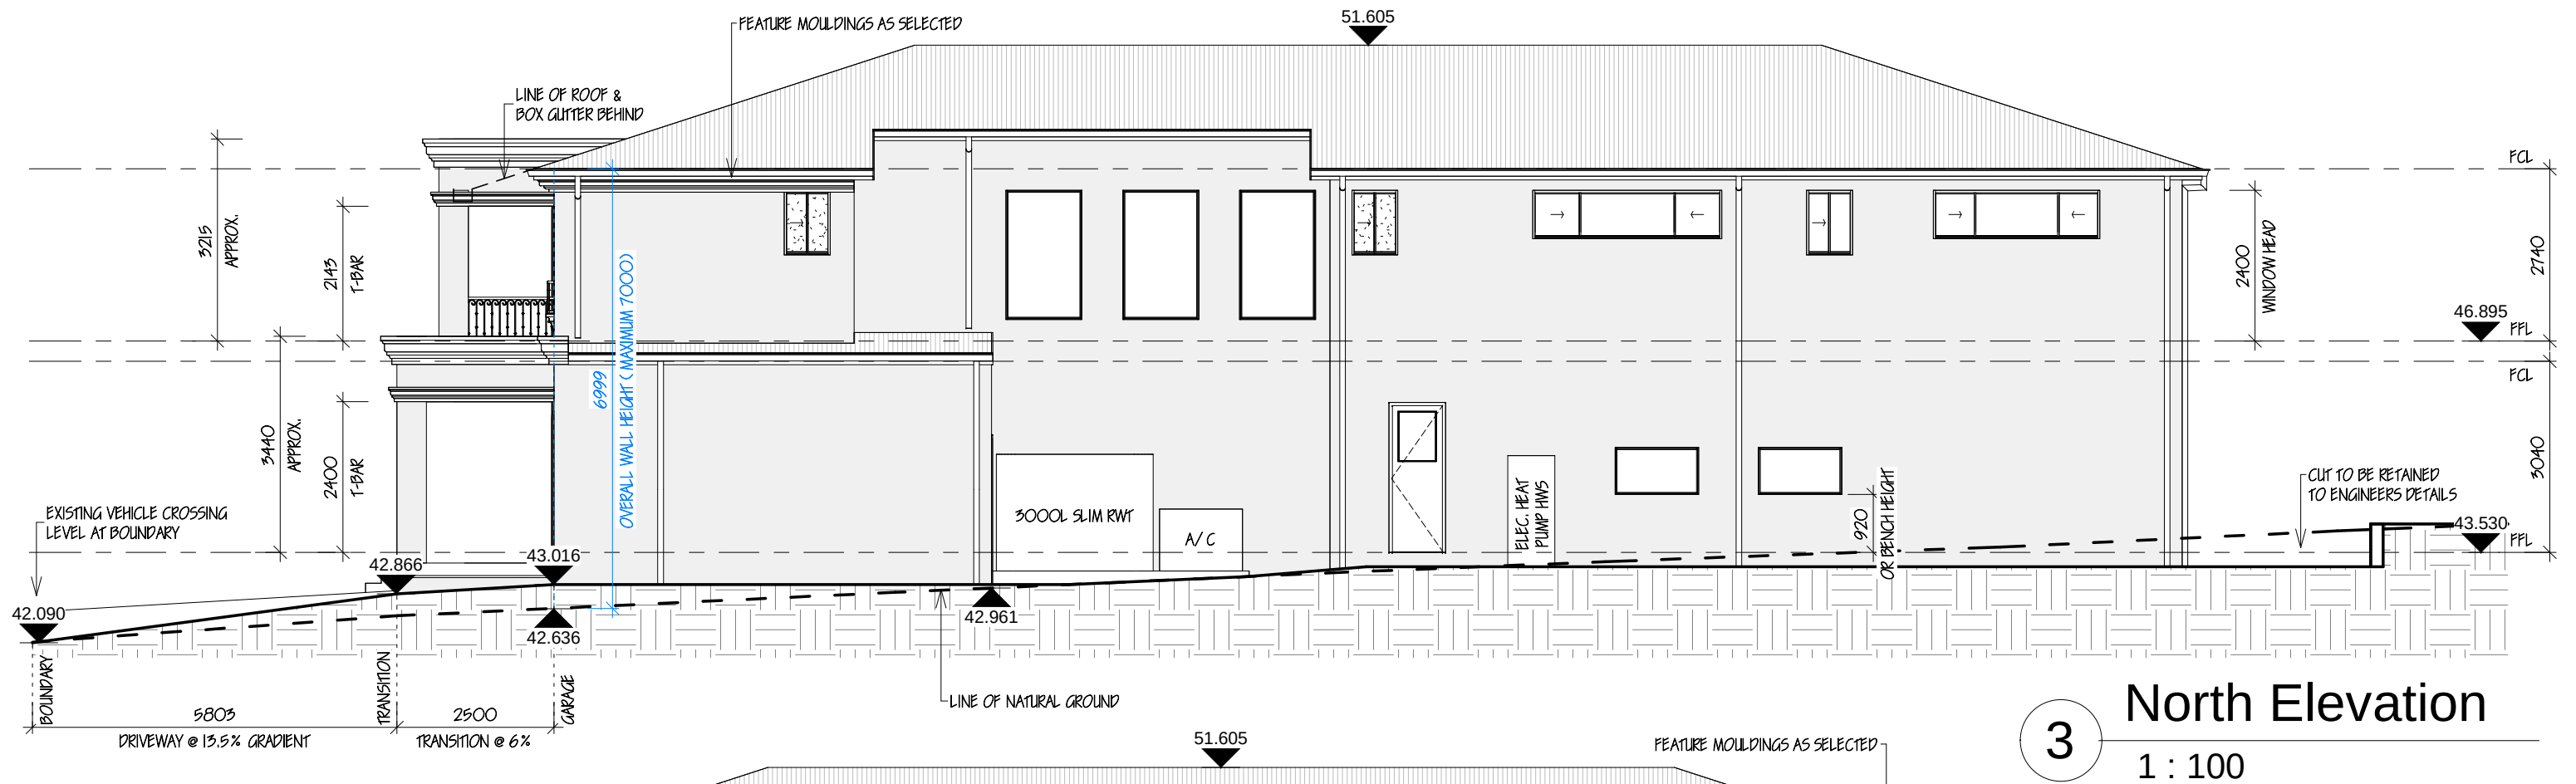

4 South Elevation

1 : 100


Materials Legend

Note: All materials on plan are to be confirmed with the associated building tender/selections document. Where a discrepancy occurs, the building tender/selections document takes precedence.


Walls		Roofing		Other (unless noted otherwise)	
	Face brick		Fibre cement clad to AS 2908.2		Aluminium windows
	Face brick		Fibre cement clad to AS 2908.2		Aluminium sliding / stacker / bi-fold doors
	Render & painted finish		Fibre cement clad to AS 2908.2		Colorbond fascia & gutter
	Stacked stone or cultured stone		Fibre cement board & timber batten finish to AS 2908.2		Translucent/obscure glazing (see schedule)
	Texture coat & painted finish on brickwork				

Disclaimer: Some items displayed or noted on these plans may be for indicative nominal placement or certification purposes only. The written words in any accompanying building tender will on all occasions take precedence to the plan. All internal room dimensions shown on any floor plan are to timber frame for construction purpose.


 definitivedrafting	ABN 67 250 466 867 Suite 7, Shop 11, 38 Exchange Parade Narellan NSW 2567 P: 0421 993 467 E: info@definitivedrafting.com.au W: www.definitivedrafting.com.au	This drawing and information theron is the property of Vogue Homes and must not be loaned, partly copied, fully copied or used without the expressed permission in license or writing	 VOGUE HOMES DESIGN - STYLE - ELEGANCE	License No. 115618C Unit 2/16 Weld Street Prestons NSW 2170 P: (02) 96079554 E: admin@vogue-homes.com.au W: www.vogue-homes.com.au	Hau Thi Bui & Toan Hoang Pham Lot 5 DP 959294 118 William St Condell Park 2200	<table><tr><td>Design Custom</td><td>Vogue Job No. 9013-22</td><td>Project Number DD-1451</td><td>DD-1451-11</td></tr><tr><td>Facade Custom</td><td>LGA Canterbury Bankstown</td><td>Current Revision 3 26/09/23</td><td>Elevations</td></tr><tr><td>Inclusions Vogue</td><td>Approval Path DA</td><td>Date 18/03/22</td><td>Scale 1 : 100 @ A3</td></tr></table>	Design Custom	Vogue Job No. 9013-22	Project Number DD-1451	DD-1451-11	Facade Custom	LGA Canterbury Bankstown	Current Revision 3 26/09/23	Elevations	Inclusions Vogue	Approval Path DA	Date 18/03/22	Scale 1 : 100 @ A3
	Design Custom	Vogue Job No. 9013-22	Project Number DD-1451	DD-1451-11														
	Facade Custom	LGA Canterbury Bankstown	Current Revision 3 26/09/23	Elevations														
Inclusions Vogue	Approval Path DA	Date 18/03/22	Scale 1 : 100 @ A3															

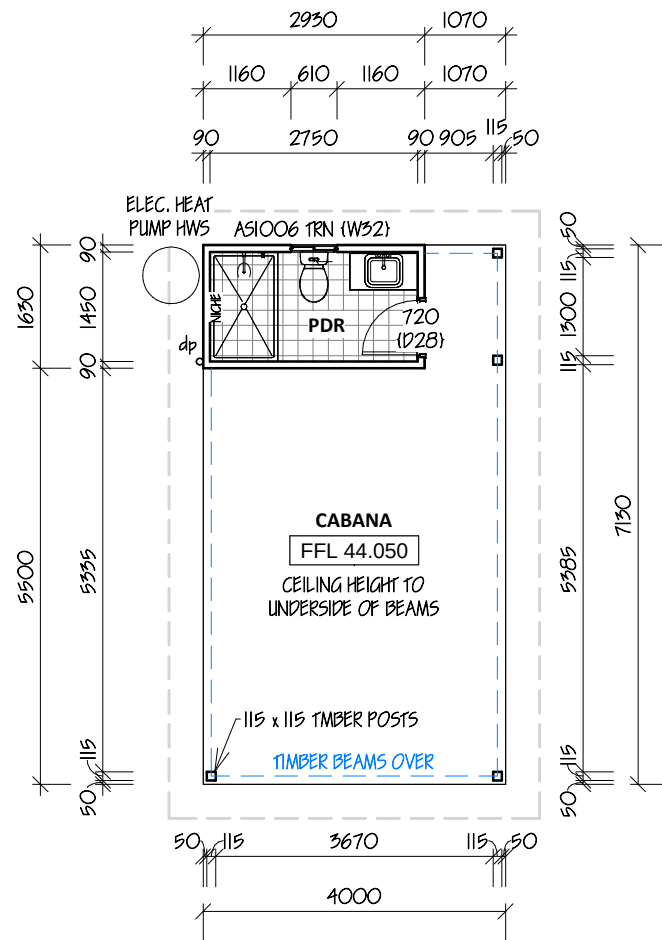


Cabana Floor
1 : 100

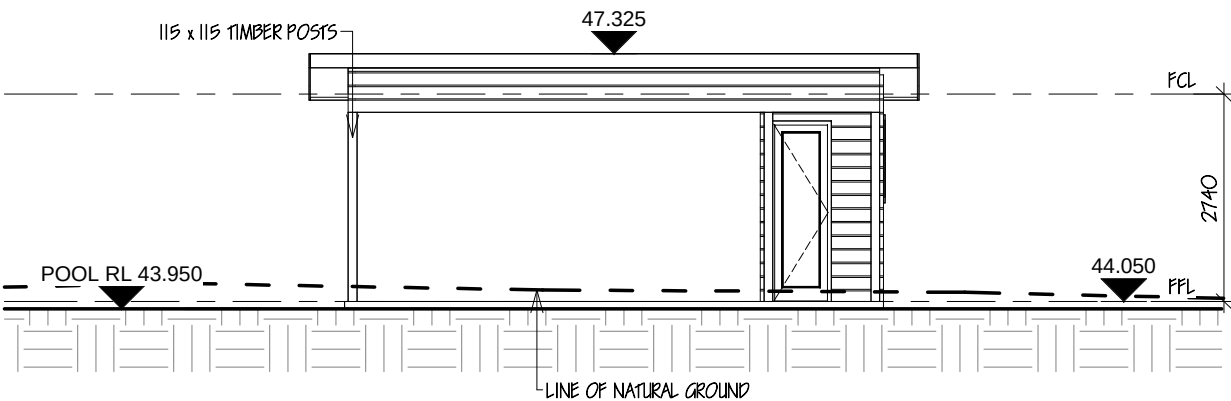


2 Cabana East Elevation
1 : 100

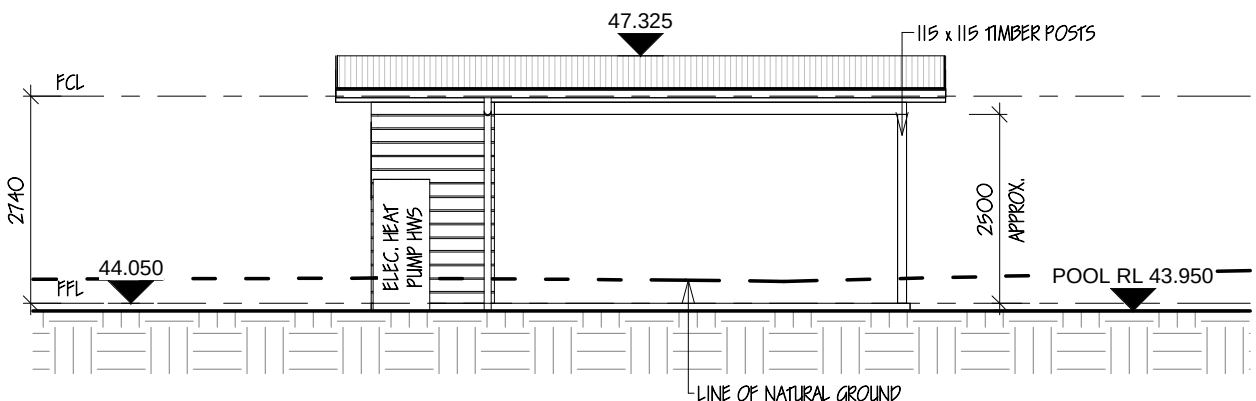

3 Cabana West Elevation
1 : 100

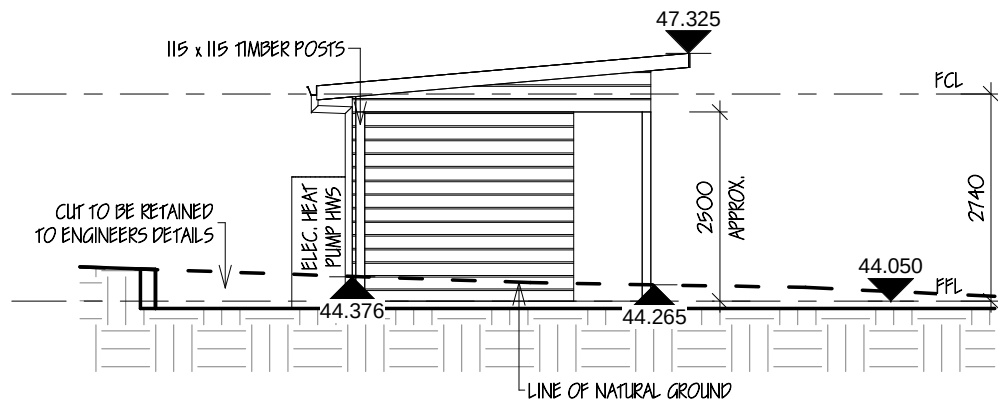

1 Cabana South Elevation
1 : 100

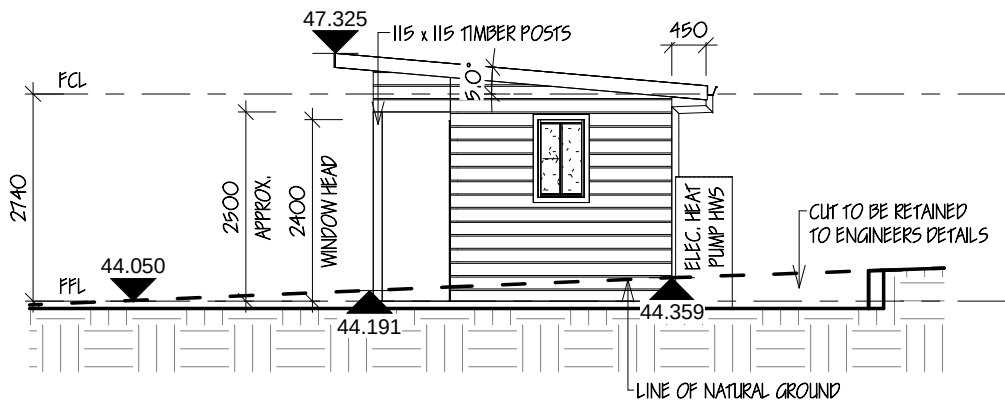



4 Cabana North Elevation
1 : 100

Disclaimer: Some items displayed or noted on these plans may be for indicative nominal placement or certification purposes only. The written words in any accompanying building tender will on all occasions take precedence to the plan. All internal room dimensions shown on any floor plan are to timber frame for construction purpose.

	ABN 67 250 466 867 Suite 7, Shop 11, 38 Exchange Parade Narellan NSW 2567 P: 0421 993 467 E: info@definitivedrafting.com.au W: www.definitivedrafting.com.au	This drawing and information thereon is the property of Vogue Homes and must not be loaned, partly copied, fully copied or used without the expressed permission in license or writing		License No. 115618C Unit 2/16 Weld Street Prestons NSW 2170 P: (02) 96079554 E: admin@vogue-homes.com.au W: www.vogue-homes.com.au	Hau Thi Bui & Toan Hoang Pham Lot 5 DP 959294 118 William St Condell Park 2200	Design Custom	Vogue Job No. 9013-22	Project Number DD-1451	DD-1451-12
						Facade Custom	LGA Canterbury Bankstown	Current Revision 3 26/09/23	Cabana Plans
						Inclusions Vogue	Approval Path DA	Date 18/03/22	Scale 1 : 100 @ A3


Window Schedule						
Mark	Material	Style	Height	Width	Glazing	Glass Area
W1	Aluminium	Double Hung	2058	850	Clear	1.75 m²
W2	Aluminium	Double Hung	2058	850	Clear	1.75 m²
W3	Aluminium	Double Hung	2058	850	Clear	1.75 m²
W4	Aluminium	Sliding	944	730	Translucent	0.69 m²
W5	Aluminium	Sliding	944	3010	Clear	2.84 m²
W6	Aluminium	Sliding	2058	1210	Clear	2.49 m²
W7	Aluminium	Sliding	2058	1210	Clear	2.49 m²
W8	Aluminium	Sliding	2058	1210	Clear	2.49 m²
W9	Aluminium	Fixed	2400	2650	Clear	6.36 m²
W10	Aluminium	Fixed	750	1330	Clear	1.00 m²
W11	Aluminium	Fixed	750	1330	Clear	1.00 m²
W12	Aluminium	Double Hung	1700	850	Clear	1.45 m²
W13	Aluminium	Double Hung	1700	850	Clear	1.45 m²
W14	Aluminium	Double Hung	1700	850	Clear	1.45 m²
W15	Aluminium	Double Hung	1700	850	Clear	1.45 m²
W16	Aluminium	Sliding	944	1810	Clear	1.71 m²
W17	Aluminium	Sliding	944	1810	Clear	1.71 m²
W18	Aluminium	Sliding	944	1810	Clear	1.71 m²
W19	Aluminium	Sliding	1030	730	Clear	0.75 m²
W20	Aluminium	Sliding	772	2650	Clear	2.05 m²
W21	Aluminium	Sliding	1540	2410	Clear	3.71 m²
W22	Aluminium	Sliding	1030	1570	Translucent	1.62 m²
W23	Aluminium	Sliding	1540	2410	Clear	3.71 m²
W24	Aluminium	Sliding	772	2650	Clear	2.05 m²
W25	Aluminium	Sliding	1030	730	Clear	0.75 m²
W26	Aluminium	Sliding	772	3010	Clear	2.32 m²
W27	Aluminium	Sliding	1030	730	Translucent	0.75 m²
W28	Aluminium	Fixed	2058	1210	Clear	2.49 m²
W29	Aluminium	Fixed	2058	1210	Clear	2.49 m²
W30	Aluminium	Fixed	2058	1210	Clear	2.49 m²
W31	Aluminium	Sliding	1030	730	Translucent	0.75 m²
W32	Aluminium	Sliding	1030	610	Translucent	0.63 m²

Door Schedule				
Mark	Material	Type	Height	Width
D1	Aluminium	External Bi-fold	2400	3686
D2	Aluminium	External Bi-fold	2400	3686
D3	Aluminium	External French Door	2100	1720
D4	Colorbond	Panelift	2700	4900
D5	Solid	Entry Double	2340	1720
D6	Semi-solid	External Garage	2340	820
D7	Semi-solid/Glass	External Laundry	2340	820
D8	Hollow Core	Internal	2340	820
D9	Hollow Core	Internal	2340	820
D10	Hollow Core	Internal	2340	820
D11	Hollow Core	Internal CSD	2340	820
D12	Hollow Core	Internal CSD	2340	1200
D13	Hollow Core	Internal	2340	820
D14	Hollow Core	Internal CSD	2340	820
D15	Hollow Core	Internal Double	2340	1720
D16	Hollow Core	Internal CSD	2340	820
D17	Hollow Core	Internal CSD	2340	820
D18	Hollow Core	Internal	2340	920
D19	Hollow Core	Internal	2340	820
D20	Hollow Core	Internal CSD	2340	820
D21	Hollow Core	Internal Double CSD	2340	820
D22	Hollow Core	Internal	2340	920
D23	Hollow Core	Internal CSD	2340	820
D24	Hollow Core	Internal	2340	920
D25	Hollow Core	Internal CSD	2340	820
D26	Hollow Core	Internal	2340	720
D27	Aluminium	Sliding Robe	2400	4090
D28	Semi-solid/Glass	External Swing	2340	720

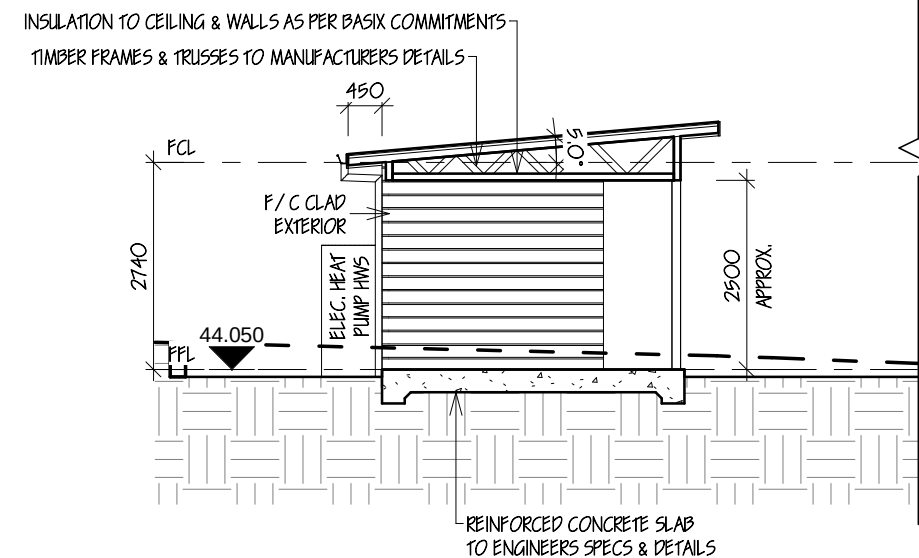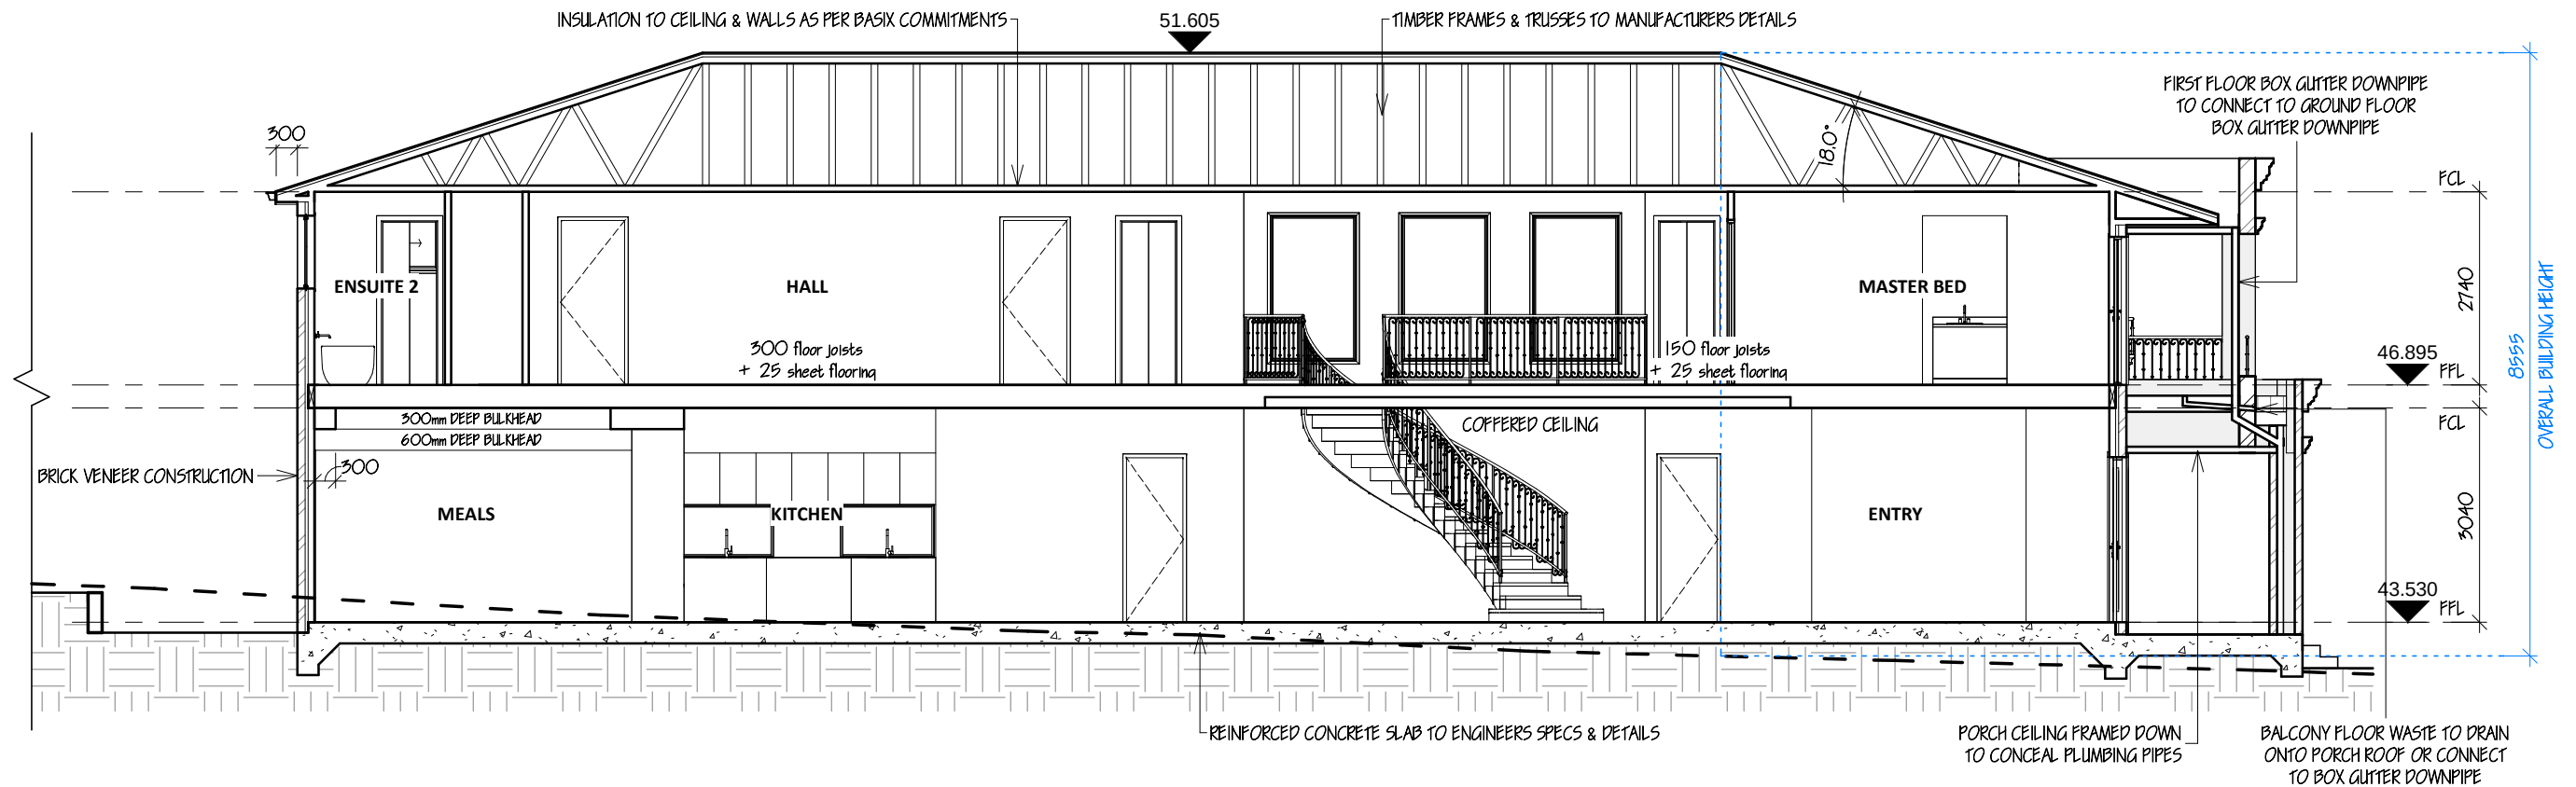


Disclaimer: Some items displayed or noted on these plans may be for indicative nominal placement or certification purposes only. The written words in any accompanying building tender will on all occasions take precedence to the plan. All internal room dimensions shown on any floor plan are to timber frame for construction purpose.

	ABN 67 250 466 867 Suite 7, Shop 11, 38 Exchange Parade Narellan NSW 2567 P: 0421 993 467 E: info@definitivedrafting.com.au W: www.definitivedrafting.com.au	This drawing and information thereon is the property of Vogue Homes and must not be loaned, partly copied, fully copied or used without the expressed permission in license or writing		License No. 115618C Unit 2/16 Weld Street Prestons NSW 2170 P: (02) 96079554 E: admin@vogue-homes.com.au W: www.vogue-homes.com.au	Hau Thi Bui & Toan Hoang Pham Lot 5 DP 959294 118 William St Condell Park 2200	Design Custom	Vogue Job No. 9013-22	Project Number DD-1451	DD-1451-14
						Facade Custom	LGA Canterbury Bankstown	Current Revision 3 26/09/23	Sections
						Inclusions Vogue	Approval Path DA	Date 18/03/22	Scale 1 : 100 @ A3

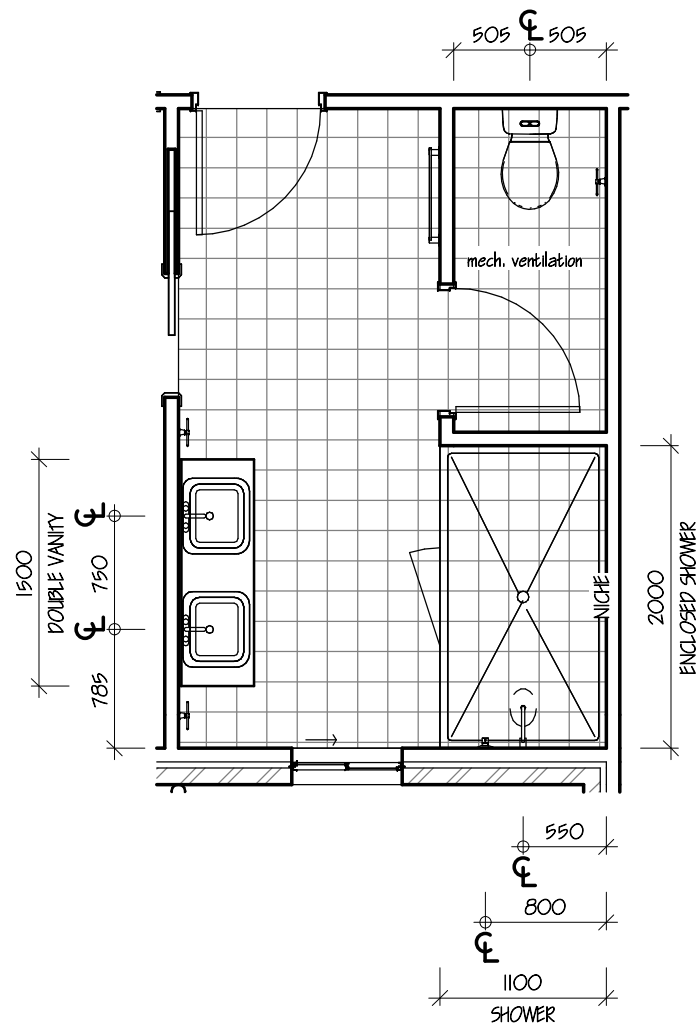


Ensuite 4 Detail

1 : 50

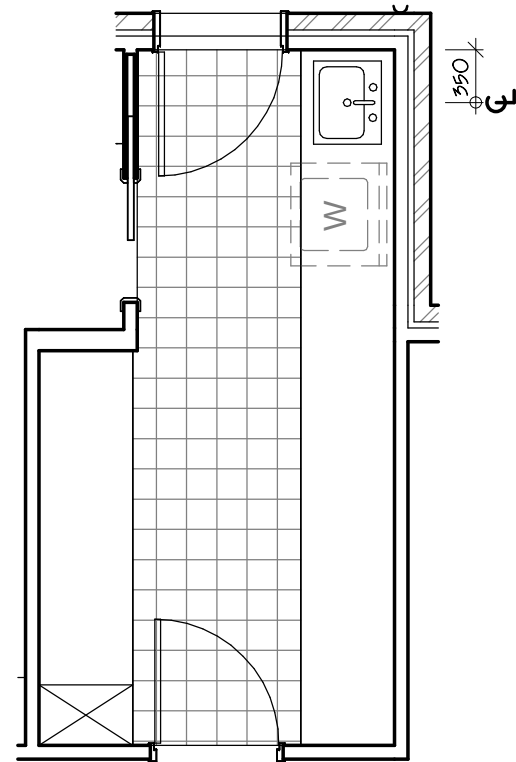


Laundry Detail

1 : 50

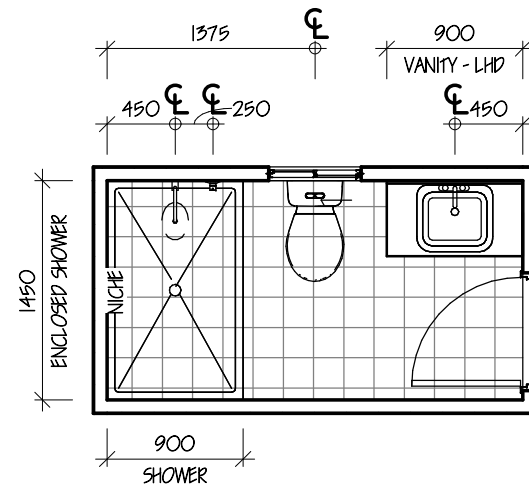

PDR Detail

1 : 50

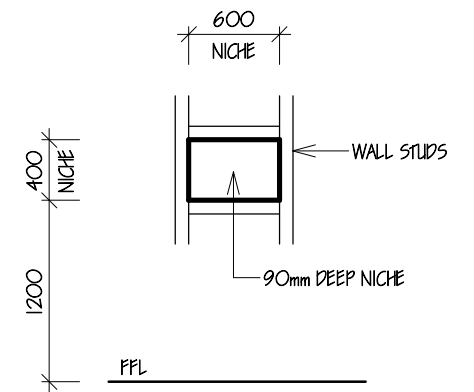

Shower Niche Detail

1 : 50


STANDARD BATHROOM PC ITEMS FIXING HEIGHTS

Note: Guide only, to be confirmed by selections and/or supervisor on site


TOWEL RAIL:	1100 ABOVE FFL or 1700 IF OVER BATH
TOWEL RING:	1100 ABOVE FFL or 1400 IF OVER VANITY DRAWERS
TOILET ROLL HOLDER:	600 ABOVE FFL
SHOWER HEAD:	1900 ABOVE FFL
SHOWER MIXER:	1050 ABOVE FFL
BATH SPOUT:	700 ABOVE FFL
BATH MIXER:	700 ABOVE FFL
WALL HUNG VANITY:	900 TO TOP OF VANITY/BOWL or ALIGN WITH OTHER FLOOR STANDING UNITS or ALIGN WITH NEAREST TILE LINE

Disclaimer: Some items displayed or noted on these plans may be for indicative nominal placement or certification purposes only. The written words in any accompanying building tender will on all occasions take precedence to the plan. All internal room dimensions shown on any floor plan are to timber frame for construction purpose.


	ABN 67 250 466 867 Suite 7, Shop 11, 38 Exchange Parade Narellan NSW 2567 P: 0421 993 467 E: info@definitivedrafting.com.au W: www.definitivedrafting.com.au	This drawing and information theron is the property of Vogue Homes and must not be loaned, partly copied, fully copied or used without the expressed permission in license or writing		License No. 115618C Unit 2/16 Weld Street Prestons NSW 2170 P: (02) 96079554 E: admin@vogue-homes.com.au W: www.vogue-homes.com.au	Hau Thi Bui & Toan Hoang Pham Lot 5 DP 959294 118 William St Condell Park 2200	Design Custom	Vogue Job No. 9013-22	Project Number DD-1451	DD-1451-15
						Facade Custom	LGA Canterbury Bankstown	Current Revision 3 26/09/23	GF Wet Area Details
						Inclusions Vogue	Approval Path DA	Date 18/03/22	Scale 1 : 50 @ A3

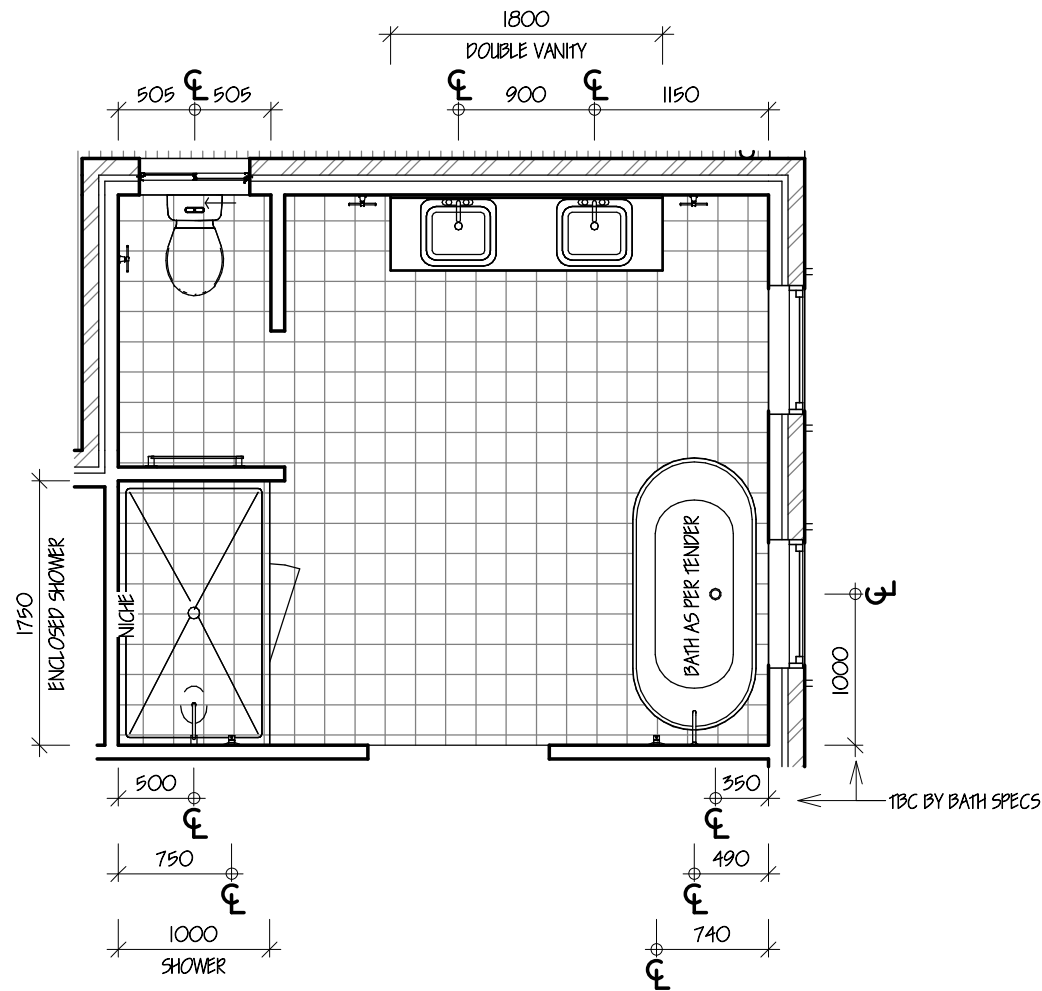


1 Ensuite 1 Detail
1 : 50

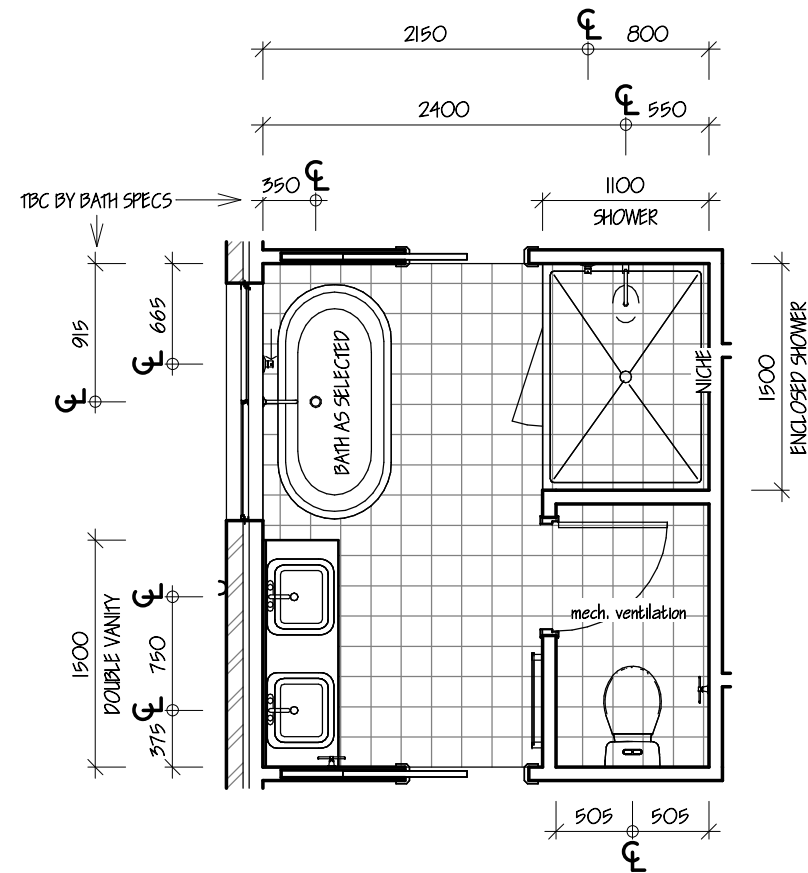

2 Ensuite 2 Detail
1 : 50

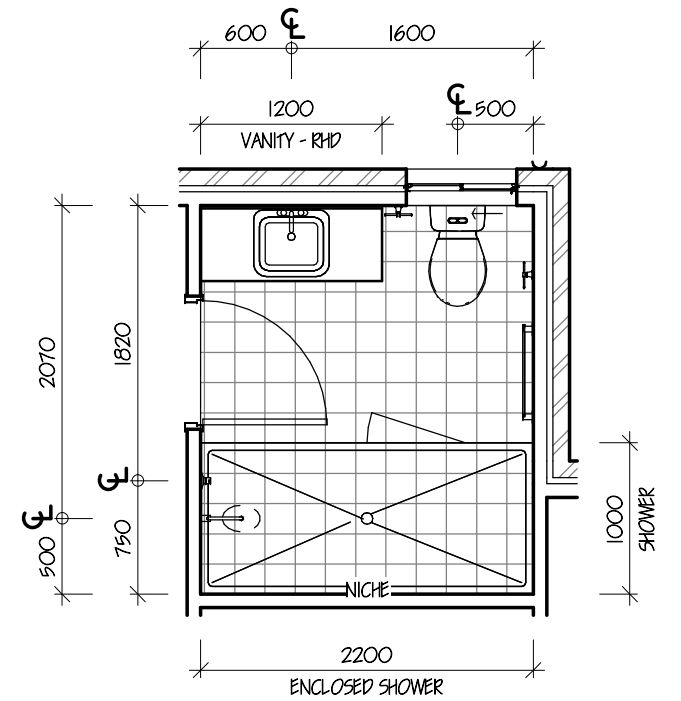

3 Ensuite 3 Detail
1 : 50

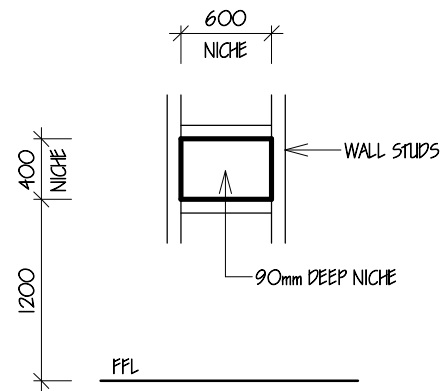

4 Shower Niche Detail
1 : 50

STANDARD BATHROOM PC ITEMS FIXING HEIGHTS

Note: Guide only, to be confirmed by selections and/or supervisor on site

TOWEL RAIL:	1100 ABOVE FFL or 1700 IF OVER BATH
TOWEL RING:	1100 ABOVE FFL or 1400 IF OVER VANITY DRAWERS
TOILET ROLL HOLDER:	600 ABOVE FFL
SHOWER HEAD:	1900 ABOVE FFL
SHOWER MIXER:	1050 ABOVE FFL
BATH SPOUT:	700 ABOVE FFL
BATH MIXER:	700 ABOVE FFL
WALL HUNG VANITY:	900 TO TOP OF VANITY/BOWL or ALIGN WITH OTHER FLOOR STANDING UNITS or ALIGN WITH NEAREST TILE LINE

Disclaimer: Some items displayed or noted on these plans may be for indicative nominal placement or certification purposes only. The written words in any accompanying building tender will on all occasions take precedence to the plan. All internal room dimensions shown on any floor plan are to timber frame for construction purpose.

	ABN 67 250 466 867 Suite 7, Shop 11, 38 Exchange Parade Narellan NSW 2567 P: 0421 993 467 E: info@definitivedrafting.com.au W: www.definitivedrafting.com.au	This drawing and information thereon is the property of Vogue Homes and must not be loaned, partly copied, fully copied or used without the expressed permission in license or writing		License No. 115618C Unit 2/16 Weld Street Prestons NSW 2170 P: (02) 96079554 E: admin@vogue-homes.com.au W: www.vogue-homes.com.au	Hau Thi Bui & Toan Hoang Pham Lot 5 DP 959294 118 William St Condell Park 2200	Design Custom	Vogue Job No. 9013-22	Project Number DD-1451	DD-1451-16
						Facade Custom	LGA Canterbury Bankstown	Current Revision 3 26/09/23	FF Wet Area Details
						Inclusions Vogue	Approval Path DA	Date 18/03/22	Scale 1 : 50 @ A3

PROPOSED NEW DWELLING


PROPOSED DRIVEWAY
APPROXIMATE AREA = 153m²

AREA OF SOFT LANDSCAPING (TURF & GARDEN BEDS)
APPROXIMATE AREA = 339m²


Appendix 5-Suggested trees for native landscaping purposes

Australian Native Species	Common Name	Preferred Soil
Acacia binervia	Myall Wattle	Sand/Clay*
Acmena smithii	Lilli Pilli	
Angophora costata	Smooth Barked Apple	
Backhousia citriodora	Lemon Scented Myrtle	
Backhousia floribunda	Flowering Myrtle	
Banksia serrata	Old Man Banksia	Sand*
Brachychiton populneum	Kurrajong	
Callistemon citrinus	Crimson Bottlebrush	
Callistemon pinifolius	Green Bottlebrush	
Callistemon viminalis	Weeping Bottlebrush	
Ceratopetalum gummiiferum	Christmas Bush	
Elaeocarpus reticulatus	Blueberry Ash	Sand*
Eucalyptus eugenioides	Thin Leaf Stringybark	Clay*
Eucalyptus fibrosa	Broad Leaf Ironbark	Clay*
Eucalyptus gummifera	Red bloodwood	Sand*
Eucalyptus haemastoma	Scribbly Gum	Sand*
Eucalyptus longifolia	Woollybutt	Clay*
Eucalyptus moluccana	Grey Box	Clay*
Eucalyptus resinifera	Red Mahogany	Sand/Clay*
Eucalyptus sideroxylon	Mugga Ironbark	Clay*
Eucalyptus tereticornis	Forest Redgum	Clay*
Flindersia australis	Australian Teak/ Crows Ash	
Glochidion ferdinandii	Cheese Tree	
Harpullia pendula	Tulipwood	
Hymenosporum flavum	Native Frangipani	
Leptospermum petersonii	Lemon Scented Tea Tree	Sand/Clay*
Lophostemon conferta	Brushbox	
Melaleuca decora	White Feather Honey Myrtle	Clay*
Melaleuca linariifolia	Narrow Leaf Paperbark	Clay*
Pittosporum revolutum	Yellow/ Rough Fruit Pittosporum	
Pittosporum rhombifolium	Diamond Leaf Pittosporum	
Podocarpus elatus	Illawarra Plum	
Stenocarpus sinuatus	Queensland Firewheel Tree	
Syncarpia glomulifera	Turpentine	Sand/Clay*
Syzygium luehmannii	Small Leaf Lilli Pilli	
Syzygium paniculatum	Brush Cherry	
Syzygium oleosum	Blue Lilli Pilli	
Tristaniopsis laurina	Water Gum	
Waterhousia floribunda	Weeping Lilli Pilli	

* Asterix denotes plant species native to Bankstown area. **NOTE:** Plants listed will benefit from improved garden soil conditions, irrigation and ongoing maintenance. The above plant list is not exhaustive, additional species may be considered. Planting to be determined with concession to site conditions, aspect, exposure, drainage and surrounding vegetation.

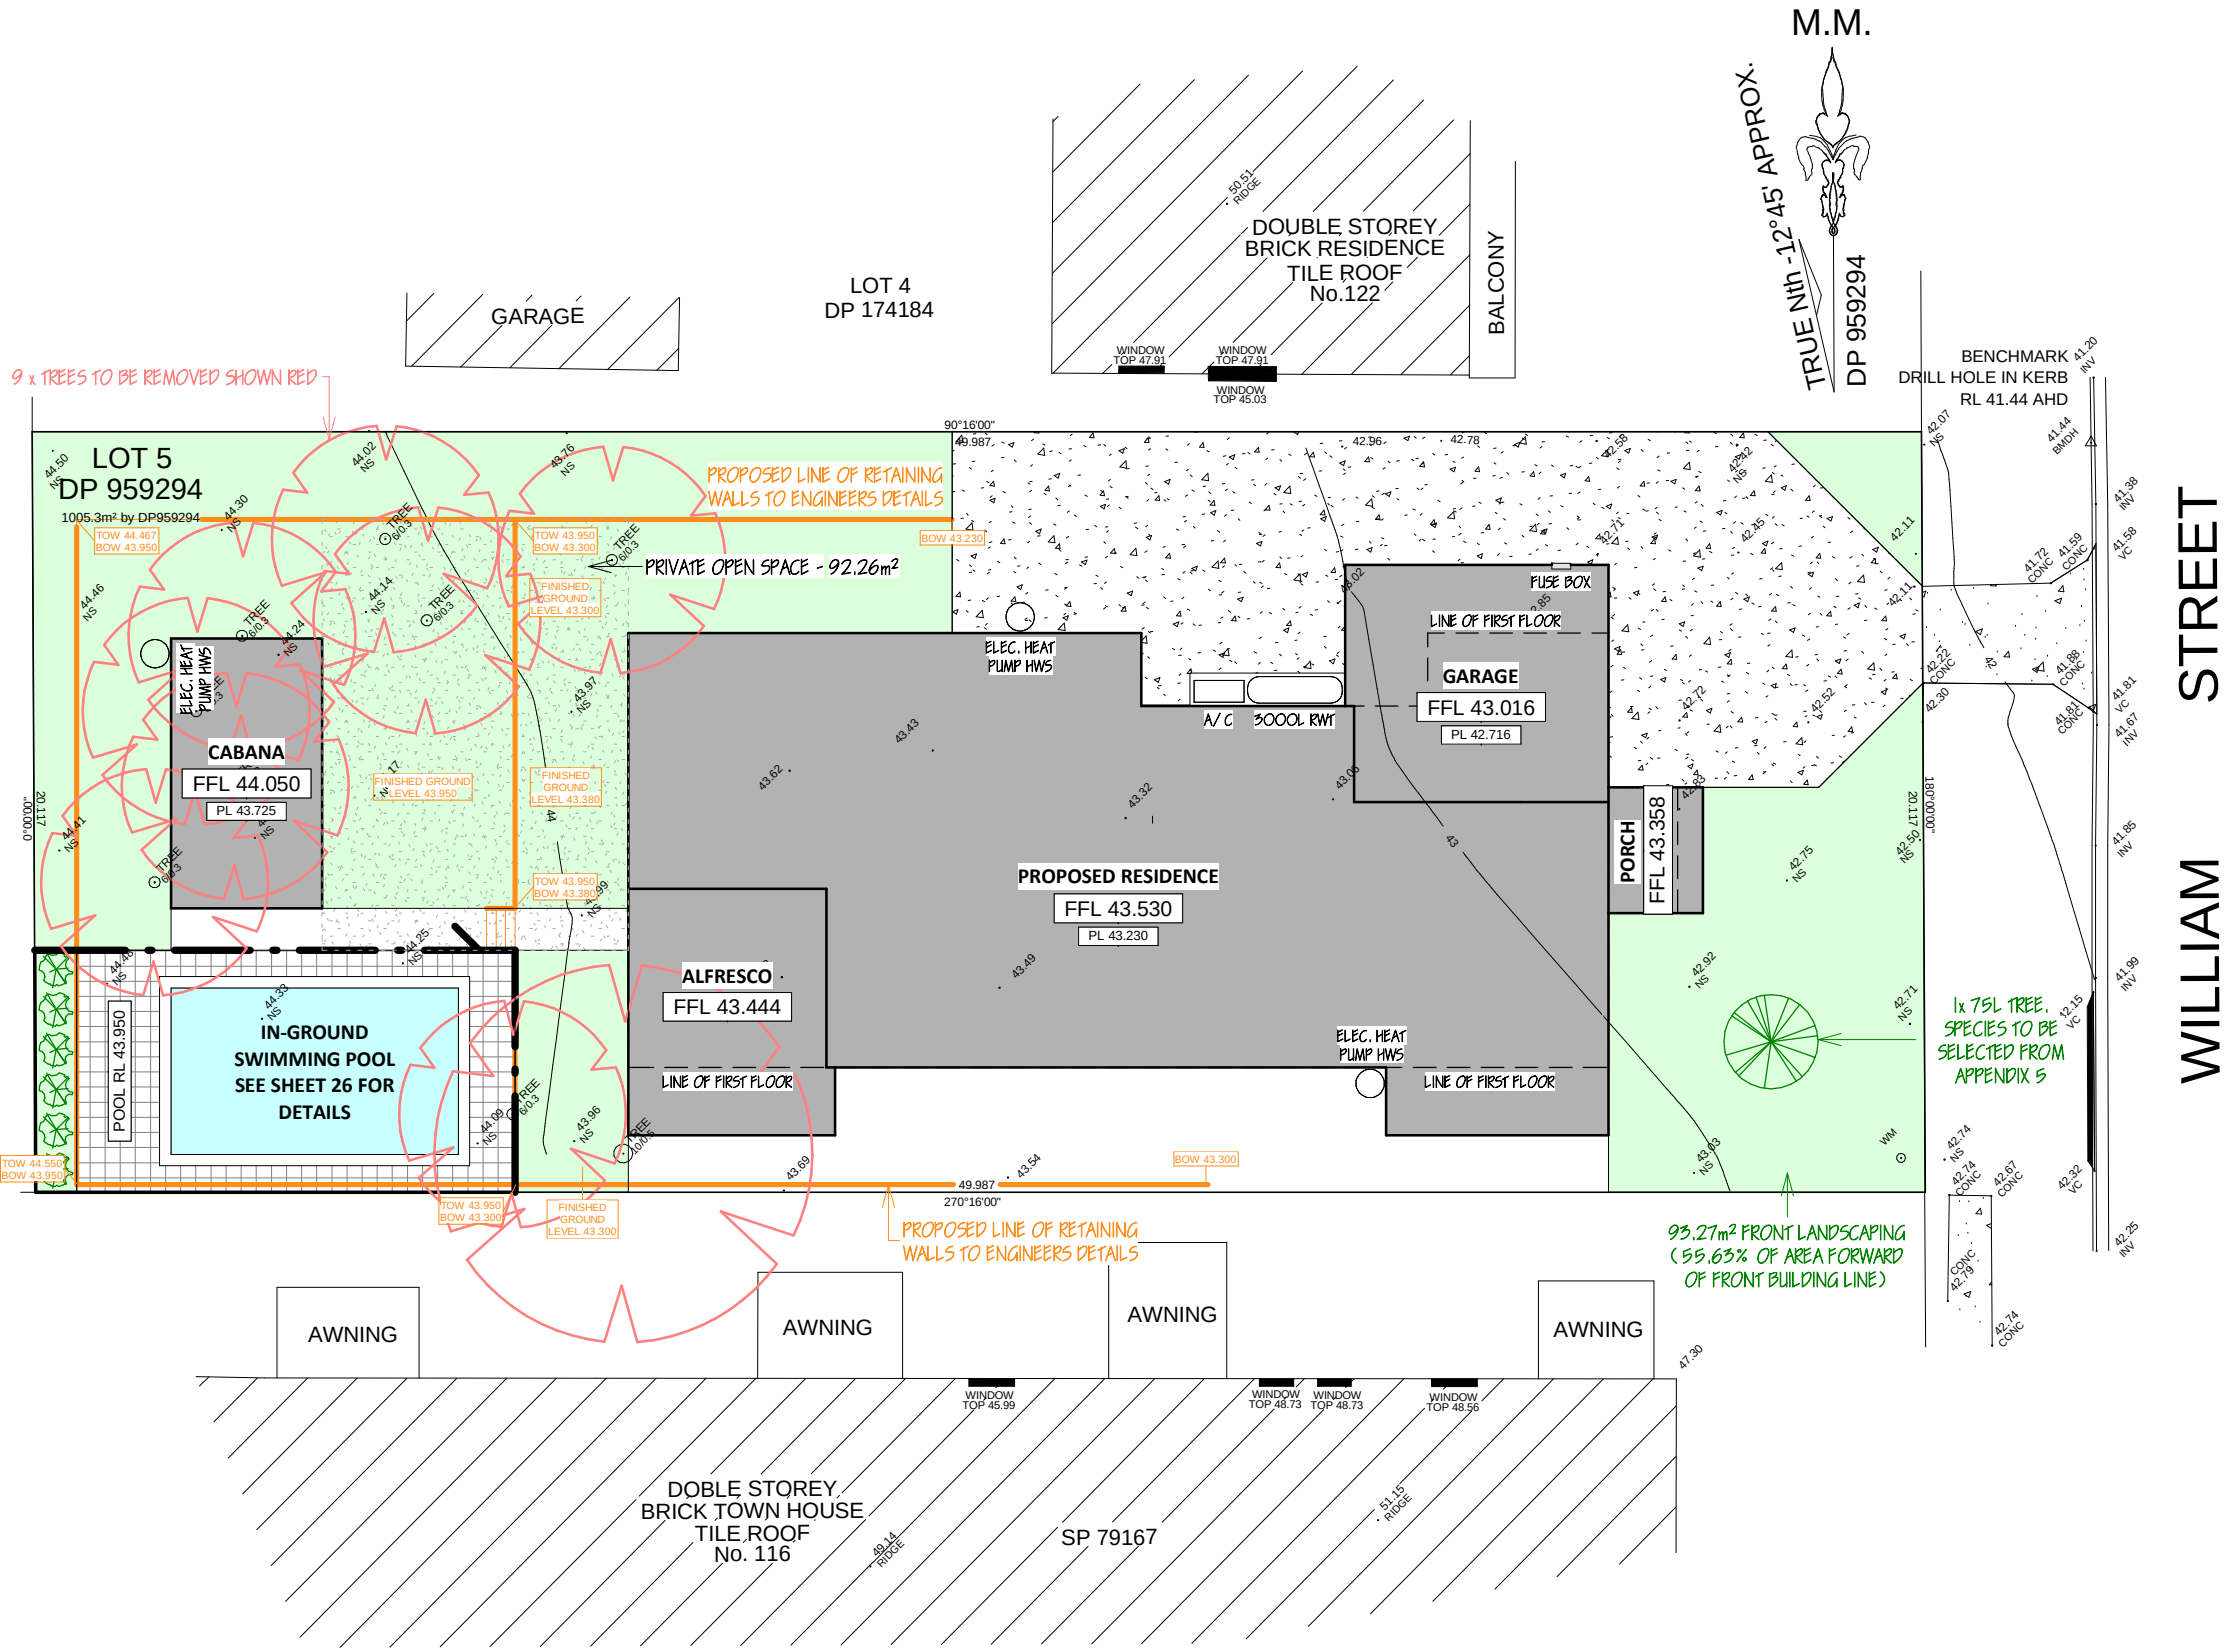


INDICATES EXTENT OF GROSS FLOOR AREA

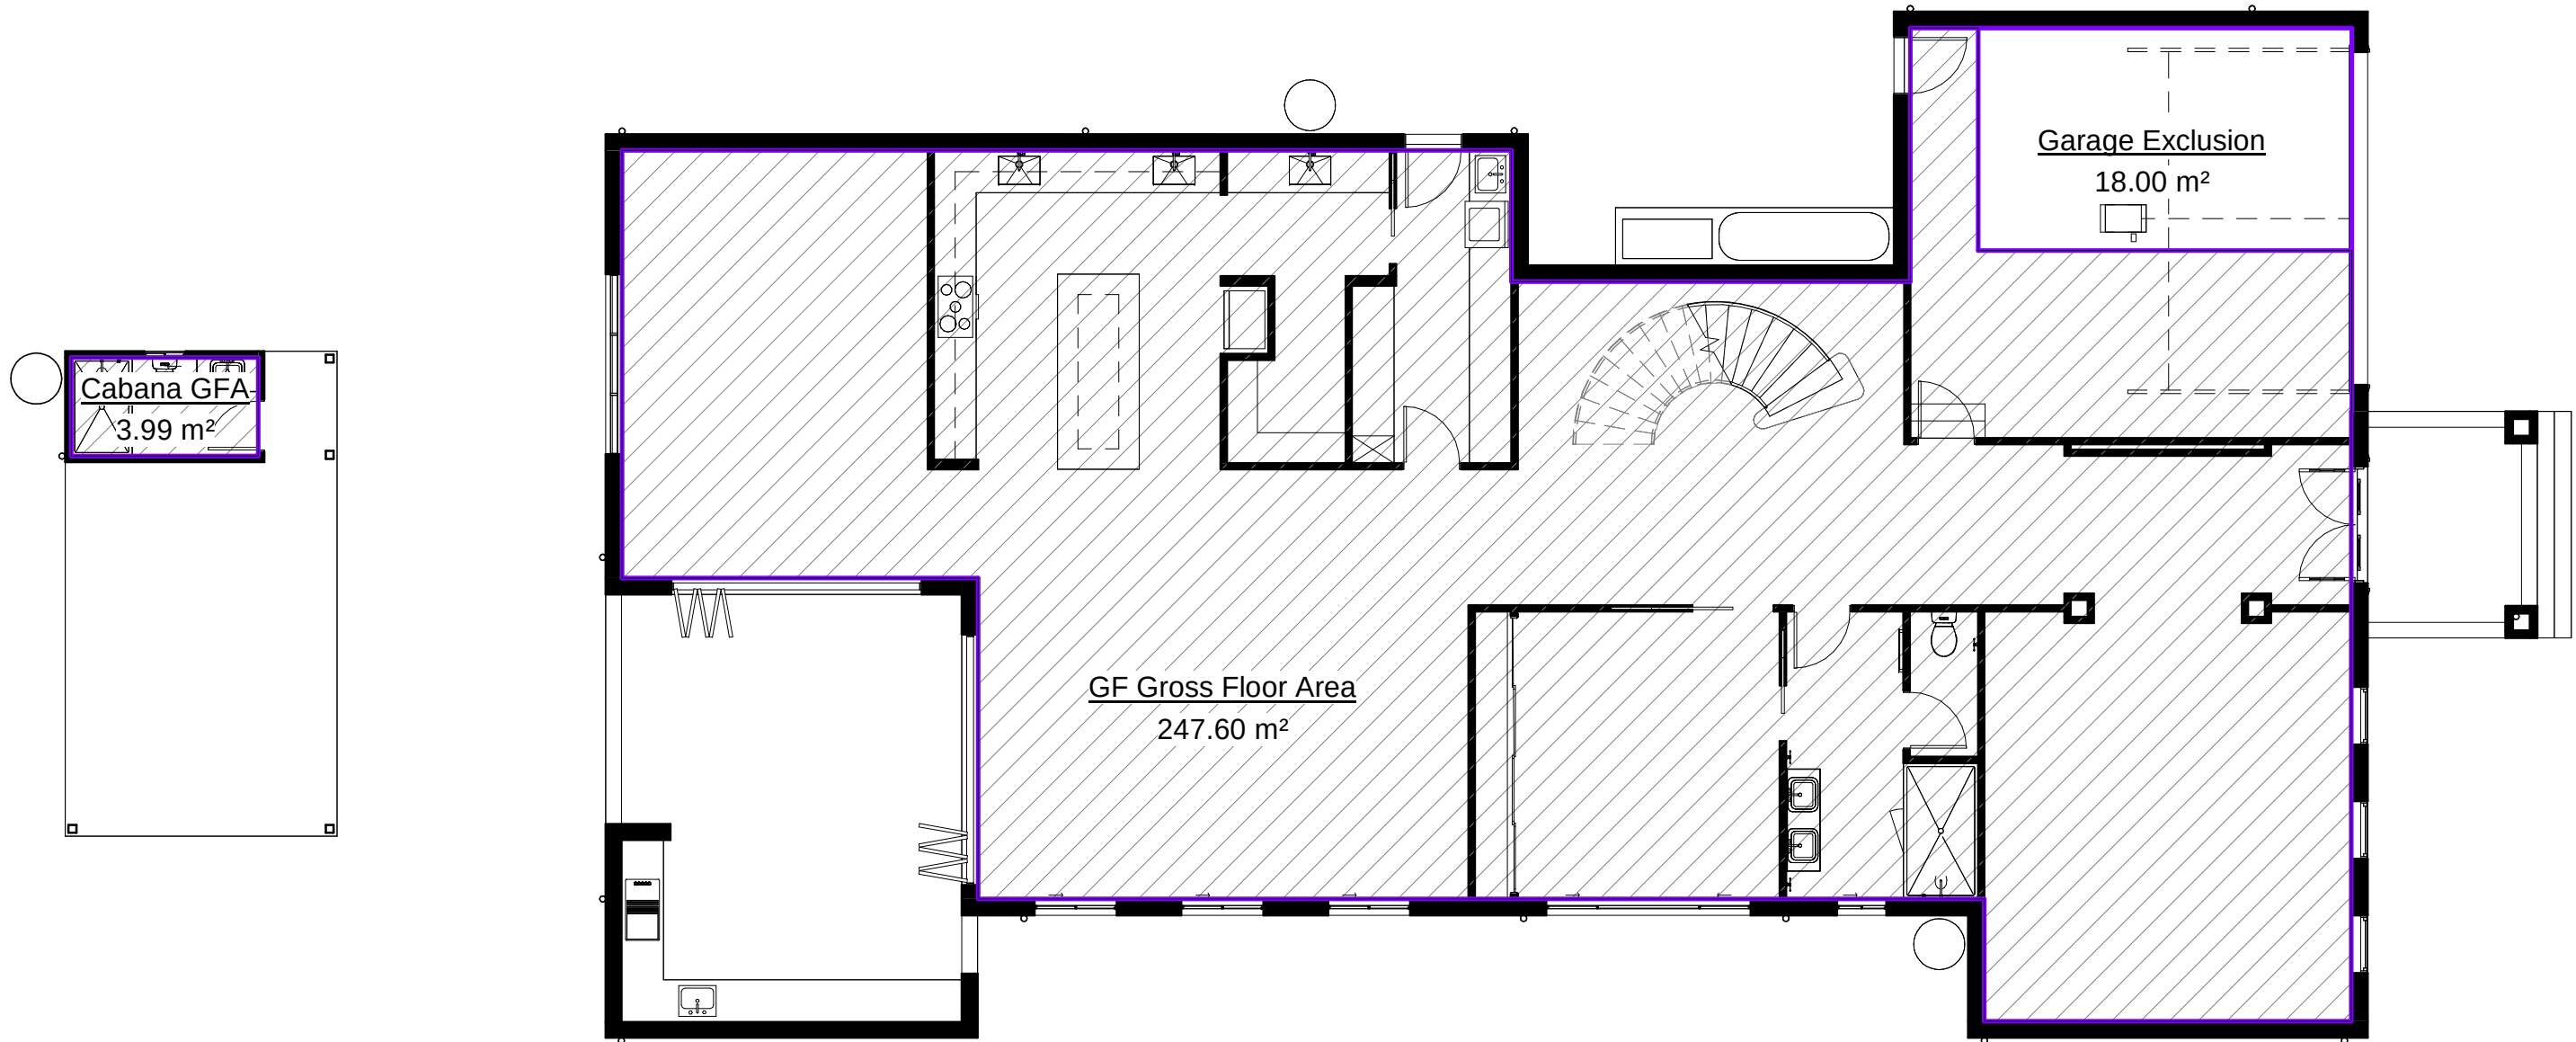

Disclaimer: Some items displayed or noted on these plans may be for indicative nominal placement or certification purposes only. The written words in any accompanying building tender will on all occasions take precedence to the plan. All internal room dimensions shown on any floor plan are to timber frame for construction purpose.

	ABN 67 250 466 867 Suite 7, Shop 11, 38 Exchange Parade Narellan NSW 2567 P: 0421 993 467 E: info@definitivedrafting.com.au W: www.definitivedrafting.com.au	This drawing and information thereon is the property of Vogue Homes and must not be loaned, partly copied, fully copied or used without the expressed permission in license or writing		License No. 115618C Unit 2/16 Weld Street Prestons NSW 2170 P: (02) 96079554 E: admin@vogue-homes.com.au W: www.vogue-homes.com.au	Hau Thi Bui & Toan Hoang Pham Lot 5 DP 959294 118 William St Condell Park 2200	Design Custom	Vogue Job No. 9013-22	Project Number DD-1451	DD-1451-18
						Facade Custom	LGA Canterbury Bankstown	Current Revision 3 26/09/23	GF Area Calculation Plan
						Inclusions Vogue	Approval Path DA	Date 18/03/22	Scale 1 : 100 @ A3


INDICATES EXTENT OF GROSS FLOOR AREA

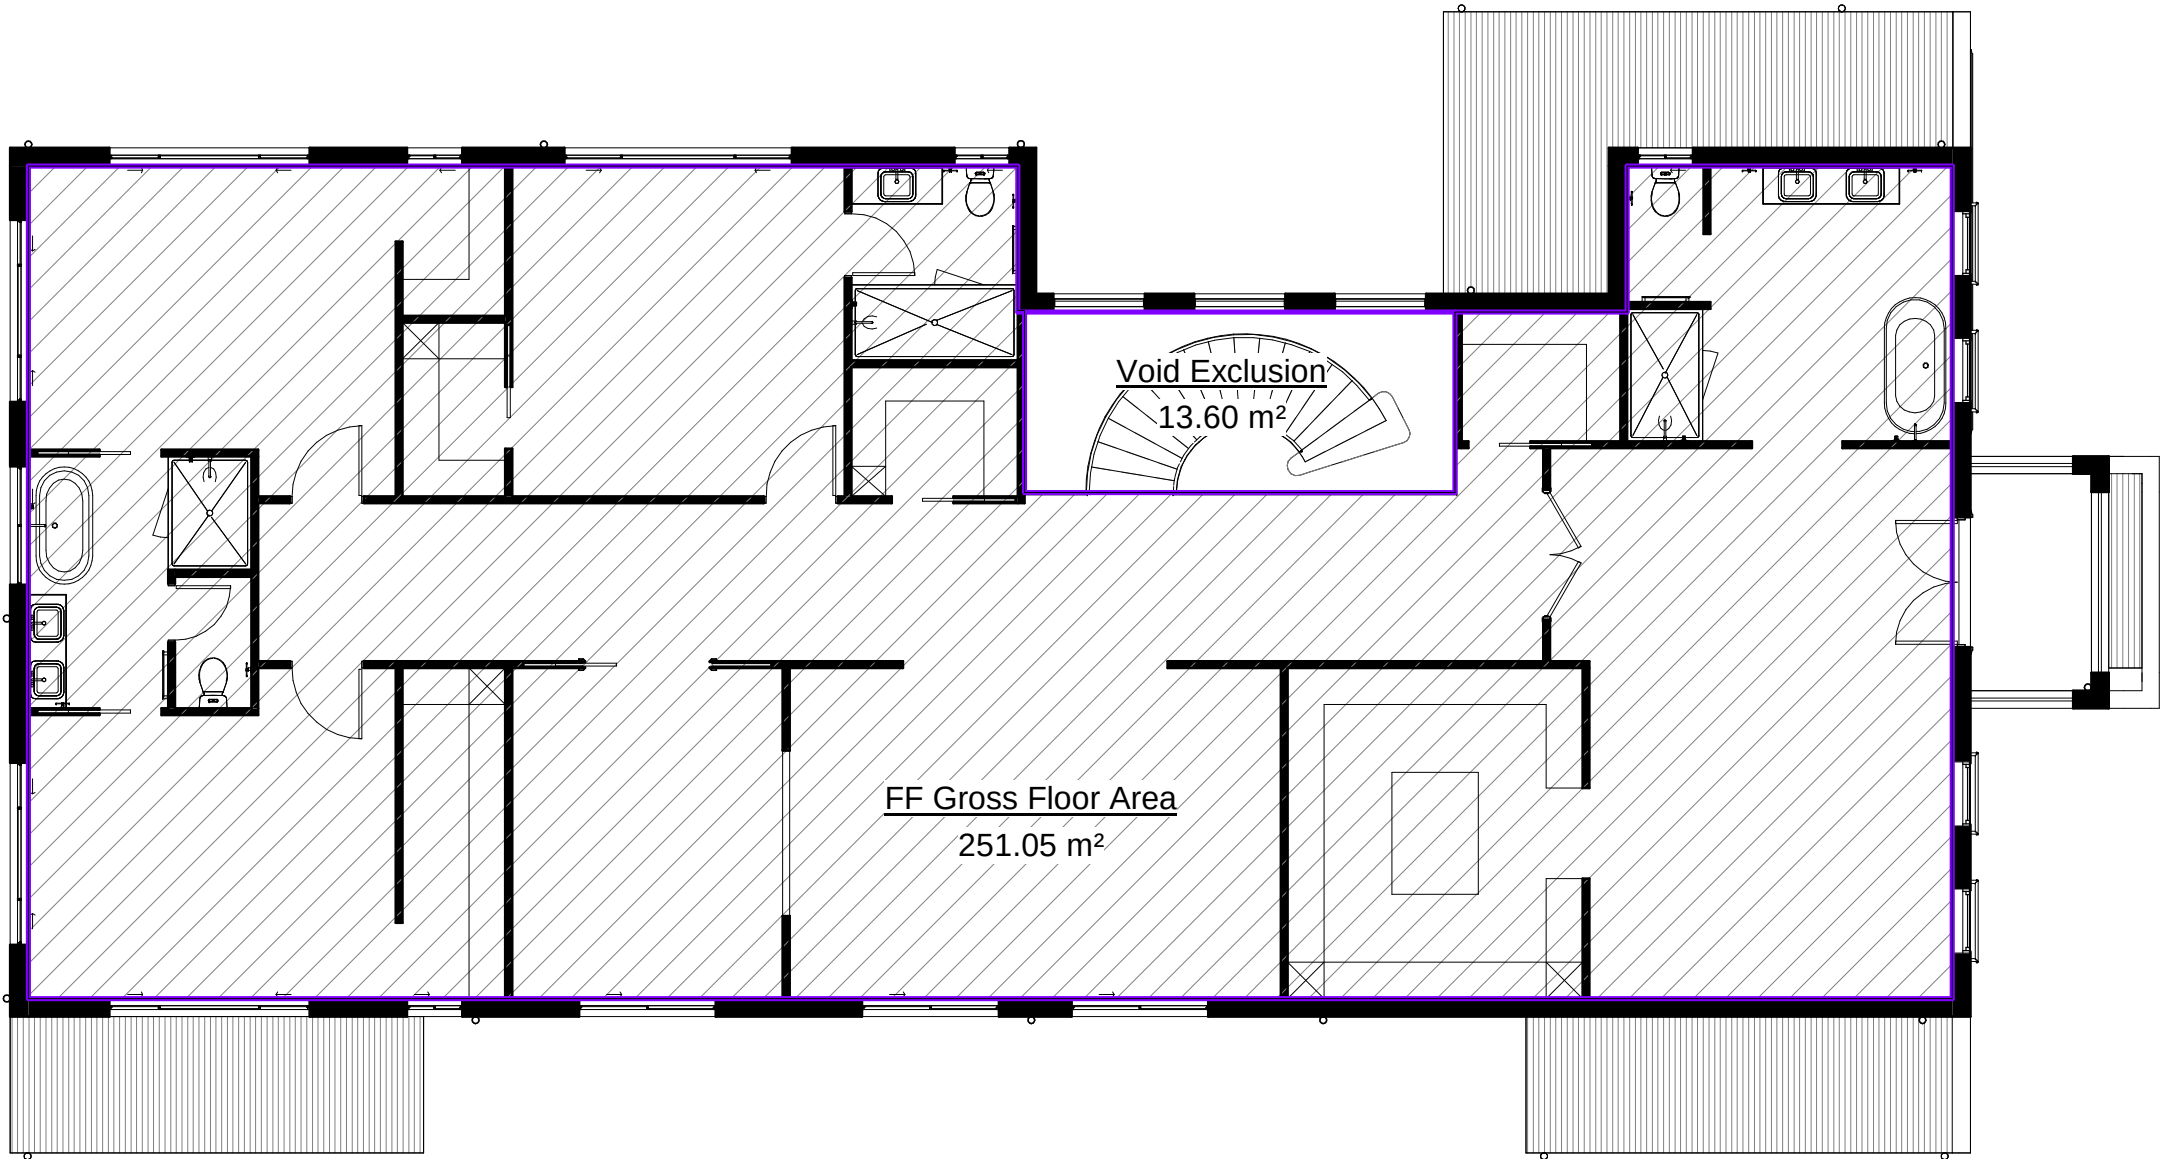


Disclaimer: Some items displayed or noted on these plans may be for indicative nominal placement or certification purposes only. The written words in any accompanying building tender will on all occasions take precedence to the plan. All internal room dimensions shown on any floor plan are to timber frame for construction purpose.

	ABN 67 250 466 867 Suite 7, Shop 11, 38 Exchange Parade Narellan NSW 2567 P: 0421 993 467 E: info@definitivedrafting.com.au W: www.definitivedrafting.com.au	This drawing and information thereon is the property of Vogue Homes and must not be loaned, partly copied, fully copied or used without the expressed permission in license or writing		License No. 115618C Unit 2/16 Weld Street Prestons NSW 2170 P: (02) 96079554 E: admin@vogue-homes.com.au W: www.vogue-homes.com.au	Hau Thi Bui & Toan Hoang Pham Lot 5 DP 959294 118 William St Condell Park 2200	Design Custom	Vogue Job No. 9013-22	Project Number DD-1451	DD-1451-19
						Facade Custom	LGA Canterbury Bankstown	Current Revision 3 26/09/23	FF Area Calculation Plan
						Inclusions Vogue	Approval Path DA	Date 18/03/22	Scale 1 : 100 @ A3


Electrical Legend			
Symbol	Description	Height	Qty
▲	Single GPO	300	
▲▲	Double GPO	300	
△	Single GPO	1050	
△△	Double GPO	1050	
△	Single GPO	1300	
△△	Double GPO	1300	
△	Single GPO	1800	
△△	Double GPO	1800	
△	Single GPO	Ceiling	
⊠	Double GPO - water proof		
○	Ceiling light - oyster		
◎	Ceiling light - down light		
▭	Ceiling light - batten		
▭	Ceiling light - fluorescent		
□	Stair light		
◐	Wall mounted light	1800	
▽	Single flood light		
▽▽	Double flood light		
▣	Heat lamp fan (2 in 1)		
▣	Heat lamp fan (4 in 1)		
⊕	Exhaust fan		1
Ⓢ	Smoke alarm		1
Ⓜ	Heat alarm		
✕	Ceiling fan		
Ⓟ	Telephone point		
ⓉⓋ	Television point		
ⓓ	Data point		
Ⓢ	Intercom		
\$	Light switch	1100	
\$ _x	Light switch (multi-bank)	1100	
Smoke alarms to be installed in accordance with clauses 9.5.1, 9.5.2 & 9.5.4			
Exhaust fans to a kitchen or wet area rooms without natural ventilation must meet the flow rates detailed in clause 10.8.2(1) and ducting to outdoor air in accordance with clause 10.8.2(2)			
Wet areas without natural ventilation, must include a run-on timer on the exhaust fan. The fan must be interlocked to the light switch and run-on for 10 minutes after the light is turned off, in accordance with clause 10.8.2(4)			
Template only. Final layout & heights to be confirmed by builder and/or electrical contractor. Heights referenced in millimetres (mm) above FFL. Locations shown on plans may vary to achieve compliance with the building code.			

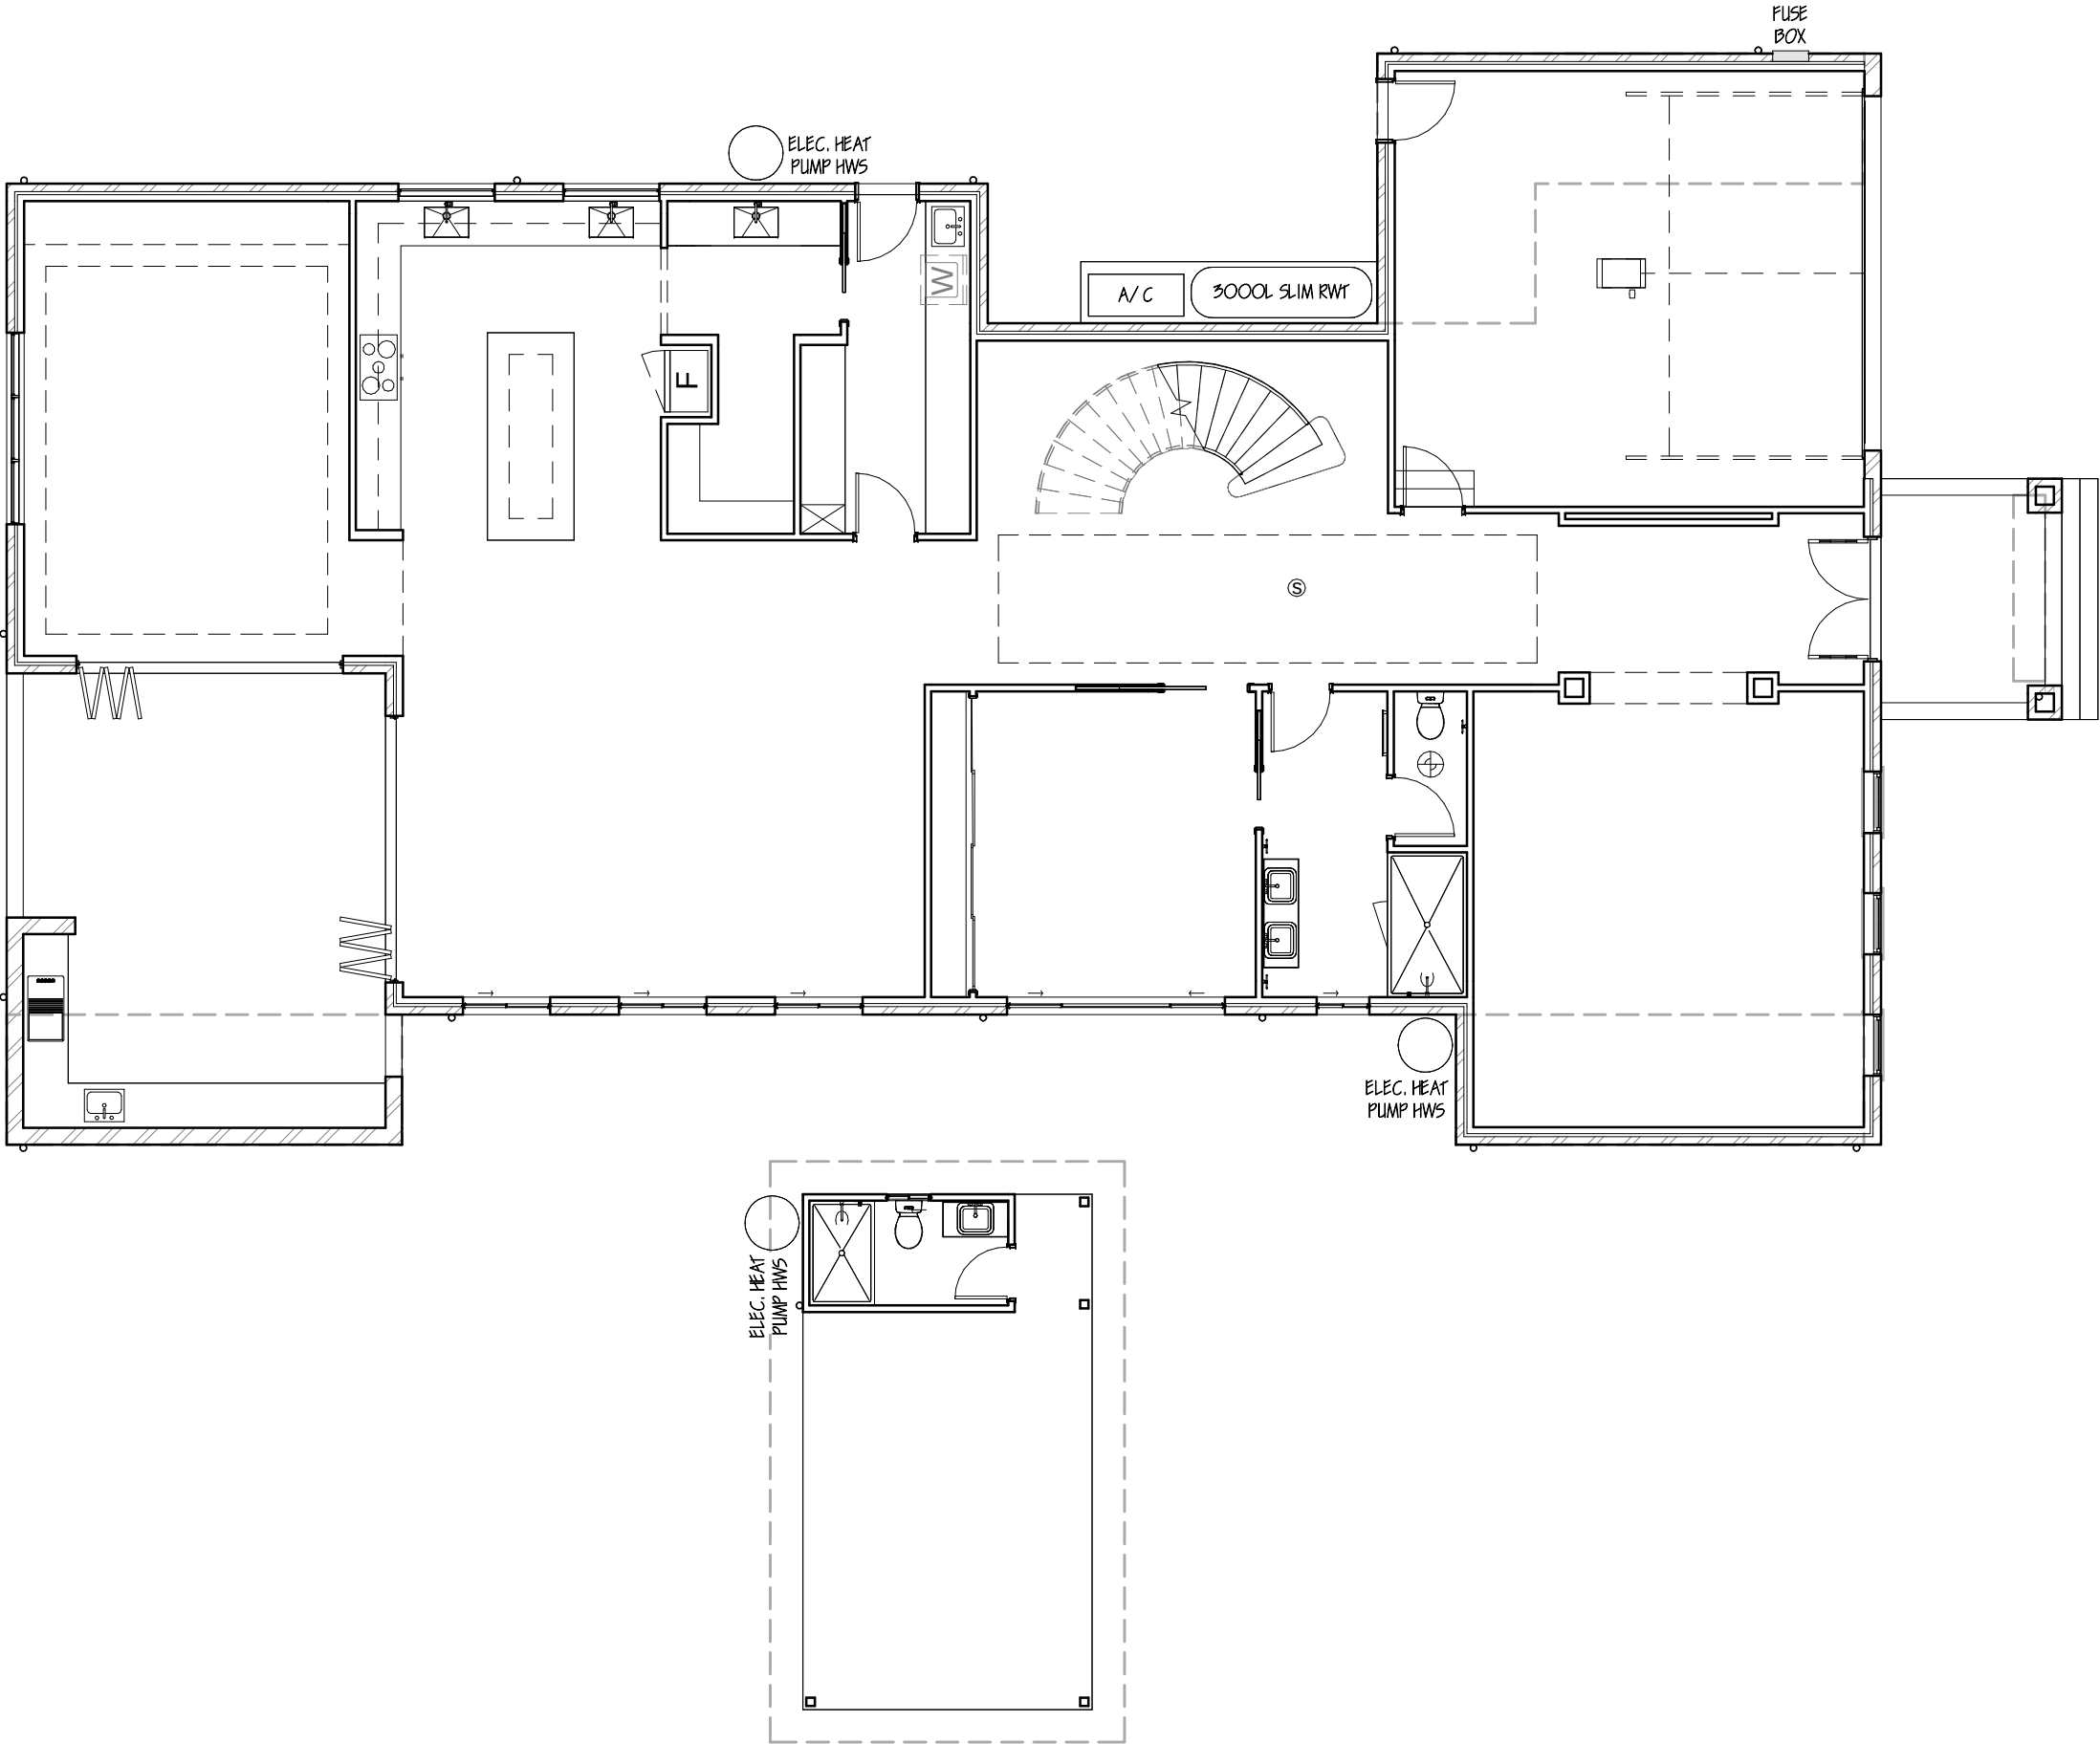

Disclaimer: Some items displayed or noted on these plans may be for indicative nominal placement or certification purposes only. The written words in any accompanying building tender will on all occasions take precedence to the plan. All internal room dimensions shown on any floor plan are to timber frame for construction purpose.

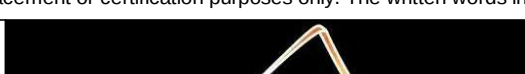
 definitivedrafting	ABN 67 250 466 867 Suite 7, Shop 11, 38 Exchange Parade Narellan NSW 2567 P: 0421 993 467 E: info@definitivedrafting.com.au W: www.definitivedrafting.com.au	This drawing and information theron is the property of Vogue Homes and must not be loaned, partly copied, fully copied or used without the expressed permission in license or writing	 DESIGN - STYLE - ELEGANCE	License No. 115618C Unit 2/16 Weld Street Prestons NSW 2170 P: (02) 96079554 E: admin@vogue-homes.com.au W: www.vogue-homes.com.au	Hau Thi Bui & Toan Hoang Pham Lot 5 DP 959294 118 William St Condell Park 2200	Design Custom	Vogue Job No. 9013-22	Project Number DD-1451	DD-1451-20
						Facade Custom	LGA Canterbury Bankstown	Current Revision 3 26/09/23	GF Electrical Plan
							Inclusions Vogue	Approval Path DA	Date 18/03/22

Electrical Legend			
Symbol	Description	Height	Qty
▲	Single GPO	300	
▲▲	Double GPO	300	
△	Single GPO	1050	
△△	Double GPO	1050	
△	Single GPO	1300	
△△	Double GPO	1300	
△	Single GPO	1800	
△△	Double GPO	1800	
△	Single GPO	Ceiling	
⊠	Double GPO - water proof		
○	Ceiling light - oyster		
◎	Ceiling light - down light		
▭	Ceiling light - batten		
▭	Ceiling light - fluorescent		
□	Stair light		
◐	Wall mounted light	1800	
▽	Single flood light		
▽▽	Double flood light		
▣	Heat lamp fan (2 in 1)		
▣	Heat lamp fan (4 in 1)		
⊕	Exhaust fan		1
Ⓢ	Smoke alarm		2
Ⓜ	Heat alarm		
✕	Ceiling fan		
Ⓟ	Telephone point		
Ⓣ	Television point		
Ⓣ	Data point		
Ⓢ	Intercom		
\$	Light switch	1100	
\$ _x	Light switch (multi-bank)	1100	
Smoke alarms to be installed in accordance with clauses 9.5.1, 9.5.2 & 9.5.4			
Exhaust fans to a kitchen or wet area rooms without natural ventilation must meet the flow rates detailed in clause 10.8.2(1) and ducting to outdoor air in accordance with clause 10.8.2(2)			
Wet areas without natural ventilation, must include a run-on timer on the exhaust fan. The fan must be interlocked to the light switch and run-on for 10 minutes after the light is turned off, in accordance with clause 10.8.2(4)			
Template only. Final layout & heights to be confirmed by builder and/or electrical contractor. Heights referenced in millimetres (mm) above FFL. Locations shown on plans may vary to achieve compliance with the building code.			

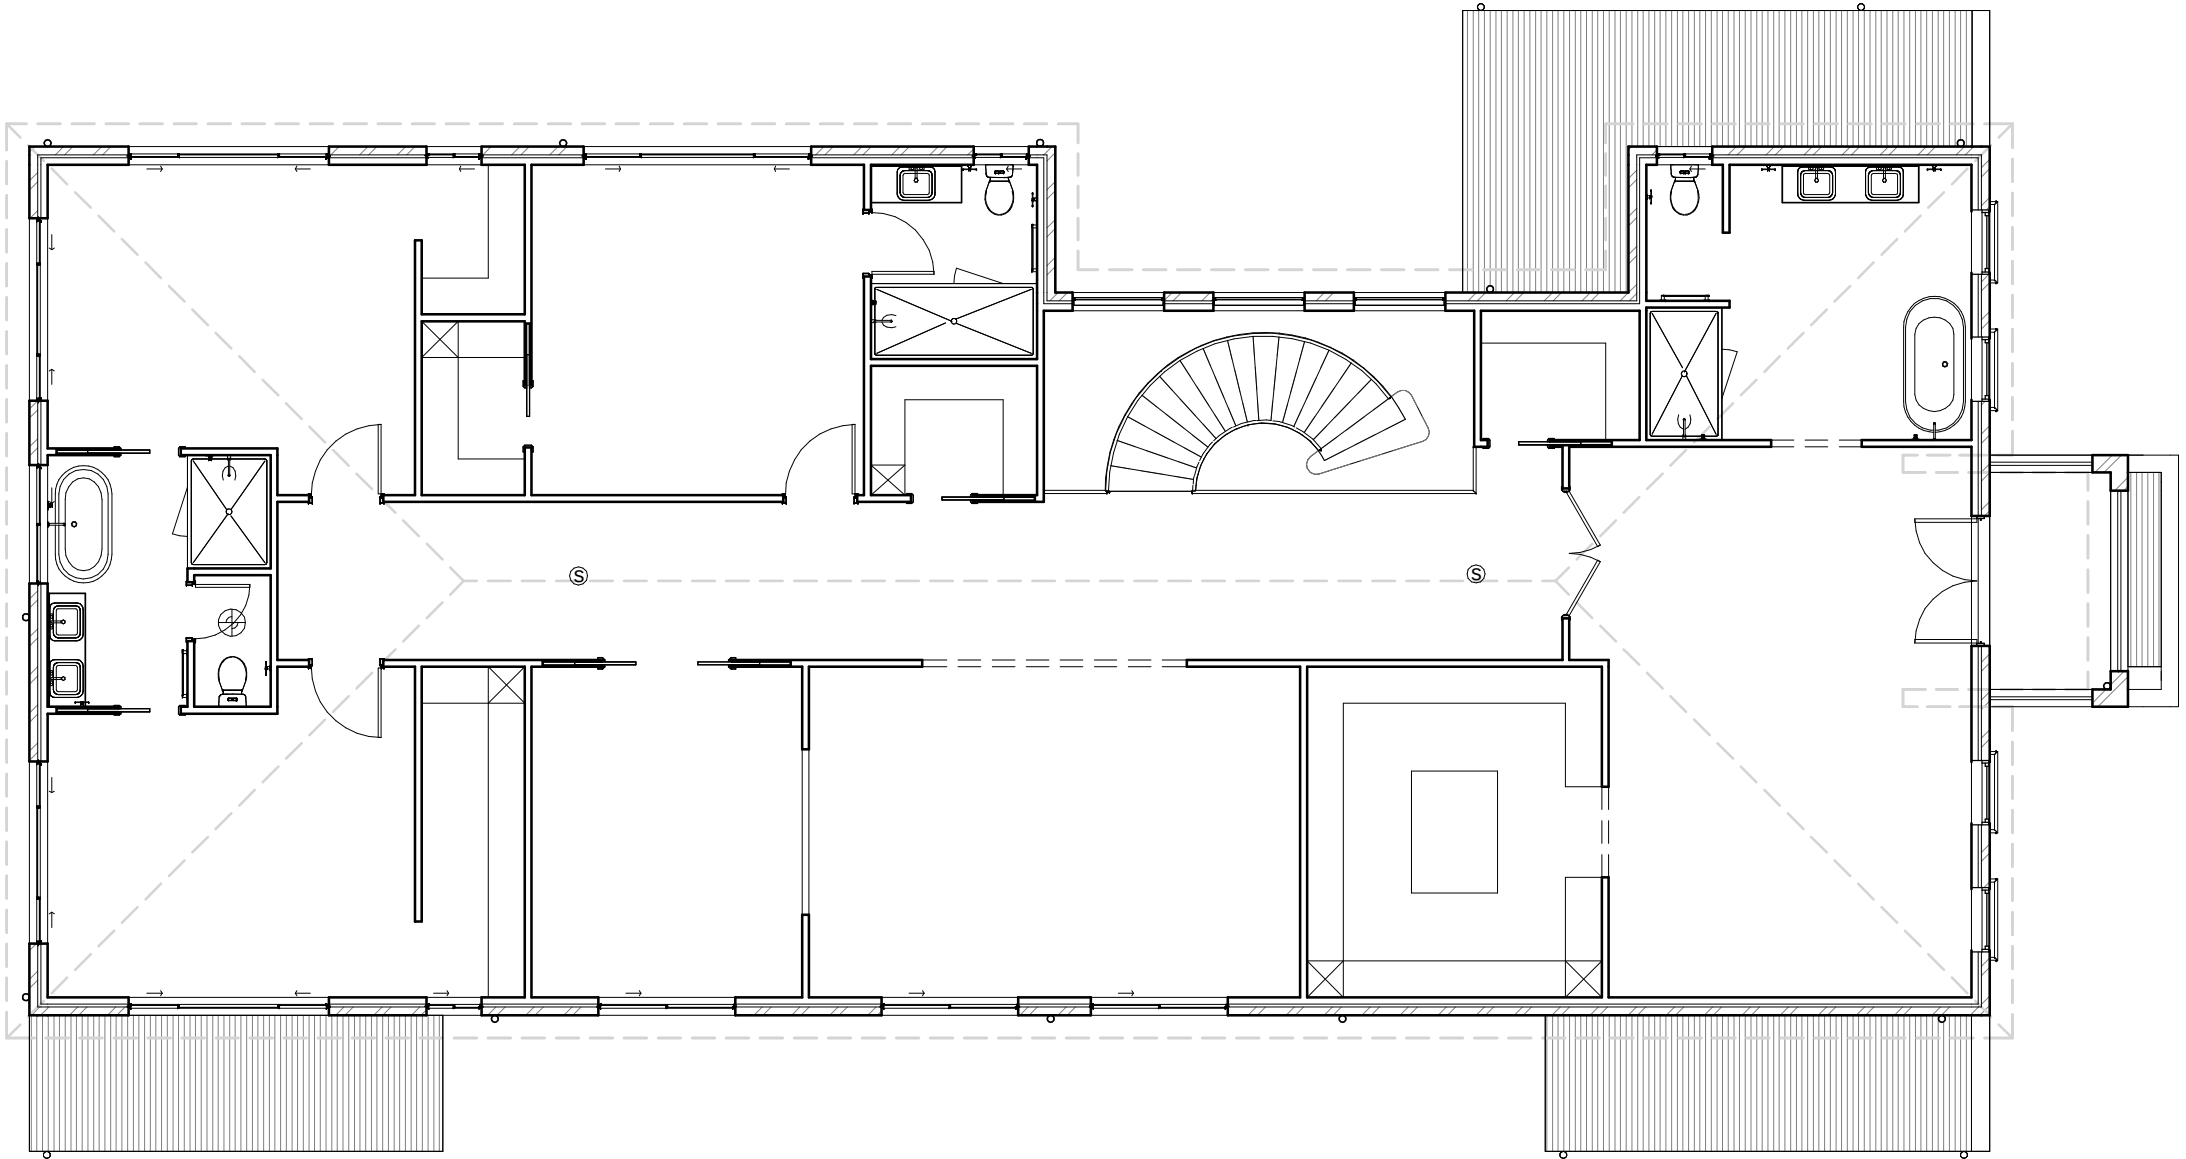


Disclaimer: Some items displayed or noted on these plans may be for indicative nominal placement or certification purposes only. The written words in any accompanying building tender will on all occasions take precedence to the plan. All internal room dimensions shown on any floor plan are to timber frame for construction purpose.

 definitivedrafting	ABN 67 250 466 867 Suite 7, Shop 11, 38 Exchange Parade Narellan NSW 2567 P: 0421 993 467 E: info@definitivedrafting.com.au W: www.definitivedrafting.com.au	This drawing and information theron is the property of Vogue Homes and must not be loaned, partly copied, fully copied or used without the expressed permission in license or writing	 DESIGN - STYLE - ELEGANCE	License No. 115618C Unit 2/16 Weld Street Prestons NSW 2170 P: (02) 96079554 E: admin@vogue-homes.com.au W: www.vogue-homes.com.au	Hau Thi Bui & Toan Hoang Pham Lot 5 DP 959294 118 William St Condell Park 2200	Design Custom	Vogue Job No. 9013-22	Project Number DD-1451	DD-1451-21
	Facade Custom	LGA Canterbury Bankstown		Current Revision 3 26/09/23		FF Electrical Plan			
	Inclusions Vogue	Approval Path DA		Date 18/03/22		Scale 1 : 100 @ A3			

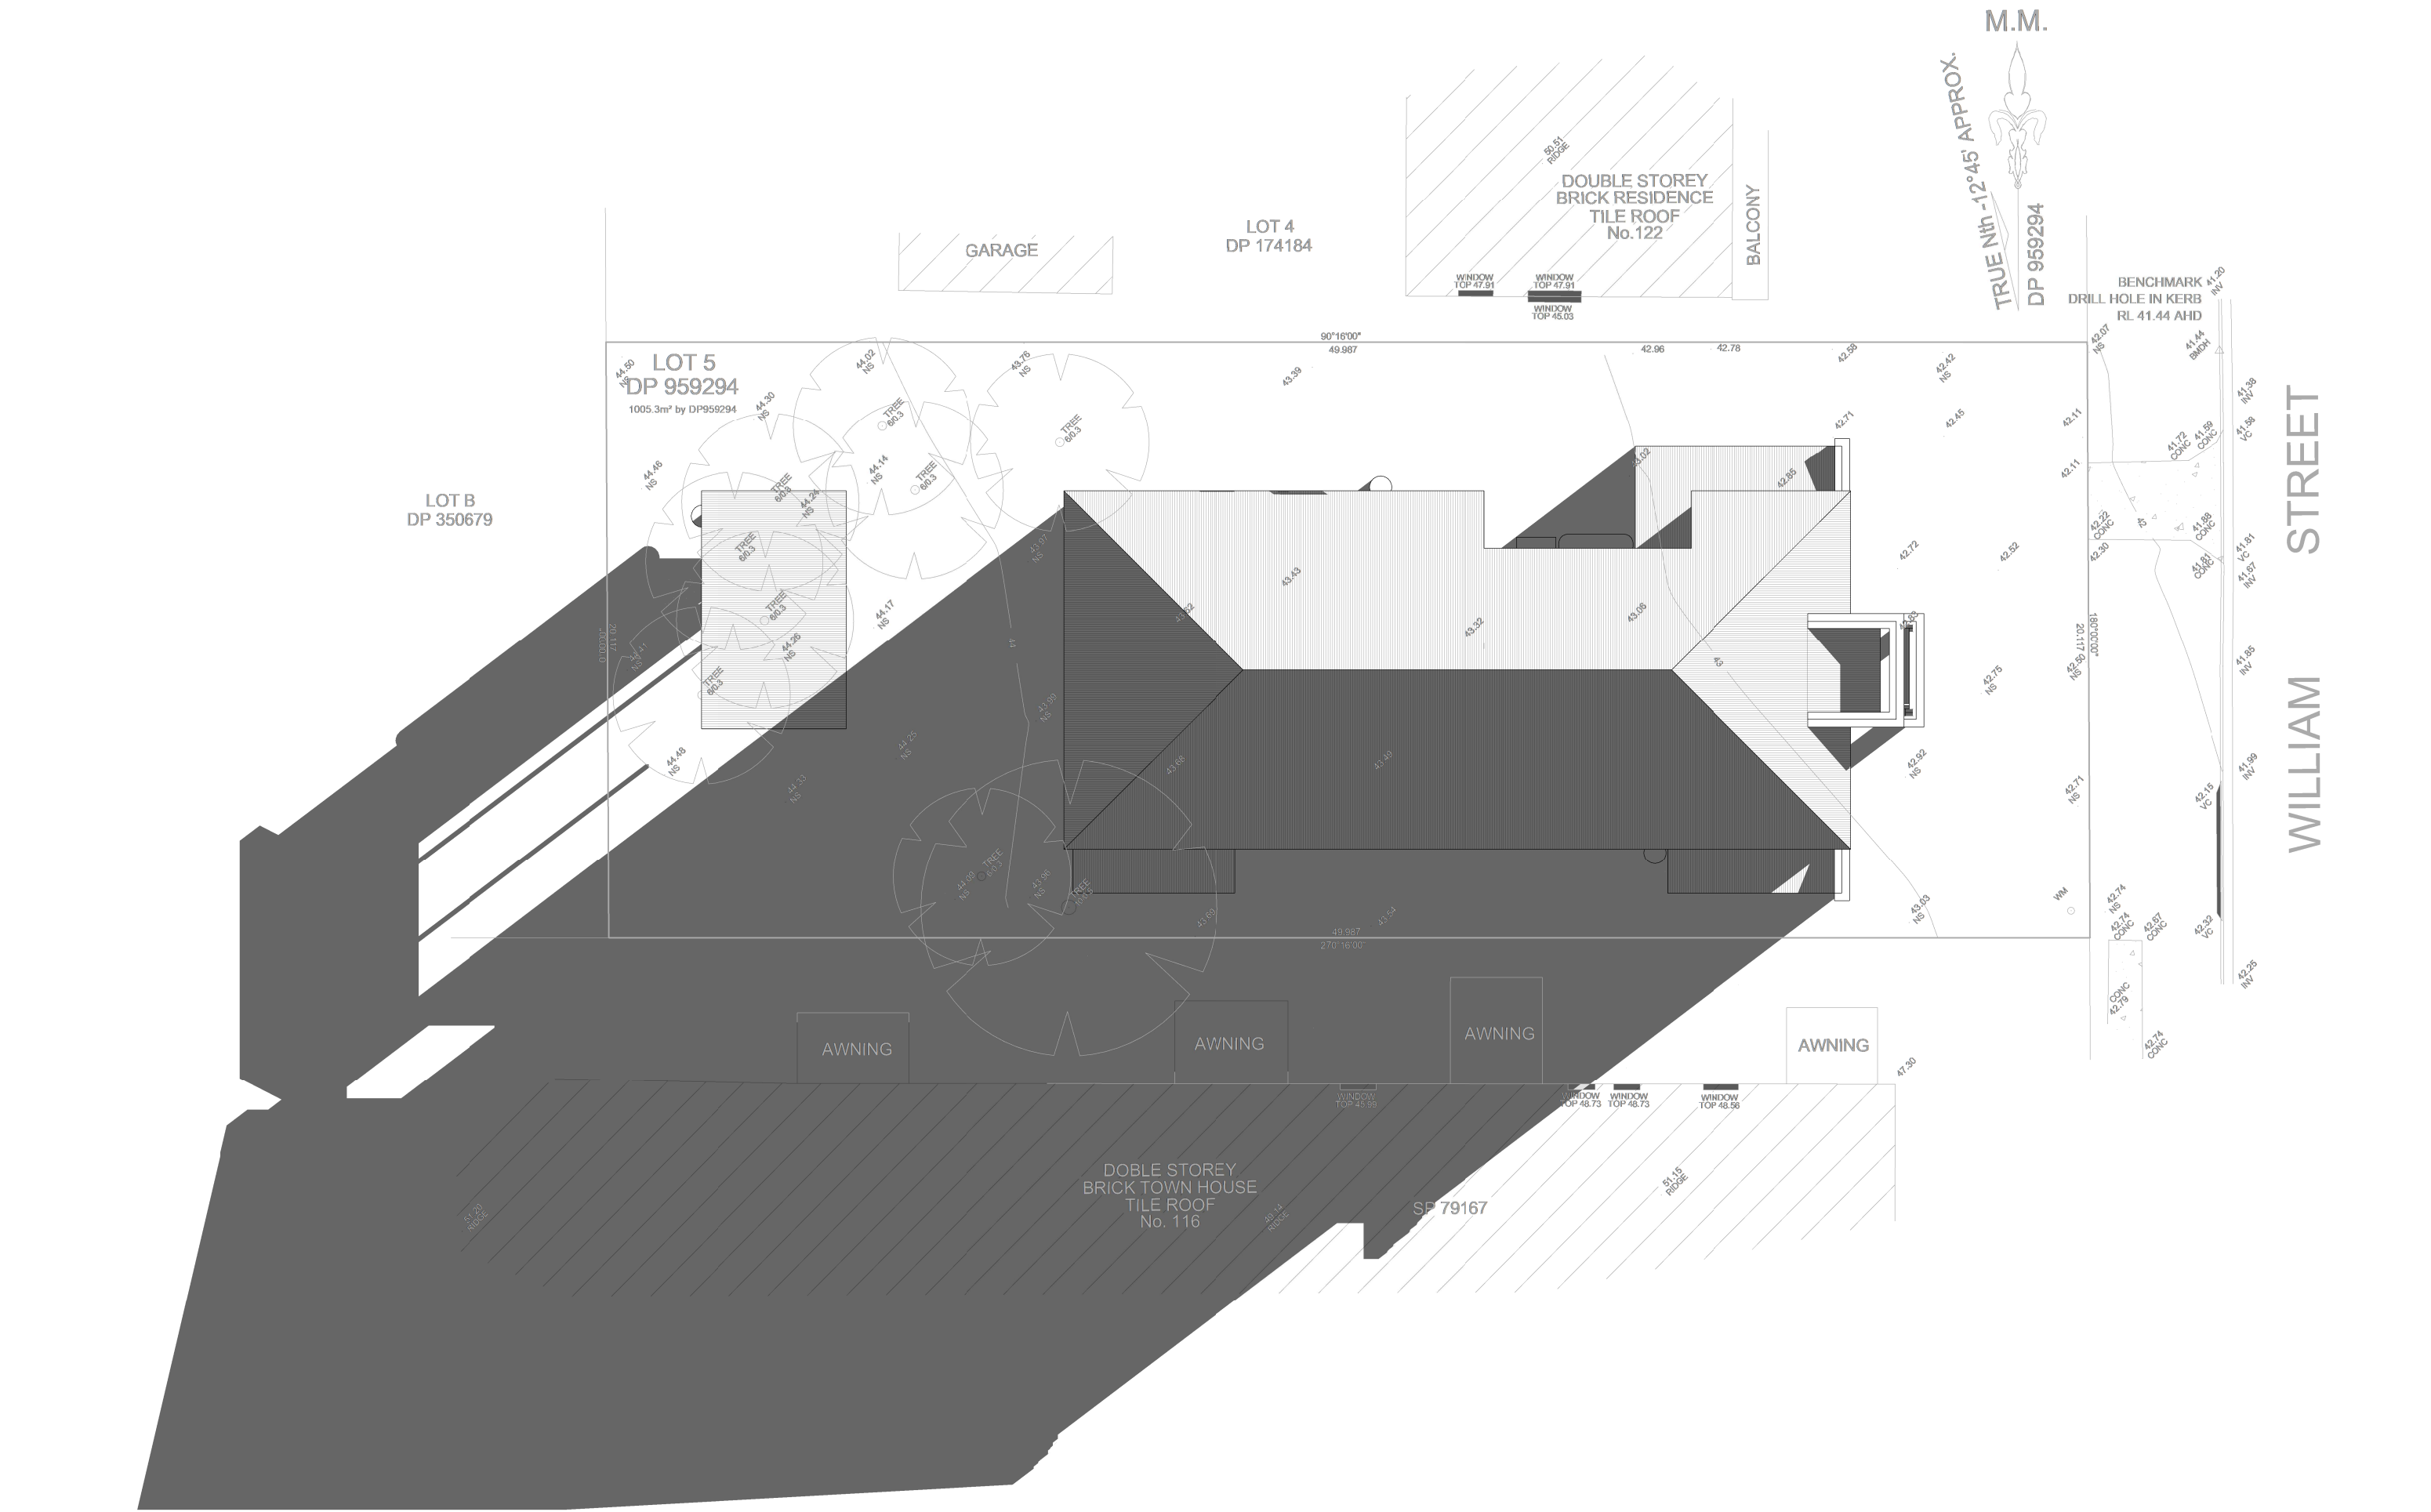


Disclaimer: Some items displayed or noted on these plans may be for indicative nominal placement or certification purposes only. The written words in any accompanying building tender will on all occasions take precedence to the plan. All internal room dimensions shown on any floor plan are to timber frame for construction purpose.

	ABN 67 250 466 867 Suite 7, Shop 11, 38 Exchange Parade Narellan NSW 2567 P: 0421 993 467 E: info@definitivedrafting.com.au W: www.definitivedrafting.com.au	This drawing and information thereon is the property of Vogue Homes and must not be loaned, partly copied, fully copied or used without the expressed permission in license or writing		License No. 115618C Unit 2/16 Weld Street Prestons NSW 2170 P: (02) 96079554 E: admin@vogue-homes.com.au W: www.vogue-homes.com.au	Hau Thi Bui & Toan Hoang Pham Lot 5 DP 959294 118 William St Condell Park 2200	Design Custom	Vogue Job No. 9013-22	Project Number DD-1451	DD-1451-22
						Facade Custom	LGA Canterbury Bankstown	Current Revision 3 26/09/23	Shadow Diagram - June 21 8am
						Inclusions Vogue	Approval Path DA	Date 18/03/22	Scale 1 : 200 @ A3

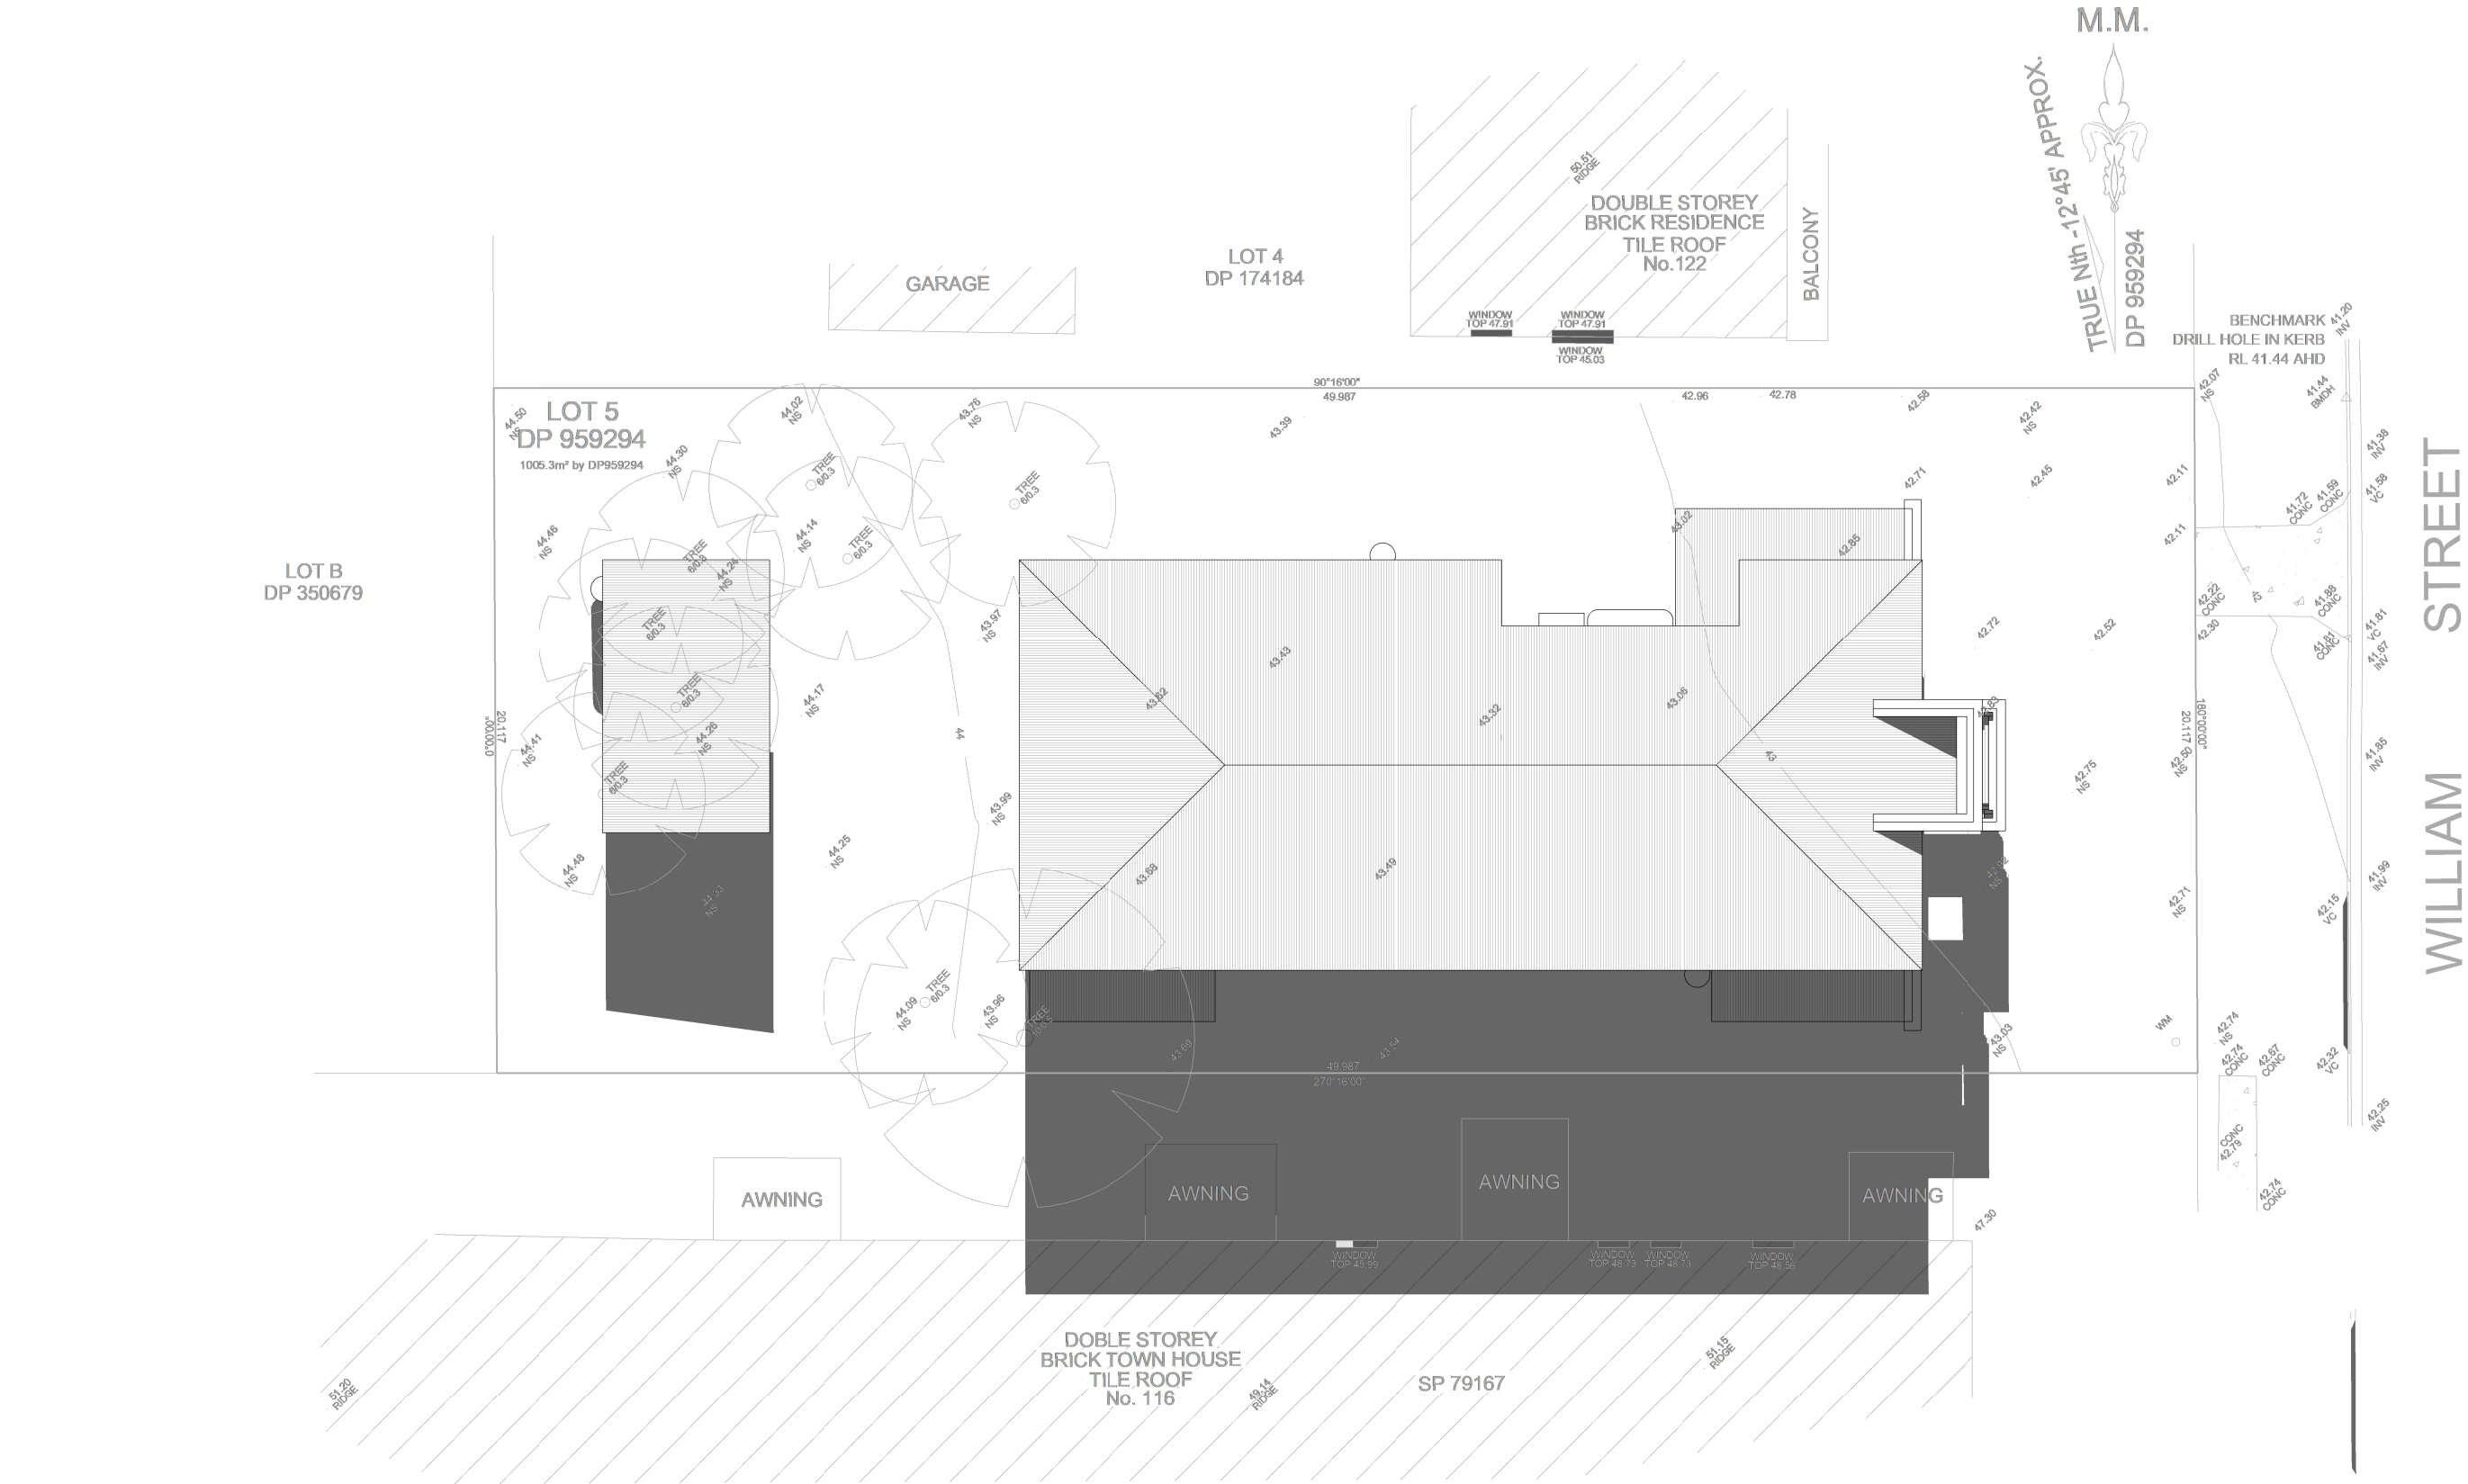


Disclaimer: Some items displayed or noted on these plans may be for indicative nominal placement or certification purposes only. The written words in any accompanying building tender will on all occasions take precedence to the plan. All internal room dimensions shown on any floor plan are to timber frame for construction purpose.									
	ABN 67 250 466 867 Suite 7, Shop 11, 38 Exchange Parade Narellan NSW 2567 P: 0421 993 467 E: info@definitivedrafting.com.au W: www.definitivedrafting.com.au	This drawing and information thereon is the property of Vogue Homes and must not be loaned, partly copied, fully copied or used without the expressed permission in license or writing		License No. 115618C Unit 2/16 Weld Street Prestons NSW 2170 P: (02) 96079554 E: admin@vogue-homes.com.au W: www.vogue-homes.com.au	Hau Thi Bui & Toan Hoang Pham Lot 5 DP 959294 118 William St Condell Park 2200	Design Custom	Vogue Job No. 9013-22	Project Number DD-1451	DD-1451-23
						Facade Custom	LGA Canterbury Bankstown	Current Revision 3 26/09/23	Shadow Diagram - June 21 12pm
						Inclusions Vogue	Approval Path DA	Date 18/03/22	Scale 1 : 200 @ A3

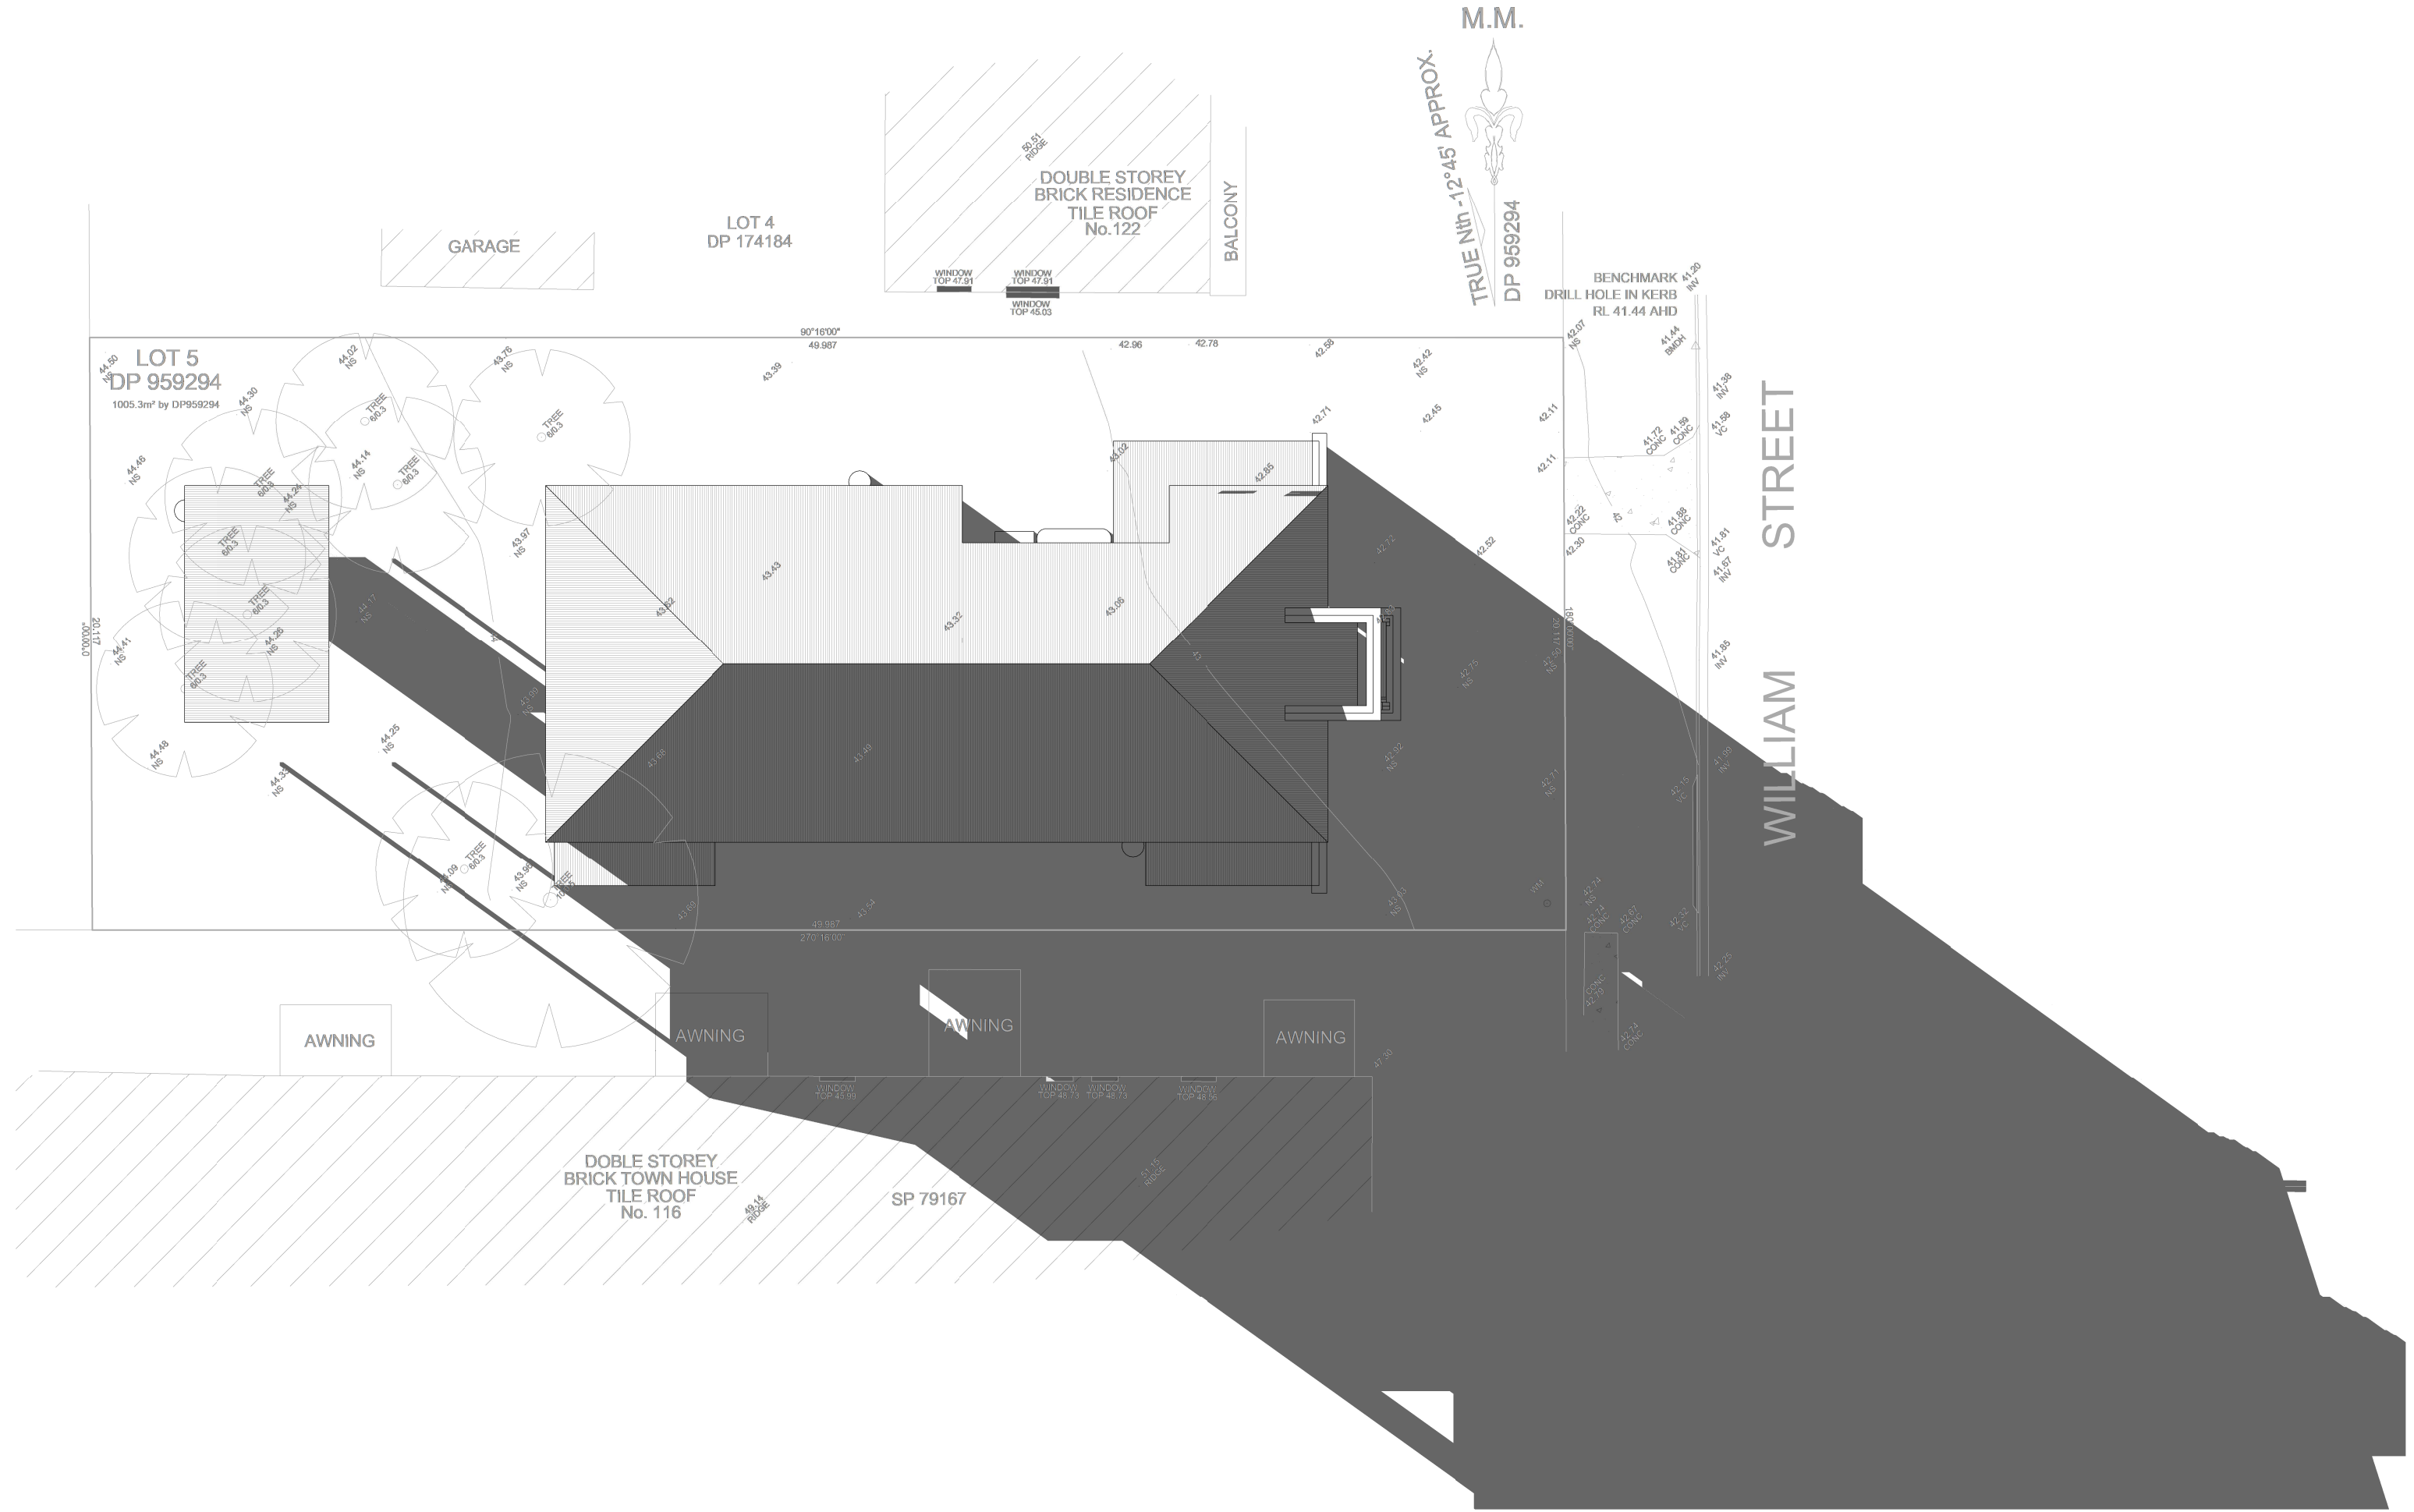

Disclaimer: Some items displayed or noted on these plans may be for indicative nominal placement or certification purposes only. The written words in any accompanying building tender will on all occasions take precedence to the plan. All internal room dimensions shown on any floor plan are to timber frame for construction purpose.


	ABN 67 250 466 867 Suite 7, Shop 11, 38 Exchange Parade Narellan NSW 2567 P: 0421 993 467 E: info@definitivedrafting.com.au W: www.definitivedrafting.com.au	This drawing and information theron is the property of Vogue Homes and must not be loaned, partly copied, fully copied or used without the expressed permission in license or writing		License No. 115618C Unit 2/16 Weld Street Prestons NSW 2170 P: (02) 96079554 E: admin@vogue-homes.com.au W: www.vogue-homes.com.au	Hau Thi Bui & Toan Hoang Pham Lot 5 DP 959294 118 William St Condell Park 2200	Design Custom	Vogue Job No. 9013-22	Project Number DD-1451	DD-1451-24
						Facade Custom	LGA Canterbury Bankstown	Current Revision 3 26/09/23	Shadow Diagram - June 21 4pm
						Inclusions Vogue	Approval Path DA	Date 18/03/22	Scale 1 : 200 @ A3

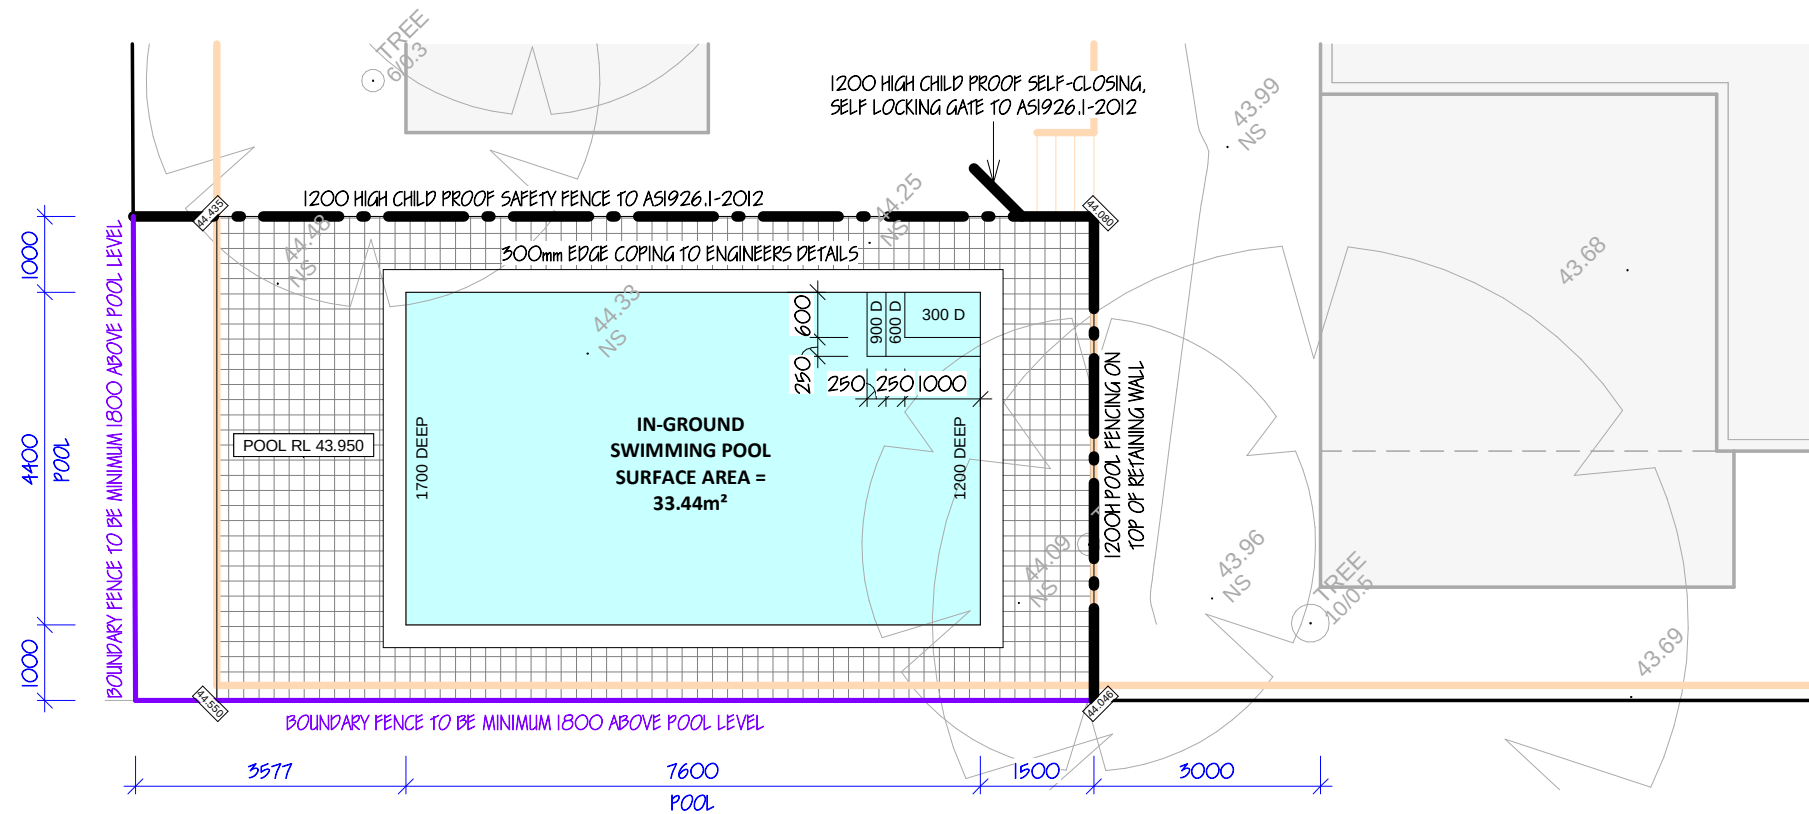

1

Swimming Pool Plan

1 : 100

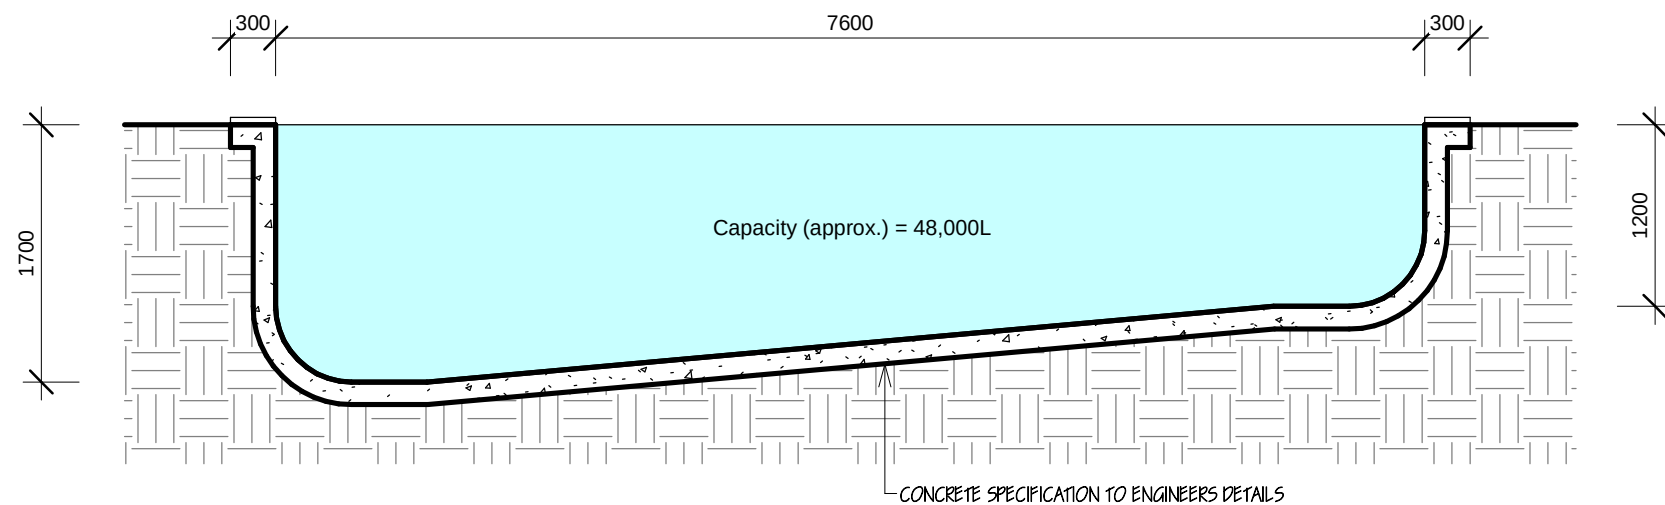


2

Pool Section

1 : 50

Disclaimer: Some items displayed or noted on these plans may be for indicative nominal placement or certification purposes only. The written words in any accompanying building tender will on all occasions take precedence to the plan. All internal room dimensions shown on any floor plan are to timber frame for construction purpose.

	ABN 67 250 466 867 Suite 7, Shop 11, 38 Exchange Parade Narellan NSW 2567 P: 0421 993 467 E: info@definitivedrafting.com.au W: www.definitivedrafting.com.au	This drawing and information thereon is the property of Vogue Homes and must not be loaned, partly copied, fully copied or used without the expressed permission in license or writing		License No. 115618C Unit 2/16 Weld Street Prestons NSW 2170 P: (02) 96079554 E: admin@vogue-homes.com.au W: www.vogue-homes.com.au	Hau Thi Bui & Toan Hoang Pham Lot 5 DP 959294 118 William St Condell Park 2200	Design Custom	Vogue Job No. 9013-22	Project Number DD-1451	DD-1451-25
						Facade Custom	LGA Canterbury Bankstown	Current Revision 3 26/09/23	Pool Site Plan
						Inclusions Vogue	Approval Path DA	Date 18/03/22	Scale As indicated @ A3

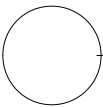

Street View at Near Kerb

Disclaimer: Some items displayed or noted on these plans may be for indicative nominal placement or certification purposes only. The written words in any accompanying building tender will on all occasions take precedence to the plan. All internal room dimensions shown on any floor plan are to timber frame for construction purpose.

	ABN 67 250 466 867 Suite 7, Shop 11, 38 Exchange Parade Narellan NSW 2567 P: 0421 993 467 E: info@definitivedrafting.com.au W: www.definitivedrafting.com.au	This drawing and information thereon is the property of Vogue Homes and must not be loaned, partly copied, fully copied or used without the expressed permission in license or writing		License No. 115618C Unit 2/16 Weld Street Prestons NSW 2170 P: (02) 96079554 E: admin@vogue-homes.com.au W: www.vogue-homes.com.au	Hau Thi Bui & Toan Hoang Pham Lot 5 DP 959294 118 William St Condell Park 2200	Design Custom	Vogue Job No. 9013-22	Project Number DD-1451	DD-1451-27
						Facade Custom	LGA Canterbury Bankstown	Current Revision 3 26/09/23	Facade Image
						Inclusions Vogue	Approval Path DA	Date 18/03/22	Scale @ A3