

SHEET INDEX

1	COVER SHEET
2	SITE ANALYSIS
3	SITE PLAN
4	SITE PLAN - TPZ/ARBORIST NOTATION
5	WATER MANAGEMENT PLAN (GF)
6	WATER MANAGEMENT PLAN (FF)
7	GROUND FLOOR PLAN
8	FIRST FLOOR PLAN
9	ROOF PLAN
10	WINDOW & DOOR SCHEDULES
11	ELEVATIONS / SECTION
12	ELEVATIONS
13	HOUSE EXTERIOR 3D VIEWS
14	KITCHEN DETAILS
15	BATHROOM DETAILS
16	ENSUITE / WC DETAILS
17	POWDER ROOM DETAILS
18	POWDER ROOM 2 DETAILS
19	LAUNDRY DETAILS
20	FLOOR COVERINGS (GF)
21	FLOOR COVERINGS (FF)
22	SLAB PLAN
23	DRAINAGE PLAN
24	SHADOW DIAGRAMS - JUNE 21

TOTAL FLOOR AREAS

MAIN DWELLING, GROUND FLOOR	
ALFRESCO	27.81
GARAGE	26.63
LIVING	124.65
PATIO	5.23
STAIRS	7.61
	191.93 m²
MAIN DWELLING, FIRST FLOOR	
LIVING	126.18
VOID	21.37
	147.55 m²
	339.48 m²

AS & NCC COMPLIANCE

ALL CONSTRUCTION TO BE IN ACCORDANCE WITH NCC 2022 AND APPLICABLE AUSTRALIAN STANDARDS AT TIME OF APPROVAL.

- SLAB IN ACCORDANCE WITH AS 2870. REFER TO ENGINEERS DETAILS FOR ALL SLAB DETAILS.
- BRICK CONTROL JOINTS PROVIDED IN ACCORDANCE WITH NCC 2022.
- ALL STEEL FRAMING TO BE DESIGNED TO AS 4100-2020 OR AS/NZS 4600-2018.
- INSULATION TO BE INSTALLED IN ACCORDANCE WITH NCC 2022 AND ALL APPLICABLE AUSTRALIAN STANDARDS.
- TERMITE PROTECTION IN ACCORDANCE WITH AS 3660 AND NCC 2022.
- GLAZING IN ACCORDANCE WITH AS 1288 AND NCC 2022.
- SMOKE ALARMS IN ACCORDANCE WITH AS 3786 AND NCC 2022.
- INTERNAL WATERPROOFING IN ACCORDANCE WITH NCC 2022 HOUSING PROVISIONS PART 10.2.
- EXTERNAL WATERPROOFING IN ACCORDANCE WITH AS 3740 AND AS 4654.
- WET AREA FLOORS TO FALL TO FLOOR WASTES AT MIN. 1:80 AND MAX. 1:50 GRADE (IF APPLICABLE).
- CONDENSATION MANAGEMENT IN ACCORDANCE WITH NCC 2019.
- BUILDING SEALING IN ACCORDANCE WITH NCC 2022.
- SERVICES IN ACCORDANCE WITH NCC 2022.
- EARTHWORKS IN ACCORDANCE WITH AS 3798-2007.
- EXTERNAL WALL WRAP (SARKING) IN ACCORDANCE WITH NCC 2022 (IF APPLICABLE).
- EXHAUST FANS DUCTED TO OUTSIDE AIR (IF APPLICABLE).


SITE SPECIFIC CONTROLS

CONTROL	DETAILS
ACID SULPHATE SOIL	CLASSIFICATION 4
BIODIVERSITY	NO
BUILDING ENVELOPE	NO
BUSHFIRE	NO
CLASSIFIED ROAD	NO
DESIGN WIND CLASSIFICATION	N1 (NOT EXPOSED)
ESTATE/DEVELOPER GUIDELINES	NO
HERITAGE	NO
LANDSLIP HAZARD	NO
MINE SUBSIDENCE	NO
MINIMUM FLOOR LEVEL	NO
NOISE ATTENUATION	NO
SALINE SOIL	NO
SITE CLASSIFICATION	P-M
SNOW LOAD	NO
WITHIN 1km CALM SALT WATER	NO
WITHIN 50km BREAKING SURF	14.40km
ZONING	R3 - MEDIUM DENSITY RESIDENTIAL

BUILDING CONTROLS & COMPLIANCE

CONTROL	REQUIRED	PROPOSED
SETBACKS		
FRONT	MIN. 5,500mm	7,000mm
GARAGE TO BOUNDARY	MIN. 5,500mm	8,120mm
GARAGE TO BUILDING LINE	MIN. 1,000mm	1,000mm
SIDE	MIN. 900mm	915mm
REAR	MIN. 6,000mm	11,812mm
BULK & SCALE		
SITE AREA	454.9m²	
SITE COVERAGE	MAX. 50%	42.23%
FLOOR SPACE RATIO	MAX. 0.5:1	0.52:1
BUILDING HEIGHT	MAX. 8,500mm	7,783mm
LANDSCAPE		
DEEP SOIL AREA	MIN. 90.98m²	174.48m²
EARTHWORKS		
CUT DEPTH	MAX. 1,000mm	195mm
FILL DEPTH	MAX. 600mm	198mm
ACCESS & AMENITY		
PARKING SPACES	MIN. 2 SPACES	2 SPACES
PRIVATE OPEN SPACE	MIN. 80m²	131.19m²

3D PERSPECTIVE

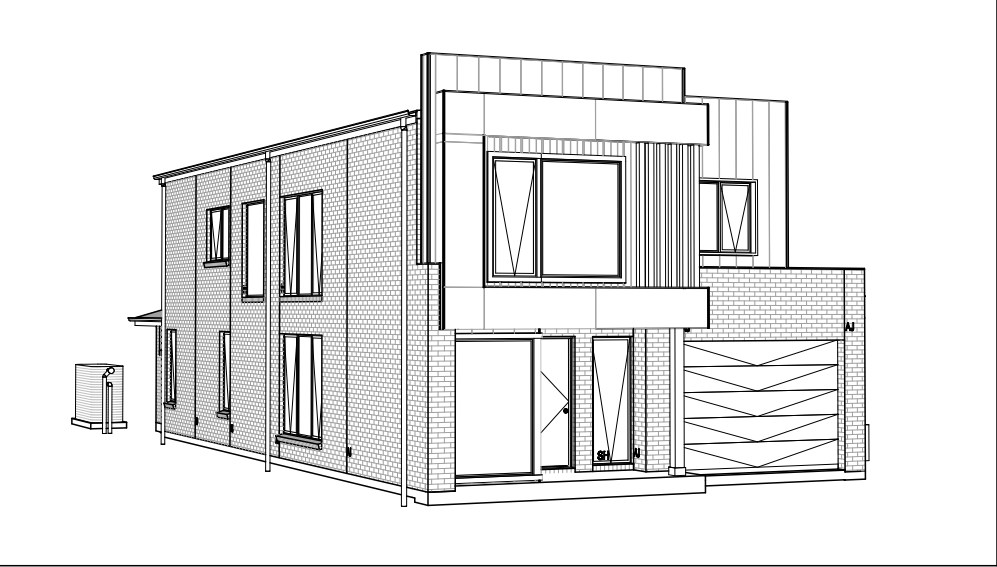

NOTE TO OWNER

THESE PLANS MAY FEATURE WORKS THAT ARE EXCLUDED FROM THE SCOPE OF WORKS WITH THE BUILDER, BUT THEY HAVE BEEN INCLUDED IN THESE DRAWINGS TO ASSIST IN THE OVERALL PLANNING AND ASSESSMENT OF THE BUILDING PROJECT. EXAMPLES OF SOME REGULARLY EXCLUDED WORKS INCLUDE DRIVEWAYS, RETAINING WALLS, SOLAR PANEL SPACING AND SITE DRAINAGE. PLEASE REFER TO YOUR SCOPE OF WORKS AND COLOUR SELECTIONS DOCUMENTATION FOR DETAILS OF INCLUDED WORKS. SOME DETAILS ARE INDICATIVE ONLY FOR EXAMPLE FLOORING, TILING, BRICKWORK AND CLADDING (EXPANSION JOINTS, ORIENTATION AND LAYOUT) AND ARE SUBJECT TO CHANGE.

LOCATION MAP



SUSTAINABILITY

PRELIMINARY SUSTAINABILITY COMPLIANCE FOR YOUR HOME REQUIRES FURTHER ASSESSMENT TO DETERMINE COMPLIANCE CRITERIA. THIS ASSESSMENT WILL BE FINALISED UPON APPROVAL OF YOUR EXTERNAL COLOUR SELECTIONS TO DETERMINE IF VARIATIONS ARE REQUIRED TO THE PROPOSED DWELLING E.G. ADDITIONAL INSULATION, CHANGES IN WINDOW GLAZING / SIZE / ORIENTATION ETC. YOU WILL BE ADVISED OF ANY REQUIREMENTS OR ALTERNATIVES ONCE THE ASSESSMENT HAS BEEN COMPLETED.

BASIX AREAS

CONDITIONED AREA	231.43 m²
UNCONDITIONED AREA	17.42 m²

WATER RATINGS

SHOWER HEADS	3 STAR (> 7.5 BUT <= 9 L/MIN)
TOILET SUITES	4 STAR
KITCHEN TAPS	4 STAR
BATHROOM TAPS	5 STAR

WATER HARVESTING AND USAGE

TOTAL ROOF AREA	198.84 m²
MIN. WATER TANK CAPACITY	3239 L
MIN. ROOF AREA DIRECTED TO TANK(S)	173.10 m²
WATER TANK(S) CONNECTED TO	AT LEAST ONE OUTDOOR TAP ALL TOILETS WASHING MACHINE
GARDEN/LAWN AREA	190 m²

RECYCLED WATER

RETICULATED RECYCLED WATER	N/A
----------------------------	-----

ENERGY COMMITMENTS

HOT WATER SYSTEM	GAS CONTINUOUS FLOW 6 STAR
HEATING SYSTEM	3-PHASE REVERSE CYCLE AIR CONDITIONING COP 3.5 - 4.0
COOLING SYSTEM	3-PHASE REVERSE CYCLE AIR CONDITIONING EER 3.0 - 3.5
CEILING FANS	4 - REFER TO FLOOR PLAN FOR LOCATIONS

VENTILATION (EXHAUST FANS)

AT LEAST ONE BATHROOM:
DUCTED TO OUTSIDE AIR, INTERLOCKED TO LIGHT
KITCHEN RANGEHOOD:
DUCTED TO OUTSIDE AIR, MANUAL SWITCH ON/OFF
NO MECHANICAL VENTILATION TO LAUNDRY

PRIMARY FLUORESCENT/LED LIGHTING (INCL. COVER)

N/A

NATURAL LIGHTING

NATURAL LIGHTING TO	KITCHEN 2 x BATHROOM(S)/TOILET(S)
---------------------	--------------------------------------

ALTERNATIVE ENERGY

PHOTOVOLTAIC SYSTEM	MIN. 6.60KW PEAK
---------------------	------------------

OTHER

GAS COOKTOP, ELECTRIC OVEN
FIXED OUTDOOR CLOTHESLINE BY OWNER
NO FIXED INDOOR CLOTHESLINE

INSULATION

ROOF	MIN. 80mm FOIL FACED BLANKET UNDER ROOFING
CEILING	R6.0 BATTS (EXCL. GARAGE)
EXT. WALLS	R2.2 BATTS (R2.2HP EXCLUDING GARAGE) CSR 15MM R0.14 TO ALL WALLS WALL WRAP TO CLADDING
INT. WALLS	R2.2 BATTS (R2.2HP BATTS) TO GARAGE, LAUNDRY AND BATHROOM
FLOOR	4.1 BATTS TO FIRST FLOOR JOIST SPACE

BUILDING INFORMATION

GROUND FLOOR PITCHING HEIGHT(S)	2745mm
FIRST FLOOR PITCHING HEIGHT(S)	2745mm
FRAMES AND TRUSSES	20° / 5° / 3°
ROOF PITCH (U.N.O.)	5.0°
ELECTRICITY SUPPLY	3-PHASE
GAS SUPPLY	MAINS / RETICULATED
ROOF MATERIAL	SHEET METAL
ROOF COLOUR	LIGHT
WALL MATERIAL	BRICK VENEER CLADDING
WALL COLOUR	N/A
SLAB CLASSIFICATION	M

SUBJECT TO NCC 2022
(1 OCT 2023 + 7 STAR)
WATERPROOFING & PLUMBING

PLAN ACCEPTANCE BY OWNER



SIGNATURE: _____ DATE: _____

SIGNATURE: _____ DATE: _____

PLEASE NOTE THAT VARIATIONS WILL NOT BE ACCEPTED
AFTER THIS PLAN ACCEPTANCE HAS BEEN SIGNED

© 2024 MCDONALD JONES HOMES PTY LTD (ABN 82 003 687 232). THIS DRAWING IS AN ORIGINAL ARTISTIC WORK WITHIN THE MEANING OF THE COPYRIGHT ACT 1968 (CTH). MCDONALD JONES HOMES PTY LTD IS THE OWNER OF COPYRIGHT IN THIS DRAWING. YOU HEREBY AGREE AND UNDERTAKE THAT YOU WILL NOT IN ANY WAY REPRODUCE, COPY, MODIFY, USE OR TAKE ADVANTAGE OF THE DRAWING TO BUILD A HOUSE BASED ON THIS PLAN (WHETHER IN WHOLE OR IN PART) WITHOUT THE PRIOR WRITTEN CONSENT OF MCDONALD JONES HOMES PTY LTD.

SPECIFICATION: TWO STOREY		REVISION	DRAWN	CLIENT:	HOUSE DESIGN:	HOUSE CODE:	DO NOT SCALE DRAWINGS. USE FIGURED DIMENSIONS ONLY. CHECK AND VERIFY DIMENSIONS AND LEVELS PRIOR TO THE COMMENCEMENT OF ANY WORK. ALL DISCREPANCIES TO BE REPORTED TO THE DRAFTING OFFICE.		
	5	COLOURS APPLIED	TNG 26/01/2024	CLIFF LAURENS & MARGARETHA HARUNISA TARUNADJAYA	PANORAMA 36	H-MDSPNR20DA			
COPYRIGHT: © 2024	6	AMENDED AS PER PCV007	GB0 22/02/2024	ADDRESS:	FACADE DESIGN:	FACADE CODE:			
	7	AMENDED AS PER PCV08 - HYDRAULIC	LFL 09/04/2024	48 WENTWORTH STREET, CROYDON PARK NSW 2133	PULSE	F-MDSPNR20PLSEA			
	8	AMENDED AS PER PCV009 & PCV011	GB0 03/05/2024	LOT / SECTION / DP:	COUNCIL:	SHEET TITLE:		SHEET No.:	SCALES:
	9	AMENDED AS PER PCV013	LCS 08/05/2024	1 / - / 304988	CANTERBURY BANKSTOWN COUNCIL	COVER SHEET		1 / 24	1:100
							607082		

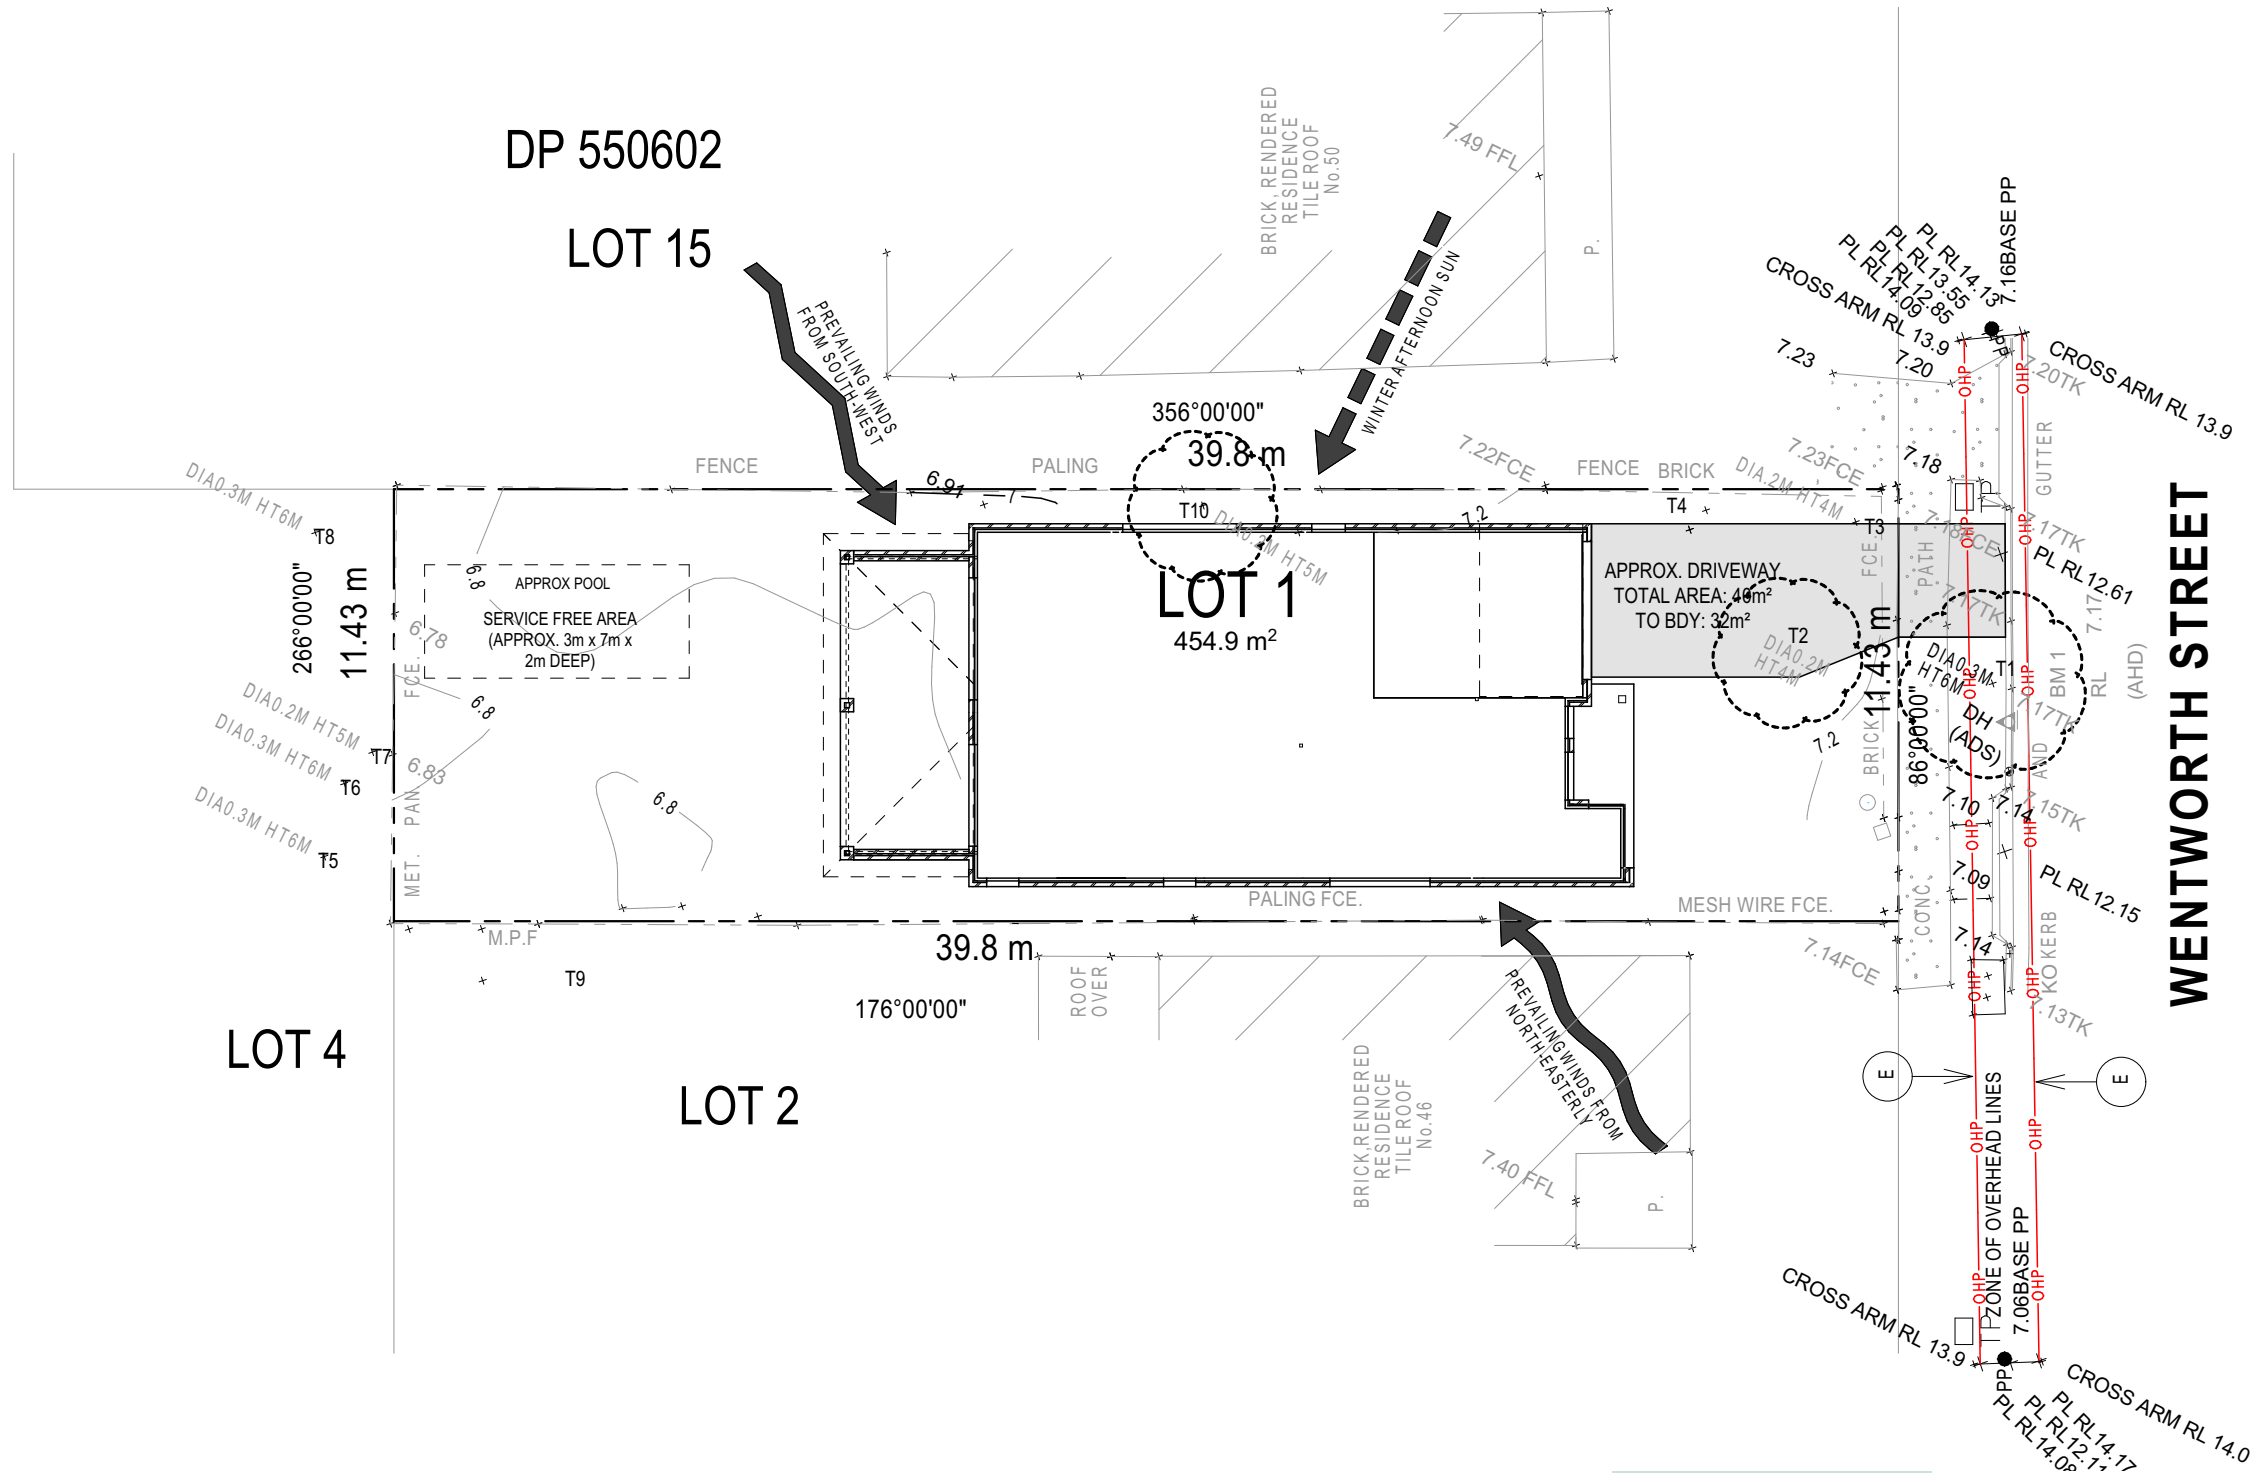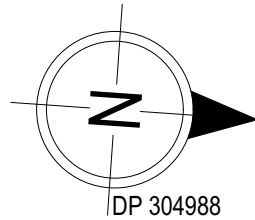

**SUBJECT TO NCC 2022
(1 OCT 2023 + 7 STAR)
WATERPROOFING & PLUMBING**

PLAN ACCEPTANCE BY OWNER	
SIGNATURE:	DATE:

SIGNATURE:	DATE:

PLEASE NOTE THAT VARIATIONS WILL NOT BE ACCEPTED AFTER THIS PLAN ACCEPTANCE HAS BEEN SIGNED	

© 2024 MCDONALD JONES HOMES PTY LTD (ABN 82 003 687 232). THIS DRAWING IS AN ORIGINAL ARTISTIC WORK WITHIN THE MEANING OF THE COPYRIGHT ACT 1968 (CTH). MCDONALD JONES HOMES PTY LTD IS THE OWNER OF COPYRIGHT IN THIS DRAWING. YOU HEREBY AGREE AND UNDERTAKE THAT YOU WILL NOT IN ANY WAY REPRODUCE, COPY, MODIFY, USE OR TAKE ADVANTAGE OF THE DRAWING TO BUILD A HOUSE BASED ON THIS PLAN (WHETHER IN WHOLE OR IN PART) WITHOUT THE PRIOR WRITTEN CONSENT OF MCDONALD JONES HOMES PTY LTD.



SPECIFICATION: TWO STOREY COPYRIGHT: © 2024	REVISION		DRAWN		CLIENT: CLIFF LAURENS & MARGARETHA HARUNISA TARUNADJAYA ADDRESS: 48 WENTWORTH STREET, CROYDON PARK NSW 2133 LOT / SECTION / DP: 1 / - / 304988	HOUSE DESIGN: PANORAMA 36 FACADE DESIGN: PULSE SHEET TITLE: SITE ANALYSIS	HOUSE CODE: H-MDSPNR20DA FACADE CODE: F-MDSPNR20PLSEA SHEET No.: 2 / 24	DO NOT SCALE DRAWINGS. USE FIGURED DIMENSIONS ONLY. CHECK AND VERIFY DIMENSIONS AND LEVELS PRIOR TO THE COMMENCEMENT OF ANY WORK. ALL DISCREPANCIES TO BE REPORTED TO THE DRAFTING OFFICE. 607082
	5	COLOURS APPLIED	TNG	26/01/2024				
	6	AMENDED AS PER PCV007	GBO	22/02/2024				
	7	AMENDED AS PER PCV08 - HYDRAULIC	LFL	09/04/2024				
	8	AMENDED AS PER PCV009 & PCV011	GBO	03/05/2024				
	9	AMENDED AS PER PCV013	LCS	08/05/2024	COUNCIL: CANTERBURY BANKSTOWN COUNCIL		SCALES: 1:200	

REFER TO SHEET 1 (COVER SHEET) FOR ALL BUILDING INFORMATION REGARDING:

- SUSTAINABILITY REQUIREMENTS
- SITE CLASSIFICATION
- GENERAL BUILDING INFORMATION

STORMWATER LAYOUT IS DIAGRAMMATIC ONLY AND NO REPRESENTATION IS MADE AS TO THE AS-BUILT LOCATION OF STORMWATER ASSETS (INCLUDING SURFACE INLET PITS) OR THE TYPE OF SYSTEM USED (CHARGED OR GRAVITY FED). ALL STORMWATER DESIGN IS SUBJECT TO CONTRACTORS RECOMMENDATIONS AND/OR ANY CONSTRUCTION CONSTRAINTS OR CHANGES AT THE DISCRETION OF THE BUILDER. THE STORMWATER SYSTEM IS NOT SUITABLE FOR ANY OTHER USE. ALL SURFACE WATER DRAINAGE MUST BE MANAGED BY OWNER INCLUDING INSTALLATION OF ADDITIONAL DISCHARGE LINES AND INLETS AS REQUIRED. THE BUILDER PROVIDES CAPACITY FOR DISPOSAL OF ROOF COLLECTED STORMWATER ONLY AND TAKES NO RESPONSIBILITY FOR OVERFLOW OR DAMAGE TO PROPERTY IF OWNER ADDS ADDITIONAL DISCHARGE LOADS TO EXISTING STANDARD PROVISIONS.

DRIVEWAY AND RETAINING WALLS BY OWNER UNLESS NOTED OTHERWISE IN THE SCOPE OF WORK AND/OR COLOUR SELECTIONS DOCUMENTATION.

PROPOSED TREES BY OWNER AFTER HANDOVER UNLESS NOTED OTHERWISE IN THE TENDER DOCUMENTATION.

APPROX. CUT/FILL		
CUT	13.92m³	31.32t
FILL	14.45m³	32.51t
DIFFERENCE	0.53m³	1.19t
EVEN CUT & FILL		

+/- 100mm TOLERANCE TO NOMINATED FINISHED FLOOR LEVELS. SUBJECT TO MAXIMUM DRIVEWAY PROFILE AND/OR ANY FLOOD RELATED LEVELS

OWNERS ARE FULLY RESPONSIBLE FOR ENSURING THEY HAVE REMOVED ALL EXISTING STRUCTURES AND UTILITY SERVICES FROM THE PROPOSED CONSTRUCTION SITE I.E.:

- EXISTING HOUSE, CARPORT, SHED, PAVING, PATHS, GARDEN BEDS, DRIVEWAYS, SWIMMING POOL OR UNDERGROUND TANKS AND ALL BELOW GROUND FOOTING STRUCTURES.
- REMOVAL OF ANY TREES, STUMPS, BARK OR EXCESSIVE GROWTH WHICH MAY IMPACT ON CONSTRUCTION SITE ACCESS.
- ALL BUILDING MATERIALS OR WASTE ON SITE IS TO BE FULLY REMOVED. ANY DEPRESSIONS TO NATURAL GROUND LEVEL ARE TO BE ADEQUATELY FILLED.
- ANY EXCESS FILL WHICH MAY IMPACT ON CONSTRUCTION SITE ACCESS TO BE REMOVED.
- GAS METER AND ASSOCIATED PIPE WORK TO BE REMOVED BACK TO SITE BOUNDARY.
- ELECTRICAL METER AND ASSOCIATED SERVICES TO BE REMOVED TO AGREED SAFE DISTANCE (BOUNDARY/POLE).
- WATER METER AND ASSOCIATED PIPE WORK TO BE REMOVED BACK TO SITE BOUNDARY.
- TELEPHONE & DATA CABLES TO BE REMOVED BACK TO SITE BOUNDARY.
- EXISTING SITE SEWER & STORM WATER CONNECTIONS TO BE REMOVED AND CAPPED OFF TO PREVENT INCIDENCE OF BUILDING MATERIALS ENTERING THOSE SYSTEMS AND LEAVING YOUR SITE.
- ASBESTOS: A SITE CLEARANCE CERTIFICATE IS REQUIRED TO BE SUPPLIED TO US BY THE OWNER PRIOR TO US COMMENCING WORK ON YOUR SITE.
- YOUR DEMOLITION COMPANY SHOULD BE ABLE ARRANGE THIS FOR YOU.

PLEASE NOTE: RELEVANT DOCUMENTED REPORT EVIDENCE & PICTURES FROM PARTIES CARRYING OUT THESE SERVICES WILL BE REQUIRED TO ENSURE THE ABOVE ASPECTS HAVE BEEN COMPLETED EFFECTIVELY TO MEET BOTH OUR LEGAL & CONTRACT REQUIREMENTS.







IMPORTANT NOTE
ANY PART OF THE FASCIA, GUTTERING OR DOWNPIPE THAT IS WITHIN 450mm OF ANY BOUNDARY IS TO BE NON-COMBUSTIBLE IN ACCORDANCE WITH THE REQUIREMENTS OF PART 3.7.1(C) OF THE BCA

OVERHEAD POWER LINES ARE PRESENT

DEMOLITION SHOWN DASHED

DP 550602

LOT 15

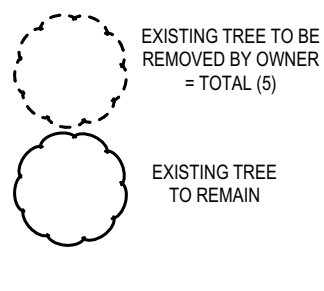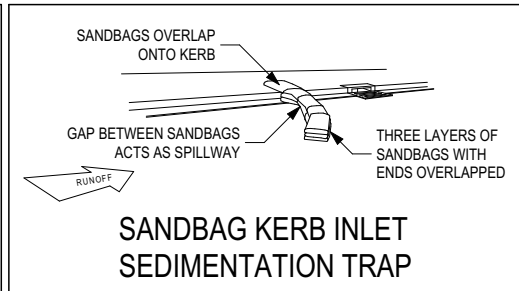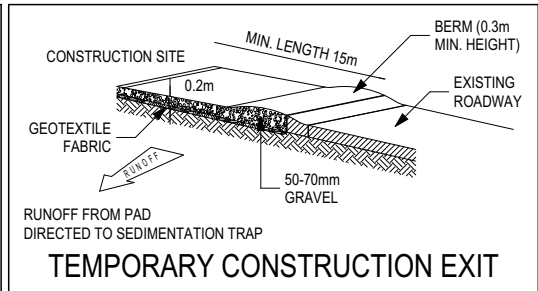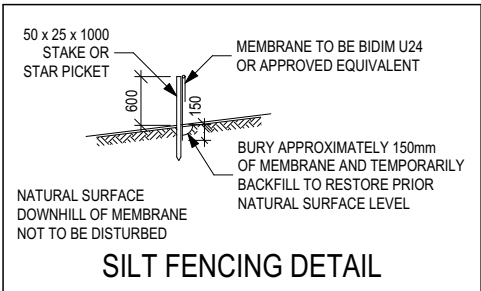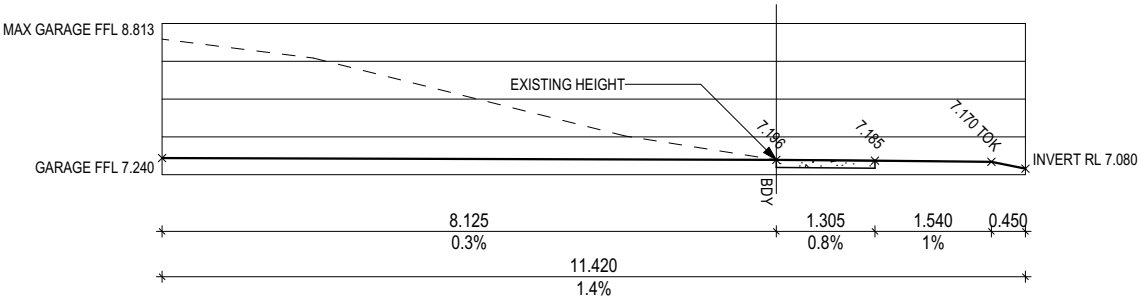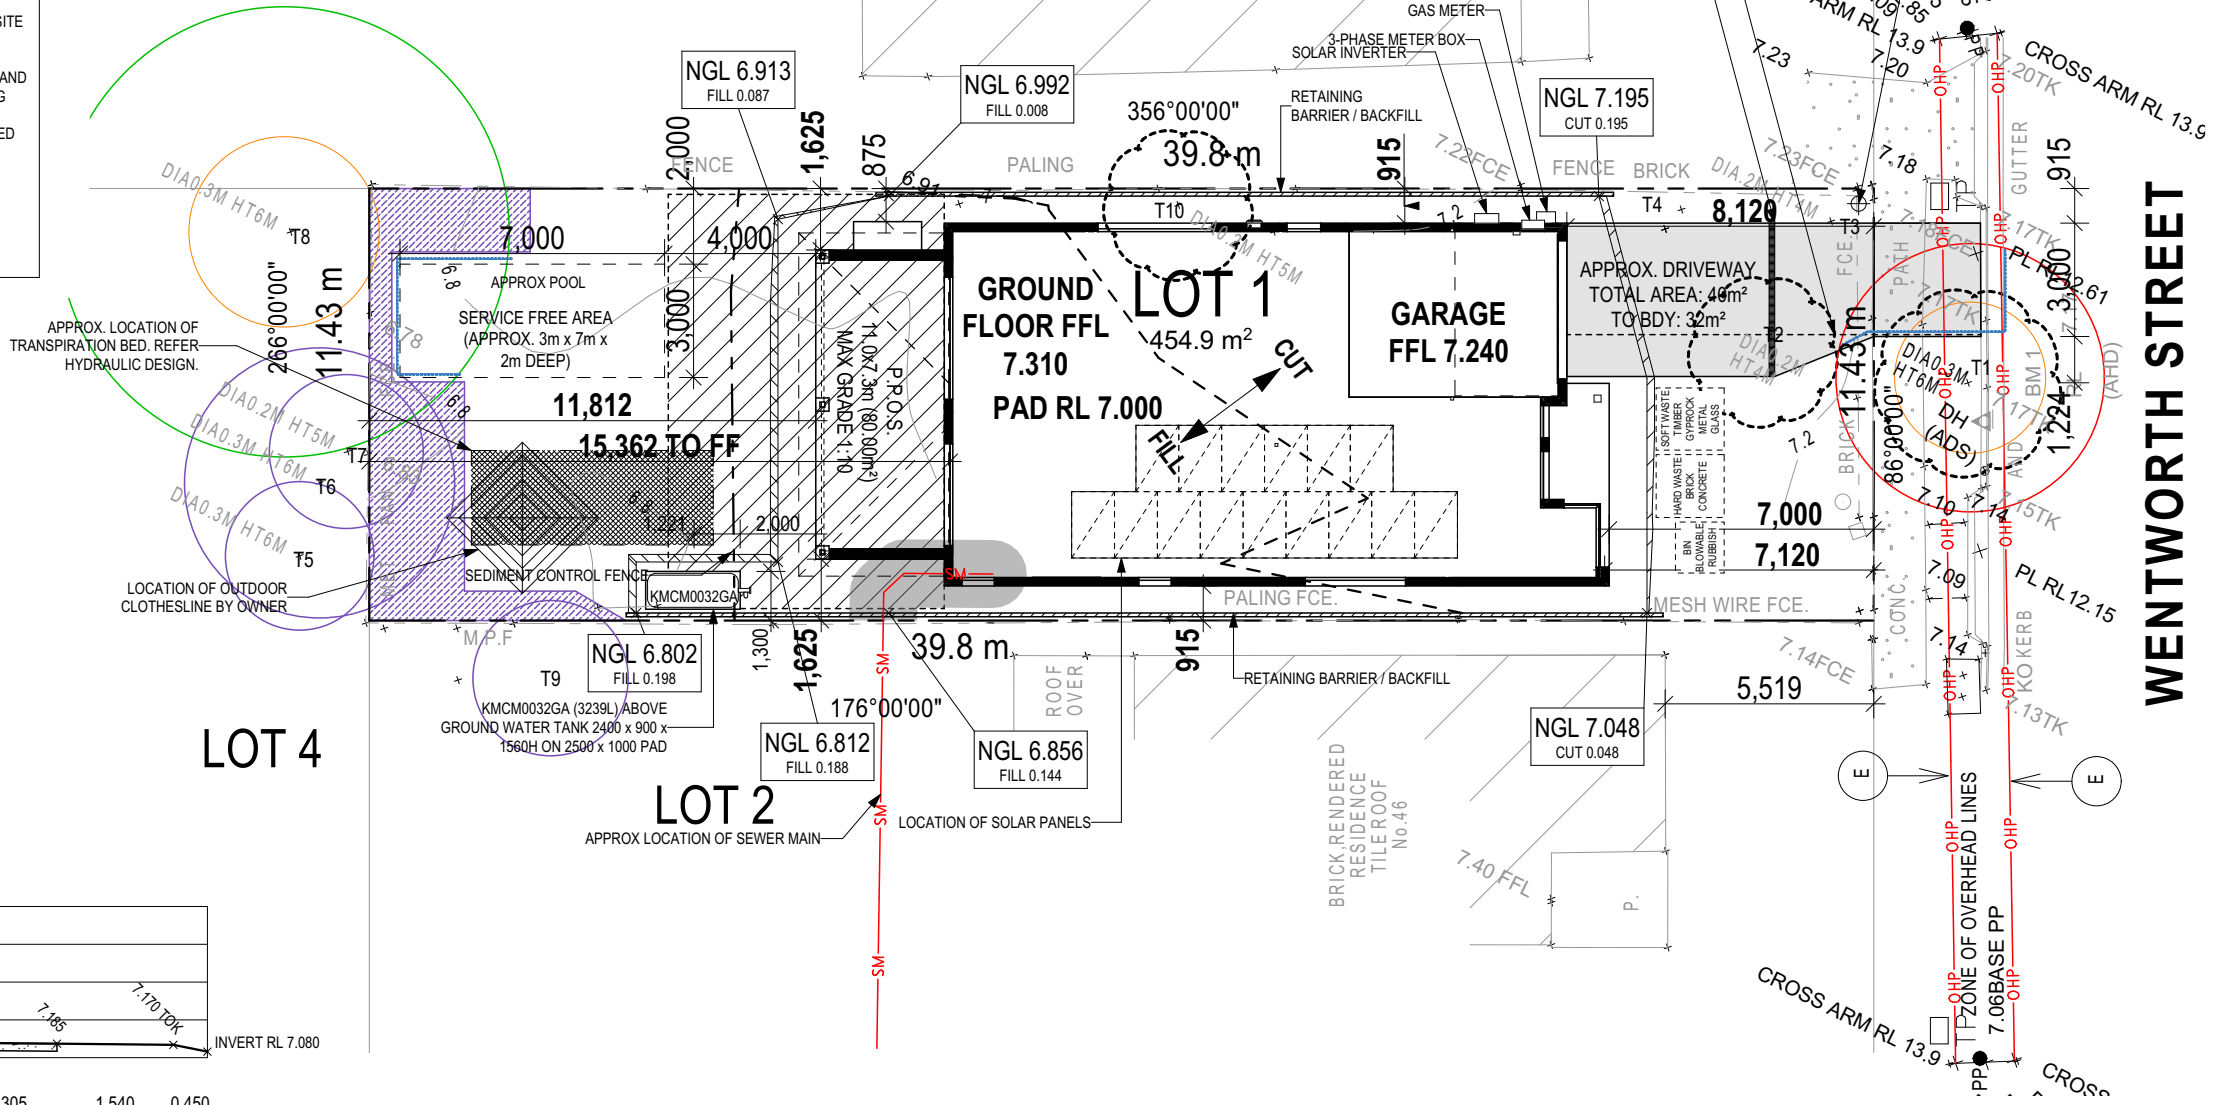

SUBJECT TO NCC 2022 (1 OCT 2023 + 7 STAR) WATERPROOFING & PLUMBING



PLAN ACCEPTANCE BY OWNER

SIGNATURE: _____ DATE: _____


SIGNATURE: _____ DATE: _____

PLEASE NOTE THAT VARIATIONS WILL NOT BE ACCEPTED AFTER THIS PLAN ACCEPTANCE HAS BEEN SIGNED

 mcdonald jones FIND YOURSELF AT HOME	SPECIFICATION:		REVISION		DRAWN		CLIENT:			HOUSE DESIGN:			HOUSE CODE:		DO NOT SCALE DRAWINGS. USE FIGURED DIMENSIONS ONLY. CHECK AND VERIFY DIMENSIONS AND LEVELS PRIOR TO THE COMMENCEMENT OF ANY WORK. ALL DISCREPANCIES TO BE REPORTED TO THE DRAFTING OFFICE. 607082
	TWO STOREY	5	COLOURS APPLIED		TNG	26/01/2024	CLIFF LAURENS & MARGARETHA HARUNISA TARUNADJAYA			PANORAMA 36			H-MDSPNR20DA		
	COPYRIGHT:	6	AMENDED AS PER PCV007		GB0	22/02/2024	ADDRESS:			FACADE DESIGN:			FACADE CODE:		
	© 2024	7	AMENDED AS PER PCV08 - HYDRAULIC		LFL	09/04/2024	48 WENTWORTH STREET, CROYDON PARK NSW 2133			PULSE			F-MDSPNR20PLSEA		
		8	AMENDED AS PER PCV009 & PCV011		GB0	03/05/2024	LOT / SECTION / DP:		COUNCIL:		SHEET TITLE:		SHEET No.:	SCALES:	
		9	AMENDED AS PER PCV013		LCS	08/05/2024	1 / - / 304988		CANTERBURY BANKSTOWN COUNCIL		SITE PLAN		3 / 24	1:200, 1:266.67	

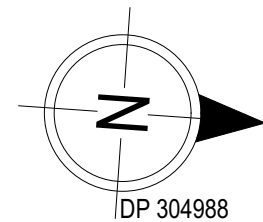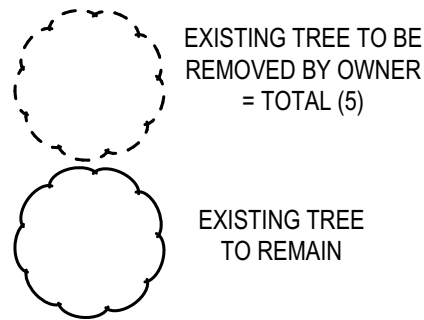

SITE PLAN (TPZ-ARBORIST)
SCALE: 1:200

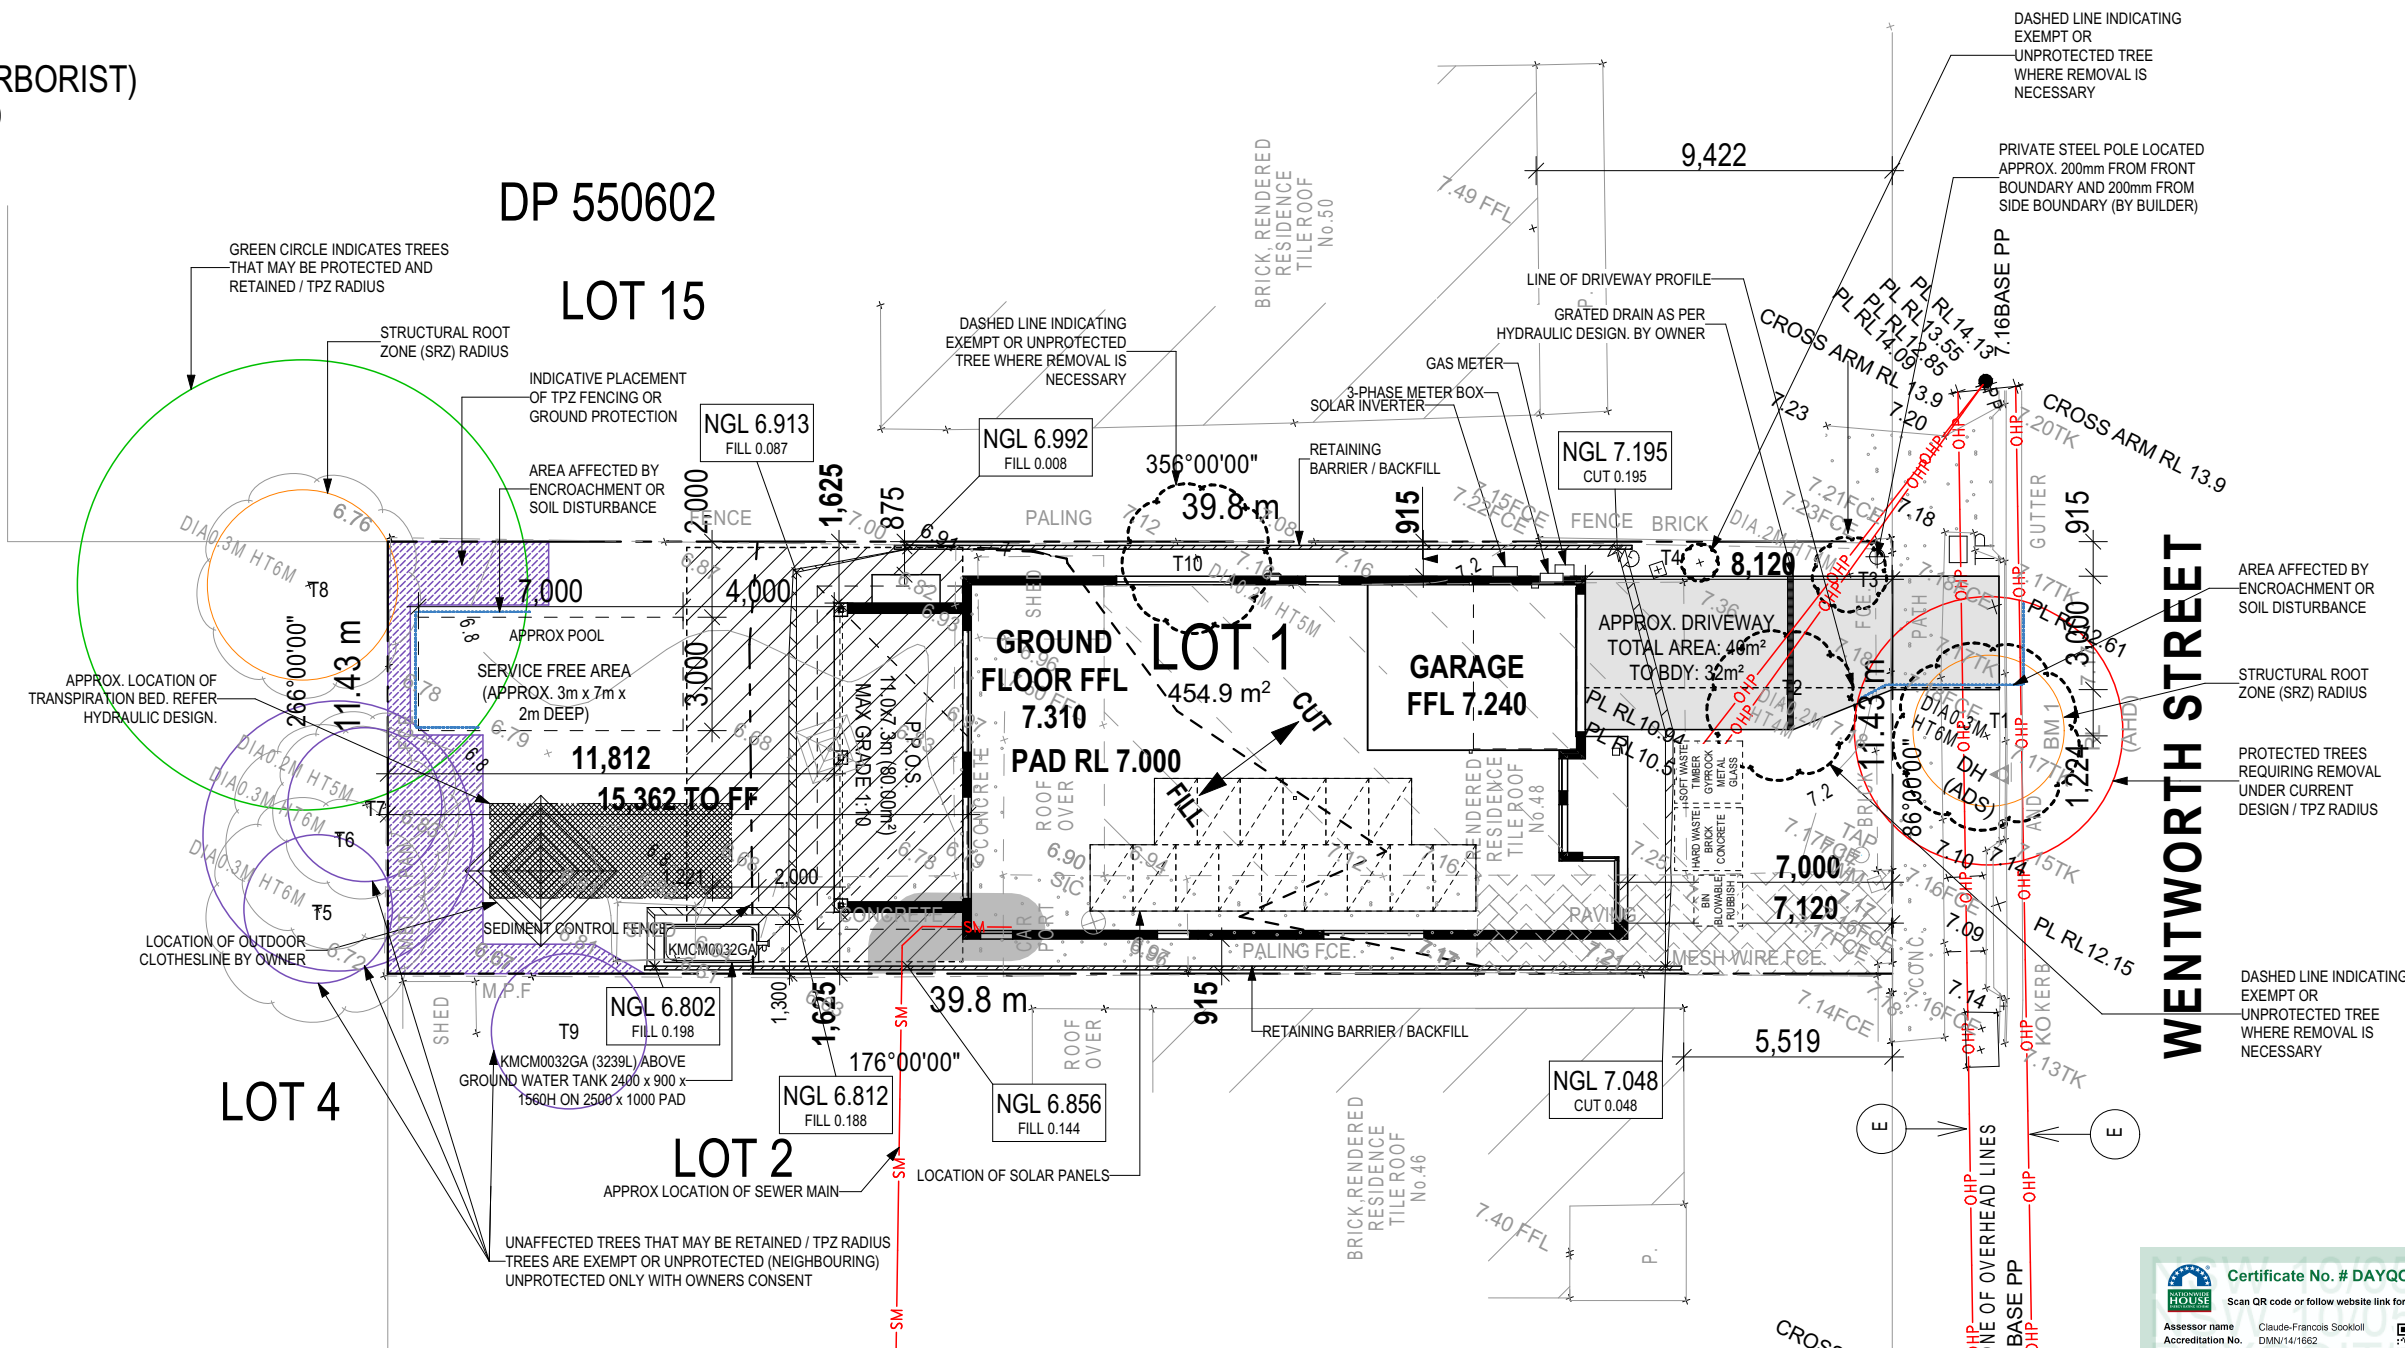

SITE PLAN (TPZ-ARBORIST)
SCALE: 1:200



© 2024 MCDONALD JONES HOMES PTY LTD (ABN 82 003 687 232). THIS DRAWING IS AN ORIGINAL ARTISTIC WORK WITHIN THE MEANING OF THE COPYRIGHT ACT 1968 (CTH). MCDONALD JONES HOMES PTY LTD IS THE OWNER OF COPYRIGHT IN THIS DRAWING. YOU HEREBY AGREE AND UNDERTAKE THAT YOU WILL NOT IN ANY WAY REPRODUCE, COPY, MODIFY, USE OR TAKE ADVANTAGE OF THE DRAWING TO BUILD A HOUSE BASED ON THIS PLAN (WHETHER IN WHOLE OR IN PART) WITHOUT THE PRIOR WRITTEN CONSENT OF MCDONALD JONES HOMES PTY LTD.




SPECIFICATION: TWO STOREY COPYRIGHT: © 2024	REVISION		DRAWN		CLIENT: CLIFF LAURENS & MARGARETHA HARUNISA TARUNADJAYA ADDRESS: 48 WENTWORTH STREET, CROYDON PARK NSW 2133 LOT / SECTION / DP: 1 / - / 304988	HOUSE DESIGN: PANORAMA 36 FACADE DESIGN: PULSE SHEET TITLE: SITE PLAN - TPZ/ARBORIST NOTATION	HOUSE CODE: H-MDSPNR20DA FACADE CODE: F-MDSPNR20PLSEA SHEET No.: 4 / 24	DO NOT SCALE DRAWINGS. USE FIGURED DIMENSIONS ONLY. CHECK AND VERIFY DIMENSIONS AND LEVELS PRIOR TO THE COMMENCEMENT OF ANY WORK. ALL DISCREPANCIES TO BE REPORTED TO THE DRAFTING OFFICE. 607082
	5	COLOURS APPLIED	TNG	26/01/2024				
	6	AMENDED AS PER PCV007	GB0	22/02/2024				
	7	AMENDED AS PER PCV08 - HYDRAULIC	LFL	09/04/2024				
	8	AMENDED AS PER PCV09 & PCV011	GB0	03/05/2024				
	9	AMENDED AS PER PCV013	LCS	08/05/2024	COUNCIL: CANTERBURY BANKSTOWN COUNCIL	SCALES: 1:200		

REFER TO SHEET 1 (COVER SHEET) FOR
ALL BUILDING INFORMATION REGARDING:

- SUSTAINABILITY REQUIREMENTS
- SITE CLASSIFICATION
- GENERAL BUILDING INFORMATION

STORMWATER LAYOUT IS DIAGRAMMATIC ONLY AND NO REPRESENTATION IS MADE AS TO THE AS-BUILT LOCATION OF STORMWATER ASSETS (INCLUDING SURFACE INLET PITS) OR THE TYPE OF SYSTEM USED (CHARGED OR GRAVITY FED). ALL STORMWATER DESIGN IS SUBJECT TO CONTRACTORS RECOMMENDATIONS AND/OR ANY CONSTRUCTION CONSTRAINTS OR CHANGES AT THE DISCRETION OF THE BUILDER. THE STORMWATER SYSTEM IS NOT SUITABLE FOR ANY OTHER USE. ALL SURFACE WATER DRAINAGE MUST BE MANAGED BY OWNER INCLUDING INSTALLATION OF ADDITIONAL DISCHARGE LINES AND INLETS AS REQUIRED. THE BUILDER PROVIDES CAPACITY FOR DISPOSAL OF ROOF COLLECTED STORMWATER ONLY AND TAKES NO RESPONSIBILITY FOR OVERFLOW OR DAMAGE TO PROPERTY IF OWNER ADDS ADDITIONAL DISCHARGE LOADS TO EXISTING STANDARD PROVISIONS.

NOTE TO PLUMBER: ROOF WATER FROM
COLLECTION AREAS

 

TO BE DIVERTED TO WATER TANK.
BALANCE REAR.
COLLECTION AREA = 173.10m²

ALL STORMWATER OVERFLOW OTHER
THAN THAT BEING DIRECTED TO WATER
TANK(S) TO BE DIRECTED REAR.

LEGEND

WATER PUMP IN ACC. WITH LOCAL WATER
AUTHORITY REQUIREMENTS

TANK CAPACITY TO BE MAINTAINED AT
MINIMUM 10% CAPACITY

ALL RECY. WATER TO BE IN APPROVED
COLOUR CODED PIPEWORK (PURPLE)

ALL DRAINAGE LINES ARE FOR ROOF
WATER / WATER TANK DRAINAGE ONLY

SDP



STANDARD DOWNPIPE

CDP



CHARGED DOWNPIPE

RECYCLED COLD
WATER LINE

TANK COLD
WATER LINE

WATER LINE TO
MAIN SUPPLY

NON-CHARGED
STORMWATER I

CHARGED
STORMWATER I

WASHING MACHINE

TOILET

YARD TAP

© 2024 MCDONALD JONES HOMES PTY LTD (ABN 82 003 687 232). THIS DRAWING IS AN ORIGINAL ARTISTIC WORK WITHIN THE MEANING OF THE COPYRIGHT ACT 1968 (THAT), MCDONALD JONES HOMES PTY LTD IS THE OWNER OF COPYRIGHT IN THIS DRAWING. YOU HEREBY AGREE AND UNDERTAKE THAT YOU WILL NOT IN ANY WAY REPRODUCE, COPY, MODIFY, USE OR TAKE ADVANTAGE OF THE DRAWING TO BUILD A HOUSE BASED ON THIS PLAN (WHETHER IN WHOLE OR IN PART) WITHOUT THE PRIOR WRITTEN CONSENT OF MCDONALD JONES HOMES PTY LTD.



SUBJECT TO NCC 2022

(1 OCT 2023 + 7 STAR)

WATERPROOFING & PLUMBING

PLAN ACCEPTANCE BY OWNER

SIGNATURE:

DATE:

SIGNATURE:

DATE:

PLEASE NOTE THAT VARIATIONS WILL NOT BE ACCEPTED
AFTER THIS PLAN ACCEPTANCE HAS BEEN SIGNED



mcDonald jones
FIND YOURSELF AT HOME

SPECIFICATION:	REVISION		DRAWN		CLIENT:		HOUSE DESIGN:		HOUSE CODE:		DO NOT SCALE DRAWINGS. USE FIGURED DIMENSIONS ONLY. CHECK AND VERIFY DIMENSIONS AND LEVELS PRIOR TO THE COMMENCEMENT OF ANY WORK. ALL DISCREPANCIES TO BE REPORTED TO THE DRAFTING OFFICE.
TWO STOREY	5	COLOURS APPLIED	TNG	26/01/2024	CLIFF LAURENS & MARGARETHA HARUNISA TARUNADJAYA		PANORAMA 36		H-MDSPNR20DA		
COPYRIGHT:	6	AMENDED AS PER PCV007	GB0	22/02/2024	ADDRESS:		FACADE DESIGN:		FACADE CODE:		
© 2024	7	AMENDED AS PER PCV08 - HYDRAULIC	LFL	09/04/2024	48 WENTWORTH STREET, CROYDON PARK NSW 2133		PULSE		F-MDSPNR20PLSEA		
	8	AMENDED AS PER PCV009 & PCV011	GB0	03/05/2024	LOT / SECTION / DP:		COUNCIL:		SHEET TITLE:		SHEET No.:
	9	AMENDED AS PER PCV013	LCS	08/05/2024	1 / - / 304988		CANTERBURY BANKSTOWN COUNCIL		WATER MANAGEMENT PLAN (GF)		5 / 24
									SCALES:		607082
									1:125, 1:50		

STORMWATER LAYOUT IS DIAGRAMMATIC ONLY AND NO REPRESENTATION IS MADE AS TO THE AS-BUILT LOCATION OF STORMWATER ASSETS (INCLUDING SURFACE INLET PITS) OR THE TYPE OF SYSTEM USED (CHARGED OR GRAVITY FED). ALL STORMWATER DESIGN IS SUBJECT TO CONTRACTORS RECOMMENDATIONS AND/OR ANY CONSTRUCTION CONSTRAINTS OR CHANGES AT THE DISCRETION OF THE BUILDER. THE STORMWATER SYSTEM IS NOT SUITABLE FOR ANY OTHER USE. ALL SURFACE WATER DRAINAGE MUST BE MANAGED BY OWNER INCLUDING INSTALLATION OF ADDITIONAL DISCHARGE LINES AND INLETS AS REQUIRED. THE BUILDER PROVIDES CAPACITY FOR DISPOSAL OF ROOF COLLECTED STORMWATER ONLY AND TAKES NO RESPONSIBILITY FOR OVERFLOW OR DAMAGE TO PROPERTY IF OWNER ADDS ADDITIONAL DISCHARGE LOADS TO EXISTING STANDARD PROVISIONS.

ALL STORMWATER OVERFLOW OTHER
THAN THAT BEING DIRECTED TO WATER
TANK(S) TO BE DIRECTED REAR.

ALL DRAINAGE LINES ARE FOR ROOF
WATER / WATER TANK DRAINAGE ONLY

SDP

CDP

1

STANDARD DOWNPIPE

CHARGED DOWNPIPE

RECYCLED COLD
WATER LINE

TANK COLD
WATER LINE

WATER LINE TO
MAIN SUPPLY

NON-CHARGED

STORMWATER LINE

CHARGED

STORMWATER LINE

WASHING MACHINE

TOILET

YARD TAP

REFERENCE: SW24114 ISSUE B
DATED: 19.04.2024



WATERPROOFING & PLUMBING

SIGNATURE: _____ DATE: _____

SIGNATURE. _____ DATE. _____

PLEASE NOTE THAT VARIATIONS WILL NOT BE ACCEPTED

AFTER THIS PLAN ACCEPTANCE HAS BEEN SIGNED

© 2024 MCDONALD JONES HOMES PTY LTD (ABN 82 003 687 232). THIS DRAWING IS AN ORIGINAL ARTISTIC WORK WITHIN THE MEANING OF THE COPYRIGHT ACT 1968 (C/TH). MCDONALD JONES HOMES PTY LTD IS THE OWNER OF COPYRIGHT IN THIS DRAWING. YOU HEREBY AGREE AND UNDERTAKE THAT YOU WILL NOT IN ANY WAY REPRODUCE, COPY, MODIFY, USE OR TAKE ADVANTAGE OF THE DRAWING TO BUILD A HOUSE BASED ON THIS PLAN (WHETHER IN WHOLE OR IN PART) WITHOUT THE PRIOR WRITTEN CONSENT OF MCDONALD JONES HOMES PTY LTD.



mcdonald jones

FIND YOURSELF AT HOME

SPECIFICATION:		REVISION	DRAWN	CLIENT:	HOUSE DESIGN:	HOUSE CODE:	DO NOT SCALE DRAWINGS, USE FIGURED DIMENSIONS ONLY. CHECK AND VERIFY DIMENSIONS AND LEVELS PRIOR TO THE COMMENCEMENT OF ANY WORK. ALL DISCREPANCIES TO BE REPORTED TO THE DRAFTING OFFICE.	
TWO STOREY	5	COLOURS APPLIED	TNG 26/01/2024	CLIFF LAURENS & MARGARETHA HARUNISA TARUNADJAYA	PANORAMA 36	H-MDSPNR20DA		
COPYRIGHT:	6	AMENDED AS PER PCV007	GB0 22/02/2024	ADDRESS:	FACADE DESIGN:	FACADE CODE:		
© 2024	7	AMENDED AS PER PCV08 - HYDRAULIC	LFL 09/04/2024	48 WENTWORTH STREET, CROYDON PARK NSW 2133	PULSE	F-MDSPNR20PLSEA		
	8	AMENDED AS PER PCV009 & PCV011	GB0 03/05/2024	LOT / SECTION / DP:	SHEET TITLE:	SHEET No.:		
	9	AMENDED AS PER PCV013	LCS 08/05/2024	1 / - / 304988	COUNCIL:	SCALES:		
				CANTERBURY BANKSTOWN COUNCIL	WATER MANAGEMENT PLAN (FF)	6 / 24	1:125, 1:50	607082

REFER TO SHEET 1 (COVER SHEET) FOR ALL BUILDING INFORMATION REGARDING:

- SUSTAINABILITY REQUIREMENTS
- SITE CLASSIFICATION
- GENERAL BUILDING INFORMATION

ALL MECHANICAL VENTILATION TO BE DISCHARGED TO OUTDOOR AIR AS PER NCC 2022 REQUIREMENTS

FIRE RESISTANT PLASTERBOARD TO BE INSTALLED BEHIND COOKTOP

ALL EXTERIOR STEPS AND LANDINGS BY CUSTOMER UNLESS NOTED OTHERWISE

ALL GROUND FLOOR BULKHEAD AND SQUARE SET OPENING FRAMES TO BE 2455 ABOVE FFL UNLESS NOTED OTHERWISE

ALL GROUND FLOOR INTERNAL DOORS TO BE 2340 HIGH UNLESS NOTED OTHERWISE

REFER TO WINDOW AND DOOR SCHEDULES FOR FULL DETAILS OF ALL WINDOWS AND DOORS. PLEASE NOTE WINDOW AND DOOR SIZES ARE BASED ON MANUFACTURERS SPECIFICATIONS AT DEPOSIT STAGE AND MAY DIFFER SLIGHTLY TO THE SIZES NOMINATED IN THE SCOPE OF WORKS DUE TO MANUFACTURING CHANGES AT THE TIME OF CONSTRUCTION.

FINAL WINDOW AND EXTERIOR DOOR LOCATIONS MAY BE ADJUSTED ON SITE TO SUIT BRICKWORK GAUGE


ALL STAIR TREADS TO PROVIDE A MINIMUM SLIP RESISTANCE TO MEET NCC 2022 REQUIREMENTS

UNLESS NOTED OTHERWISE ALL ROOMS ARE REFERENCED AS FOLLOWS:



LEGEND

HS / WS	HOB SPOUT / WALL SPOUT
	FACE BRICK / COMMON BRICK
	HEBEL
	SOUND INSULATION
AJ	BRICK ARTICULATION JOINT
SDP	STANDARD DOWNSPIPE
CDP	CHARGED DOWNSPIPE
	EXHAUST FAN
L.B.W	LOAD BEARING WALL
	THIS DOOR OPENS FIRST
	INTERCONNECTED SMOKE ALARM
# UC	LIFT OFF HINGE / UNDERCUT
+	WATER POINT
WP	FRIDGE WATER POINT
GAS	GAS BAYONET

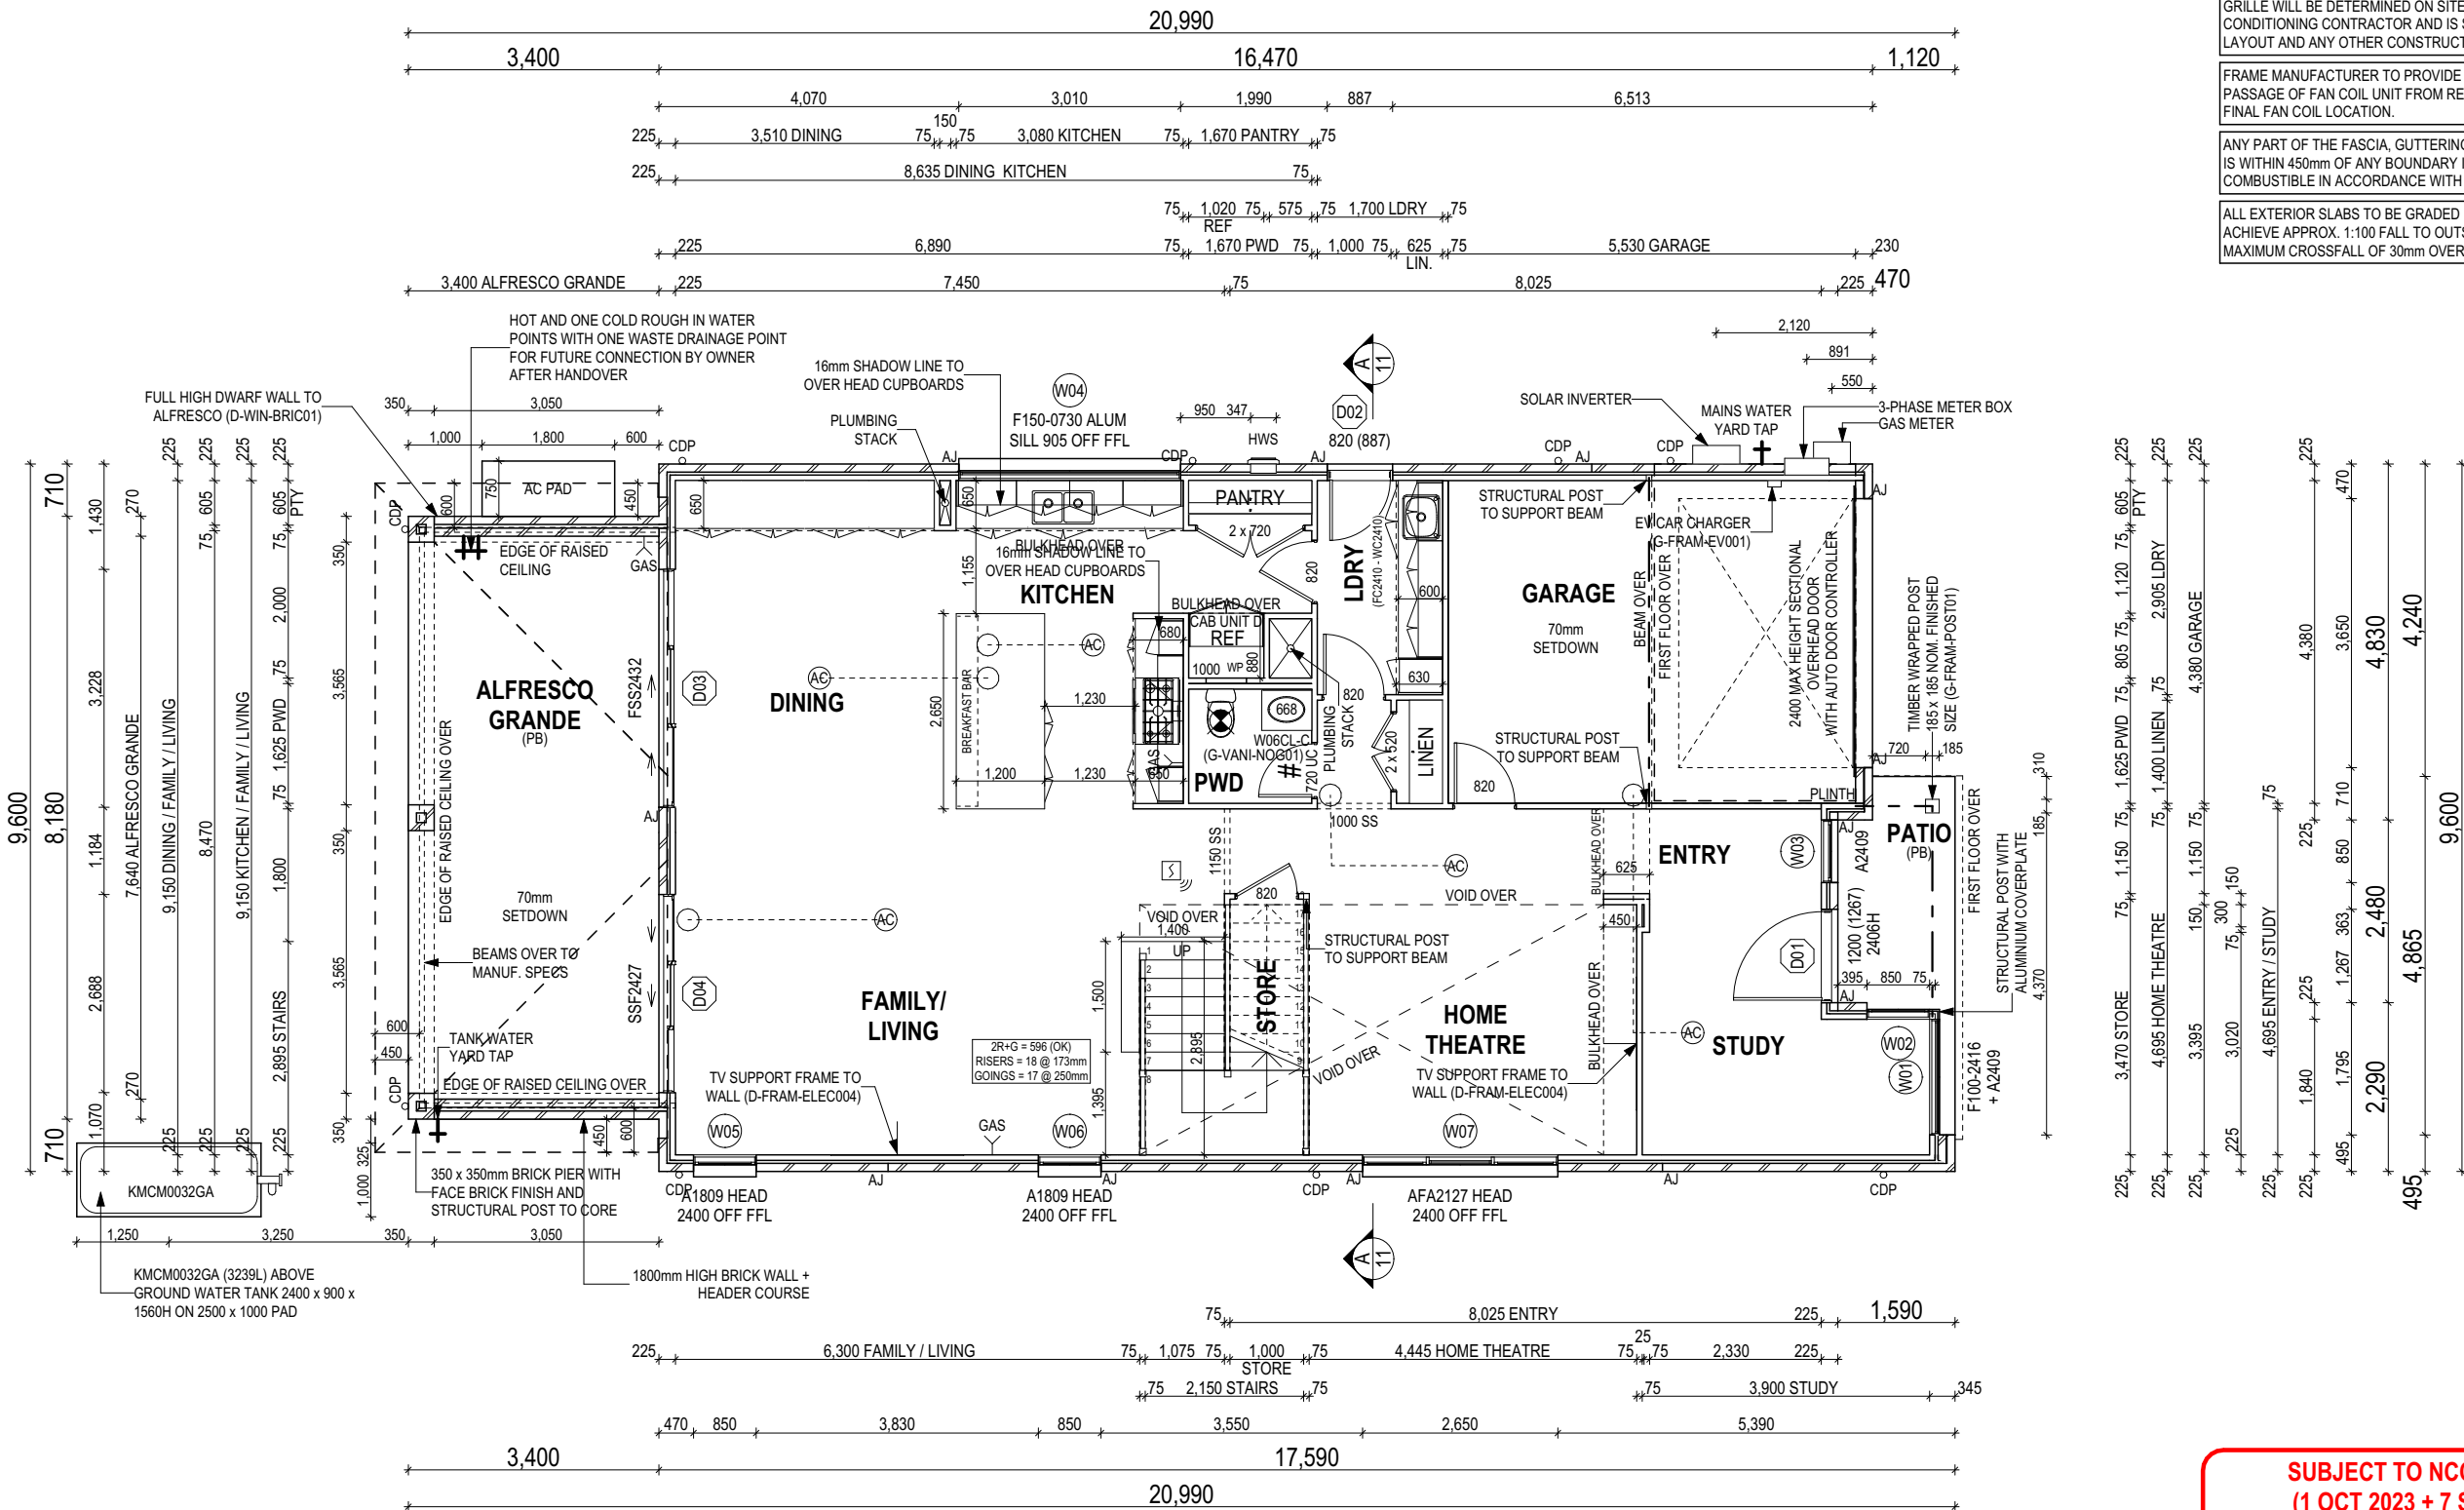

ALL DIMENSIONS ARE FRAME DIMENSIONS

© 2024 MCDONALD JONES HOMES PTY LTD (ABN 82 003 687 232). THIS DRAWING IS AN ORIGINAL ARTISTIC WORK WITHIN THE MEANING OF THE COPYRIGHT ACT 1968 (CTH). MCDONALD JONES HOMES PTY LTD IS THE OWNER OF COPYRIGHT IN THIS DRAWING. YOU HEREBY AGREE AND UNDERTAKE THAT YOU WILL NOT IN ANY WAY REPRODUCE, COPY, MODIFY, USE OR TAKE ADVANTAGE OF THE DRAWING TO BUILD A HOUSE BASED ON THIS PLAN (WHETHER IN WHOLE OR IN PART) WITHOUT THE PRIOR WRITTEN CONSENT OF MCDONALD JONES HOMES PTY LTD.

PROVIDE AND INSTALL 3 PHASE REVERSE CYCLE AIR CONDITIONING SYSTEM. NUMBER AND POSITIONING OF OUTLETS AND THE FINAL LOCATION OF THE RETURN AIR GRILLE WILL BE DETERMINED ON SITE BY THE AIR CONDITIONING CONTRACTOR AND IS SUBJECT TO TRUSS LAYOUT AND ANY OTHER CONSTRUCTION CONSTRAINTS.

FRAME MANUFACTURER TO PROVIDE CLEARANCE FOR PASSAGE OF FAN COIL UNIT FROM RETURN AIR OPENING TO FINAL FAN COIL LOCATION.

ANY PART OF THE FASCIA, GUTTERING OR DOWNPIPE THAT IS WITHIN 450mm OF ANY BOUNDARY IS TO BE NON-COMBUSTIBLE IN ACCORDANCE WITH NCC 2022

ALL EXTERIOR SLABS TO BE GRADED BY CONCRETER TO ACHIEVE APPROX. 1:100 FALL TO OUTSIDE EDGE WITH MAXIMUM CROSSFALL OF 30mm OVER ENTIRE SLAB.

**SUBJECT TO NCC 2022
(1 OCT 2023 + 7 STAR)
WATERPROOFING & PLUMBING**

PLAN ACCEPTANCE BY OWNER

SIGNATURE: _____ DATE: _____

SIGNATURE: _____ DATE: _____

PLEASE NOTE THAT VARIATIONS WILL NOT BE ACCEPTED AFTER THIS PLAN ACCEPTANCE HAS BEEN SIGNED



SPECIFICATION:

TWO STOREY

COPYRIGHT:

© 2024

REVISION

5	COLOURS APPLIED	TNG	26/01/2024
6	AMENDED AS PER PCV007	GB0	22/02/2024
7	AMENDED AS PER PCV08 - HYDRAULIC	LFL	09/04/2024
8	AMENDED AS PER PCV009 & PCV011	GB0	03/05/2024
9	AMENDED AS PER PCV013	LCS	08/05/2024

DRAWN

CLIENT:

CLIFF LAURENS & MARGARETHA HARUNISA TARUNADJAYA

ADDRESS:

48 WENTWORTH STREET, CROYDON PARK NSW 2133

LOT / SECTION / DP:

1 / - / 304988

COUNCIL:

CANTERBURY BANKSTOWN COUNCIL

HOUSE DESIGN:

PANORAMA 36

FACADE DESIGN:

PULSE

SHEET TITLE:

GROUND FLOOR PLAN

SHEET No.:

7 / 24

HOUSE CODE:

H-MDSPNR20DA

FACADE CODE:

F-MDSPNR20PLSEA

SCALES:

1:100

DO NOT SCALE DRAWINGS. USE FIGURED DIMENSIONS ONLY. CHECK AND VERIFY DIMENSIONS AND LEVELS PRIOR TO THE COMMENCEMENT OF ANY WORK. ALL DISCREPANCIES TO BE REPORTED TO THE DRAFTING OFFICE.

607082

REFER TO SHEET 1 (COVER SHEET) FOR ALL BUILDING INFORMATION REGARDING:

- SUSTAINABILITY REQUIREMENTS
- SITE CLASSIFICATION
- GENERAL BUILDING INFORMATION

ALL MECHANICAL VENTILATION TO BE DISCHARGED TO OUTDOOR AIR AS PER NCC 2022 REQUIREMENTS

FIRE RESISTANT PLASTERBOARD TO BE INSTALLED BEHIND COOKTOP

ALL EXTERIOR STEPS AND LANDINGS BY CUSTOMER UNLESS NOTED OTHERWISE

ALL FIRST FLOOR BULKHEAD AND SQUARE SET OPENING FRAMES TO BE 2455 ABOVE FFL UNLESS NOTED OTHERWISE

ALL FIRST FLOOR INTERNAL DOORS TO BE 2340 HIGH UNLESS NOTED OTHERWISE

REFER TO WINDOW AND DOOR SCHEDULES FOR FULL DETAILS OF ALL WINDOWS AND DOORS. PLEASE NOTE WINDOW AND DOOR SIZES ARE BASED ON MANUFACTURERS SPECIFICATIONS AT DEPOSIT STAGE AND MAY DIFFER SLIGHTLY TO THE SIZES NOMINATED IN THE SCOPE OF WORKS DUE TO MANUFACTURING CHANGES AT THE TIME OF CONSTRUCTION.

FINAL WINDOW AND EXTERIOR DOOR LOCATIONS MAY BE ADJUSTED ON SITE TO SUIT BRICKWORK GAUGE

ALL STAIR TREADS TO PROVIDE A MINIMUM SLIP RESISTANCE TO MEET NCC 2022 REQUIREMENTS

FIRST FLOOR WINDOW OPENINGS TO BE RESTRICTED AS REQUIRED BY THE NCC 2022

PROVIDE FLOOR WASTE AND OVERFLOW SPITTERS TO UPPER FLOOR TANKED BALCONIES WHERE APPLICABLE AS PER:

- G-FACA-BALC02 (PFC/BRICKWORK)
- G-FRAM-BALC01 (LIGHTWEIGHT CLADDING)






UNLESS NOTED OTHERWISE ALL ROOMS ARE REFERENCED AS FOLLOWS:



LEGEND

HS / WS	HOB SPOUT / WALL SPOUT
	FACE BRICK / COMMON BRICK
	HEBEL
	SOUND INSULATION
AJ	BRICK ARTICULATION JOINT
SDP	STANDARD DOWNPIPE
CDP	CHARGED DOWNPIPE
	EXHAUST FAN
L.B.W	LOAD BEARING WALL
	THIS DOOR OPENS FIRST
	INTERCONNECTED SMOKE ALARM
# UC	LIFT OFF HINGE / UNDERCUT
+	WATER POINT
WP	FRIDGE WATER POINT
GAS	GAS BAYONET

STAIR VOID DETAIL SCALE: 1:100

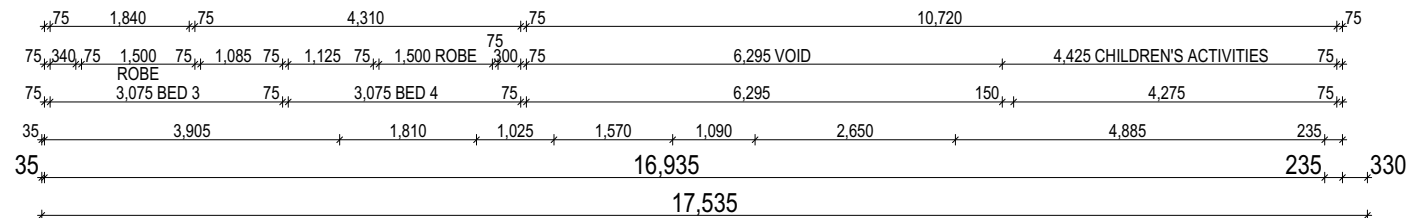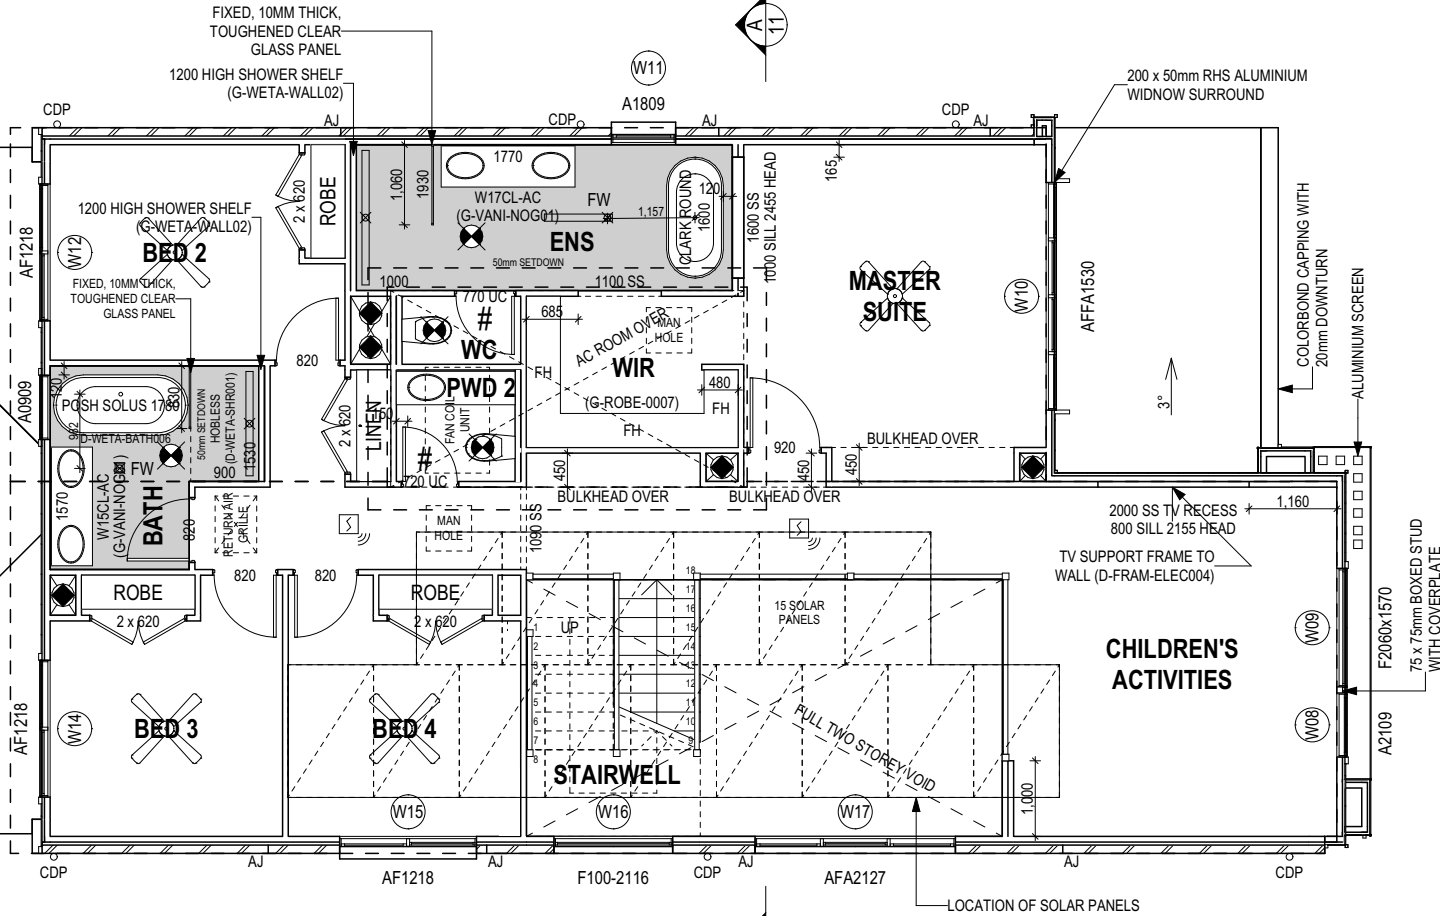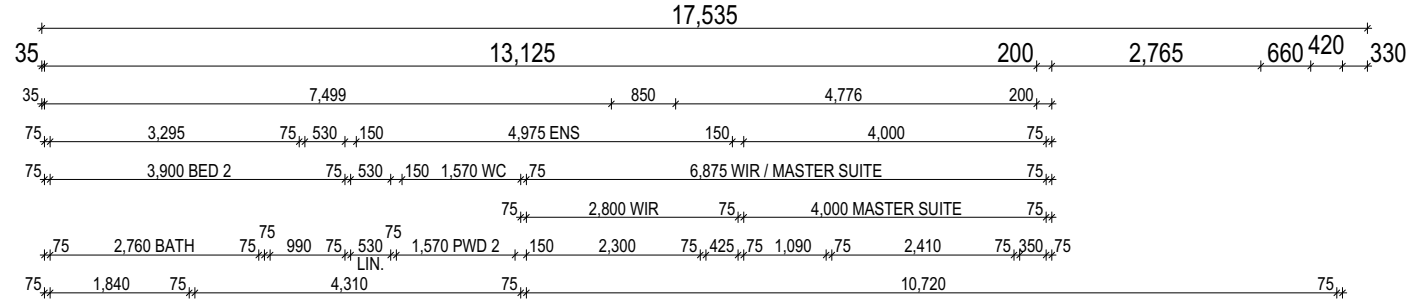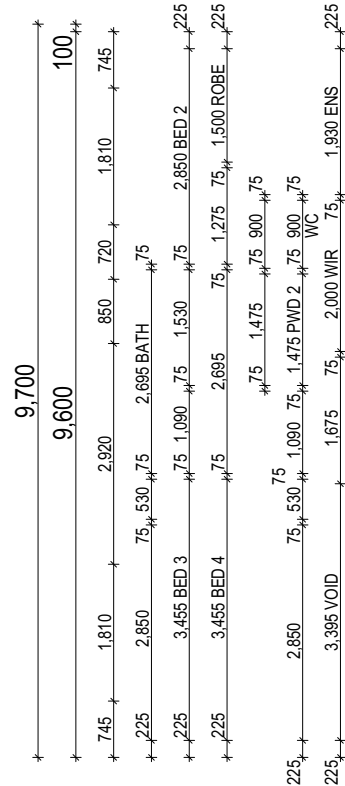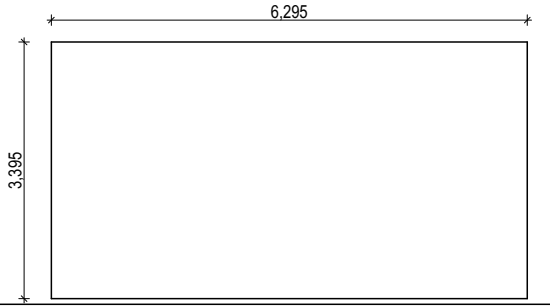

ALL DIMENSIONS ARE FRAME DIMENSIONS

© 2024 MCDONALD JONES HOMES PTY LTD (ABN 82 003 687 232). THIS DRAWING IS AN ORIGINAL ARTISTIC WORK WITHIN THE MEANING OF THE COPYRIGHT ACT 1968 (CTH). MCDONALD JONES HOMES PTY LTD IS THE OWNER OF COPYRIGHT IN THIS DRAWING. YOU HEREBY AGREE AND UNDERTAKE THAT YOU WILL NOT IN ANY WAY REPRODUCE, COPY, MODIFY, USE OR TAKE ADVANTAGE OF THE DRAWING TO BUILD A HOUSE BASED ON THIS PLAN (WHETHER IN WHOLE OR IN PART) WITHOUT THE PRIOR WRITTEN CONSENT OF MCDONALD JONES HOMES PTY LTD.

PROVIDE AND INSTALL 3 PHASE REVERSE CYCLE AIR CONDITIONING SYSTEM. NUMBER AND POSITIONING OF OUTLETS AND THE FINAL LOCATION OF THE RETURN AIR GRILLE WILL BE DETERMINED ON SITE BY THE AIR CONDITIONING CONTRACTOR AND IS SUBJECT TO TRUSS LAYOUT AND ANY OTHER CONSTRUCTION CONSTRAINTS.

FRAME MANUFACTURER TO PROVIDE CLEARANCE FOR PASSAGE OF FAN COIL UNIT FROM RETURN AIR OPENING TO FINAL FAN COIL LOCATION.

ANY PART OF THE FASCIA, GUTTERING OR DOWNPIPE THAT IS WITHIN 450mm OF ANY BOUNDARY IS TO BE NON-COMBUSTIBLE IN ACCORDANCE WITH NCC 2022

ALL EXTERIOR SLABS TO BE GRADED BY CONCRETER TO ACHIEVE APPROX. 1:100 FALL TO OUTSIDE EDGE WITH MAXIMUM CROSSFALL OF 30mm OVER ENTIRE SLAB.



**SUBJECT TO NCC 2022
(1 OCT 2023 + 7 STAR)
WATERPROOFING & PLUMBING**

PLAN ACCEPTANCE BY OWNER


SIGNATURE: _____ DATE: _____

SIGNATURE: _____ DATE: _____


PLEASE NOTE THAT VARIATIONS WILL NOT BE ACCEPTED AFTER THIS PLAN ACCEPTANCE HAS BEEN SIGNED



SPECIFICATION: TWO STOREY	REVISION 5 COLOURS APPLIED	DRAWN TNG 26/01/2024	CLIENT: CLIFF LAURENS & MARGARETHA HARUNISA TARUNADJAYA	HOUSE DESIGN: PANORAMA 36	HOUSE CODE: H-MDSPNR20DA	DO NOT SCALE DRAWINGS. USE FIGURED DIMENSIONS ONLY. CHECK AND VERIFY DIMENSIONS AND LEVELS PRIOR TO THE COMMENCEMENT OF ANY WORK. ALL DISCREPANCIES TO BE REPORTED TO THE DRAFTING OFFICE.
COPYRIGHT: © 2024	6 AMENDED AS PER PCV007	GB0 22/02/2024	ADDRESS: 48 WENTWORTH STREET, CROYDON PARK NSW 2133	FACADE DESIGN: PULSE	FACADE CODE: F-MDSPNR20PLSEA	
	7 AMENDED AS PER PCV08 - HYDRAULIC	LFL 09/04/2024	LOT / SECTION / DP: 1 / - / 304988	SHEET TITLE: FIRST FLOOR PLAN	SHEET No.: 8 / 24	
	8 AMENDED AS PER PCV009 & PCV011	GB0 03/05/2024	COUNCIL: CANTERBURY BANKSTOWN COUNCIL		SCALES: 1:100	
	9 AMENDED AS PER PCV013	LCS 08/05/2024				607082

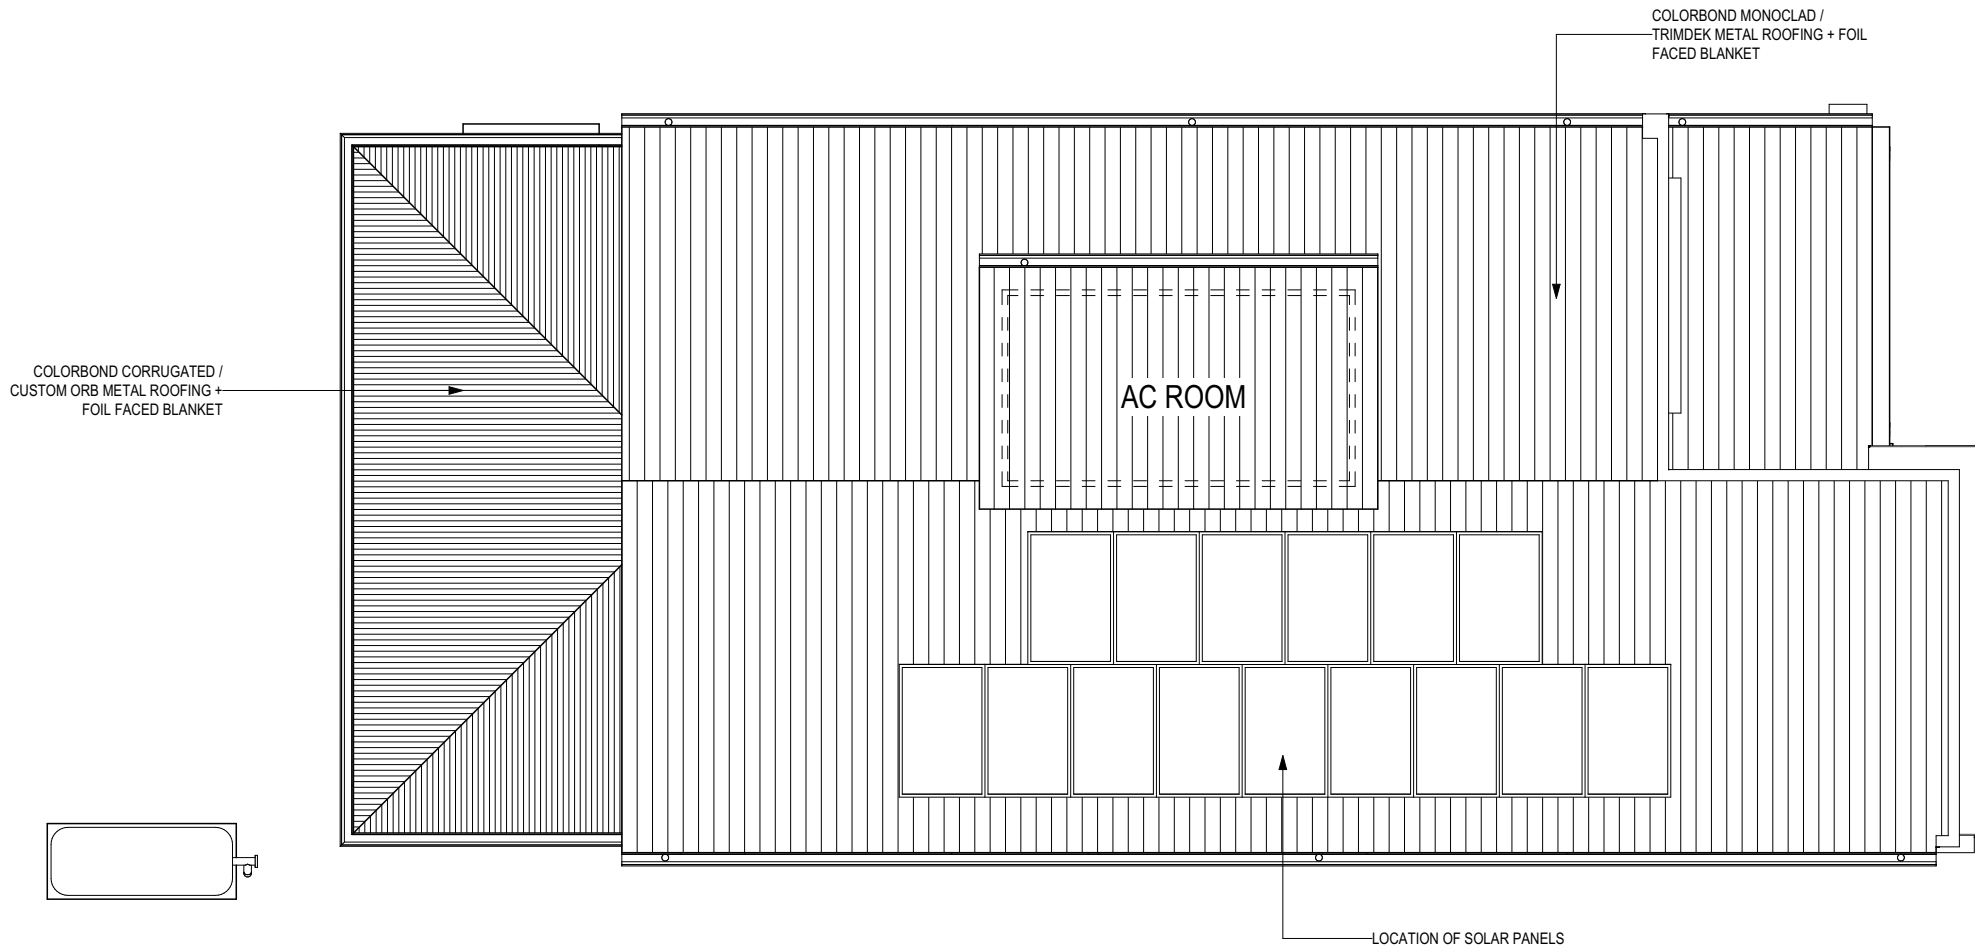

ROOF PLAN
SCALE: 1:100

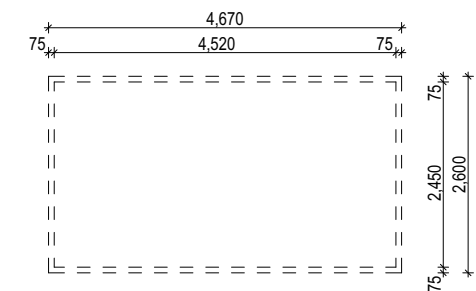

AC ROOM PLAN
SCALE: 1:100

**SUBJECT TO NCC 2022
(1 OCT 2023 + 7 STAR)
WATERPROOFING & PLUMBING**

PLAN ACCEPTANCE BY OWNER

SIGNATURE: _____ DATE: _____

SIGNATURE: _____ DATE: _____

PLEASE NOTE THAT VARIATIONS WILL NOT BE ACCEPTED AFTER THIS PLAN ACCEPTANCE HAS BEEN SIGNED



© 2024 MCDONALD JONES HOMES PTY LTD (ABN 82 003 687 232). THIS DRAWING IS AN ORIGINAL ARTISTIC WORK WITHIN THE MEANING OF THE COPYRIGHT ACT 1968 (CTH). MCDONALD JONES HOMES PTY LTD IS THE OWNER OF COPYRIGHT IN THIS DRAWING. YOU HEREBY AGREE AND UNDERTAKE THAT YOU WILL NOT IN ANY WAY REPRODUCE, COPY, MODIFY, USE OR TAKE ADVANTAGE OF THE DRAWING TO BUILD A HOUSE BASED ON THIS PLAN (WHETHER IN WHOLE OR IN PART) WITHOUT THE PRIOR WRITTEN CONSENT OF MCDONALD JONES HOMES PTY LTD.

 mcdonald jones FIND YOURSELF AT HOME	SPECIFICATION:				CLIENT:	HOUSE DESIGN:		HOUSE CODE:	DO NOT SCALE DRAWINGS, USE FIGURED DIMENSIONS ONLY. CHECK AND VERIFY DIMENSIONS AND LEVELS PRIOR TO THE COMMENCEMENT OF ANY WORK. ALL DISCREPANCIES TO BE REPORTED TO THE DRAFTING OFFICE.
	TWO STOREY	5	COLOURS APPLIED	TNG 26/01/2024	CLIFF LAURENS & MARGARETHA HARUNISA TARUNADJAYA	PANORAMA 36		H-MDSPNR20DA	
	COPYRIGHT:	6	AMENDED AS PER PCV007	GBO 22/02/2024	ADDRESS:	FACADE DESIGN:		FACADE CODE:	
	© 2024	7	AMENDED AS PER PCV08 - HYDRAULIC	LFL 09/04/2024	48 WENTWORTH STREET, CROYDON PARK NSW 2133	PULSE		F-MDSPNR20PLSEA	
		8	AMENDED AS PER PCV009 & PCV011	GBO 03/05/2024	LOT / SECTION / DP:	SHEET TITLE:	SHEET No.:	SCALES:	
		9	AMENDED AS PER PCV013	LCS 08/05/2024	1 / - / 304988	CANTERBURY BANKSTOWN COUNCIL	1 / 1	1:100	607082

EXTERIOR WINDOW & DOOR SCHEDULE 1,2 ASSUME LOOKING FROM OUTSIDE

STOREY	ID	CODE¹	TYPE	ROOM	HEIGHT	WIDTH	PERIMETER	AREA (m²)	FRAME TYPE	BAL RATING	SILL TYPE	ORIENT.	GLAZING AREA (m²)	GLAZING TYPE	ADDITIONAL INFORMATION²
WINDOW															
GROUND FLOOR	W01	F100-2416	FIXED	STUDY	2,360	1,570	7,860	3.71	ALUMINIUM	N/A	NONE	N	3.43	CLEAR, DOUBLE GLAZED, TOUGHENED, DOUBLE LOW-E	CORNER JOINING (POST & COVERPLATE)
GROUND FLOOR	W02	A2409	AWNING	STUDY	2,360	850	6,420	2.01	ALUMINIUM	N/A	NONE	W	1.62	CLEAR, DOUBLE GLAZED, DOUBLE LOW-E	CORNER JOINING (POST & COVERPLATE)
GROUND FLOOR	W03	A2409	AWNING	ENTRY	2,360	850	6,420	2.01	ALUMINIUM	N/A	SNAP HEADER	N	1.62	CLEAR, DOUBLE GLAZED, DOUBLE LOW-E	
GROUND FLOOR	W04	F150-0730	FIXED	KITCHEN	727	3,010	7,474	2.19	ALUMINIUM	N/A	ANGLED	W	1.92	CLEAR, DOUBLE GLAZED, TOUGHENED, LOW-E	
GROUND FLOOR	W05	A1809	AWNING	FAMILY / LIVING	1,800	850	5,300	1.53	ALUMINIUM	N/A	ANGLED	E	1.21	CLEAR, DOUBLE GLAZED, DOUBLE LOW-E	
GROUND FLOOR	W06	A1809	AWNING	FAMILY / LIVING	1,800	850	5,300	1.53	ALUMINIUM	N/A	ANGLED	E	1.21	CLEAR, DOUBLE GLAZED, DOUBLE LOW-E	
GROUND FLOOR	W07	AFA2127	AWNING	HOME THEATRE	2,060	2,650	9,420	5.46	ALUMINIUM	N/A	ANGLED	E	4.54	CLEAR, DOUBLE GLAZED, DOUBLE LOW-E	MP 883-883
FIRST FLOOR	W08	A2109	AWNING	CHILDREN'S ACTIVITIES	2,060	850	5,820	1.75	ALUMINIUM	N/A	NONE	N	1.40	CLEAR, DOUBLE GLAZED, DOUBLE LOW-E	
FIRST FLOOR	W09	F2060x1570	SPECIAL	CHILDREN'S ACTIVITIES	2,060	1,570	7,260	3.23	ALUMINIUM	N/A	NONE	N	2.98	CLEAR, DOUBLE GLAZED, TOUGHENED, DOUBLE LOW-E	
FIRST FLOOR	W10	AFFA1530	AWNING	MASTER SUITE	1,460	3,010	8,940	4.39	ALUMINIUM	N/A	NONE	N	3.56	CLEAR, DOUBLE GLAZED, DOUBLE LOW-E	MP 753-753-753
FIRST FLOOR	W11	A1809	AWNING	ENS	1,800	850	5,300	1.53	ALUMINIUM	N/A	ANGLED	W	1.21	SATINLITE, DOUBLE GLAZED, TOUGHENED	
FIRST FLOOR	W12	AF1218	AWNING	BED 2	1,200	1,810	6,020	2.17	ALUMINIUM	N/A	NONE	S	1.77	CLEAR, DOUBLE GLAZED, DOUBLE LOW-E	MP 905
FIRST FLOOR	W13	A0909	AWNING	BATH	860	850	3,420	0.73	ALUMINIUM	N/A	NONE	S	0.53	SATINLITE, DOUBLE GLAZED, TOUGHENED	
FIRST FLOOR	W14	AF1218	AWNING	BED 3	1,200	1,810	6,020	2.17	ALUMINIUM	N/A	NONE	S	1.77	CLEAR, DOUBLE GLAZED, DOUBLE LOW-E	MP 905
FIRST FLOOR	W15	AF1218	AWNING	BED 4	1,200	1,810	6,020	2.17	ALUMINIUM	N/A	ANGLED	E	1.77	CLEAR, DOUBLE GLAZED, DOUBLE LOW-E	MP 905
FIRST FLOOR	W16	F100-2116	FIXED	STAIRWELL	2,060	1,570	7,260	3.23	ALUMINIUM	N/A	SNAP HEADER	E	2.98	CLEAR, DOUBLE GLAZED, TOUGHENED, DOUBLE LOW-E	
FIRST FLOOR	W17	AFA2127	AWNING	VOID	2,060	2,650	9,420	5.46	ALUMINIUM	N/A	SNAP HEADER	E	4.54	CLEAR, DOUBLE GLAZED, TOUGHENED, DOUBLE LOW-E	MP 883-883
								45.27					38.06		
DOOR															
GROUND FLOOR	D01	1200	SWINGING	STUDY	2,406	1,267	7,346	3.05	TIMBER	N/A	SNAP HEADER	N	---	DOOR(S): N/A - SIDELIGHT(S): N/A	LEAF SIZE: 2340 x 1200mm
GROUND FLOOR	D02	820	SWINGING	LDRY	2,106	887	5,986	1.87	TIMBER	N/A	SNAP HEADER	W	---	DOOR(S): CLEAR - SIDELIGHT(S): N/A	LEAF SIZE: 2040 x 820mm
GROUND FLOOR	D03	FSS2432	STACKER	DINING	2,400	3,228	11,256	7.75	ALUMINIUM	N/A	SNAP HEADER	S	6.94	CLEAR, DOUBLE GLAZED, TOUGHENED, DOUBLE LOW-E	
GROUND FLOOR	D04	SSF2427	STACKER	FAMILY / LIVING	2,400	2,688	10,176	6.45	ALUMINIUM	N/A	SNAP HEADER	S	5.70	CLEAR, DOUBLE GLAZED, TOUGHENED, DOUBLE LOW-E	
								19.12					12.64		
								64.39					50.70		

INTERIOR WINDOW & DOOR SCHEDULE

STOREY	QTY	CODE	TYPE	HEIGHT	WIDTH	GLAZING TYPE	ADDITIONAL INFORMATION
DOOR							
GROUND FLOOR	1	1000 SS	SQUARE SET OPENING	2,455	1,000	N/A	
GROUND FLOOR	1	1150 SS	SQUARE SET OPENING	2,455	1,150	N/A	
GROUND FLOOR	1	2 x 520	SWINGING	2,340	1,040	N/A	
GROUND FLOOR	1	2 x 720	SWINGING	2,340	1,440	N/A	
GROUND FLOOR	1	720 UC	SWINGING	2,340	720	N/A	20mm UNDERCUT, LIFT-OFF HINGES
GROUND FLOOR	3	820	SWINGING	2,340	820	N/A	
GROUND FLOOR	1	820	SWINGING	2,040	820	N/A	
FIRST FLOOR	1	1090 SS	SQUARE SET OPENING	2,455	1,090	N/A	
FIRST FLOOR	1	1100 SS	SQUARE SET OPENING	2,455	1,100	N/A	
FIRST FLOOR	4	2 x 620	SWINGING	2,340	1,240	N/A	
FIRST FLOOR	1	720 UC	SWINGING	2,340	720	N/A	20mm UNDERCUT, LIFT-OFF HINGES
FIRST FLOOR	1	770 UC	SWINGING	2,340	770	N/A	20mm UNDERCUT, LIFT-OFF HINGES
FIRST FLOOR	4	820	SWINGING	2,340	820	N/A	
FIRST FLOOR	1	920	SWINGING	2,340	920	N/A	

REFER TO SHEET 1 (COVER SHEET) FOR ALL BUILDING INFORMATION REGARDING:

- SUSTAINABILITY REQUIREMENTS
- SITE CLASSIFICATION
- GENERAL BUILDING INFORMATION

© 2024 MCDONALD JONES HOMES PTY LTD (ABN 82 003 687 232). THIS DRAWING IS AN ORIGINAL ARTISTIC WORK WITHIN THE MEANING OF THE COPYRIGHT ACT 1968 (CTH). MCDONALD JONES HOMES PTY LTD IS THE OWNER OF COPYRIGHT IN THIS DRAWING. YOU HEREBY AGREE AND UNDERTAKE THAT YOU WILL NOT IN ANY WAY REPRODUCE, COPY, MODIFY, USE OR TAKE ADVANTAGE OF THE DRAWING TO BUILD A HOUSE BASED ON THIS PLAN (WHETHER IN WHOLE OR IN PART) WITHOUT THE PRIOR WRITTEN CONSENT OF MCDONALD JONES HOMES PTY LTD.



SUBJECT TO NCC 2022
(1 OCT 2023 + 7 STAR)
WATERPROOFING & PLUMBING

PLAN ACCEPTANCE BY OWNER

SIGNATURE: _____ DATE: _____

SIGNATURE: _____ DATE: _____


PLEASE NOTE THAT VARIATIONS WILL NOT BE ACCEPTED AFTER THIS PLAN ACCEPTANCE HAS BEEN SIGNED

PICTURE, TV RECESS AND SS WINDOW OPENINGS


QTY	TYPE	HEIGHT	WIDTH	AREA (m²)
1	SS WINDOW OPENING	1,455	1,600	2.33
1	TV RECESS	1,355	2,000	2.71




SPECIFICATION:		REVISION		DRAWN		CLIENT:		HOUSE DESIGN:		HOUSE CODE:		DO NOT SCALE DRAWINGS. USE FIGURED DIMENSIONS ONLY. CHECK AND VERIFY DIMENSIONS AND LEVELS PRIOR TO THE COMMENCEMENT OF ANY WORK. ALL DISCREPANCIES TO BE REPORTED TO THE DRAFTING OFFICE.
TWO STOREY		5	COLOURS APPLIED	TNG	26/01/2024	CLIFF LAURENS & MARGARETHA HARUNISA TARUNADJAYA		PANORAMA 36		H-MDSPNR20DA		
COPYRIGHT:		6	AMENDED AS PER PCV007	GB0	22/02/2024	ADDRESS:		FACADE DESIGN:		FACADE CODE:		
© 2024		7	AMENDED AS PER PCV08 - HYDRAULIC	LFL	09/04/2024	48 WENTWORTH STREET, CROYDON PARK NSW 2133		PULSE		F-MDSPNR20PLSEA		
		8	AMENDED AS PER PCV009 & PCV011	GB0	03/05/2024	LOT / SECTION / DP:		SHEET TITLE:		SHEET No.:		
		9	AMENDED AS PER PCV013	LCS	08/05/2024	1 / - / 304988		COUNCIL:		CANTERBURY BANKSTOWN COUNCIL		
								WINDOW & DOOR SCHEDULES		10 / 24		
										SCALES:		607082

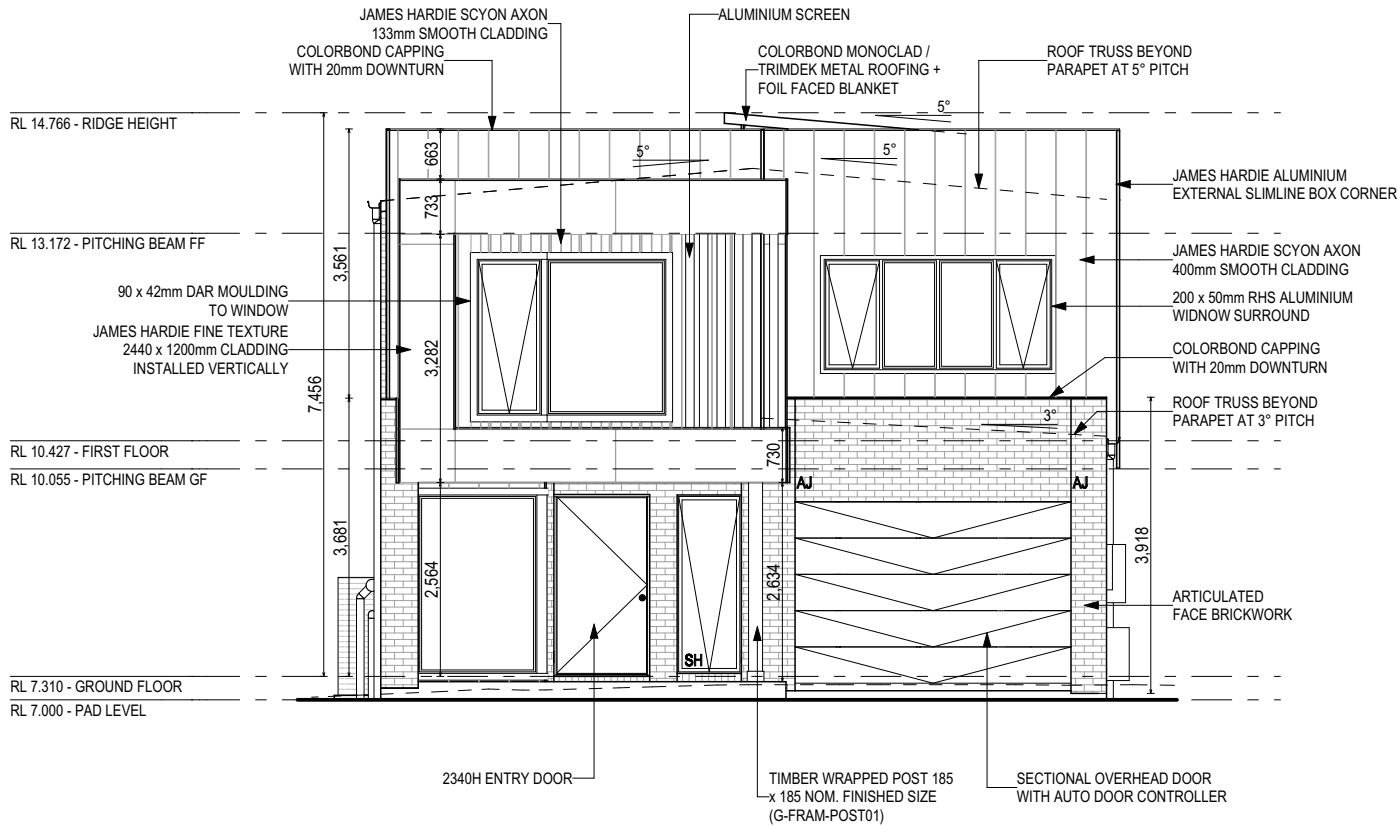

FRONT ELEVATION (NORTH)
SCALE: 1:100

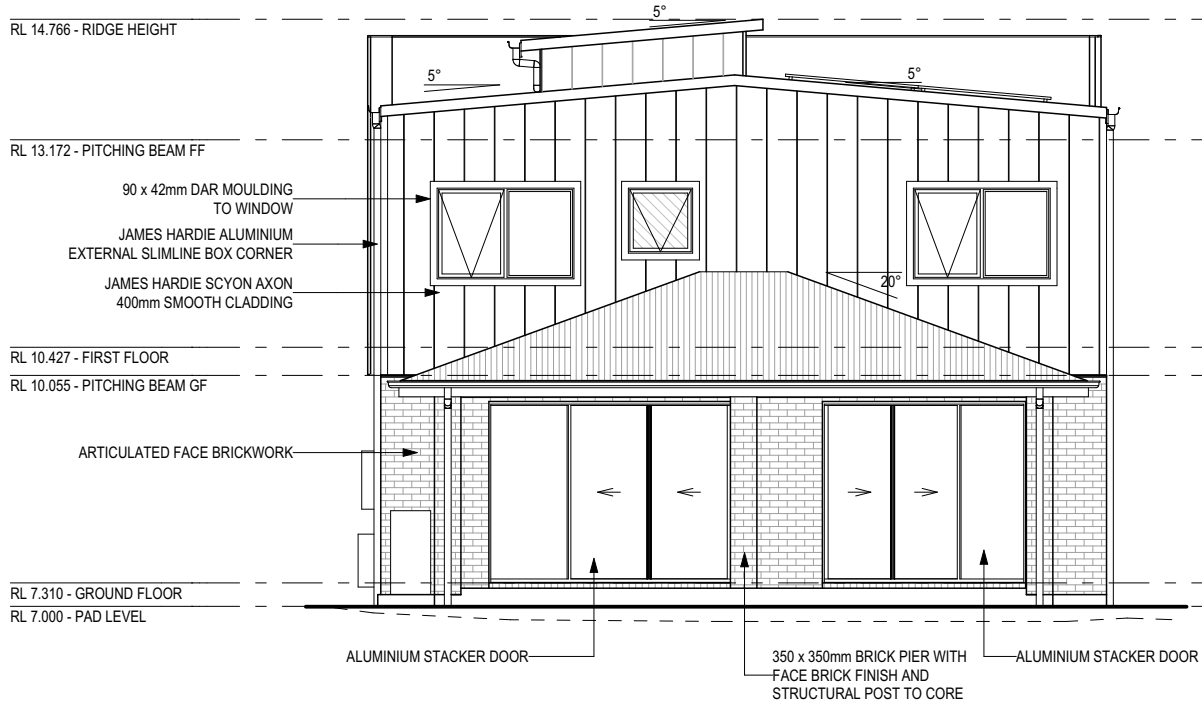

REAR ELEVATION (SOUTH)
SCALE: 1:100

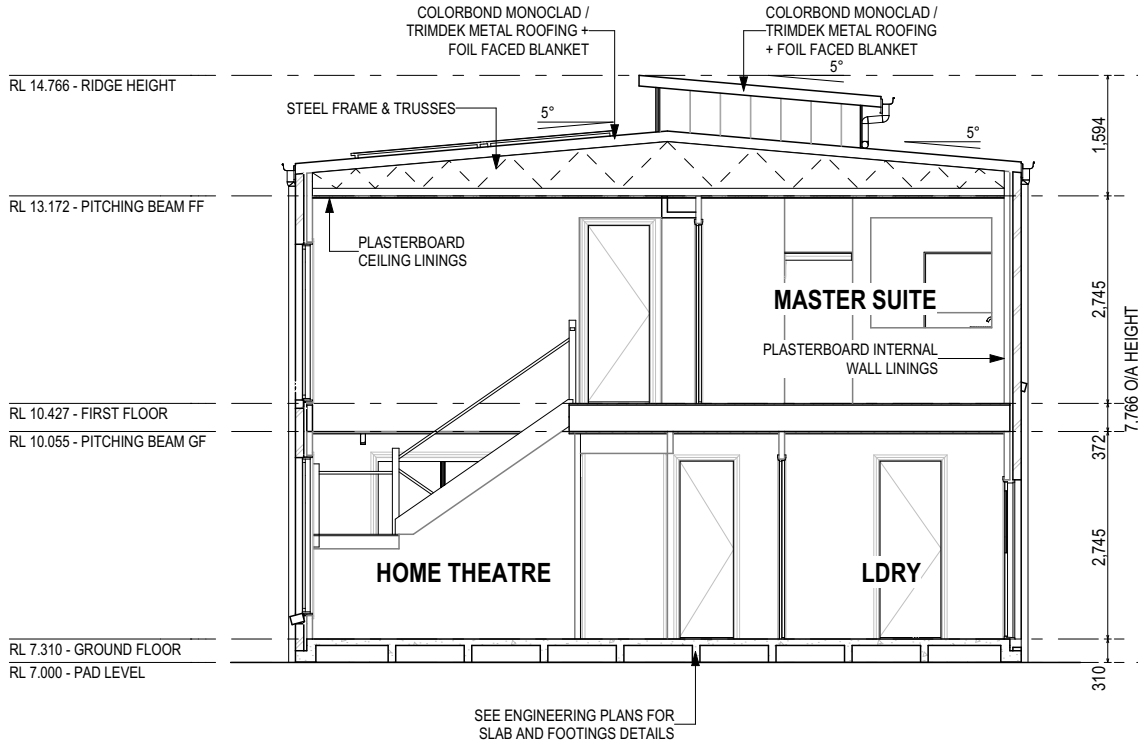


SECTION A-A
SCALE: 1:100




SUBJECT TO NCC 2022
(1 OCT 2023 + 7 STAR)
WATERPROOFING & PLUMBING

GLASS TYPE LEGEND

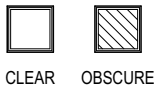

WINDOW TYPE LEGEND

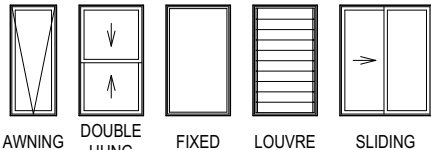

PLAN ACCEPTANCE BY OWNER

SIGNATURE: DATE:


SIGNATURE: DATE:


PLEASE NOTE THAT VARIATIONS WILL NOT BE ACCEPTED AFTER THIS PLAN ACCEPTANCE HAS BEEN SIGNED

© 2024 MCDONALD JONES HOMES PTY LTD (ABN 82 003 687 232). THIS DRAWING IS AN ORIGINAL ARTISTIC WORK WITHIN THE MEANING OF THE COPYRIGHT ACT 1968 (CTH). MCDONALD JONES HOMES PTY LTD IS THE OWNER OF COPYRIGHT IN THIS DRAWING. YOU HEREBY AGREE AND UNDERTAKE THAT YOU WILL NOT IN ANY WAY REPRODUCE, COPY, MODIFY, USE OR TAKE ADVANTAGE OF THE DRAWING TO BUILD A HOUSE BASED ON THIS PLAN (WHETHER IN WHOLE OR IN PART) WITHOUT THE PRIOR WRITTEN CONSENT OF MCDONALD JONES HOMES PTY LTD.




SPECIFICATION: TWO STOREY COPYRIGHT: © 2024	REVISION		DRAWN	CLIENT: CLIFF LAURENS & MARGARETHA HARUNISA TARUNADJAYA ADDRESS: 48 WENTWORTH STREET, CROYDON PARK NSW 2133 LOT / SECTION / DP: 1 / - / 304988 COUNCIL: CANTERBURY BANKSTOWN COUNCIL	HOUSE DESIGN: PANORAMA 36 FACADE DESIGN: PULSE SHEET TITLE: ELEVATIONS / SECTION	HOUSE CODE: H-MDSPNR20DA FACADE CODE: F-MDSPNR20PLSEA SHEET No.: 11 / 24 SCALES: 1:100	DO NOT SCALE DRAWINGS. USE FIGURED DIMENSIONS ONLY. CHECK AND VERIFY DIMENSIONS AND LEVELS PRIOR TO THE COMMENCEMENT OF ANY WORK. ALL DISCREPANCIES TO BE REPORTED TO THE DRAFTING OFFICE. 607082
	5	COLOURS APPLIED	TNG	26/01/2024			
	6	AMENDED AS PER PCV007	GBO	22/02/2024			
	7	AMENDED AS PER PCV08 - HYDRAULIC	LFL	09/04/2024			
	8	AMENDED AS PER PCV009 & PCV011	GBO	03/05/2024			
	9	AMENDED AS PER PCV013	LCS	08/05/2024			

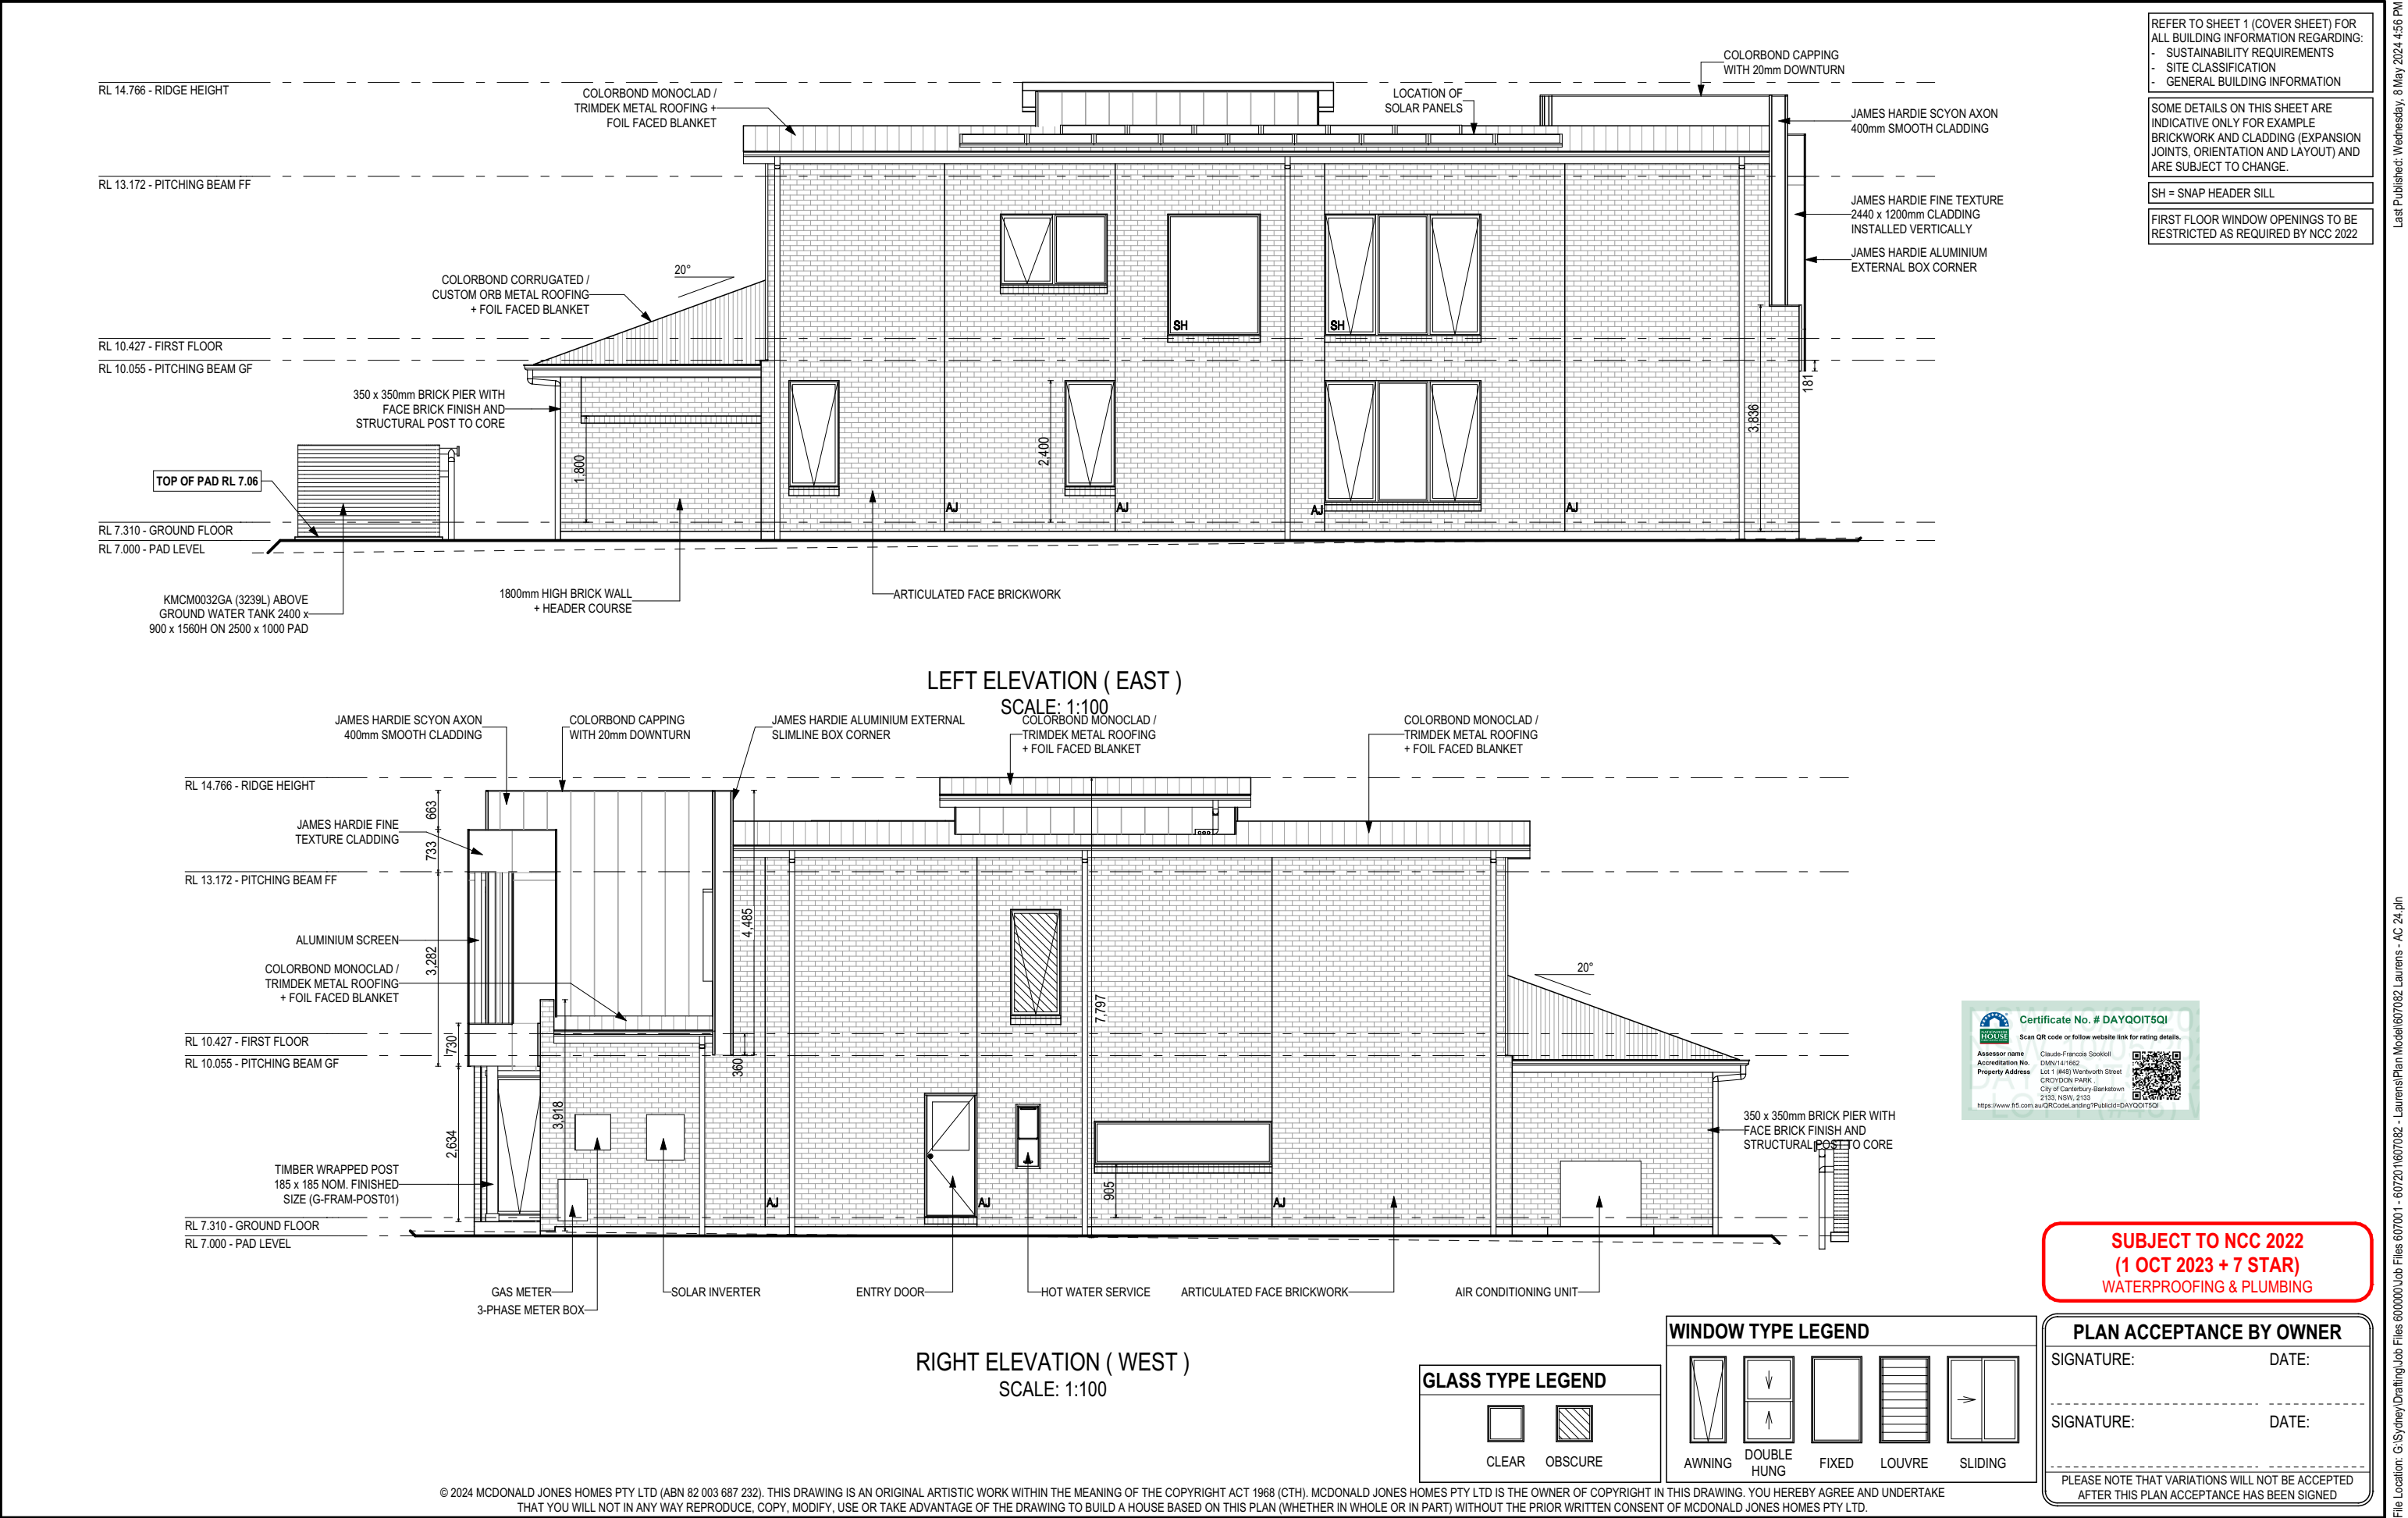


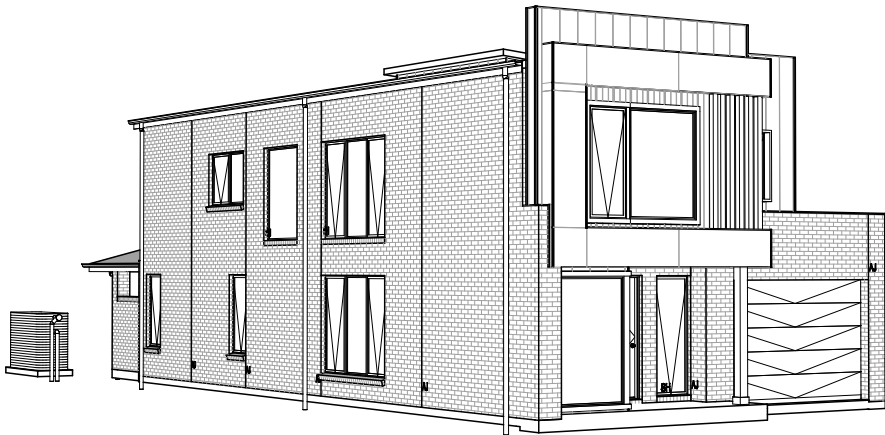


FRONT LEFT

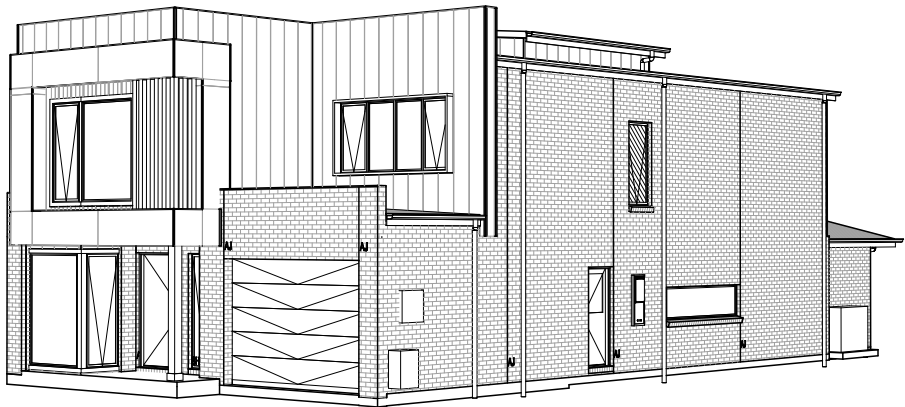

FRONT RIGHT

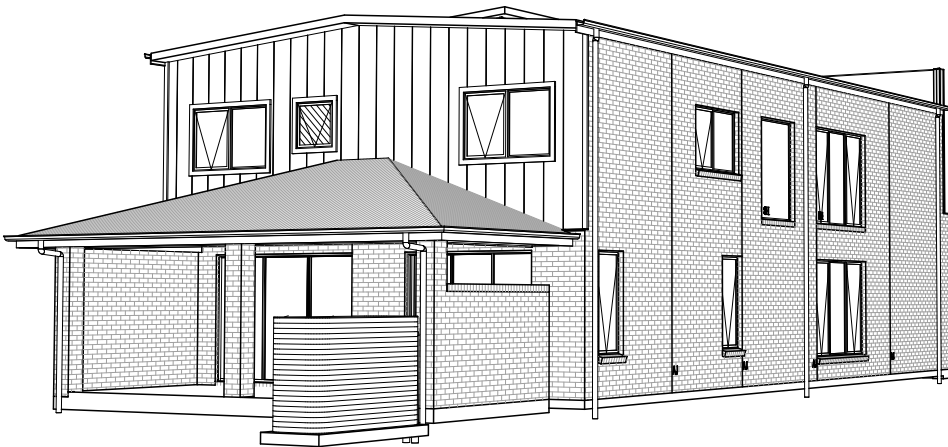

REAR LEFT

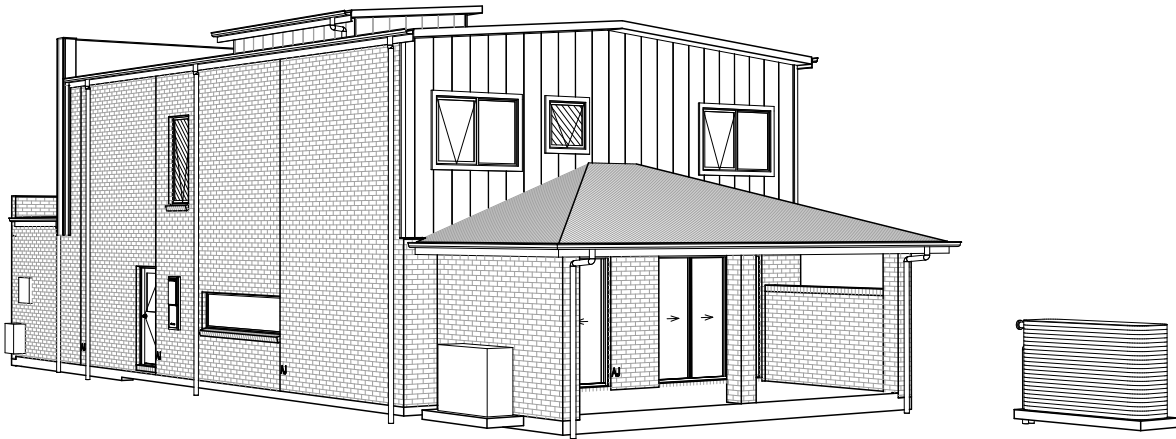


REAR RIGHT




© 2024 MCDONALD JONES HOMES PTY LTD (ABN 82 003 687 232). THIS DRAWING IS AN ORIGINAL ARTISTIC WORK WITHIN THE MEANING OF THE COPYRIGHT ACT 1968 (CTH). MCDONALD JONES HOMES PTY LTD IS THE OWNER OF COPYRIGHT IN THIS DRAWING. YOU HEREBY AGREE AND UNDERTAKE THAT YOU WILL NOT IN ANY WAY REPRODUCE, COPY, MODIFY, USE OR TAKE ADVANTAGE OF THE DRAWING TO BUILD A HOUSE BASED ON THIS PLAN (WHETHER IN WHOLE OR IN PART) WITHOUT THE PRIOR WRITTEN CONSENT OF MCDONALD JONES HOMES PTY LTD.


 mcdonald jones FIND YOURSELF AT HOME	SPECIFICATION: TWO STOREY		REVISION	DRAWN	CLIENT:	HOUSE DESIGN:		HOUSE CODE:	DO NOT SCALE DRAWINGS. USE FIGURED DIMENSIONS ONLY. CHECK AND VERIFY DIMENSIONS AND LEVELS PRIOR TO THE COMMENCEMENT OF ANY WORK. ALL DISCREPANCIES TO BE REPORTED TO THE DRAFTING OFFICE. 607082
	COPYRIGHT: © 2024	5	COLOURS APPLIED	TNG 26/01/2024	CLIFF LAURENS & MARGARETHA HARUNISA TARUNADJAYA	PANORAMA 36		H-MDSPNR20DA	
		6	AMENDED AS PER PCV007	GBO 22/02/2024	ADDRESS:	FACADE DESIGN:		FACADE CODE:	
		7	AMENDED AS PER PCV08 - HYDRAULIC	LFL 09/04/2024	48 WENTWORTH STREET, CROYDON PARK NSW 2133	PULSE		F-MDSPNR20PLSEA	
		8	AMENDED AS PER PCV009 & PCV011	GBO 03/05/2024	LOT / SECTION / DP:	SHEET TITLE:	SHEET No.:	SCALES:	
		9	AMENDED AS PER PCV013	LCS 08/05/2024	1 / - / 304988	HOUSE EXTERIOR 3D VIEWS	13 / 24		
					COUNCIL:	CANTERBURY BANKSTOWN COUNCIL			

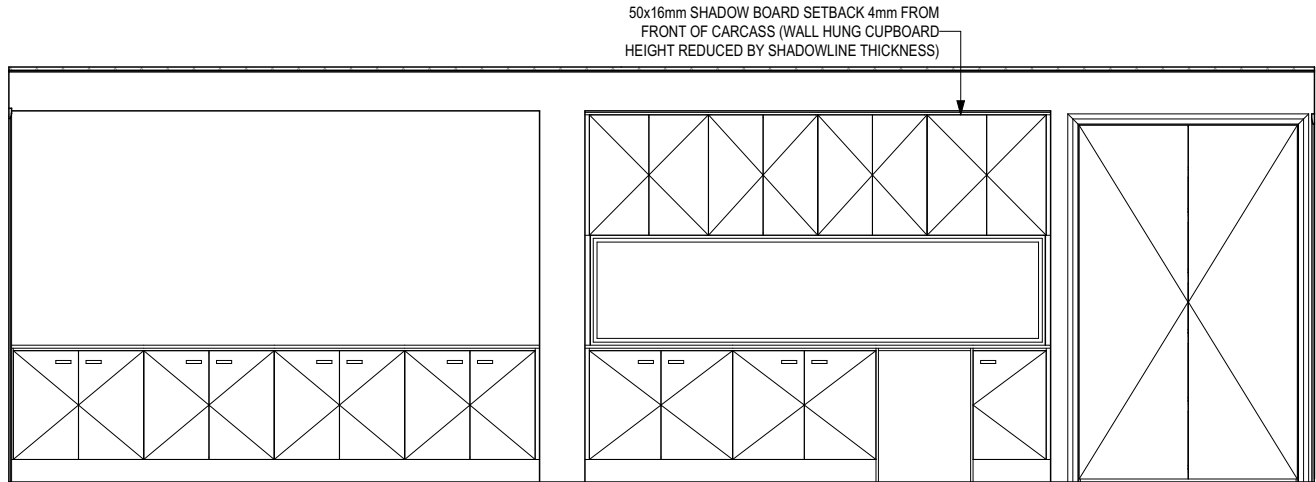


ELEVATION A
SCALE: 1:50

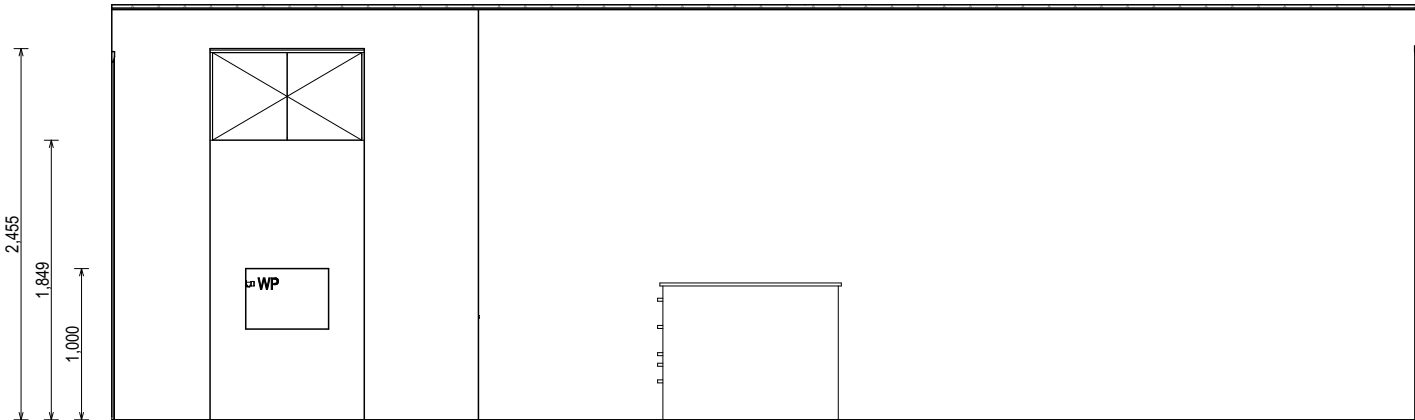


ELEVATION C
SCALE: 1:50

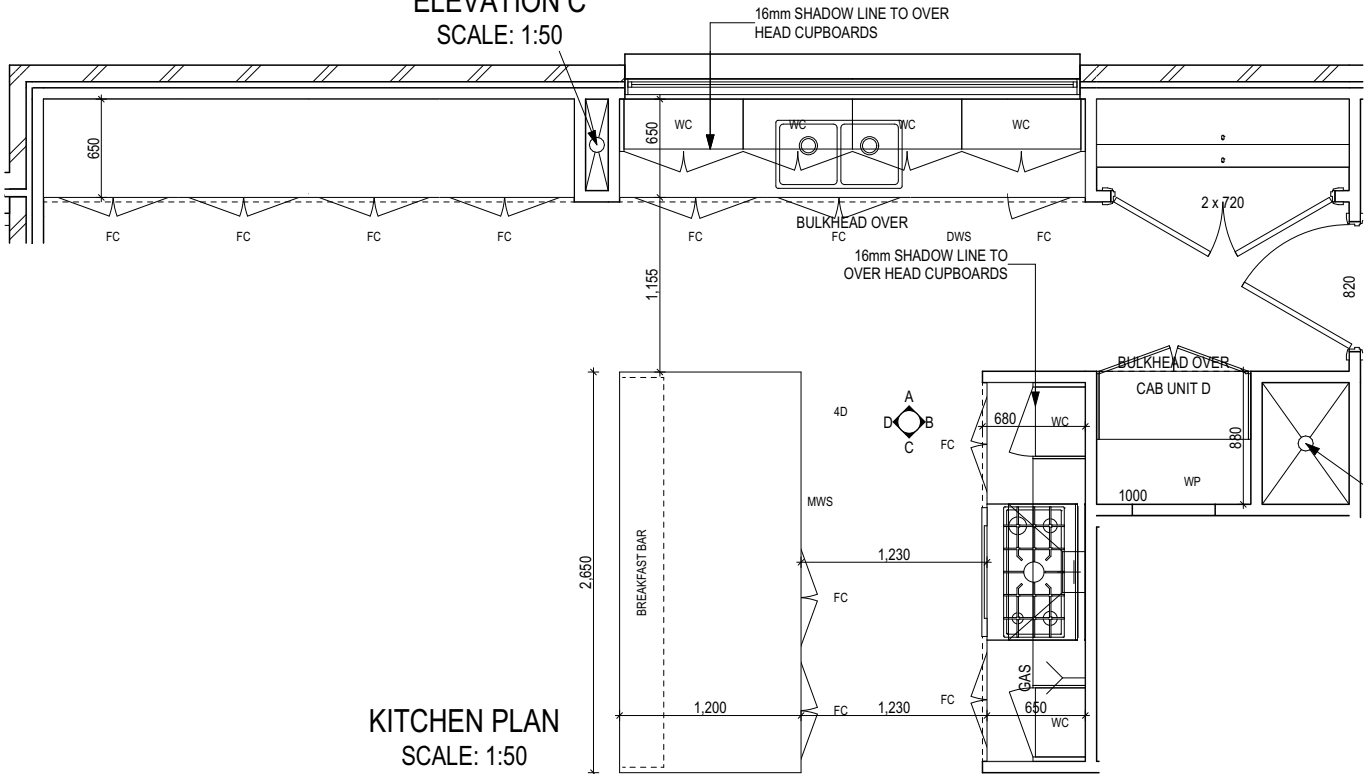



KITCHEN PLAN
SCALE: 1:50

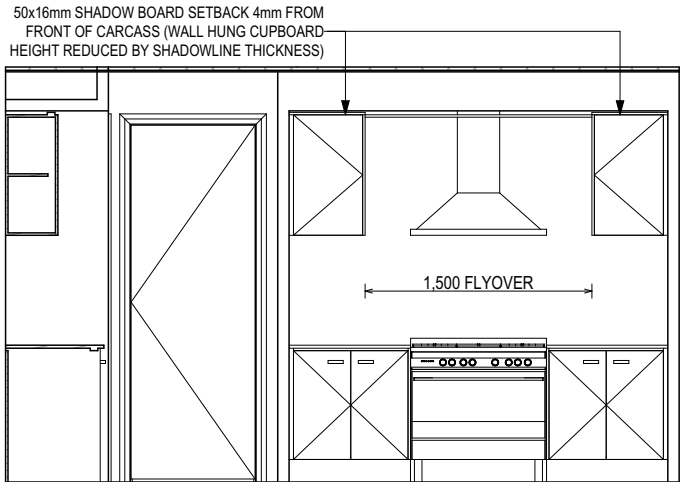

ELEVATION B
SCALE: 1:50

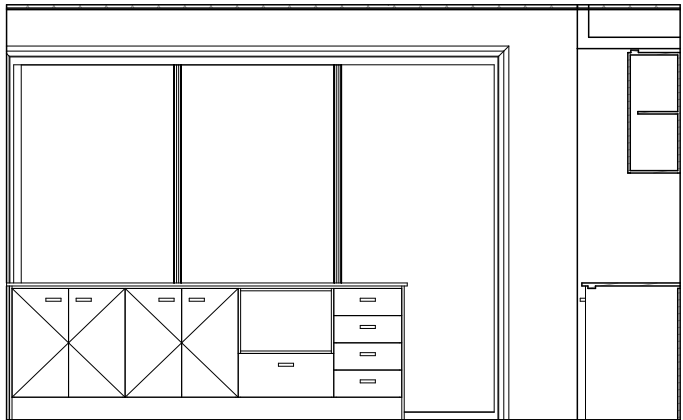

ELEVATION D
SCALE: 1:50

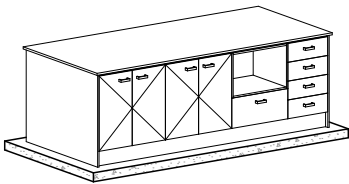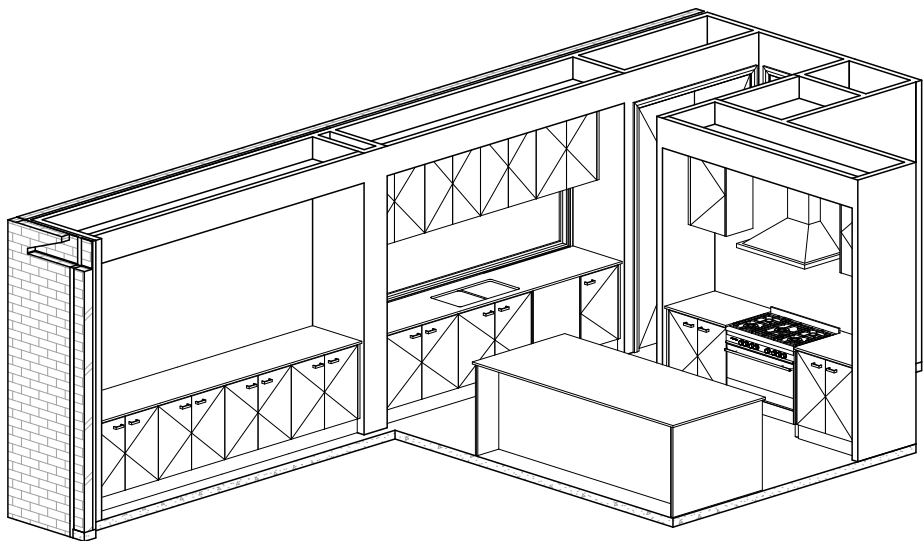

**SUBJECT TO NCC 2022
(1 OCT 2023 + 7 STAR)
WATERPROOFING & PLUMBING**

PLAN ACCEPTANCE BY OWNER

SIGNATURE: DATE:

SIGNATURE: DATE:

PLEASE NOTE THAT VARIATIONS WILL NOT BE ACCEPTED AFTER THIS PLAN ACCEPTANCE HAS BEEN SIGNED

ALL DIMENSIONS ARE FRAME DIMENSIONS

© 2024 MCDONALD JONES HOMES PTY LTD (ABN 82 003 687 232). THIS DRAWING IS AN ORIGINAL ARTISTIC WORK WITHIN THE MEANING OF THE COPYRIGHT ACT 1968 (CTH). MCDONALD JONES HOMES PTY LTD IS THE OWNER OF COPYRIGHT IN THIS DRAWING. YOU HEREBY AGREE AND UNDERTAKE THAT YOU WILL NOT IN ANY WAY REPRODUCE, COPY, MODIFY, USE OR TAKE ADVANTAGE OF THE DRAWING TO BUILD A HOUSE BASED ON THIS PLAN (WHETHER IN WHOLE OR IN PART) WITHOUT THE PRIOR WRITTEN CONSENT OF MCDONALD JONES HOMES PTY LTD.



SPECIFICATION: TWO STOREY COPYRIGHT: © 2024	REVISION		DRAWN		CLIENT: CLIFF LAURENS & MARGARETHA HARUNISA TARUNADJAYA ADDRESS: 48 WENTWORTH STREET, CROYDON PARK NSW 2133 LOT / SECTION / DP: 1 / - / 304988 COUNCIL: CANTERBURY BANKSTOWN COUNCIL	HOUSE DESIGN: PANORAMA 36 FACADE DESIGN: PULSE SHEET TITLE: KITCHEN DETAILS	HOUSE CODE: H-MDSPNR20DA FACADE CODE: F-MDSPNR20PLSEA SHEET No.: 14 / 24	DO NOT SCALE DRAWINGS. USE FIGURED DIMENSIONS ONLY. CHECK AND VERIFY DIMENSIONS AND LEVELS PRIOR TO THE COMMENCEMENT OF ANY WORK. ALL DISCREPANCIES TO BE REPORTED TO THE DRAFTING OFFICE. 607082
	5	COLOURS APPLIED	TNG	26/01/2024				
	6	AMENDED AS PER PCV007	GB0	22/02/2024				
	7	AMENDED AS PER PCV08 - HYDRAULIC	LFL	09/04/2024				
	8	AMENDED AS PER PCV009 & PCV011	GB0	03/05/2024				
	9	AMENDED AS PER PCV013	LCS	08/05/2024				


REFER TO SHEET 1 (COVER SHEET) FOR ALL BUILDING INFORMATION REGARDING:

- SUSTAINABILITY REQUIREMENTS
- SITE CLASSIFICATION
- GENERAL BUILDING INFORMATION


DETAILS DEPICTED ON THIS SHEET ARE A REPRESENTATION ONLY

LEGEND


- RSHR RAIL SHOWER
- ROSE SHOWER ROSE
- ELBW SHOWER ELBOW CONNECTION
- MIX MIXER TAP
- HT HOT TAP
- CT COLD TAP
- HS HOB SPOUT
- WS WALL SPOUT
- SC STOP COCK
- TRH TOILET ROLL HOLDER
- TR-S TOWEL RAIL - SINGLE
- TR-D TOWEL RAIL - DOUBLE
- TL TOWEL LADDER
- TH TOWEL HOLDER
- TR TOWEL RACK
- TMB TUMBLER HOLDER
- RNG TOWEL RING
- RH ROBE HOOK
- SHLF SHELF
- SR SHAMPOO RECESS
- SOAP SOAP HOLDER

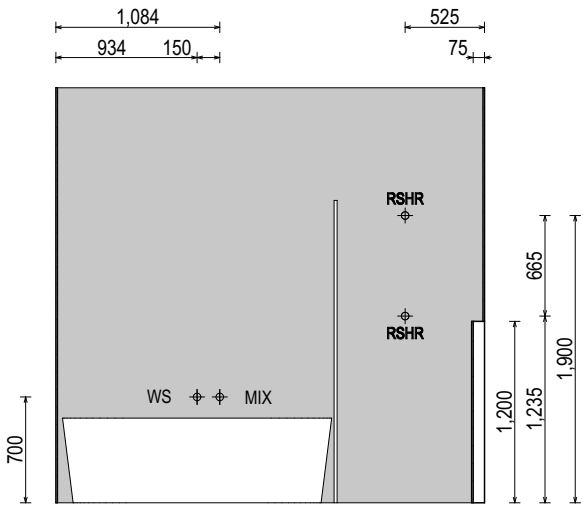


ELEVATION A
SCALE: 1:50

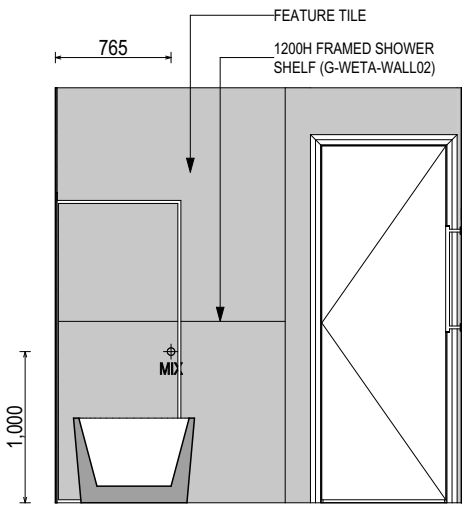


ELEVATION B
SCALE: 1:50

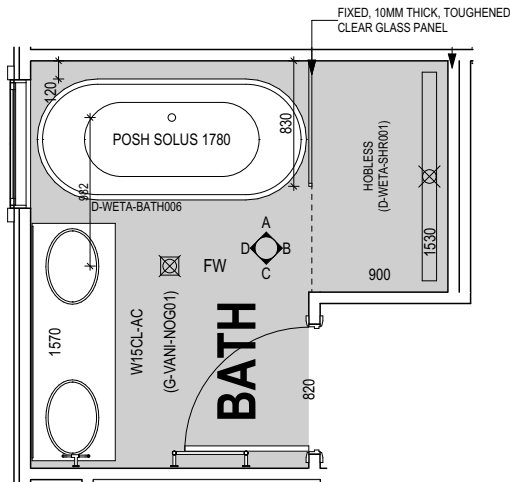

BATHROOM PLAN
SCALE: 1:50

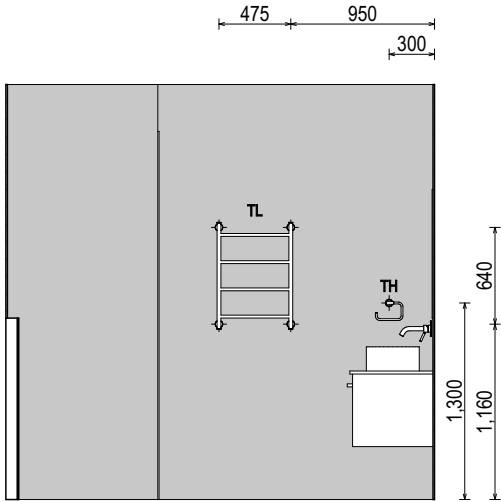

ELEVATION C
SCALE: 1:50

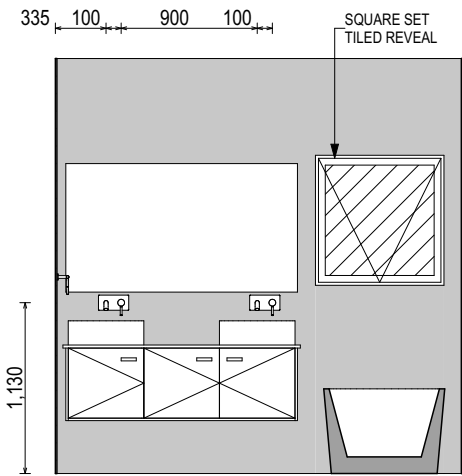

ELEVATION D
SCALE: 1:50

Certificate No. # DAYQOIT5QI

Scan QR code or follow website link for rating details.

Assessor name: Claude-Francois Sookloll
Accreditation No: DMN/14/1662
Property Address: Lot 1 (#48) Wentworth Street, CROYDON PARK, City of Canterbury-Bankstown, 2133, NSW, 2133
<https://www.fr5.com.au/QRCodeLanding?PublicId=DAYQOIT5QI>

**SUBJECT TO NCC 2022
(1 OCT 2023 + 7 STAR)
WATERPROOFING & PLUMBING**

PLAN ACCEPTANCE BY OWNER

SIGNATURE: DATE:

SIGNATURE: DATE:

PLEASE NOTE THAT VARIATIONS WILL NOT BE ACCEPTED AFTER THIS PLAN ACCEPTANCE HAS BEEN SIGNED

ALL DIMENSIONS ARE FRAME DIMENSIONS

© 2024 MCDONALD JONES HOMES PTY LTD (ABN 82 003 687 232). THIS DRAWING IS AN ORIGINAL ARTISTIC WORK WITHIN THE MEANING OF THE COPYRIGHT ACT 1968 (CTH). MCDONALD JONES HOMES PTY LTD IS THE OWNER OF COPYRIGHT IN THIS DRAWING. YOU HEREBY AGREE AND UNDERTAKE THAT YOU WILL NOT IN ANY WAY REPRODUCE, COPY, MODIFY, USE OR TAKE ADVANTAGE OF THE DRAWING TO BUILD A HOUSE BASED ON THIS PLAN (WHETHER IN WHOLE OR IN PART) WITHOUT THE PRIOR WRITTEN CONSENT OF MCDONALD JONES HOMES PTY LTD.



SPECIFICATION: TWO STOREY		REVISION	DRAWN	CLIENT:	HOUSE DESIGN:	HOUSE CODE:	DO NOT SCALE DRAWINGS. USE FIGURED DIMENSIONS ONLY. CHECK AND VERIFY DIMENSIONS AND LEVELS PRIOR TO THE COMMENCEMENT OF ANY WORK. ALL DISCREPANCIES TO BE REPORTED TO THE DRAFTING OFFICE.	
	5	COLOURS APPLIED	TNG	26/01/2024	CLIFF LAURENS & MARGARETHA HARUNISA TARUNADJAYA	PANORAMA 36		H-MDSPNR20DA
COPYRIGHT: © 2024	6	AMENDED AS PER PCV007	GB0	22/02/2024	ADDRESS:	FACADE DESIGN:		FACADE CODE:
	7	AMENDED AS PER PCV08 - HYDRAULIC	LFL	09/04/2024	48 WENTWORTH STREET, CROYDON PARK NSW 2133	PULSE		F-MDSPNR20PLSEA
	8	AMENDED AS PER PCV009 & PCV011	GB0	03/05/2024	LOT / SECTION / DP:	COUNCIL:		SHEET TITLE:
	9	AMENDED AS PER PCV013	LCS	08/05/2024	1 / - / 304988	CANTERBURY BANKSTOWN COUNCIL		BATHROOM DETAILS
						SHEET No.:	SCALES:	
						15 / 24	1:50	607082


REFER TO SHEET 1 (COVER SHEET) FOR ALL BUILDING INFORMATION REGARDING:

- SUSTAINABILITY REQUIREMENTS
- SITE CLASSIFICATION
- GENERAL BUILDING INFORMATION


DETAILS DEPICTED ON THIS SHEET ARE A REPRESENTATION ONLY

LEGEND


RSHR	RAIL SHOWER
ROSE	SHOWER ROSE
ELBW	SHOWER ELBOW CONNECTION
MIX	MIXER TAP
HT	HOT TAP
CT	COLD TAP
HS	HOB SPOUT
WS	WALL SPOUT
SC	STOP COCK
TRH	TOILET ROLL HOLDER
TR-S	TOWEL RAIL - SINGLE
TR-D	TOWEL RAIL - DOUBLE
TL	TOWEL LADDER
TH	TOWEL HOLDER
TR	TOWEL RACK
TMB	TUMBLER HOLDER
RNG	TOWEL RING
RH	ROBE HOOK
SHLF	SHELF
SR	SHAMPOO RECESS
SOAP	SOAP HOLDER

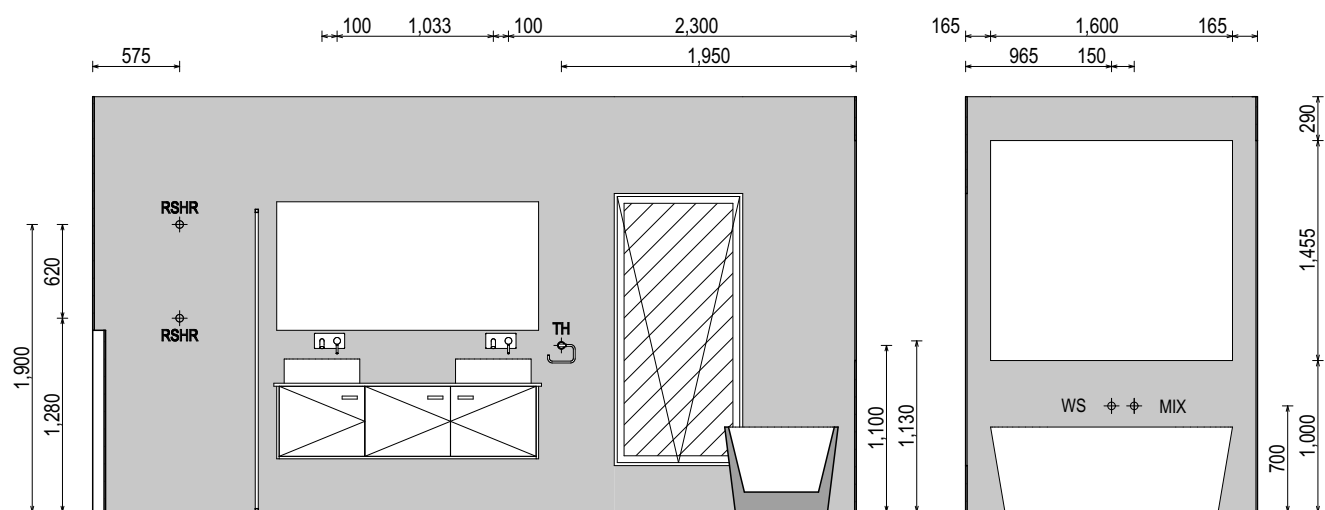


ELEVATION A
SCALE: 1:50

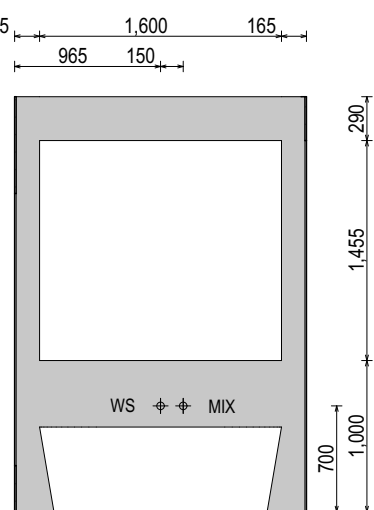


ELEVATION B
SCALE: 1:50

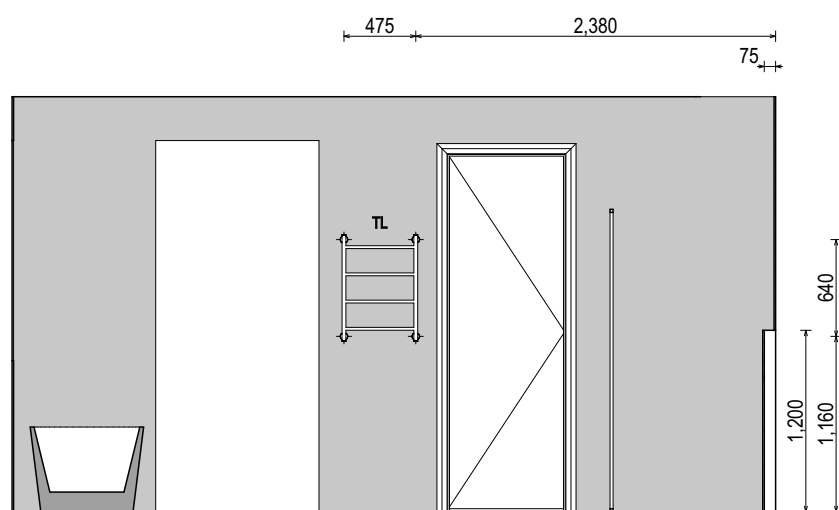

ELEVATION C
SCALE: 1:50

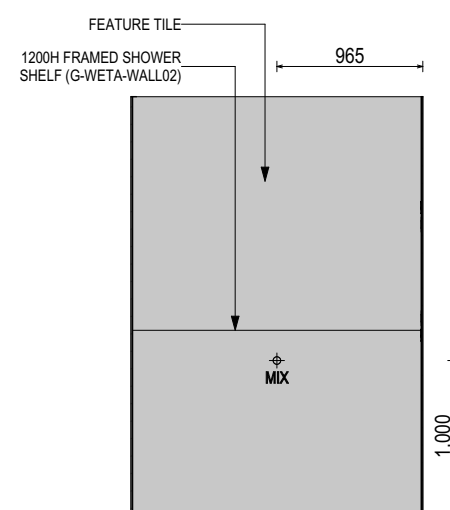


ELEVATION D
SCALE: 1:50

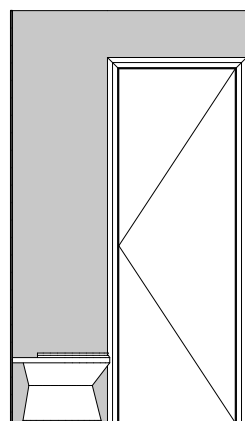


ELEVATION E
SCALE: 1:50




ELEVATION F
SCALE: 1:50

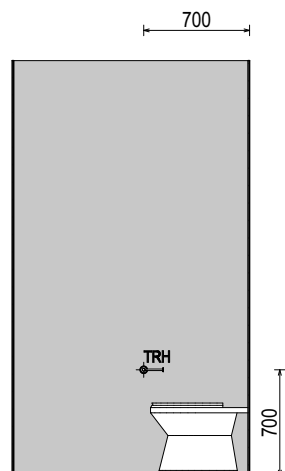

ELEVATION G
SCALE: 1:50

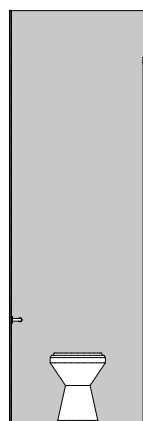

ELEVATION H
SCALE: 1:50

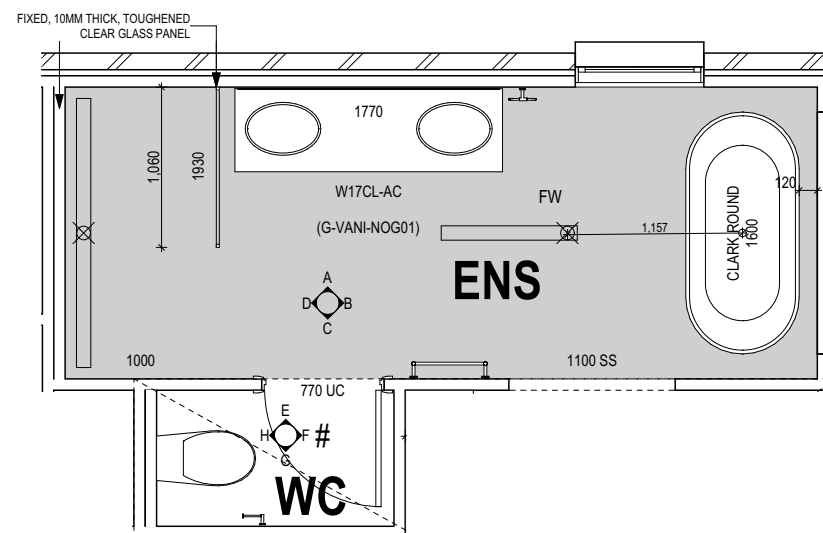

ENSUITE / WC PLAN
SCALE: 1:50



**SUBJECT TO NCC 2022
(1 OCT 2023 + 7 STAR)
WATERPROOFING & PLUMBING**

PLAN ACCEPTANCE BY OWNER

SIGNATURE: _____ DATE: _____

SIGNATURE: _____ DATE: _____

PLEASE NOTE THAT VARIATIONS WILL NOT BE ACCEPTED
AFTER THIS PLAN ACCEPTANCE HAS BEEN SIGNED

ALL DIMENSIONS ARE FRAME DIMENSIONS

© 2024 MCDONALD JONES HOMES PTY LTD (ABN 82 003 687 232). THIS DRAWING IS AN ORIGINAL ARTISTIC WORK WITHIN THE MEANING OF THE COPYRIGHT ACT 1968 (CTH). MCDONALD JONES HOMES PTY LTD IS THE OWNER OF COPYRIGHT IN THIS DRAWING. YOU HEREBY AGREE AND UNDERTAKE THAT YOU WILL NOT IN ANY WAY REPRODUCE, COPY, MODIFY, USE OR TAKE ADVANTAGE OF THE DRAWING TO BUILD A HOUSE BASED ON THIS PLAN (WHETHER IN WHOLE OR IN PART) WITHOUT THE PRIOR WRITTEN CONSENT OF MCDONALD JONES HOMES PTY LTD.



mcdonald jones
FIND YOURSELF AT HOME

SPECIFICATION:		REVISION	DRAWN	CLIENT:	HOUSE DESIGN:	HOUSE CODE:	DO NOT SCALE DRAWINGS. USE FIGURED DIMENSIONS ONLY. CHECK AND VERIFY DIMENSIONS AND LEVELS PRIOR TO THE COMMENCEMENT OF ANY WORK. ALL DISCREPANCIES TO BE REPORTED TO THE DRAFTING OFFICE.
TWO STOREY	5	COLOURS APPLIED	TNG 26/01/2024	CLIFF LAURENS & MARGARETHA HARUNISA TARUNADJAYA	PANORAMA 36	H-MDSPNR20DA	
COPYRIGHT:	6	AMENDED AS PER PCV007	GB0 22/02/2024	ADDRESS:	FACADE DESIGN:	FACADE CODE:	
© 2024	7	AMENDED AS PER PCV08 - HYDRAULIC	LFL 09/04/2024	48 WENTWORTH STREET, CROYDON PARK NSW 2133	PULSE	F-MDSPNR20PLSEA	
	8	AMENDED AS PER PCV009 & PCV011	GB0 03/05/2024	LOT / SECTION / DP:	SHEET TITLE:	SHEET No.:	
	9	AMENDED AS PER PCV013	LCS 08/05/2024	1 / - / 304988	COUNCIL: CANTERBURY BANKSTOWN COUNCIL	SCALES: 16 / 24	607082


REFER TO SHEET 1 (COVER SHEET) FOR ALL BUILDING INFORMATION REGARDING:

- SUSTAINABILITY REQUIREMENTS
- SITE CLASSIFICATION
- GENERAL BUILDING INFORMATION


DETAILS DEPICTED ON THIS SHEET ARE A REPRESENTATION ONLY

LEGEND


- RSHR RAIL SHOWER
- ROSE SHOWER ROSE
- ELBW SHOWER ELBOW CONNECTION
- MIX MIXER TAP
- HT HOT TAP
- CT COLD TAP
- HS HOB SPOUT
- WS WALL SPOUT
- SC STOP COCK
- TRH TOILET ROLL HOLDER
- TR-S TOWEL RAIL - SINGLE
- TR-D TOWEL RAIL - DOUBLE
- TL TOWEL LADDER
- TH TOWEL HOLDER
- TR TOWEL RACK
- TMB TUMBLER HOLDER
- RNG TOWEL RING
- RH ROBE HOOK
- SHLF SHELF
- SR SHAMPOO RECESS
- SOAP SOAP HOLDER

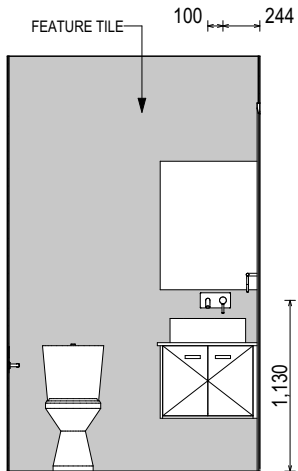


ELEVATION A
SCALE: 1:50

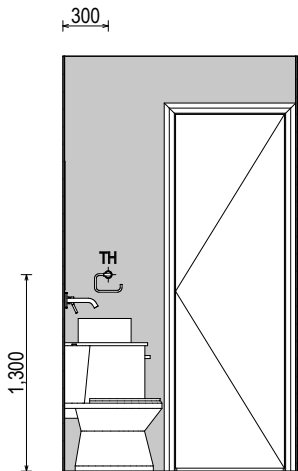


ELEVATION B
SCALE: 1:50

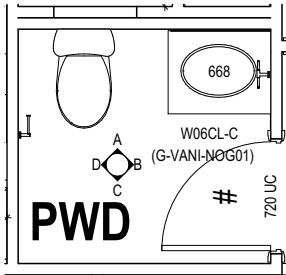

POWDER ROOM PLAN
SCALE: 1:50

 

ELEVATION C
SCALE: 1:50

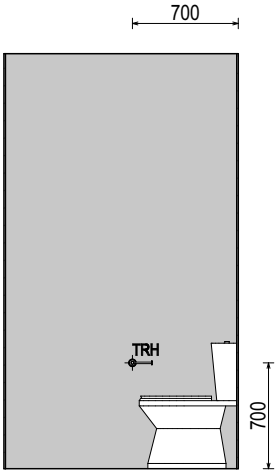

ELEVATION D
SCALE: 1:50



SUBJECT TO NCC 2022
(1 OCT 2023 + 7 STAR)
WATERPROOFING & PLUMBING

PLAN ACCEPTANCE BY OWNER

SIGNATURE: DATE:

SIGNATURE: DATE:

PLEASE NOTE THAT VARIATIONS WILL NOT BE ACCEPTED AFTER THIS PLAN ACCEPTANCE HAS BEEN SIGNED

ALL DIMENSIONS ARE FRAME DIMENSIONS

© 2024 MCDONALD JONES HOMES PTY LTD (ABN 82 003 687 232). THIS DRAWING IS AN ORIGINAL ARTISTIC WORK WITHIN THE MEANING OF THE COPYRIGHT ACT 1968 (CTH). MCDONALD JONES HOMES PTY LTD IS THE OWNER OF COPYRIGHT IN THIS DRAWING. YOU HEREBY AGREE AND UNDERTAKE THAT YOU WILL NOT IN ANY WAY REPRODUCE, COPY, MODIFY, USE OR TAKE ADVANTAGE OF THE DRAWING TO BUILD A HOUSE BASED ON THIS PLAN (WHETHER IN WHOLE OR IN PART) WITHOUT THE PRIOR WRITTEN CONSENT OF MCDONALD JONES HOMES PTY LTD.



SPECIFICATION: TWO STOREY COPYRIGHT: © 2024		REVISION	DRAWN	CLIENT:	HOUSE DESIGN:	HOUSE CODE:	DO NOT SCALE DRAWINGS. USE FIGURED DIMENSIONS ONLY. CHECK AND VERIFY DIMENSIONS AND LEVELS PRIOR TO THE COMMENCEMENT OF ANY WORK. ALL DISCREPANCIES TO BE REPORTED TO THE DRAFTING OFFICE. 607082
	5	COLOURS APPLIED	TNG 26/01/2024	CLIFF LAURENS & MARGARETHA HARUNISA TARUNADJAYA	PANORAMA 36	H-MDSPNR20DA	
	6	AMENDED AS PER PCV007	GB0 22/02/2024	ADDRESS:	FACADE DESIGN:	FACADE CODE:	
	7	AMENDED AS PER PCV08 - HYDRAULIC	LFL 09/04/2024	48 WENTWORTH STREET, CROYDON PARK NSW 2133	PULSE	F-MDSPNR20PLSEA	
	8	AMENDED AS PER PCV009 & PCV011	GB0 03/05/2024	LOT / SECTION / DP:	SHEET TITLE:	SHEET No.:	
	9	AMENDED AS PER PCV013	LCS 08/05/2024	1 / - / 304988	COUNCIL: CANTERBURY BANKSTOWN COUNCIL	POWDER ROOM DETAILS	17 / 24
						SCALES:	1:50


REFER TO SHEET 1 (COVER SHEET) FOR ALL BUILDING INFORMATION REGARDING:

- SUSTAINABILITY REQUIREMENTS
- SITE CLASSIFICATION
- GENERAL BUILDING INFORMATION


DETAILS DEPICTED ON THIS SHEET ARE A REPRESENTATION ONLY

LEGEND


- RSHR RAIL SHOWER
- ROSE SHOWER ROSE
- ELBW SHOWER ELBOW CONNECTION
- MIX MIXER TAP
- HT HOT TAP
- CT COLD TAP
- HS HOB SPOUT
- WS WALL SPOUT
- SC STOP COCK
- TRH TOILET ROLL HOLDER
- TR-S TOWEL RAIL - SINGLE
- TR-D TOWEL RAIL - DOUBLE
- TL TOWEL LADDER
- TH TOWEL HOLDER
- TR TOWEL RACK
- TMB TUMBLER HOLDER
- RNG TOWEL RING
- RH ROBE HOOK
- SHLF SHELF
- SR SHAMPOO RECESS
- SOAP SOAP HOLDER

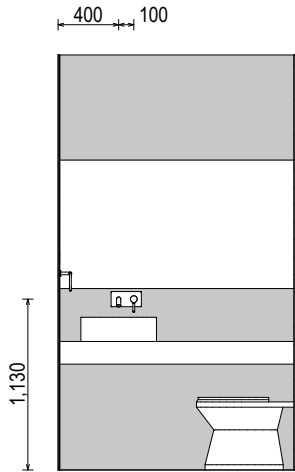


ELEVATION A
SCALE: 1:50

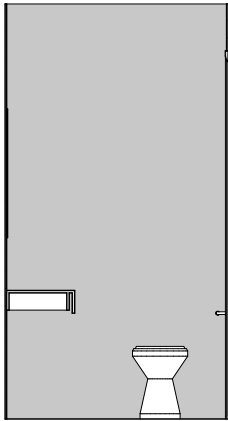


ELEVATION B
SCALE: 1:50

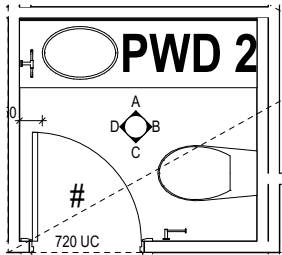


POWDER ROOM 2 PLAN
SCALE: 1:50

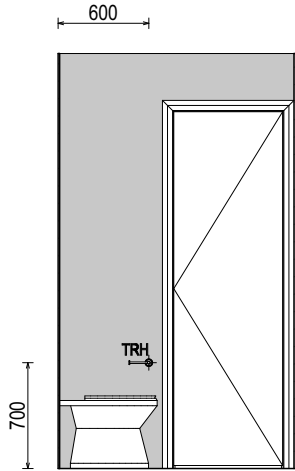

ELEVATION C
SCALE: 1:50

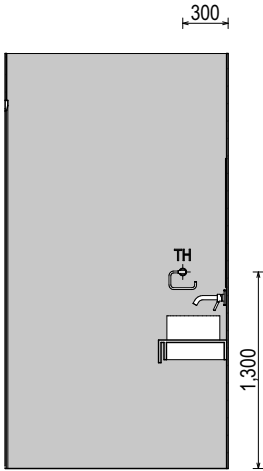

ELEVATION D
SCALE: 1:50

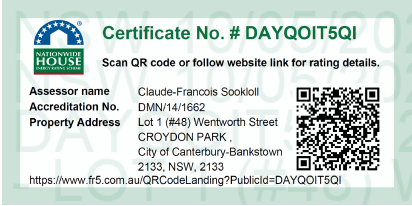

**SUBJECT TO NCC 2022
(1 OCT 2023 + 7 STAR)
WATERPROOFING & PLUMBING**

PLAN ACCEPTANCE BY OWNER

SIGNATURE: DATE:

SIGNATURE: DATE:

PLEASE NOTE THAT VARIATIONS WILL NOT BE ACCEPTED AFTER THIS PLAN ACCEPTANCE HAS BEEN SIGNED

ALL DIMENSIONS ARE FRAME DIMENSIONS

© 2024 MCDONALD JONES HOMES PTY LTD (ABN 82 003 687 232). THIS DRAWING IS AN ORIGINAL ARTISTIC WORK WITHIN THE MEANING OF THE COPYRIGHT ACT 1968 (CTH). MCDONALD JONES HOMES PTY LTD IS THE OWNER OF COPYRIGHT IN THIS DRAWING. YOU HEREBY AGREE AND UNDERTAKE THAT YOU WILL NOT IN ANY WAY REPRODUCE, COPY, MODIFY, USE OR TAKE ADVANTAGE OF THE DRAWING TO BUILD A HOUSE BASED ON THIS PLAN (WHETHER IN WHOLE OR IN PART) WITHOUT THE PRIOR WRITTEN CONSENT OF MCDONALD JONES HOMES PTY LTD.



SPECIFICATION: TWO STOREY COPYRIGHT: © 2024		REVISION	DRAWN	CLIENT:	HOUSE DESIGN:	HOUSE CODE:	DO NOT SCALE DRAWINGS. USE FIGURED DIMENSIONS ONLY. CHECK AND VERIFY DIMENSIONS AND LEVELS PRIOR TO THE COMMENCEMENT OF ANY WORK. ALL DISCREPANCIES TO BE REPORTED TO THE DRAFTING OFFICE. 607082
	5	COLOURS APPLIED	TNG 26/01/2024	CLIFF LAURENS & MARGARETHA HARUNISA TARUNADJAYA	PANORAMA 36	H-MDSPNR20DA	
	6	AMENDED AS PER PCV007	GBO 22/02/2024	ADDRESS:	FACADE DESIGN:	FACADE CODE:	
	7	AMENDED AS PER PCV08 - HYDRAULIC	LFL 09/04/2024	48 WENTWORTH STREET, CROYDON PARK NSW 2133	PULSE	F-MDSPNR20PLSEA	
	8	AMENDED AS PER PCV009 & PCV011	GBO 03/05/2024	LOT / SECTION / DP:	SHEET TITLE:	SHEET No.:	
	9	AMENDED AS PER PCV013	LCS 08/05/2024	1 / - / 304988	COUNCIL: CANTERBURY BANKSTOWN COUNCIL	18 / 24	SCALES: 1:50


REFER TO SHEET 1 (COVER SHEET) FOR ALL BUILDING INFORMATION REGARDING:

- SUSTAINABILITY REQUIREMENTS
- SITE CLASSIFICATION
- GENERAL BUILDING INFORMATION


DETAILS DEPICTED ON THIS SHEET ARE A REPRESENTATION ONLY

LEGEND


- | | |
|------|-------------------------|
| RSHR | RAIL SHOWER |
| ROSE | SHOWER ROSE |
| ELBW | SHOWER ELBOW CONNECTION |
| MIX | MIXER TAP |
| HT | HOT TAP |
| CT | COLD TAP |
| HS | HOB SPOUT |
| WS | WALL SPOUT |
| SC | STOP COCK |
| TRH | TOILET ROLL HOLDER |
| TR-S | TOWEL RAIL - SINGLE |
| TR-D | TOWEL RAIL - DOUBLE |
| TL | TOWEL LADDER |
| TH | TOWEL HOLDER |
| TR | TOWEL RACK |
| TMB | TUMBLER HOLDER |
| RNG | TOWEL RING |
| RH | ROBE HOOK |
| SHLF | SHELF |
| SR | SHAMPOO RECESS |
| SOAP | SOAP HOLDER |

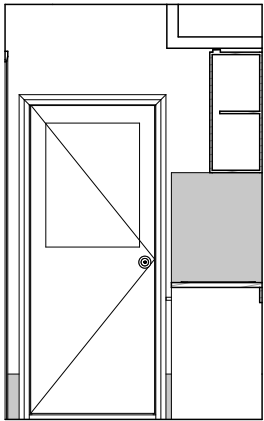


ELEVATION A
SCALE: 1:50

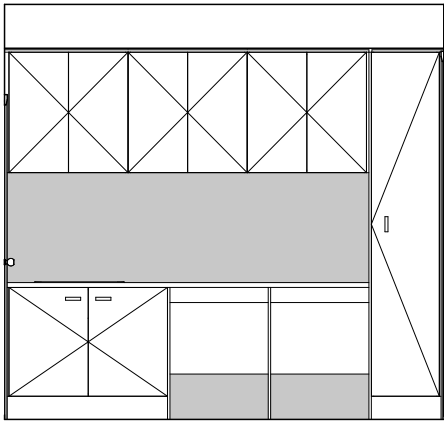


ELEVATION B
SCALE: 1:50

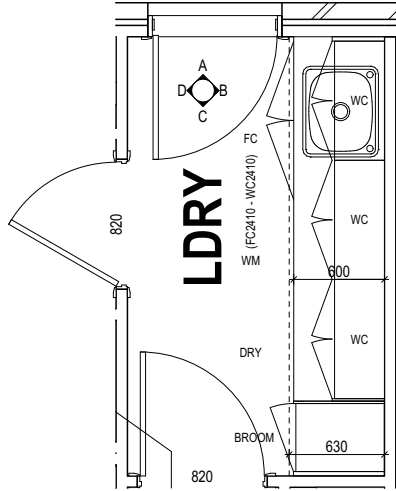

LAUNDRY PLAN
SCALE: 1:50

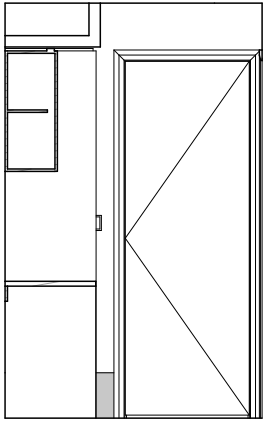

ELEVATION C
SCALE: 1:50

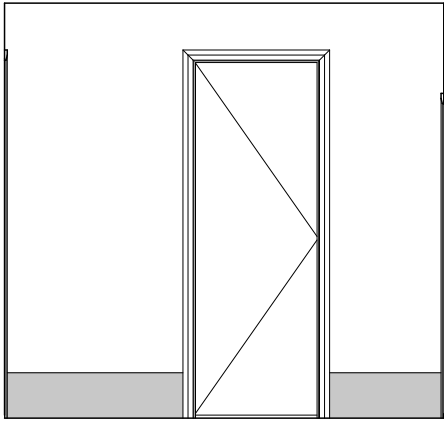

ELEVATION D
SCALE: 1:50



**SUBJECT TO NCC 2022
(1 OCT 2023 + 7 STAR)
WATERPROOFING & PLUMBING**

PLAN ACCEPTANCE BY OWNER

SIGNATURE: DATE:

SIGNATURE: DATE:

PLEASE NOTE THAT VARIATIONS WILL NOT BE ACCEPTED AFTER THIS PLAN ACCEPTANCE HAS BEEN SIGNED

ALL DIMENSIONS ARE FRAME DIMENSIONS

© 2024 MCDONALD JONES HOMES PTY LTD (ABN 82 003 687 232). THIS DRAWING IS AN ORIGINAL ARTISTIC WORK WITHIN THE MEANING OF THE COPYRIGHT ACT 1968 (CTH). MCDONALD JONES HOMES PTY LTD IS THE OWNER OF COPYRIGHT IN THIS DRAWING. YOU HEREBY AGREE AND UNDERTAKE THAT YOU WILL NOT IN ANY WAY REPRODUCE, COPY, MODIFY, USE OR TAKE ADVANTAGE OF THE DRAWING TO BUILD A HOUSE BASED ON THIS PLAN (WHETHER IN WHOLE OR IN PART) WITHOUT THE PRIOR WRITTEN CONSENT OF MCDONALD JONES HOMES PTY LTD.



SPECIFICATION: TWO STOREY	REVISION	DRAWN	CLIENT:	HOUSE DESIGN:	HOUSE CODE:	DO NOT SCALE DRAWINGS. USE FIGURED DIMENSIONS ONLY. CHECK AND VERIFY DIMENSIONS AND LEVELS PRIOR TO THE COMMENCEMENT OF ANY WORK. ALL DISCREPANCIES TO BE REPORTED TO THE DRAFTING OFFICE.
COPYRIGHT: © 2024	5 COLOURS APPLIED	TNG 26/01/2024	CLIFF LAURENS & MARGARETHA HARUNISA TARUNADJAYA	PANORAMA 36	H-MDSPNR20DA	
	6 AMENDED AS PER PCV007	GBO 22/02/2024	ADDRESS:	FACADE DESIGN:	FACADE CODE:	
	7 AMENDED AS PER PCV08 - HYDRAULIC	LFL 09/04/2024	48 WENTWORTH STREET, CROYDON PARK NSW 2133	PULSE	F-MDSPNR20PLSEA	
	8 AMENDED AS PER PCV009 & PCV011	GBO 03/05/2024	LOT / SECTION / DP:	SHEET TITLE:	SHEET No.:	
	9 AMENDED AS PER PCV013	LCS 08/05/2024	1 / - / 304988	COUNCIL:	19 / 24	607082
			CANTERBURY BANKSTOWN COUNCIL	LAUNDRY DETAILS	1:50	

REFER TO SHEET 1 (COVER SHEET) FOR ALL BUILDING INFORMATION REGARDING:

- SUSTAINABILITY REQUIREMENTS
- SITE CLASSIFICATION
- GENERAL BUILDING INFORMATION

FLOOR TILES SHOWN ON PLAN DO NOT INDICATE THE SIZE OR JOINT LOCATIONS OF THE ACTUAL FLOOR TILES.
TIMBER FLOORING SHOWN ON PLAN DOES NOT INDICATE THE BOARD SIZE OR DIRECTION OF THE ACTUAL FLOORING.

COVERINGS LEGEND

NO COVERING

COVER GRADE CONCRETE


CARPET

TIMBER/LAMINATE (BY BUILDER)

TILE (STANDARD WET AREAS)

TILE (UPGRADED AREAS)

VINYL

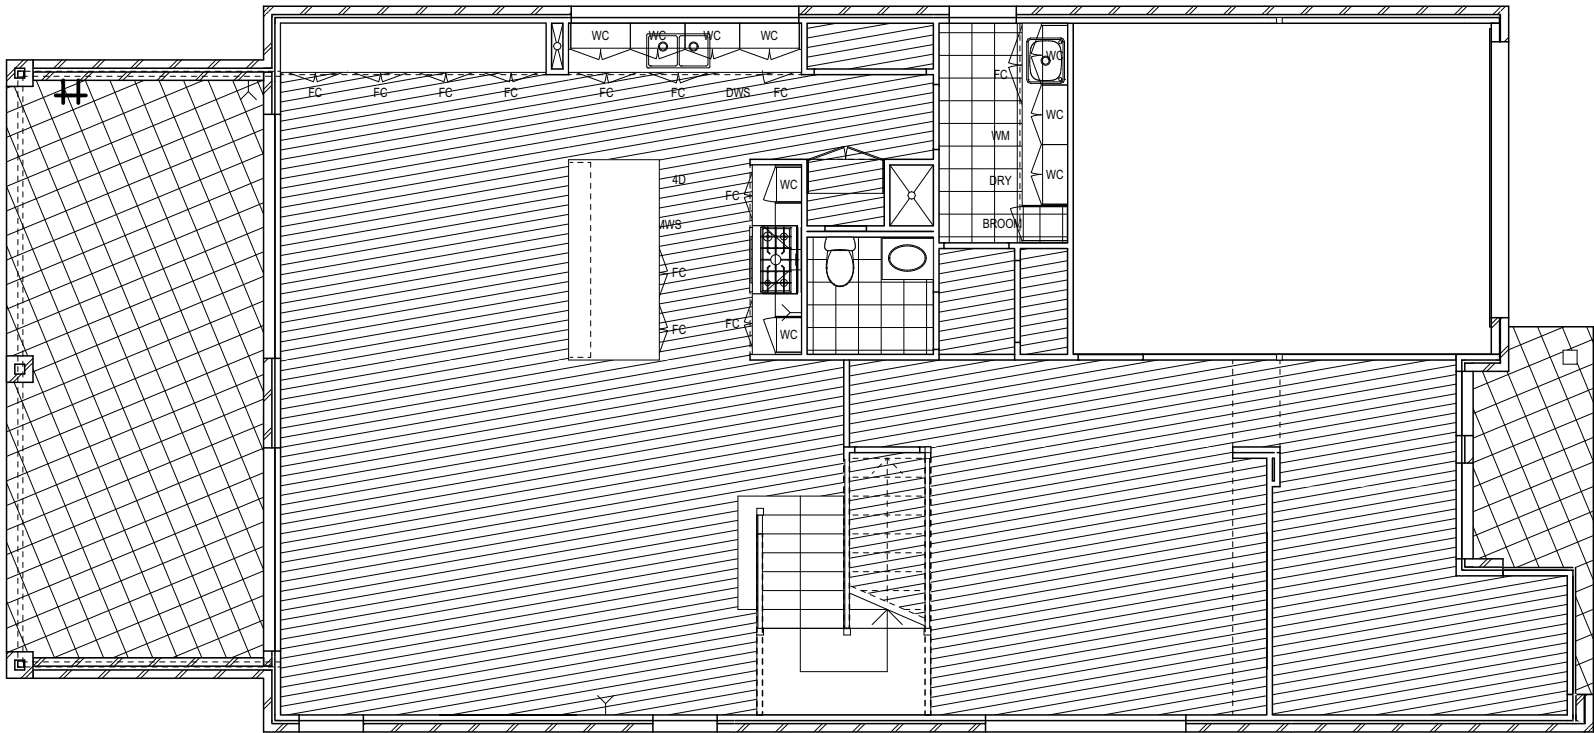

FLOOR COVERINGS (GROUND FLOOR)
SCALE: 1:100



Certificate No. # DAYQOIT5QI

Scan QR code or follow website link for rating details.

Assessor name

Accreditation No.

Property Address

Claude-Francois Sookloll

DMN/14/1662

Lot 1 (#48) Wentworth Street

CROYDON PARK

City of Canterbury-Bankstown

2133, NSW, 2133



<https://www.fr5.com.au/QRCodeLanding?PublicId=DAYQOIT5QI>

SUBJECT TO NCC 2022

(1 OCT 2023 + 7 STAR)

WATERPROOFING & PLUMBING

PLAN ACCEPTANCE BY OWNER

SIGNATURE: _____ DATE: _____

SIGNATURE: _____ DATE: _____

PLEASE NOTE THAT VARIATIONS WILL NOT BE ACCEPTED AFTER THIS PLAN ACCEPTANCE HAS BEEN SIGNED

© 2024 MCDONALD JONES HOMES PTY LTD (ABN 82 003 687 232). THIS DRAWING IS AN ORIGINAL ARTISTIC WORK WITHIN THE MEANING OF THE COPYRIGHT ACT 1968 (CTH). MCDONALD JONES HOMES PTY LTD IS THE OWNER OF COPYRIGHT IN THIS DRAWING. YOU HEREBY AGREE AND UNDERTAKE THAT YOU WILL NOT IN ANY WAY REPRODUCE, COPY, MODIFY, USE OR TAKE ADVANTAGE OF THE DRAWING TO BUILD A HOUSE BASED ON THIS PLAN (WHETHER IN WHOLE OR IN PART) WITHOUT THE PRIOR WRITTEN CONSENT OF MCDONALD JONES HOMES PTY LTD.

 mcdonald jones FIND YOURSELF AT HOME	SPECIFICATION:	REVISION		DRAWN	CLIENT:	HOUSE DESIGN:		HOUSE CODE:	DO NOT SCALE DRAWINGS. USE FIGURED DIMENSIONS ONLY. CHECK AND VERIFY DIMENSIONS AND LEVELS PRIOR TO THE COMMENCEMENT OF ANY WORK. ALL DISCREPANCIES TO BE REPORTED TO THE DRAFTING OFFICE.
	TWO STOREY	5	COLOURS APPLIED	TNG 26/01/2024	CLIFF LAURENS & MARGARETHA HARUNISA TARUNADJAYA	PANORAMA 36		H-MDSPNR20DA	
	COPYRIGHT:	6	AMENDED AS PER PCV007	GB0 22/02/2024	ADDRESS:	FACADE DESIGN:		FACADE CODE:	
	© 2024	7	AMENDED AS PER PCV08 - HYDRAULIC	LFL 09/04/2024	48 WENTWORTH STREET, CROYDON PARK NSW 2133	PULSE		F-MDSPNR20PLSEA	
		8	AMENDED AS PER PCV009 & PCV011	GB0 03/05/2024	LOT / SECTION / DP:	SHEET TITLE:	SHEET No.:	SCALES:	
		9	AMENDED AS PER PCV013	LCS 08/05/2024	1 / - / 304988	COUNCIL:	20 / 24	1:100	607082
					CANTERBURY BANKSTOWN COUNCIL	FLOOR COVERINGS (GF)			

Last Published: Wednesday, 8 May 2024 4:57 PM

File Location: G:\Sydney\Drafting\Job Files 600000\Job Files 607001 - 60720\1607082 - Laurens\Plan Model\607082 Laurens - AC 24.pln

Template Version: 24.033

REFER TO SHEET 1 (COVER SHEET) FOR ALL BUILDING INFORMATION REGARDING:

- SUSTAINABILITY REQUIREMENTS
- SITE CLASSIFICATION
- GENERAL BUILDING INFORMATION

FLOOR TILES SHOWN ON PLAN DO NOT INDICATE THE SIZE OR JOINT LOCATIONS OF THE ACTUAL FLOOR TILES.
TIMBER FLOORING SHOWN ON PLAN DOES NOT INDICATE THE BOARD SIZE OR DIRECTION OF THE ACTUAL FLOORING.

COVERINGS LEGEND

NO COVERING

COVER GRADE CONCRETE


CARPET

TIMBER/LAMINATE (BY BUILDER)

TILE (STANDARD WET AREAS)

TILE (UPGRADED AREAS)

VINYL

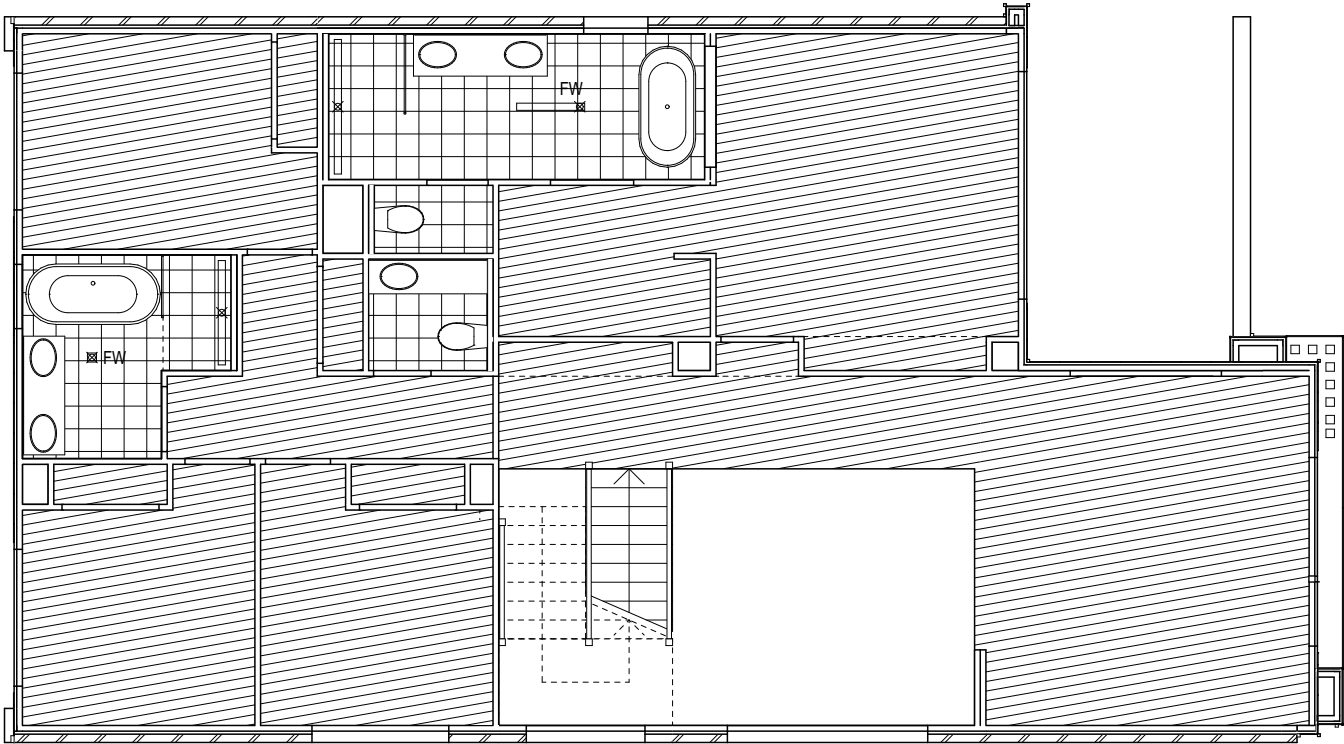

FLOOR COVERINGS (FIRST FLOOR)
SCALE: 1:100

Certificate No. # DAYQ0IT5QI

Scan QR code or follow website link for rating details.

Assessor name: Claude-Francois Sookkoll

Accreditation No: DM/N/14/11662

Property Address: Lot 1 (#48) Wentworth Street CROYDON PARK City of Canterbury-Bankstown 2133, NSW, 2133

<https://www.fr5.com.au/QRCodeLanding?PublicId=DAYQ0IT5QI>

SUBJECT TO NCC 2022
(1 OCT 2023 + 7 STAR)
WATERPROOFING & PLUMBING

PLAN ACCEPTANCE BY OWNER

SIGNATURE: _____

DATE: _____

SIGNATURE: _____


DATE: _____

PLEASE NOTE THAT VARIATIONS WILL NOT BE ACCEPTED AFTER THIS PLAN ACCEPTANCE HAS BEEN SIGNED

© 2024 MCDONALD JONES HOMES PTY LTD (ABN 82 003 687 232). THIS DRAWING IS AN ORIGINAL ARTISTIC WORK WITHIN THE MEANING OF THE COPYRIGHT ACT 1968 (CTH). MCDONALD JONES HOMES PTY LTD IS THE OWNER OF COPYRIGHT IN THIS DRAWING. YOU HEREBY AGREE AND UNDERTAKE THAT YOU WILL NOT IN ANY WAY REPRODUCE, COPY, MODIFY, USE OR TAKE ADVANTAGE OF THE DRAWING TO BUILD A HOUSE BASED ON THIS PLAN (WHETHER IN WHOLE OR IN PART) WITHOUT THE PRIOR WRITTEN CONSENT OF MCDONALD JONES HOMES PTY LTD.

 FIND YOURSELF AT HOME	SPECIFICATION:				CLIENT:	HOUSE DESIGN:		HOUSE CODE:	DO NOT SCALE DRAWINGS. USE FIGURED DIMENSIONS ONLY. CHECK AND VERIFY DIMENSIONS AND LEVELS PRIOR TO THE COMMENCEMENT OF ANY WORK. ALL DISCREPANCIES TO BE REPORTED TO THE DRAFTING OFFICE. 607082
	TWO STOREY	5	COLOURS APPLIED	TNG 26/01/2024	CLIFF LAURENS & MARGARETHA HARUNISA TARUNADJAYA	PANORAMA 36		H-MDSPNR20DA	
	COPYRIGHT:	6	AMENDED AS PER PCV007	GBO 22/02/2024	ADDRESS:	FACADE DESIGN:		FACADE CODE:	
	© 2024	7	AMENDED AS PER PCV08 - HYDRAULIC	LFL 09/04/2024	48 WENTWORTH STREET, CROYDON PARK NSW 2133	PULSE		F-MDSPNR20PLSEA	
		8	AMENDED AS PER PCV009 & PCV011	GBO 03/05/2024	LOT / SECTION / DP:	SHEET TITLE:	SHEET No.:	SCALES:	
		9	AMENDED AS PER PCV013	LCS 08/05/2024	1 / - / 304988	CANTERBURY BANKSTOWN COUNCIL	21 / 24	1:100	

Last Published: Wednesday, 8 May 2024 4:57 PM

 


SCALE: 1:100



Template Version: 24.033

SPECIFICATION:		REVISION	DRAWN	CLIENT:		HOUSE DESIGN:		HOUSE CODE:	DO NOT SCALE DRAWINGS. USE FIGURED DIMENSIONS ONLY. CHECK AND VERIFY DIMENSIONS AND LEVELS PRIOR TO THE COMMENCEMENT OF ANY WORK. ALL DISCREPANCIES TO BE REPORTED TO THE DRAFTING OFFICE.
TWO STOREY	5	COLOURS APPLIED	TNG 26/01/2024	CLIFF LAURENS & MARGARETHA HARUNISA TARUNADJAYA		PANORAMA 36		H-MDSPNR20DA	
COPYRIGHT:	6	AMENDED AS PER PCV007	GB0 22/02/2024	ADDRESS:		FACADE DESIGN:		FACADE CODE:	
© 2024	7	AMENDED AS PER PCV08 - HYDRAULIC	LFL 09/04/2024	48 WENTWORTH STREET, CROYDON PARK NSW 2133		PULSE		F-MDSPNR20PLSEA	
	8	AMENDED AS PER PCV009 & PCV011	GB0 03/05/2024	LOT / SECTION / DP:	COUNCIL:	SHEET TITLE:	SHEET No.:	SCALES:	607082
	9	AMENDED AS PER PCV013	LCS 08/05/2024	1 / - / 304988	CANTERBURY BANKSTOWN COUNCIL	SLAB PLAN	22 / 24	1:100	


ALL EXTERIOR SLABS TO BE GRADED BY CONCRETER TO ACHIEVE APPROX. 1:100 FALL TO OUTSIDE EDGE WITH MAXIMUM CROSSFALL OF 30mm OVER ENTIRE SLAB.

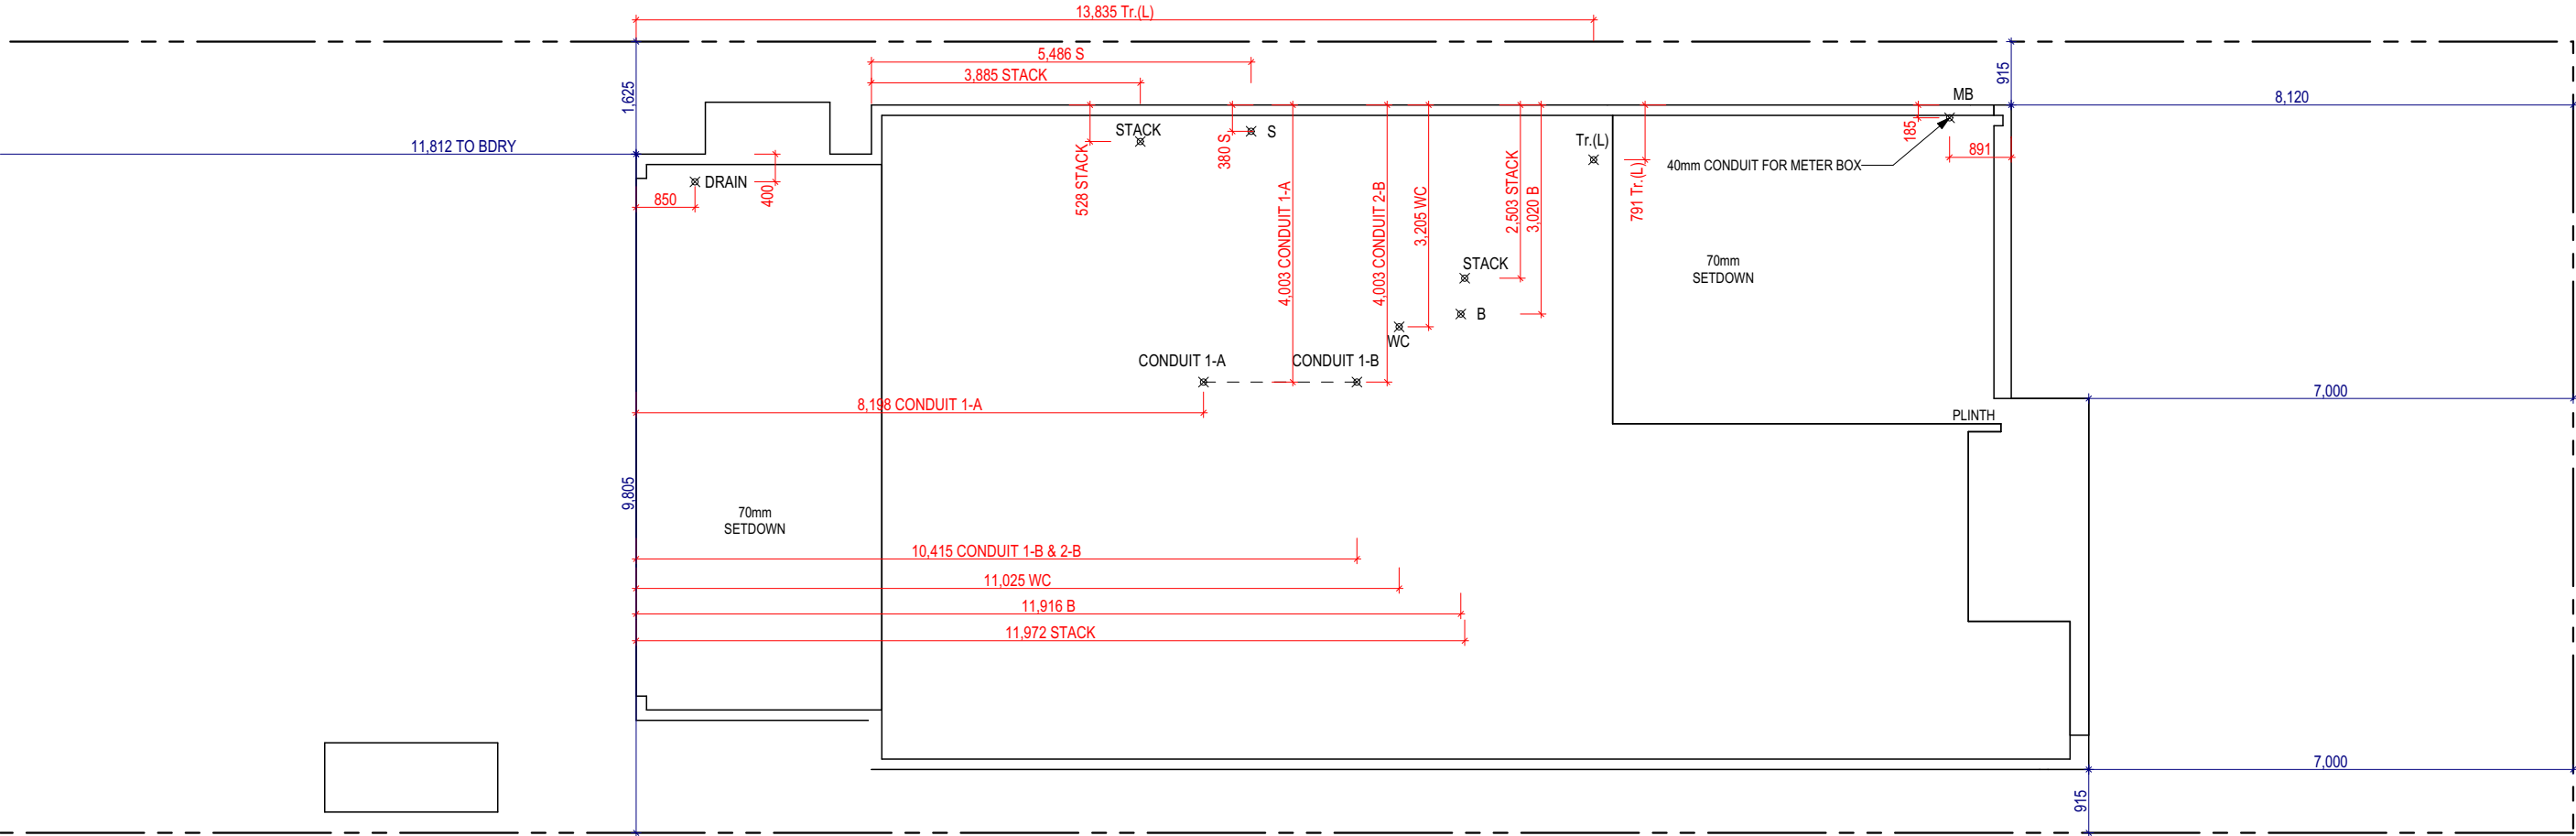

DRAINAGE PLAN
SCALE: 1:100

LEGEND

- B BASIN
- Bth BATH WASTE
- FW FLOOR WASTE GULLY
- Shr SHOWER
- S SINK (KITCHEN)
- Tr.(L) TROUGH (LAUNDRY)
- WC WATER CLOSET

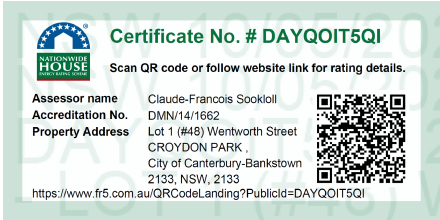


SUBJECT TO NCC 2022
(1 OCT 2023 + 7 STAR)
WATERPROOFING & PLUMBING


© 2024 MCDONALD JONES HOMES PTY LTD (ABN 82 003 687 232). THIS DRAWING IS AN ORIGINAL ARTISTIC WORK WITHIN THE MEANING OF THE COPYRIGHT ACT 1968 (CTH). MCDONALD JONES HOMES PTY LTD IS THE OWNER OF COPYRIGHT IN THIS DRAWING. YOU HEREBY AGREE AND UNDERTAKE THAT YOU WILL NOT IN ANY WAY REPRODUCE, COPY, MODIFY, USE OR TAKE ADVANTAGE OF THE DRAWING TO BUILD A HOUSE BASED ON THIS PLAN (WHETHER IN WHOLE OR IN PART) WITHOUT THE PRIOR WRITTEN CONSENT OF MCDONALD JONES HOMES PTY LTD.




SPECIFICATION: TWO STOREY COPYRIGHT: © 2024		REVISION	DRAWN	CLIENT:	HOUSE DESIGN:		HOUSE CODE:	DO NOT SCALE DRAWINGS. USE FIGURED DIMENSIONS ONLY. CHECK AND VERIFY DIMENSIONS AND LEVELS PRIOR TO THE COMMENCEMENT OF ANY WORK. ALL DISCREPANCIES TO BE REPORTED TO THE DRAFTING OFFICE. 607082
	5	COLOURS APPLIED	TNG 26/01/2024	CLIFF LAURENS & MARGARETHA HARUNISA TARUNADJAYA	PANORAMA 36		H-MDSPNR20DA	
	6	AMENDED AS PER PCV007	GBO 22/02/2024	ADDRESS:	FACADE DESIGN:		FACADE CODE:	
	7	AMENDED AS PER PCV08 - HYDRAULIC	LFL 09/04/2024	48 WENTWORTH STREET, CROYDON PARK NSW 2133	PULSE		F-MDSPNR20PLSEA	
	8	AMENDED AS PER PCV009 & PCV011	GBO 03/05/2024	LOT / SECTION / DP:	SHEET TITLE:	SHEET No.:	SCALES:	
	9	AMENDED AS PER PCV013	LCS 08/05/2024	1 / - / 304988	COUNCIL:	23 / 24	1:100	
				CANTERBURY BANKSTOWN COUNCIL	DRAINAGE PLAN			

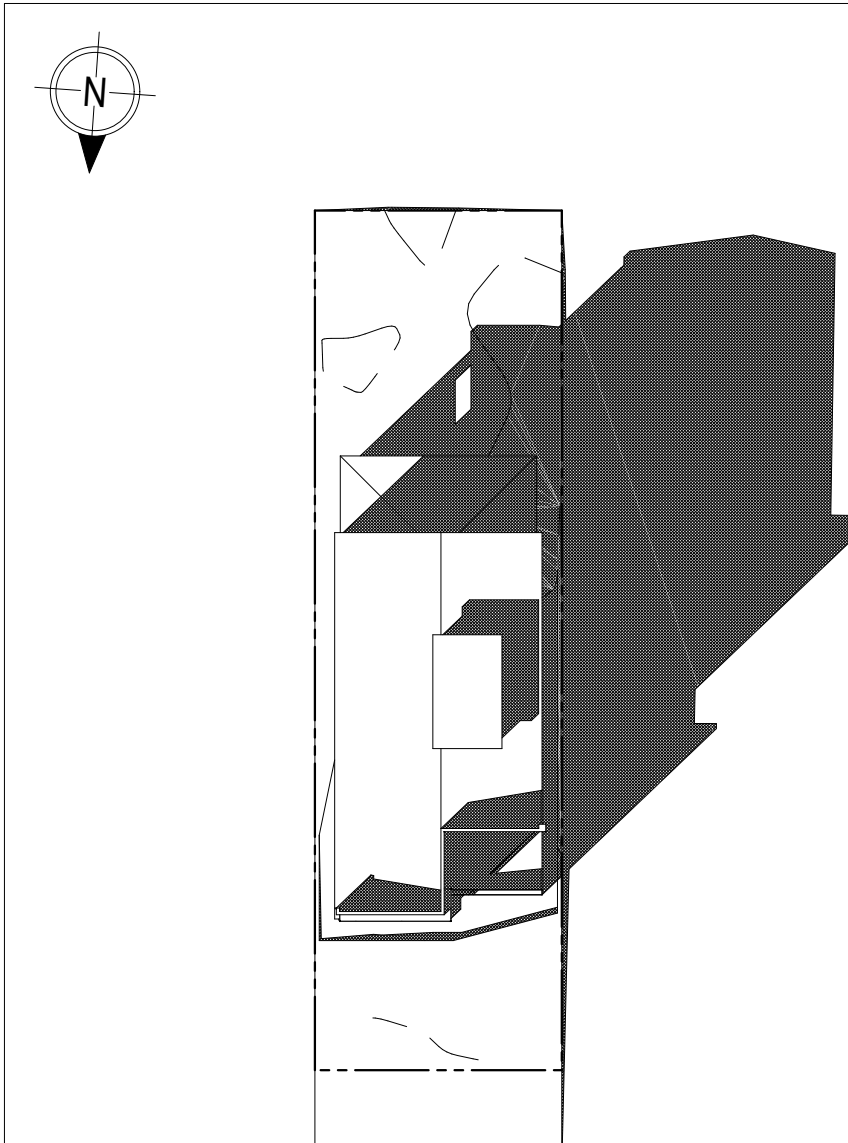

JUNE 21 - 0900

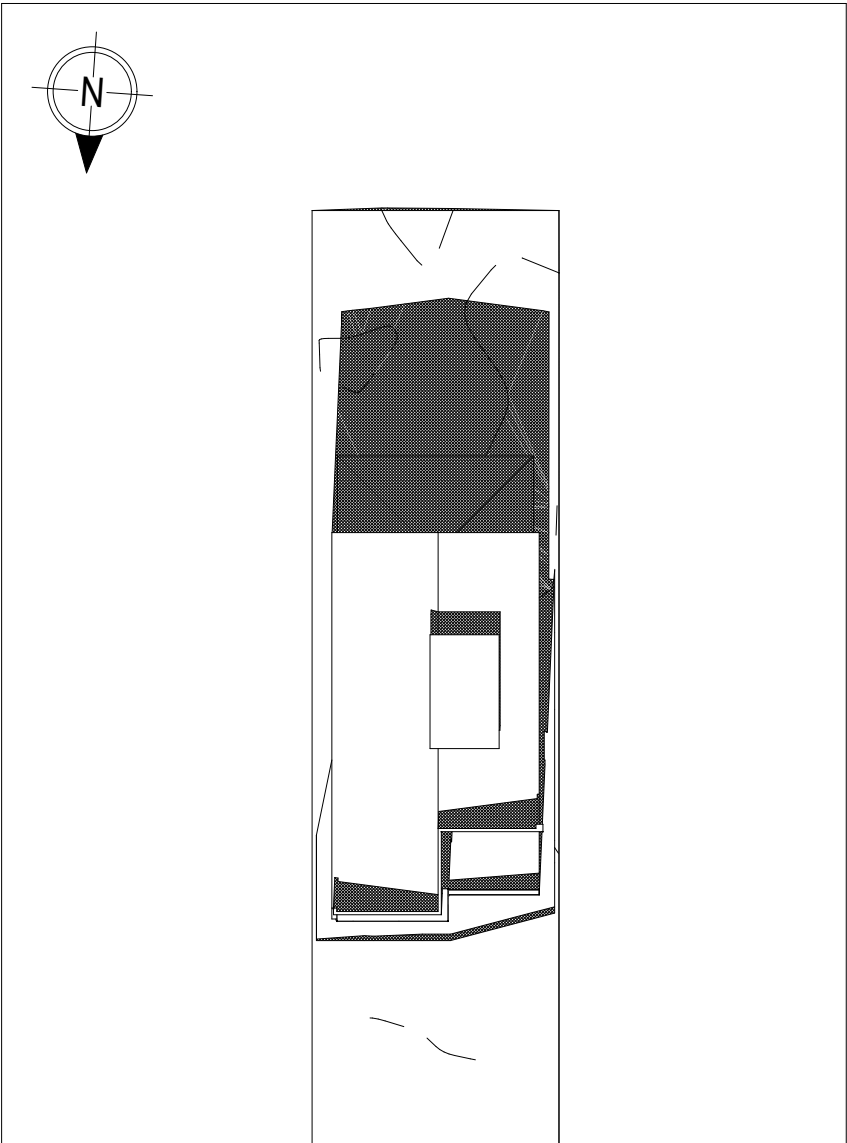

JUNE 21 - 1200

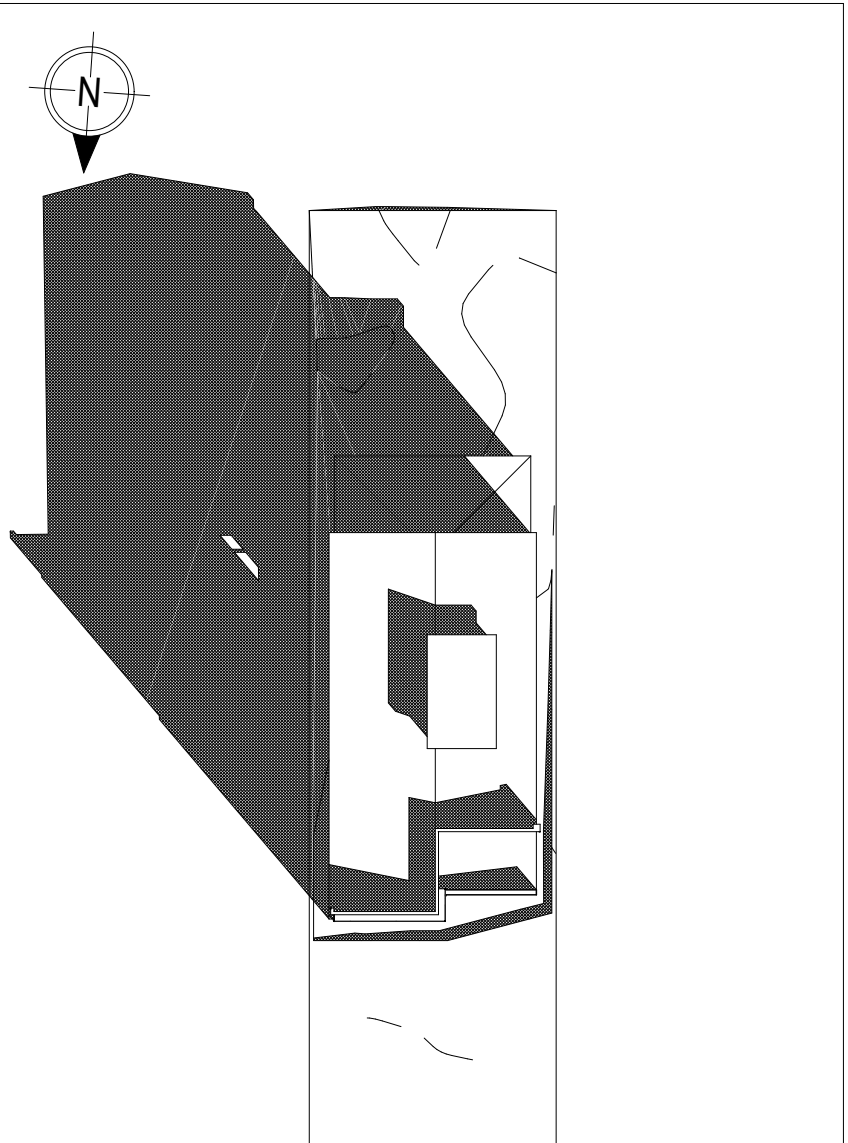

JUNE 21 - 1500



© 2024 MCDONALD JONES HOMES PTY LTD (ABN 82 003 687 232). THIS DRAWING IS AN ORIGINAL ARTISTIC WORK WITHIN THE MEANING OF THE COPYRIGHT ACT 1968 (CTH). MCDONALD JONES HOMES PTY LTD IS THE OWNER OF COPYRIGHT IN THIS DRAWING. YOU HEREBY AGREE AND UNDERTAKE THAT YOU WILL NOT IN ANY WAY REPRODUCE, COPY, MODIFY, USE OR TAKE ADVANTAGE OF THE DRAWING TO BUILD A HOUSE BASED ON THIS PLAN (WHETHER IN WHOLE OR IN PART) WITHOUT THE PRIOR WRITTEN CONSENT OF MCDONALD JONES HOMES PTY LTD.

 mcdonald jones FIND YOURSELF AT HOME	SPECIFICATION: TWO STOREY		REVISION	DRAWN	CLIENT: CLIFF LAURENS & MARGARETHA HARUNISA TARUNADJAYA	HOUSE DESIGN: PANORAMA 36		HOUSE CODE: H-MDSPNR20DA	DO NOT SCALE DRAWINGS, USE FIGURED DIMENSIONS ONLY. CHECK AND VERIFY DIMENSIONS AND LEVELS PRIOR TO THE COMMENCEMENT OF ANY WORK. ALL DISCREPANCIES TO BE REPORTED TO THE DRAFTING OFFICE. 607082
	COPYRIGHT: © 2024	5	COLOURS APPLIED	TNG 26/01/2024	ADDRESS: 48 WENTWORTH STREET, CROYDON PARK NSW 2133	FACADE DESIGN: PULSE		FACADE CODE: F-MDSPNR20PLSEA	
		6	AMENDED AS PER PCV007	GBO 22/02/2024	LOT / SECTION / DP: 1 / - / 304988	SHEET TITLE: SHADOW DIAGRAMS - JUNE 21	SHEET No.: 24 / 24	SCALES: 1:350	
		7	AMENDED AS PER PCV08 - HYDRAULIC	LFL 09/04/2024	COUNCIL: CANTERBURY BANKSTOWN COUNCIL				
		8	AMENDED AS PER PCV009 & PCV011	GBO 03/05/2024					
		9	AMENDED AS PER PCV013	LCS 08/05/2024					